




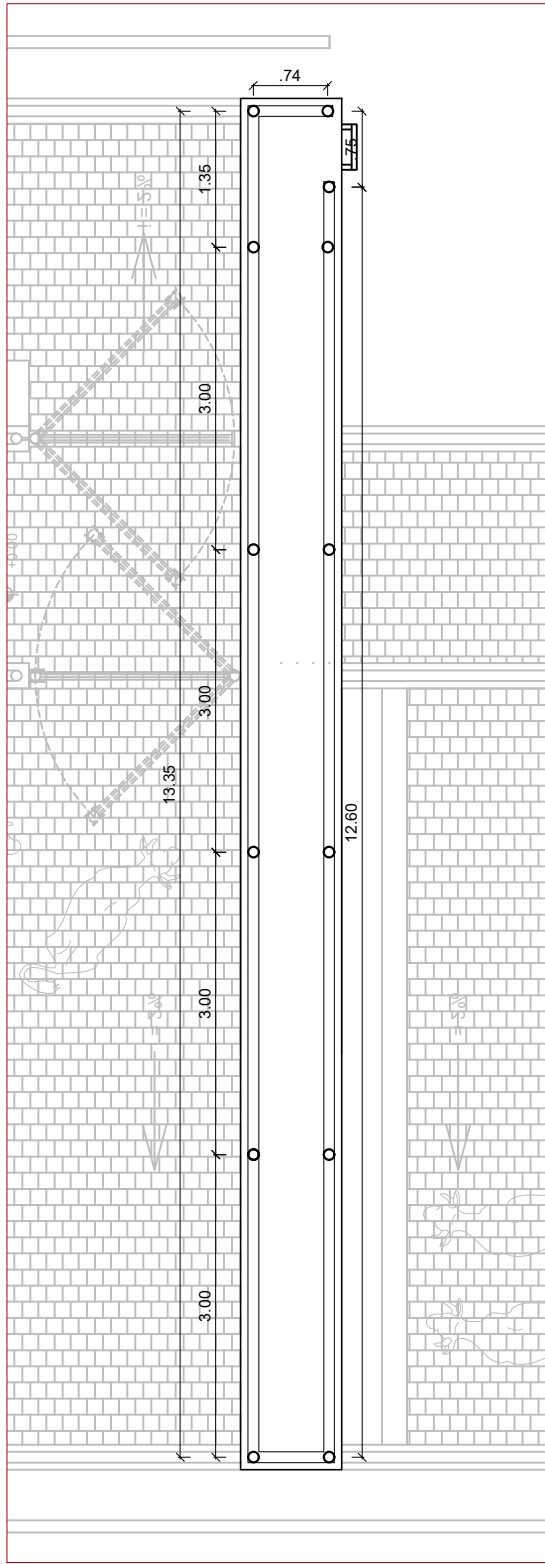


Planta Baixa – Plataforma de Observação
escala + 1/75

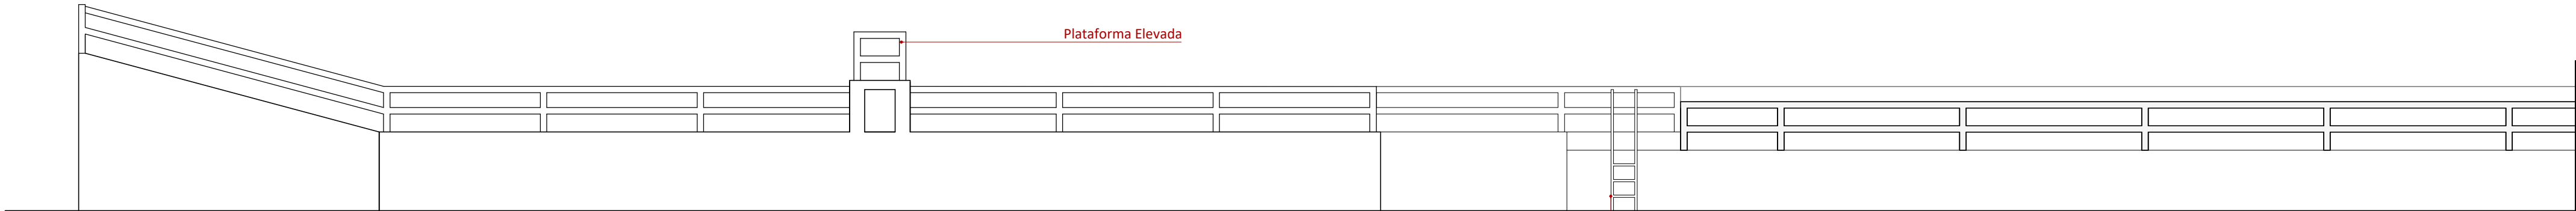


Fachada Lateral Esquerda – Curral Bovino
escala + 1/75

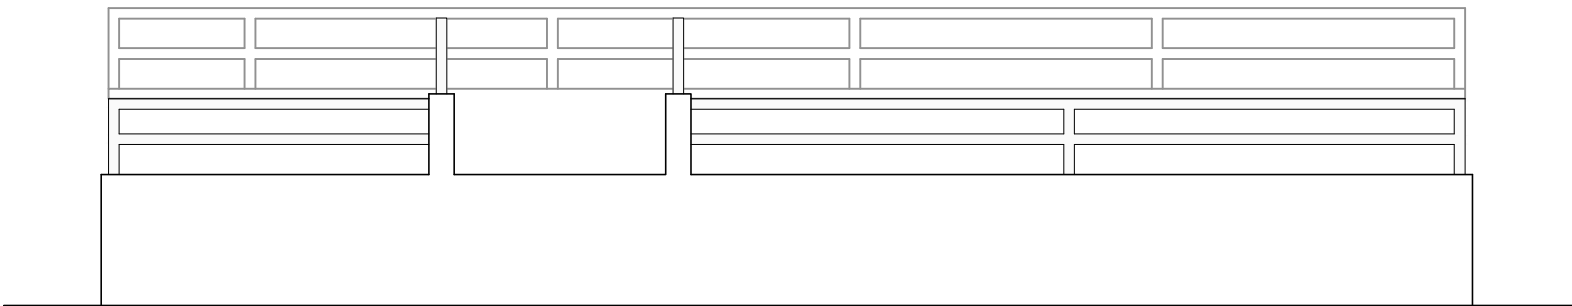

Fachada Frontal – Curral Bovino
escala + 1/75

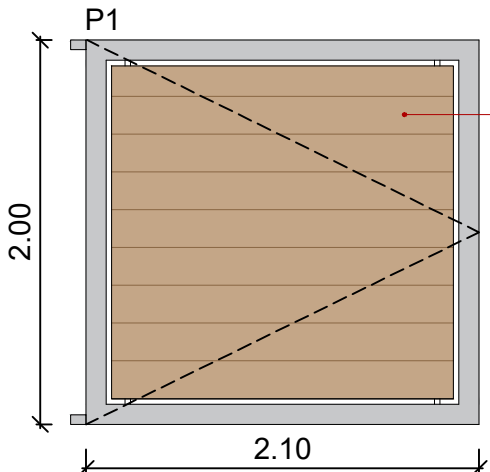

Detalhe – Porteira de abrir
escala + 1/40

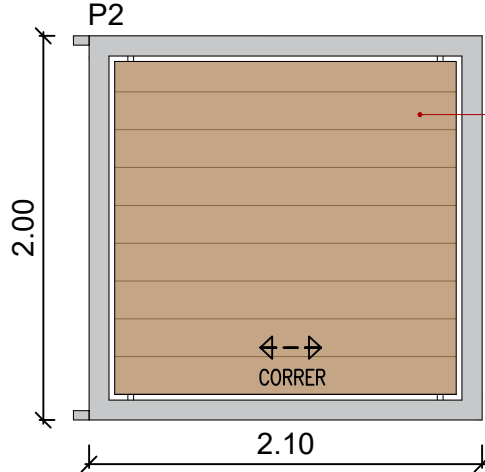

Detalhe – Porteira de correr
escala + 1/40

QUADRO DE ESPECIFICAÇÕES		
PISO	PAREDE	TETO
01 – Pavimento em paralelepípedo sobre colchão de areia rejuntado com argamassa no traço 1:3 (cim:areia)	01 – Massa única e caiação caiação com adoção de fixador duas demãos	–

QUADRO DE ESQUADRIAS						
PORTAS						
TIPO	LARGURA	ALTURA	QUANT.	TIPO	ÁREA (P/ UNID.)	OBSERVAÇÕES
P1	2.10	2.00	3	VAI E VEM	4.20 m²	AÇO GALVANIZADO E FECH. EM MADEIRA
P2	2.10	2.00	2	CORRER	4.20 m²	AÇO GALVANIZADO E FECH. EM MADEIRA

RESPONSÁVEL TÉCNICO:			
PROPRIETÁRIO:			
PRANCHA		PREFEITURA MUNICIPAL DE COREMAS – PB	
2/4		PROJETO DE CONSTRUÇÃO DE MATADOURO – 9389922022	
		PROJETO ARQUITETÔNICO – CURRAL BOVINO	
	DATA	RESPONSÁVEL	RUBRICA
DESENHO			
PROJETO			
CÓPIA			
ESCALA:			
1/75		DESENHO:	
1/75		PLANTA BAIXA – PLATAFORMA DE OBSERVAÇÃO	
1/75		FACHADA LATERAL ESQUERDA	
1/40		FACHADA FRONTAL	
1/40		DETALHE – PORTEIRA DE ABRIR	
1/40		DETALHE – PORTEIRA DE CORRER	
		ÁREA DE TERRENO	ÁREA CONSTRUÍDA
		10.000,00 M²	871,58 M²