


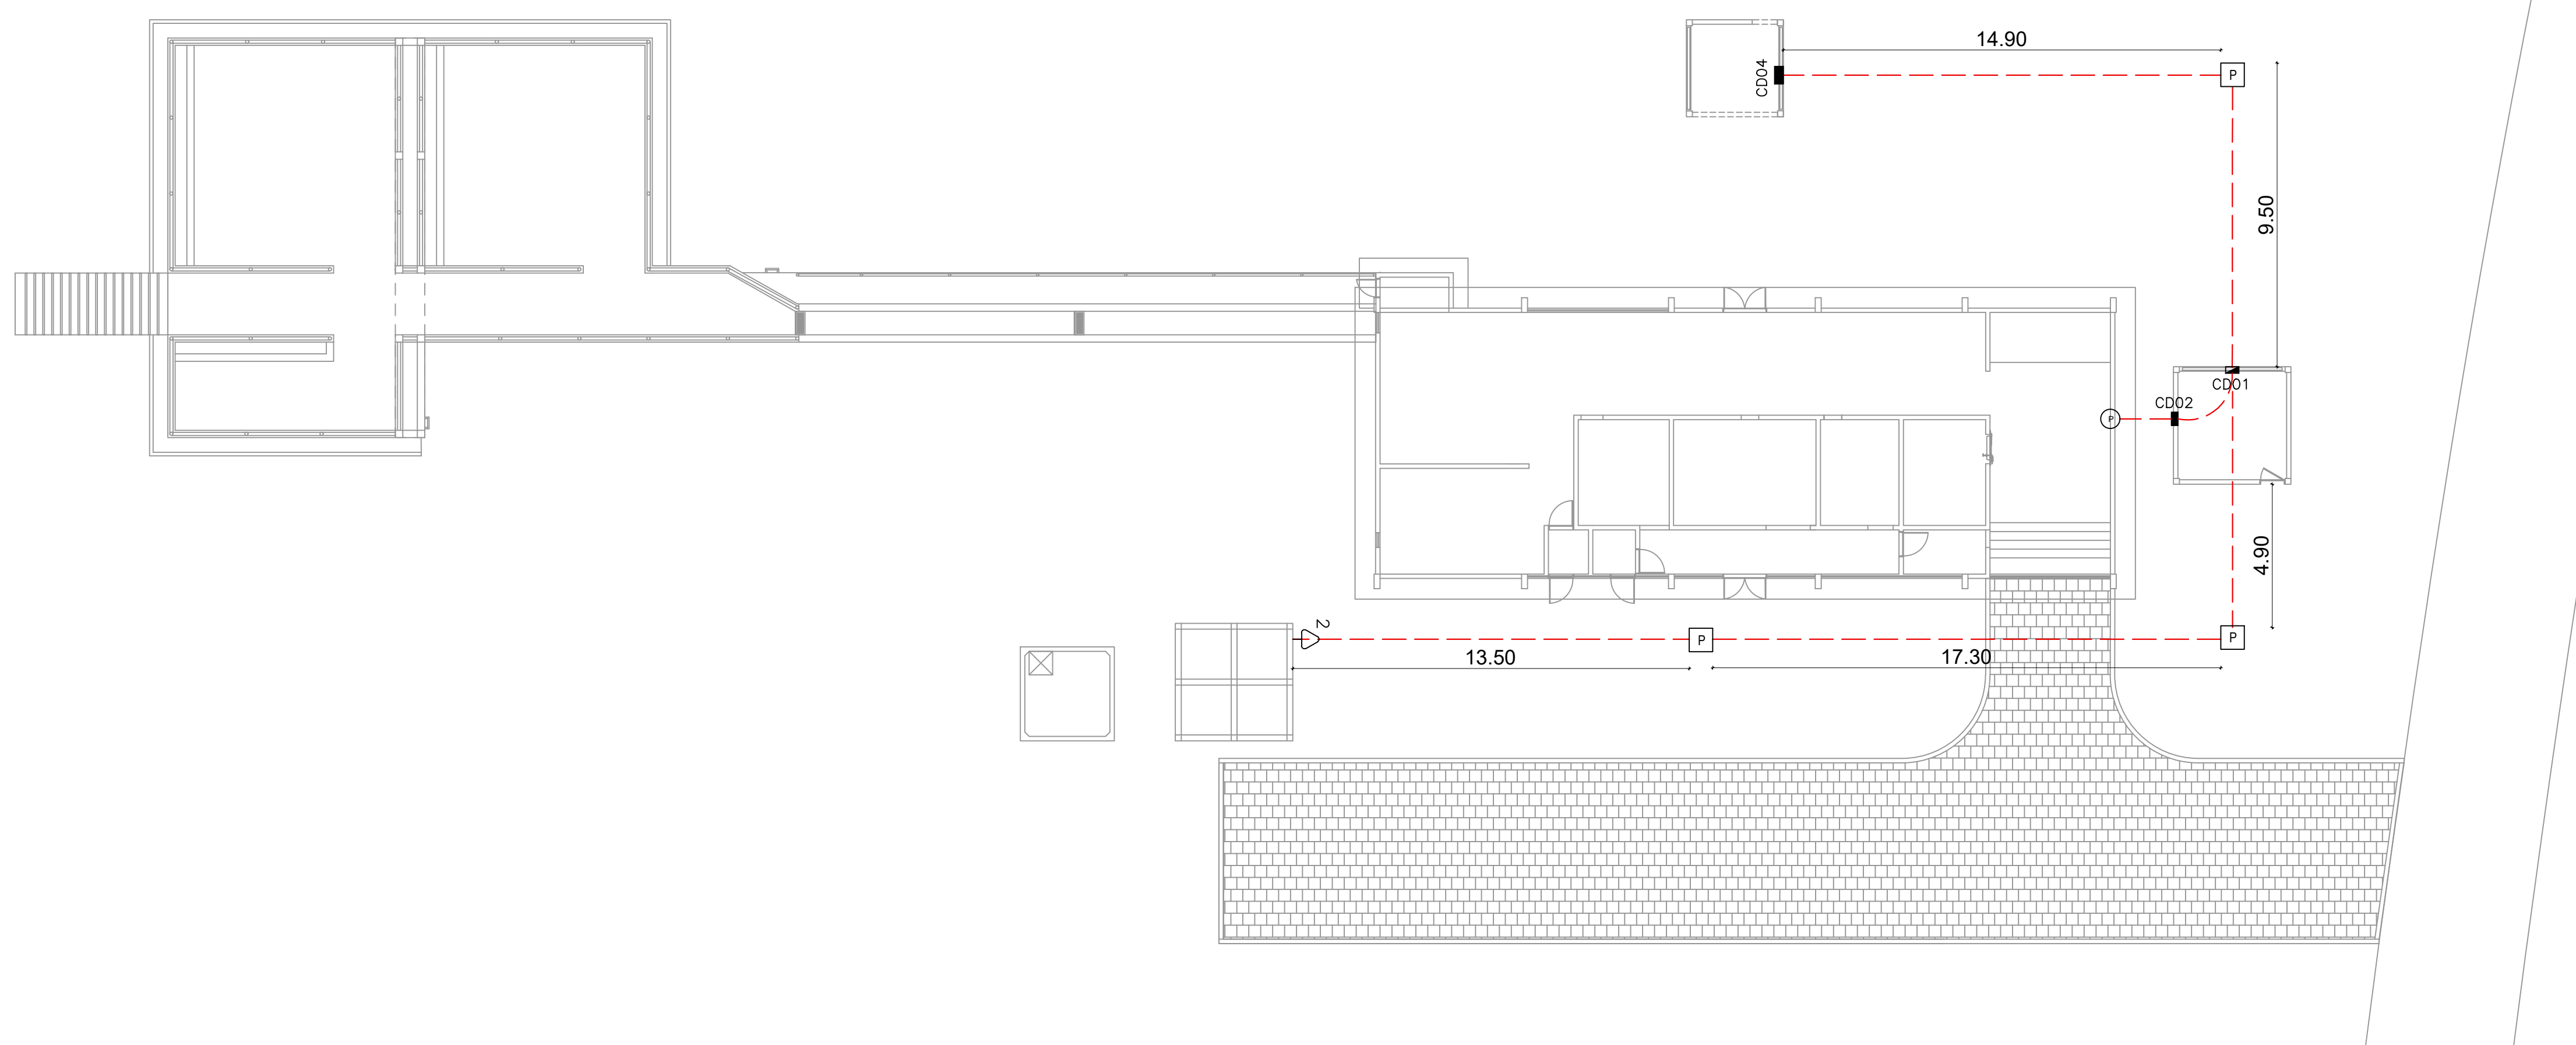

Núm.	Quant.	Und.	Dimensão	Código	Descrição
1	1	pc		PECC2X4	Caixa 2x4
2	13	pc			Caixa de passagem no piso
3	16	pc	1"		Cabo ruiscável mocho – Rígido
4	35,80	m	1"	14.02.190.6	Eletroduto Rígido – Parede
5	193,05	m	1"	14.02.190.6	Eletroduto Rígido – Piso
6	25	pc	1"	14.02.190.6	Eletroduto Rígido – Teto
7	32	pc	1"		Linha ruiscável – Rígido
8	1	pc			Tomada baia 30cm
9	10	pc			Luminária de LED 120w

Num.	Quant.	Und.	Dimensão	Código	Descrição
1	5	pc			Poste

Num.	Quant.	Und.	Dimensão	Código	Descrição
1	91.62	n	6 mm2		Cabo de cobre nu - Fase
2	30.54	n	6 mm2		Cabo de cobre nu - Neutro
3	489.69	n	2.5 mm2	3000	Fio cabo 750 V - PVC - Fase
4	170.11	n	2.5 mm2	3000	Fio cabo 750 V - PVC - Neutro
5	183.05	n	2.5 mm2	3000	Fio cabo 750 V - PVC - Terra

LEGENDA:

	- Arandela		- Interruptor duplo		- Interruptor simples		- Luminária LED 120W		- Luminária LED 25W		- Poste		- Tomada 130cm		- Tomada baixa 30cm		- Tomada no piso		- Quadro Geral de luz e força		- Quadro Parcial de luz e força		- Caixa de passagem na parede		- Caixa de passagem no piso		- Rese Fotoelétrica		- Disjuntor a seco - DIN 10A 1P		- Disjuntor a seco - DIN 10A 3P		- Disjuntor a seco - DIN 125A 3P		- Disjuntor a seco - DIN 25A 1P		- Eletroduto no Teto/ Aéreo		- Eletroduto no Piso		- Neutro, Fase, Retorno, Terra		- Fio de cobre nu, aéreo 6mm
OBSERVAÇÕES 1)Obs.: O eletroduto que não estiver indicado o dimensionamento, considerar como Ø1". 2)Obs.: O fio que não estiver indicada o dimensionamento, considerar como Ø6mm". 3)Obs.: Cada poste terá uma caixa de Passagem e Fotoelétrica.	

NOTAS TÉCNICAS - PROJETO ELÉTRICO MATADOURO PÚBLICO

- NT 01: "No quadro CD02 referente a instalação elétrica do galpão, os circuitos dos equipamentos foram estipulados de acordo com as necessidades para o pleno funcionamento da intervenção, porém a instalação de todos os equipamentos serão através de recursos próprios municipais, e a empresa especializada contratada para o serviço tem o livre arbítrio para alteração dos circuitos de acordo com as especificidades de cada fabricante, observando apenas a potência demandada equivalente do quadro, tal empresa deverá emitir anotação de responsabilidade técnica-ART por profissional registrado"


- NT 02: A imagem/formato dos quadros é meramente ilustrativa, servem apenas para indicar as tubulações que saem/chegam nos mesmos.

- **NT 03:** Os recursos federais provenientes desse CR, não englobam os aspectos necessários para a instalação dos equipamentos (vide NT 01), deixando apenas os espaço e potência demandada reservada no quadro de alimentação.

- NT 04: Todas as instalações devem atender as leis, normas e aspectos de segurança do trabalho vigentes no país.

- **NT 05:** A execução do Padrão de Entrada de Energia até a Sala de Painéis Elétricos, necessário para o Projeto de Construção do Matadouro Público de SÃO BENTO serão executados através de recursos próprios municipais.

- **NT 06:** Os equipamentos necessários para o pleno funcionamento do galpão: As portas guilhotinas, suas instalações elétricas e seus respectivos dispositivos hidrossanitários serão executadas através de recursos próprios municipais.

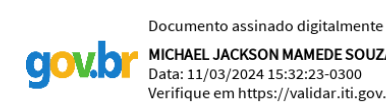

RESPONSÁVEL TÉCNICO:

PROPRIETÁRIO:

PRANCHA

PREFEITURA MUNICIPAL DE COREMAS – PB

14

PROJETO DE CONSTRUÇÃO DE MATADOURO

PROJETO ELÉTRICO

DATA	
DESENHO	

RESPONSÁVEL	RUBR
-------------	------

PROJETO	
CÓDIGO	

	AREA TERRE
--	------------

Escala:

DESENHO:

9009022022_ELE