




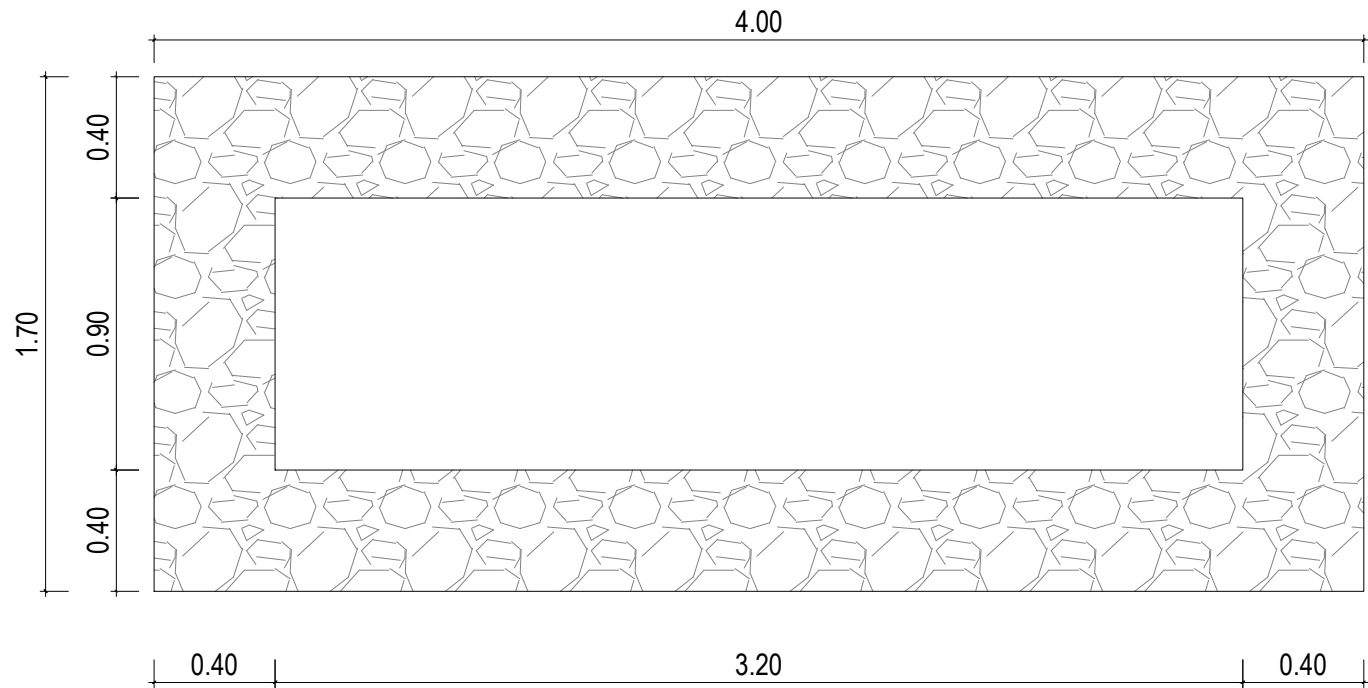

Detalhe – emb. em pedra argamassada
escala 1/25

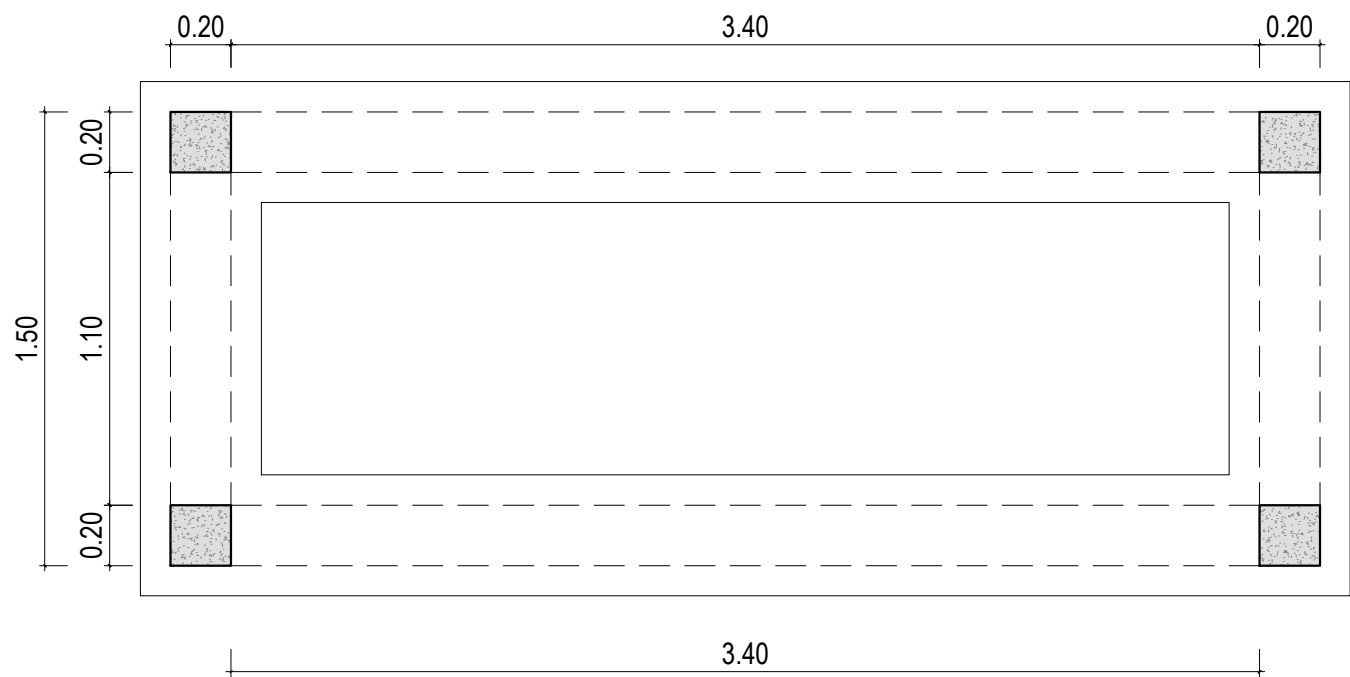


Detalhe – pilaretes
escala 1/25

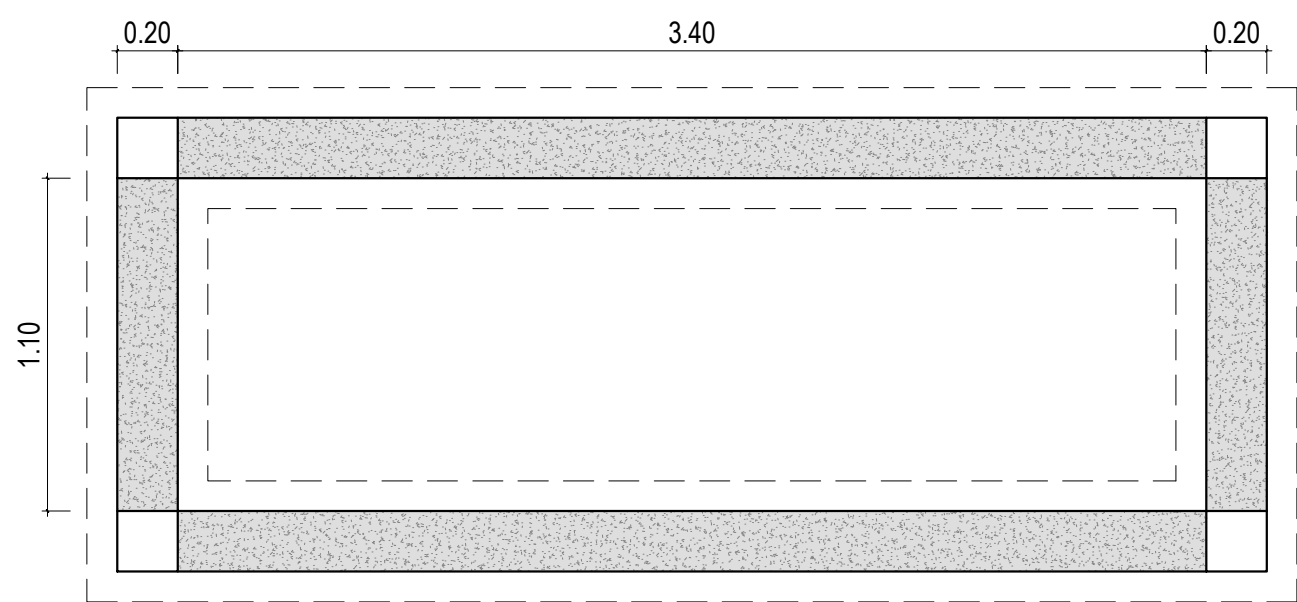

Detalhe – Cintas
escala 1/25


CINTA GERAL INFERIOR - CGI
(PERÍMETRO: 9,80m)

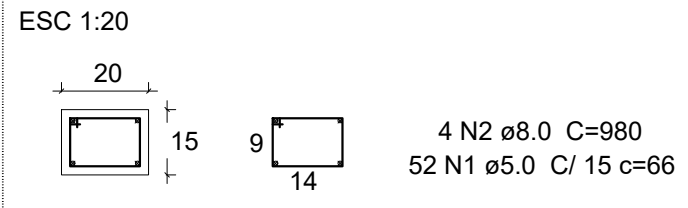

Relação do aço						CGI
AÇO	N	DIAM	Q	UNIT (cm)	C.TOTAL (cm)	
CA60	1	5.0	66	66	4356	
CA50	2	8.0	4	980	3920	

Resumo do aço				
AÇO	DIAM	C.TOTAL (m)	PESO + 10 % (kg)	
CA50	8.0	39.20	17.03	
CA60	5.0	43.56	7.38	


PILARES DA ESTERQUEIRA - PE (4x)

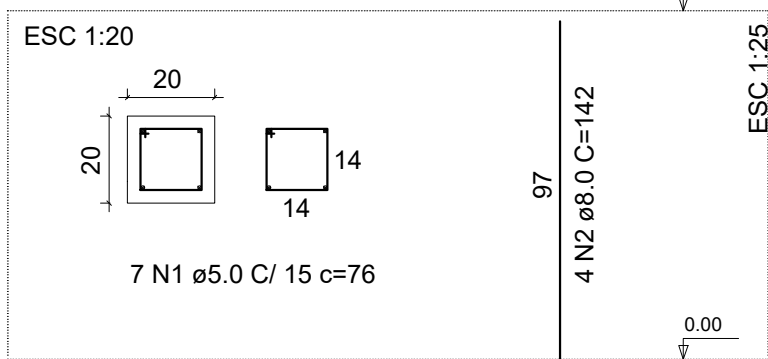

Relação do aço						PM/PC/PS
AÇO	N	DIAM	Q	UNIT (cm)	C.TOTAL (cm)	
CA60	1	5.0	28	60	1680	
CA50	2	8.0	16	142	2272	

Resumo do aço				
AÇO	DIAM	C.TOTAL (m)	PESO + 10 % (kg)	
CA50	8.0	22.7	9.8	
CA60	5.0	16.8	2.8	

CINTA GERAL SUPERIOR - CGS
(PERÍMETRO: 9,80m)

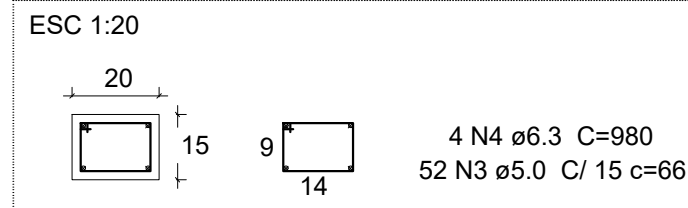

Relação do aço						CGS
AÇO	N	DIAM	Q	UNIT (cm)	C.TOTAL (cm)	
CA60	3	5.0	66	66	4356	
CA50	4	8.0	4	980	3920	

Resumo do aço				
AÇO	DIAM	C.TOTAL (m)	PESO + 10 % (kg)	
CA50	8.0	39.20	17.03	
CA60	5.0	43.56	7.38	

Detalhes – estruturais
escala 1/25

Documento assinado digitalmente
gov.br MICHAEL JACKSON MAMEDE SOUZA
Data: 11/03/2024 15:18:34 -0300
Verifique em https://validar.iti.gov.br

RESPONSÁVEL TÉCNICO:

PROPRIETÁRIO:

PRANCHA		PREFEITURA MUNICIPAL DE COREMAS – PB			
2/2		PROJETO DE CONSTRUÇÃO DE MATADOURO – 9389922022			
		PROJETO ARQUITETÔNICO – ESTERQUEIRA			
	DATA	RESPONSÁVEL		RUBRICA	
DESENHO					
PROJETO				ÁREA DE TERRENO	ÁREA CONSTRUÍDA
CÓPIA				10.000,00 M²	871,58 M²
ESCALA:		DESENHO:			
1/25		PLANTA – EMBASAMENTO			
1/25		PLANTA – PILARES			
1/25		PLANTA – CINTAS			
S/ESC		DETALHES ESTRUTURAIS			

9389922022_Esterqueira