




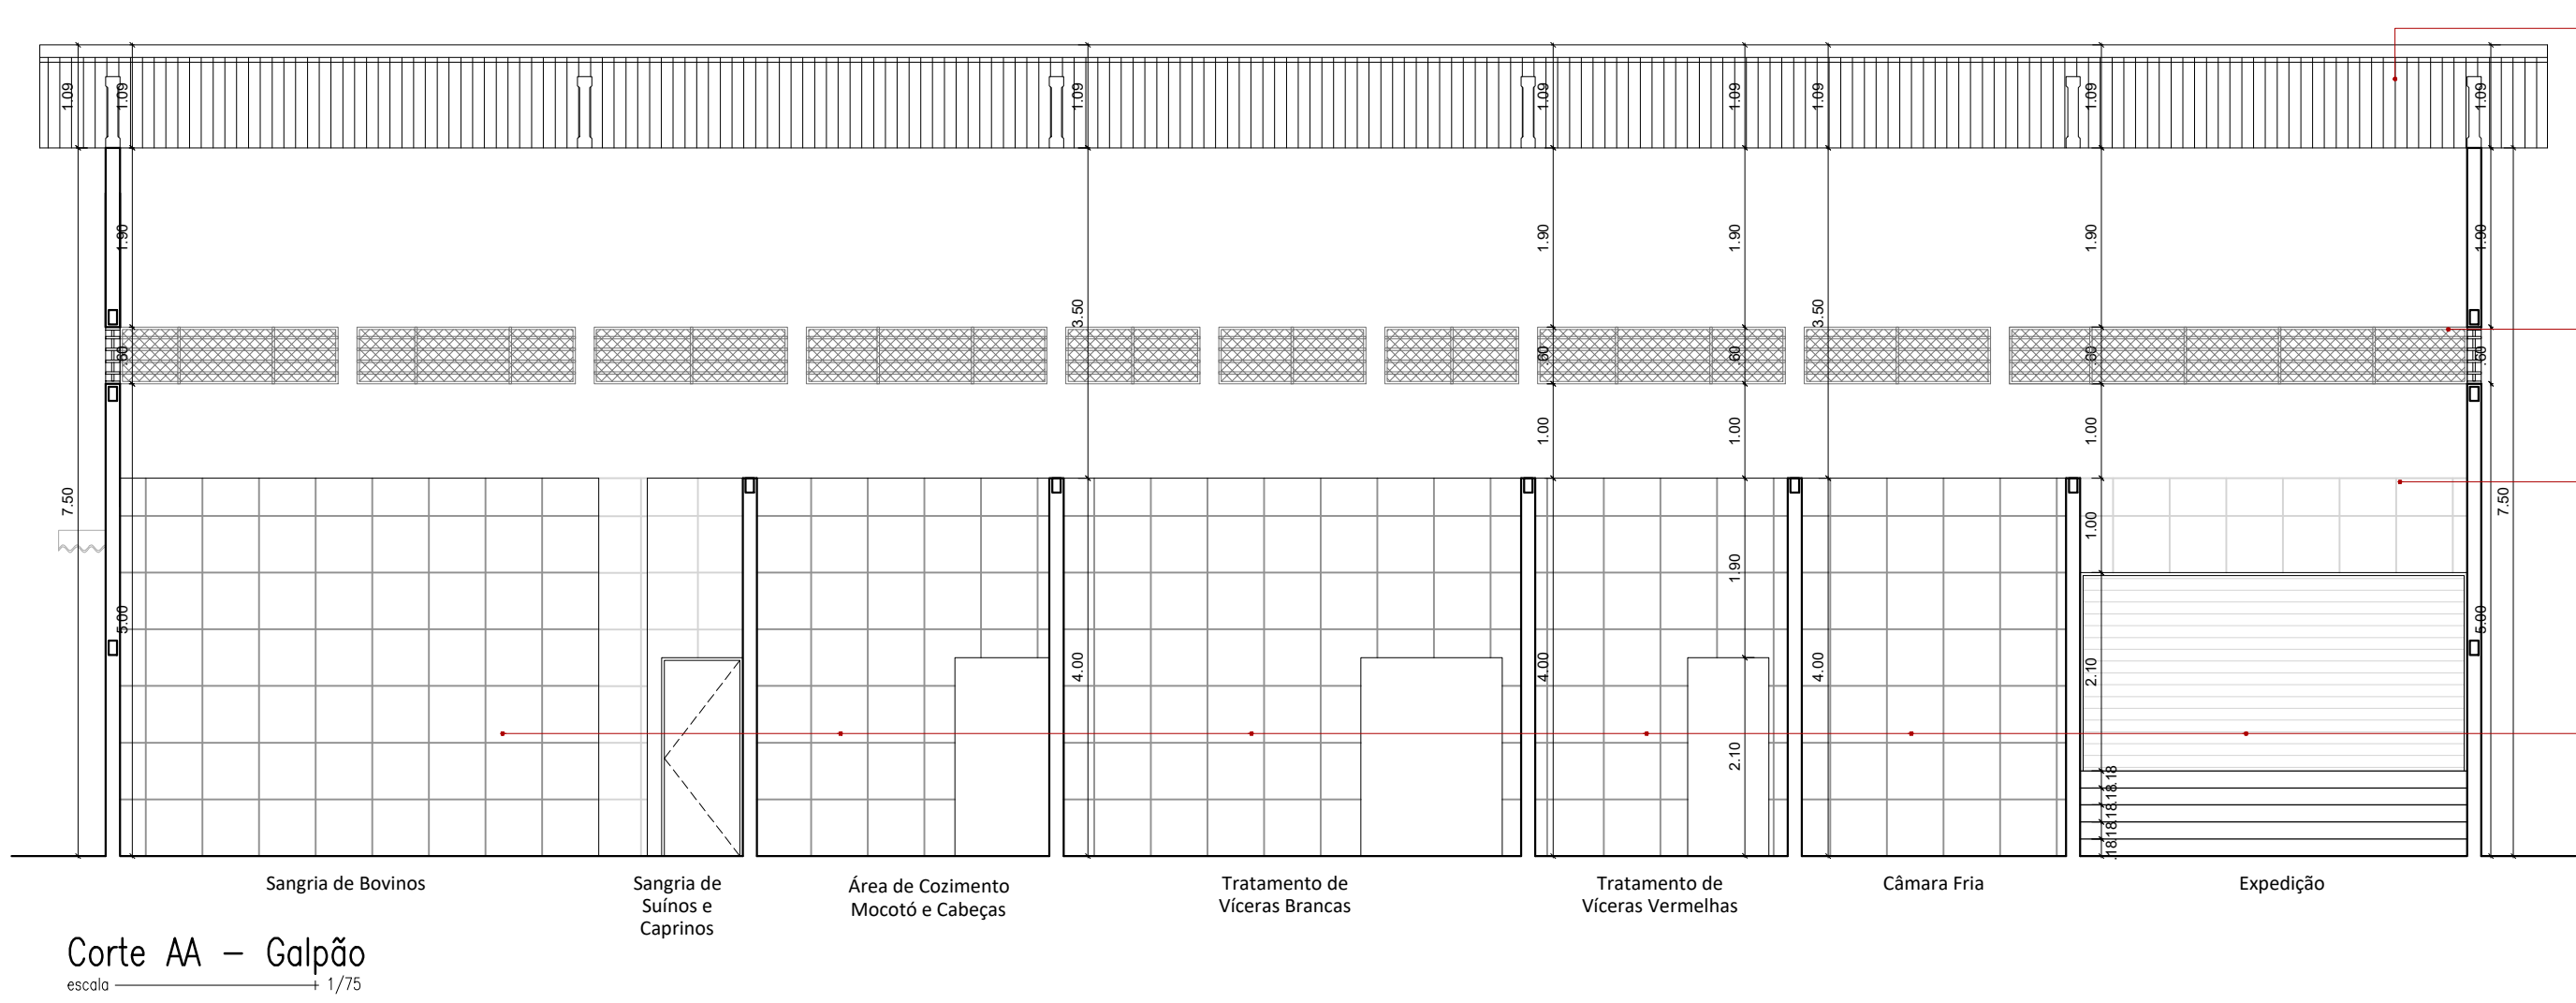


Corte AA – Galpão
escala 1/75

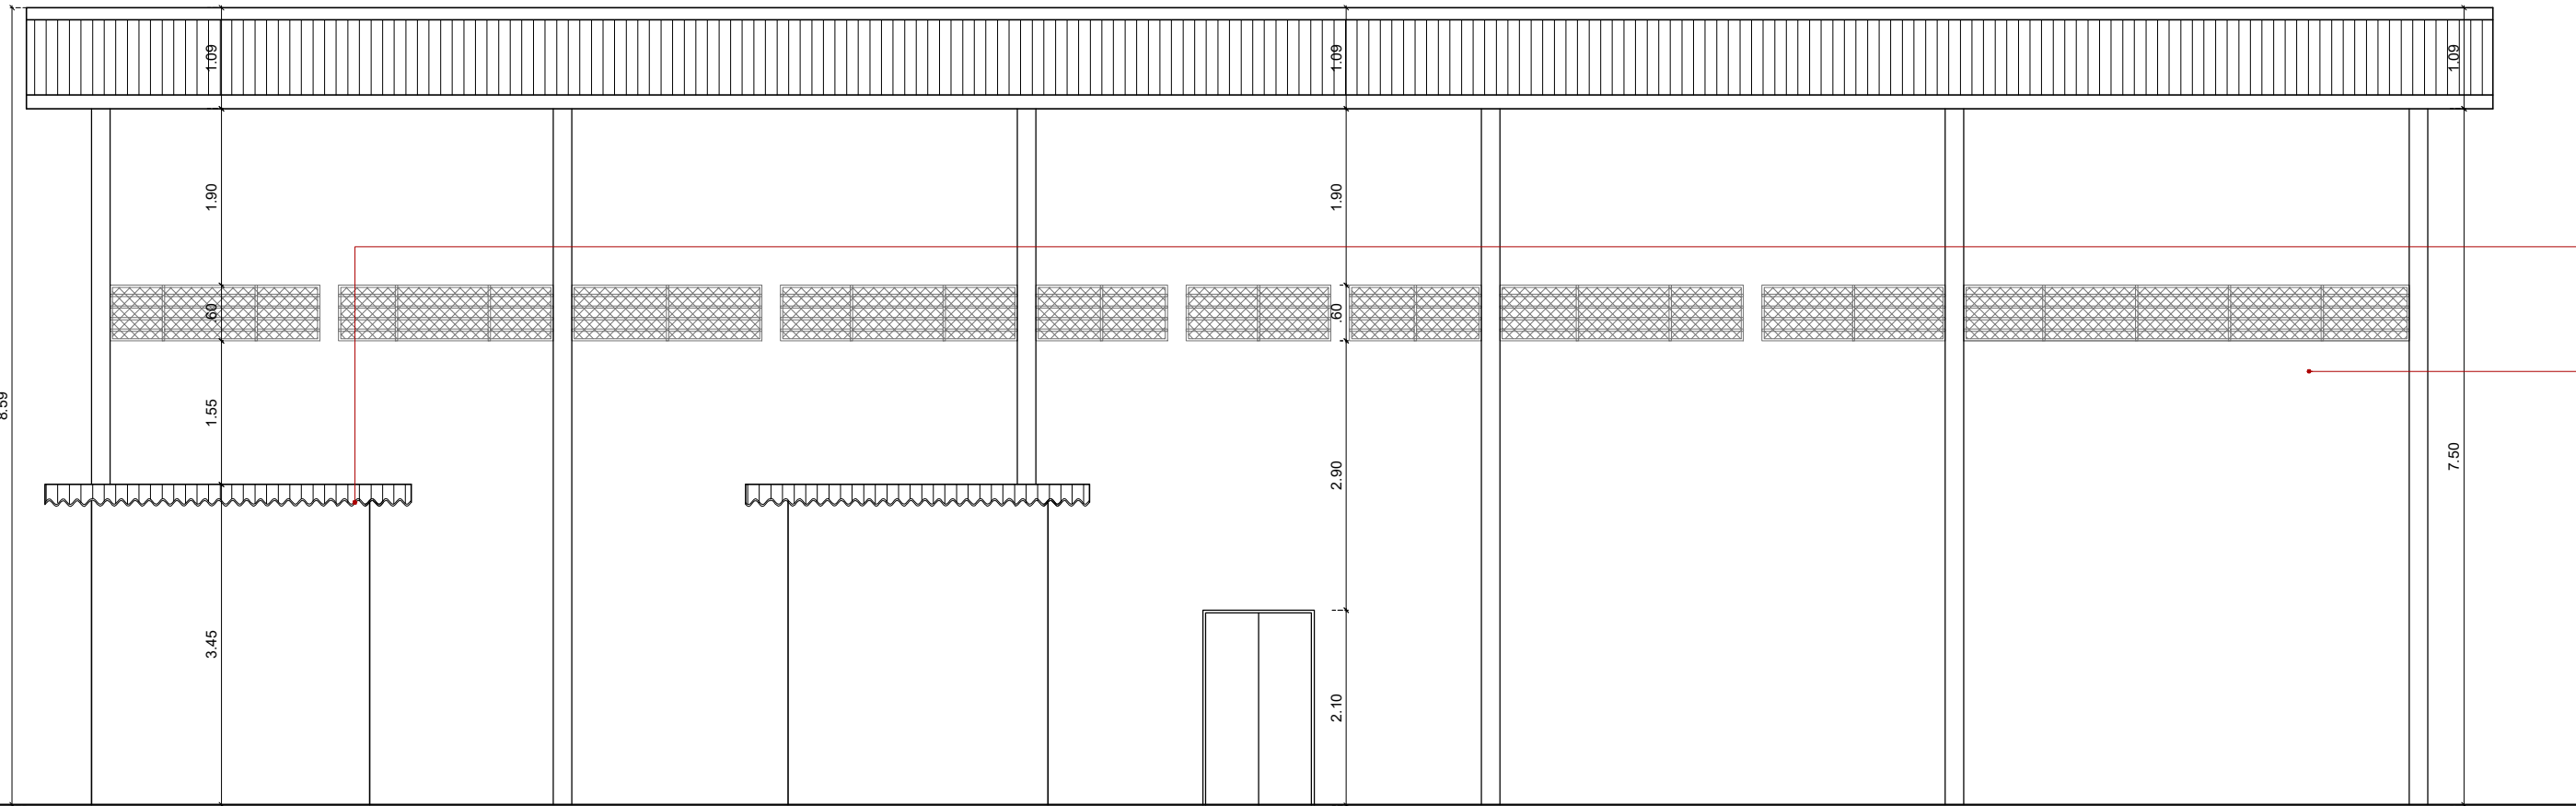


Fachada Lateral Esquerda – Galpão
escala 1/75

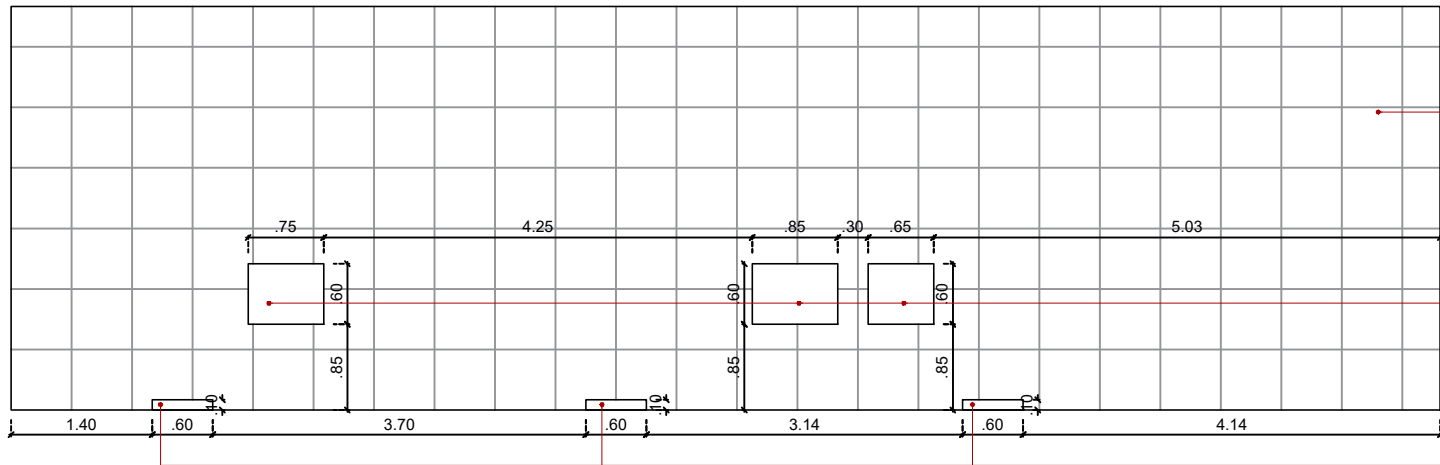

Vista 01 – Aberturas
escala 1/75

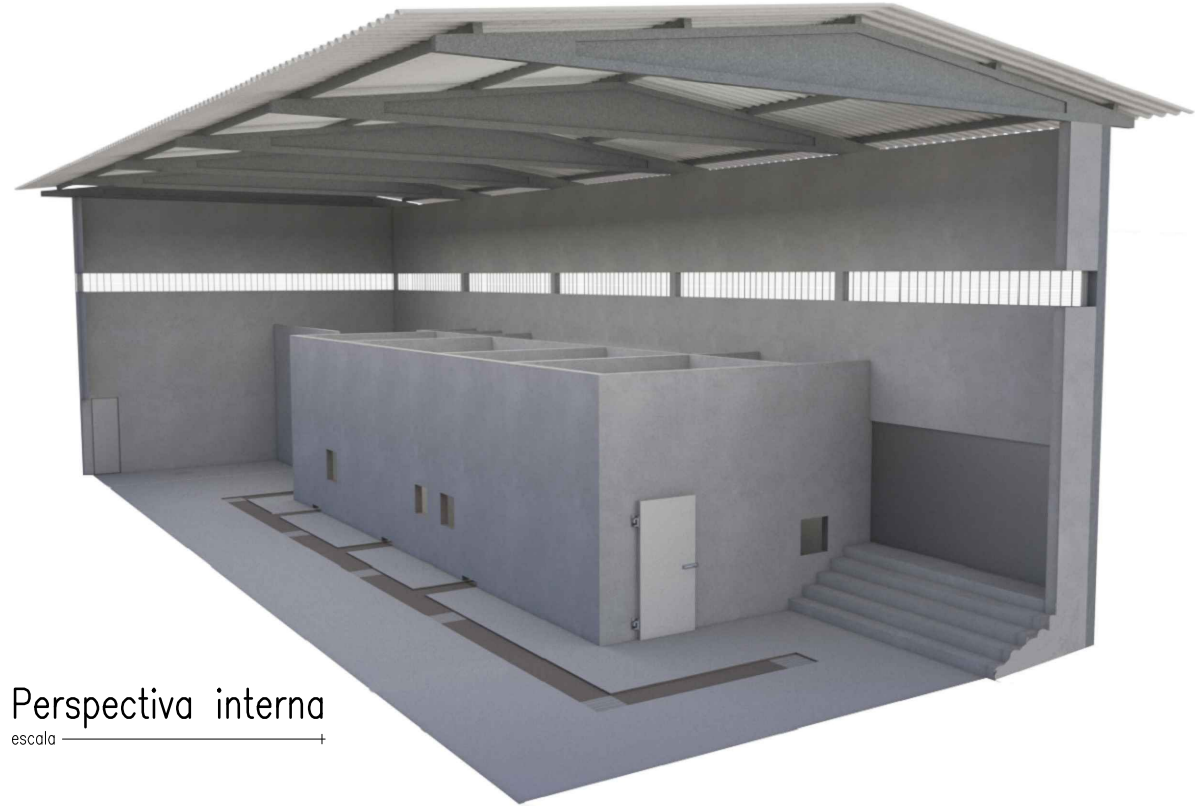

Perspectiva interna
escala 1/75

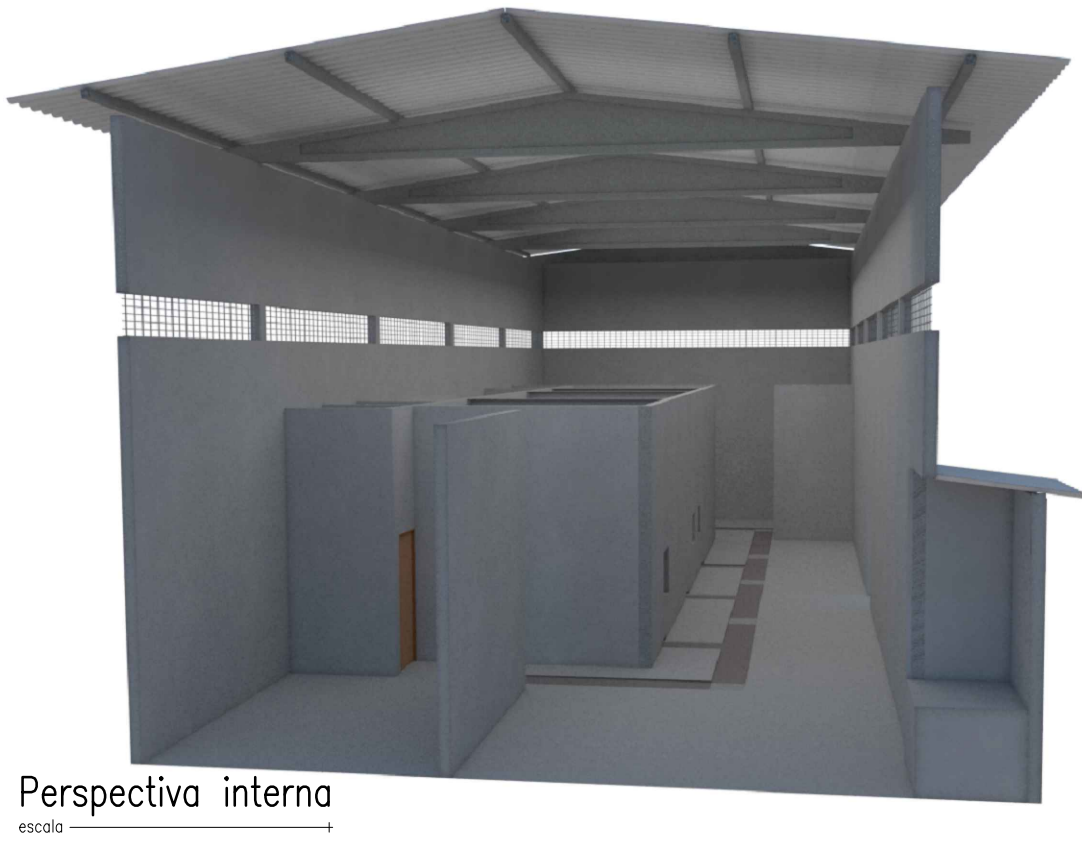

Perspectiva interna
escala 1/75

Telha fibrocimento sobre estrutura pré-moldada

Gradil de ferro barra chata 1 x 3/16" com tela de fibra de vidro tipo mosquiteiro com moldura em madeira 15x2,5cm

Revestimento cerâmico com placas tipo esmaltada 60 x 60 cm


Porta de Madeira de abrir

CARACTERÍSTICAS CONSTRUTIVAS DA TRILHAGEM AÉREA


- 1) Altura do trilho aéreo no local de sangria = 5,25 m;
- 2) Declive máximo do trilho, do ponto em que é alçado o animal até o local da sangria, no sistema não-mecanizado (sem nora) = 3,5 %;
- 3) Distância mínima da extremidade inferior da rês (focinho) ao piso, no local da sangria = 0,75 m;
- 4) Comprimento da canaleta de sangria e respectivo trilho = 4,60m;
- 5) Altura mínima do trilho baixo, até a linha de inspeção de carcaças = 4,00m;
- 6) Altura mínima do trilho após a linha de inspeção de carcaças, incluindo neste percurso a Inspeção Final = 3,50m;
- 7) Distância mínima do trilho às colunas existentes =0,80m;
- 8) Distância mínima do trilho à parede mais próxima = 1,20m;
- 9) Distância mínima do trilho à parede mais próxima, na linha de sangria =1,50m;
- 10) Distância mínima do trilho à parede, quando a mesa de evisceração (fixa) situar-se paralelamente àquela =3,50 m
- 11) Distância mínima do trilho à parede, quando se tratar de mesa móvel (de forma que entre a parede e a mesa haja um afastamento de 1,20 m =4,00 m
- 12) Distância mínima entre dois trilhos paralelos =2,00 m
- 13) Distância mínima entre dois trilhos paralelos, quando a mesa de e visceração se localizar entre os dois =5,00 m.

Telha fibrocimento sobre madeiramento em terças

Parede em tijolo de 8 furos com aplicação de chapisco e reboco com acabamento liso, pintura acrílica exterior

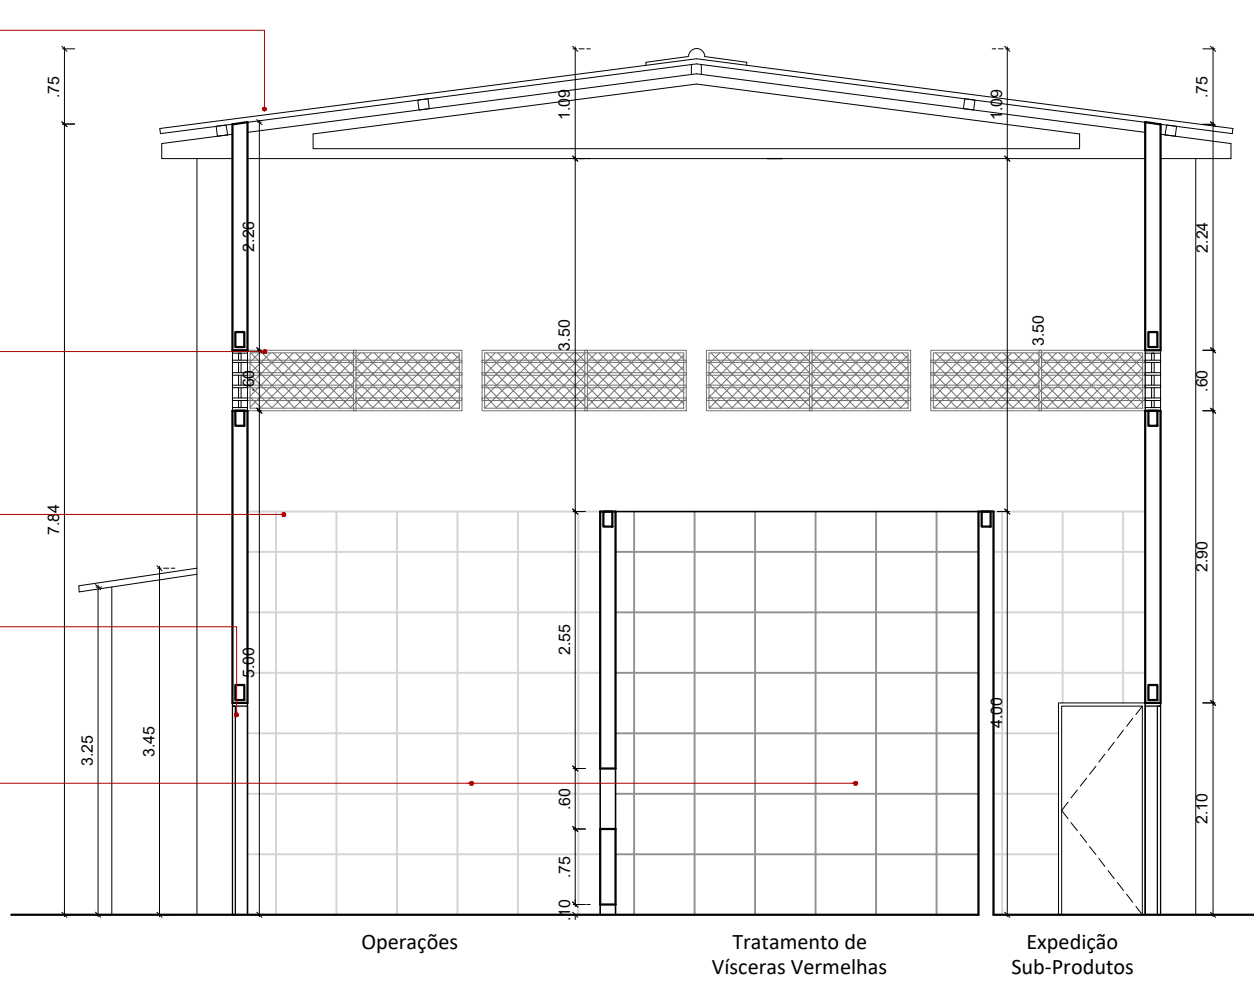

Corte BB – Galpão
escala 1/75

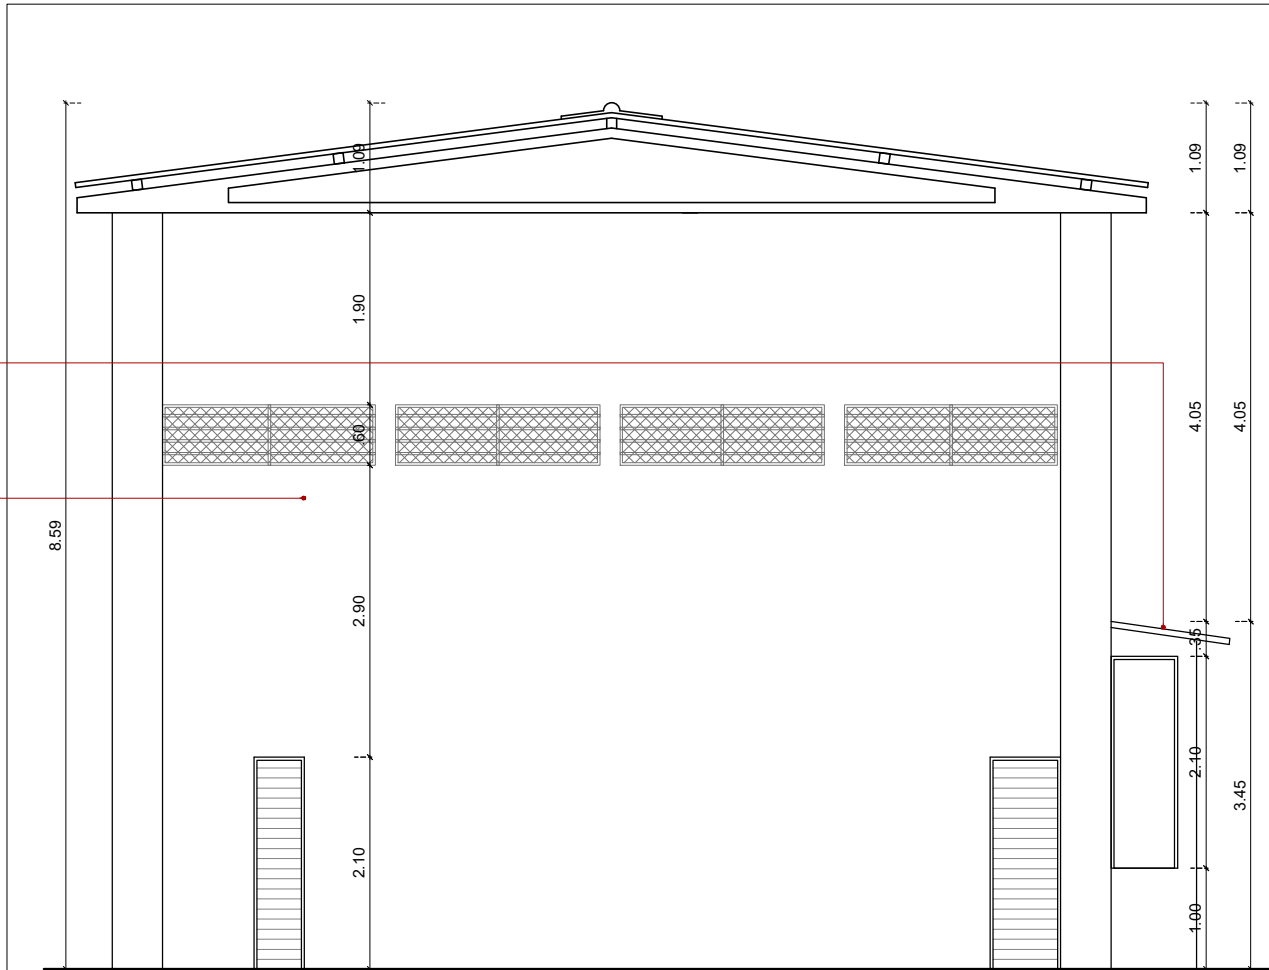

Fachada Frontal – Galpão
escala 1/75

RESPONSÁVEL TÉCNICO:

PROPRIETÁRIO:

PRANCHA		PREFEITURA MUNICIPAL DE COREMAS – PB		
2/5		PROJETO DE CONSTRUÇÃO DE MATADOURO – 9389922022		
		PROJETO ARQUITETÔNICO – GALPÃO		
	DATA	RESPONSÁVEL	RUBRICA	
DESENHO				
PROJETO			ÁREA DE TERRENO	ÁREA CONSTRUÍDA
CÓPIA			10.000,00 M²	871,58 M²
ESCALA:	DESENHO:			
1/75	PLANTA BAIXA			
1/75	FACHADA LATERAL ESQUERDA E FRONTAL			
1/75	VISTA 01 – ABERTURAS			