




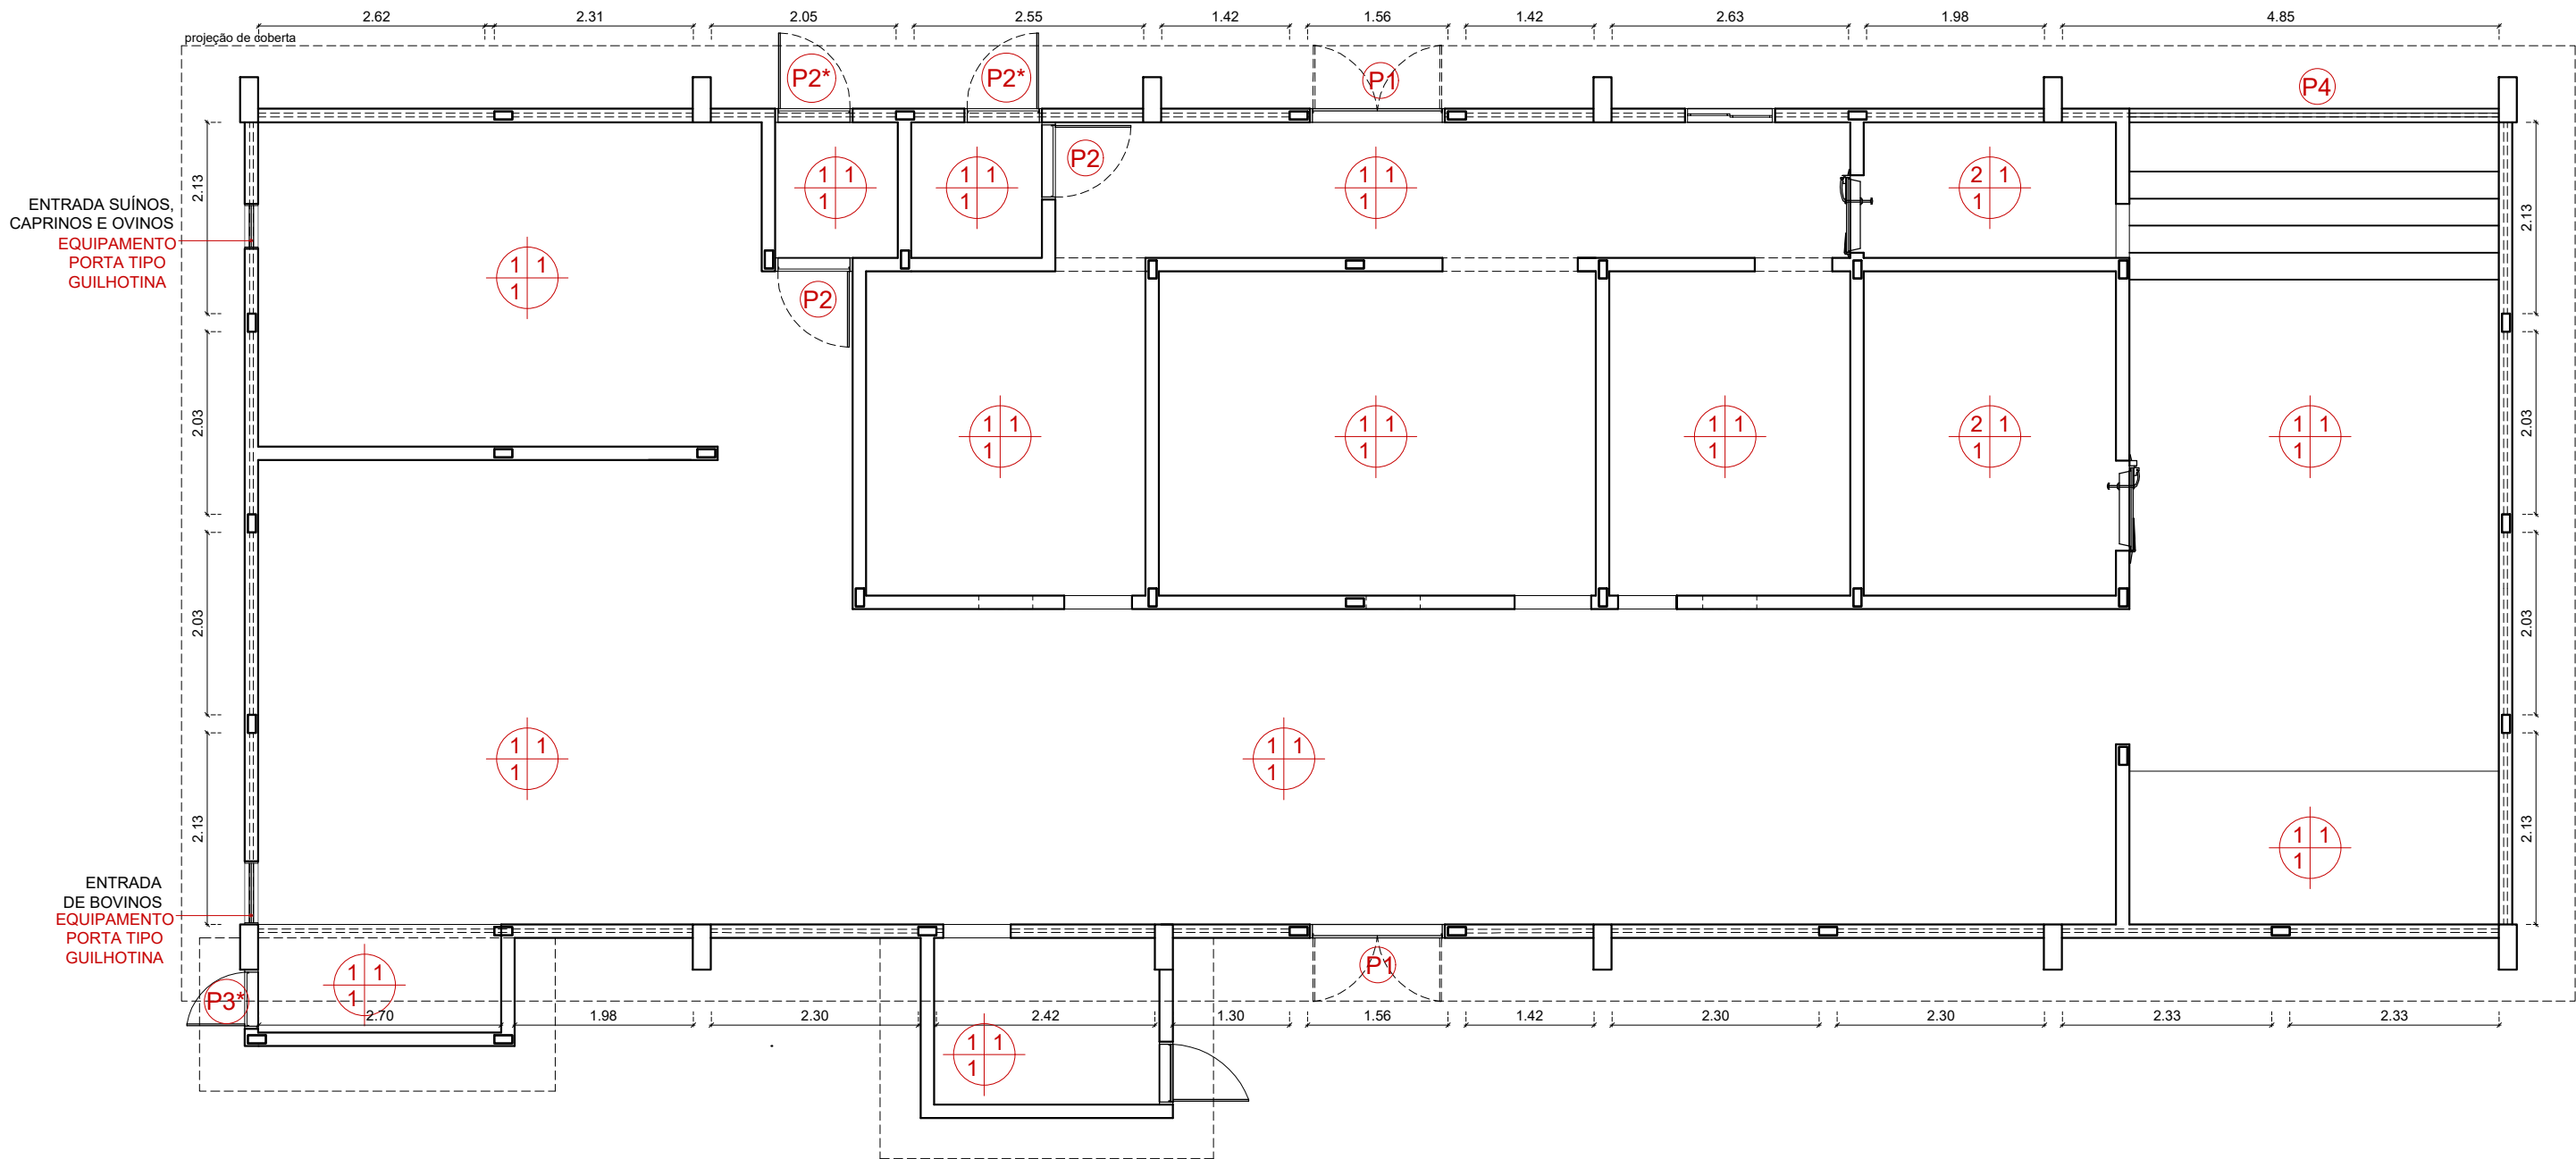

Planta Baixa Acabamento e esquadrias
escala 1/75

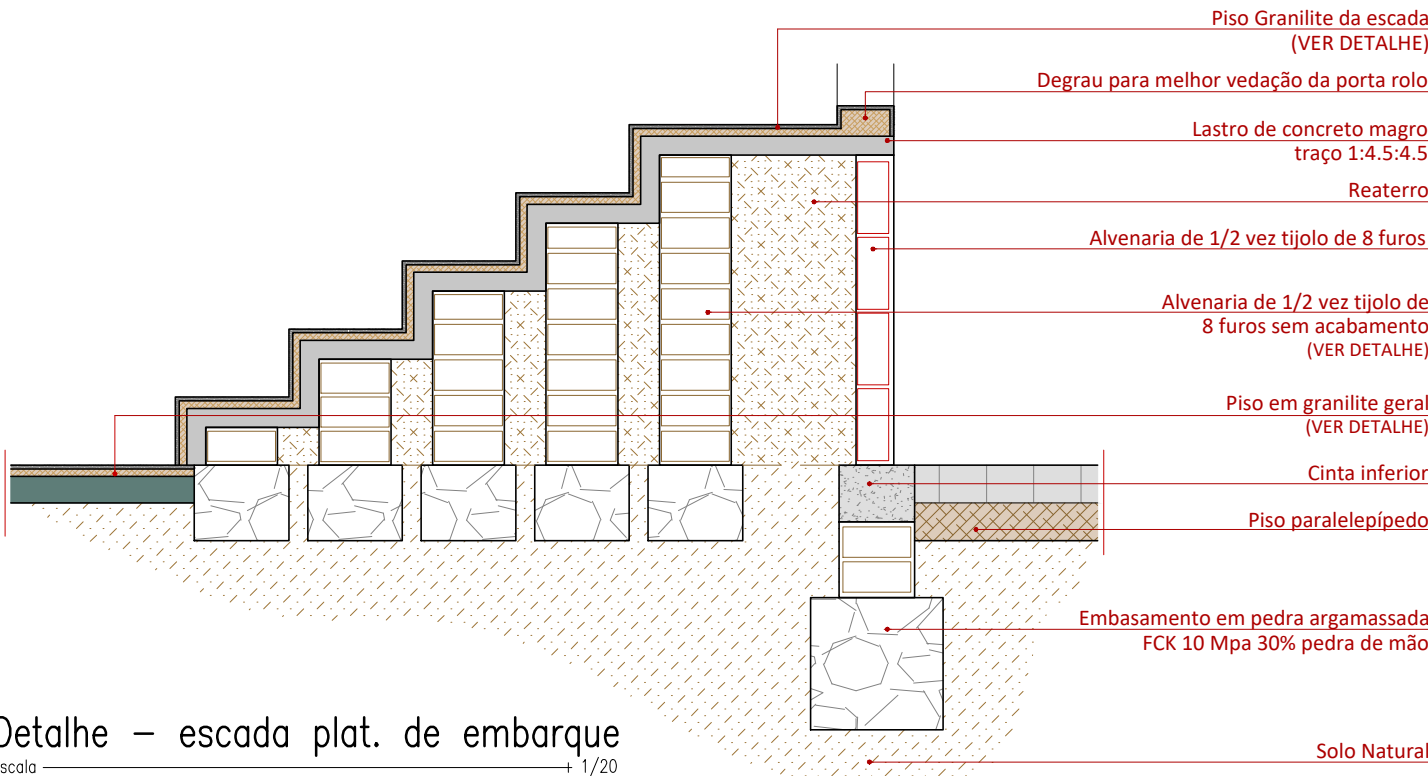


Detalhe - escada plat. de embarque
escala 1/20

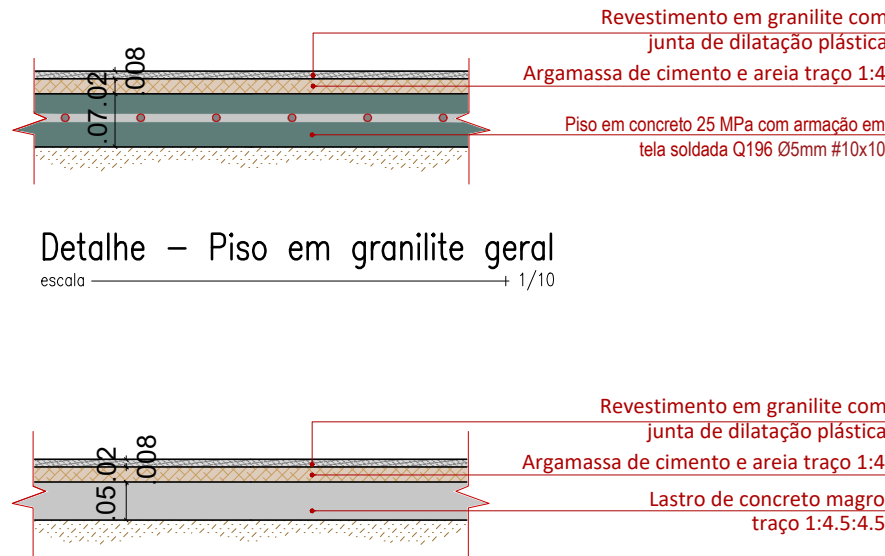


Detalhe - Piso em granilite geral
escala 1/10


Detalhe - Piso em granilite escada
escala 1/10

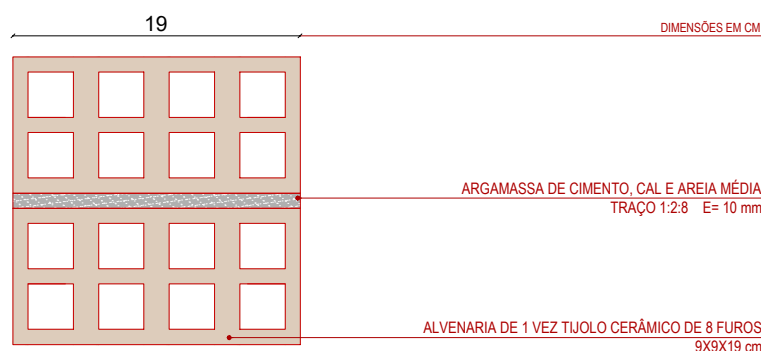

Detalhe - Fundação alvenarias galpão
escala 1/5

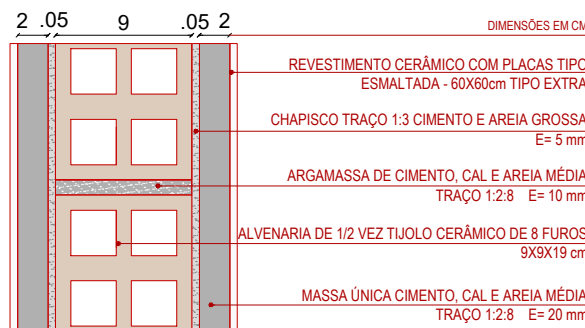

Detalhe - Alvenaria com revestimento
escala 1/5

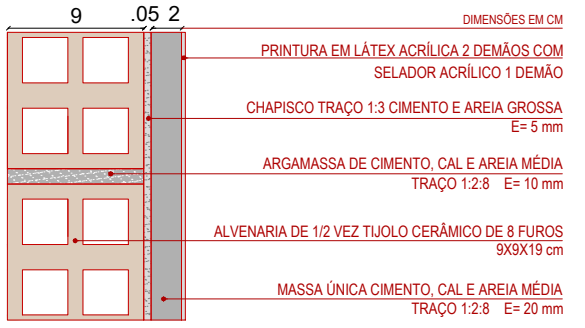

Detalhe - Alvenaria externa e das câmaras
escala 1/5

QUADRO DE ESPECIFICAÇÕES	
	PISO PAREDE TETO
PISO	01 - Piso Granilite e=8mm sobre argamassa de cimento e areia traço 1:4 e=2cm incluso junta de dilatação plástica
PAREDE	01 - Revestimento cerâmico com placas tipo esmaltada - 60X60cm tipo extra 02 - Pintura em látex acrílica, duas demãos com selador acrílico 1 demão
TETO	01 - Telha de fibrocimento sob estrutura de concreto pré-moldada

QUADRO DE ESQUADRIAS						
PORTAS						
TIPO	LARGURA	ALTURA	QUANT.	ÁREA (unid.)	TIPO	OBSERVAÇÕES
P1	1.50	2.10	2	3,15 m²	ABRIR 2 FOLHAS	CHAPA AÇO 14GSG
P2	0.80	2.10	2	1,68 m²	ABRIR	PORTA DE ALUMÍNIO
P2*	0.80	2.10	2	1,68 m²	ABRIR	P2 + TELA MOSQUETEIRO
P3*	0.60	2.10	1	1,26 m²	ABRIR	P3 + TELA MOSQUETEIRO
P4	4.10	2.10	1	8,61 m²	ROLO	AÇO CHAPA 24 RAIADA

* OBS.: IMPLANTAÇÃO DE TELA DE FIBRA DE VIDRO TIPO MOSQUETEIRO C/ MOLDURA EM MADEIRA SEGUINDO AS MESMAS DIMENSÕES DA TABELA NAS PORTAS P2* E P3*. (VER DETALHE)

ABERTURAS					
TIPO	LARGURA	ALTURA	QUANT.	TIPO	OBSERVAÇÕES
GERAL	VARIÁVEL	0.60	62,61m	FIXA	GRADIL DE FERRO BARRA CHATA

JANELAS						
TIPO	LARGURA	ALTURA	PEITORIL	ÁREA	QUANT.	ESPECIFICAÇÕES
J01	1.00	0.30	1.10	0,30 m²	1	CORRER ALUMÍNIO COM FECHAMENTO EM VIDRO

OBS.: IMPLANTAÇÃO DE TELA DE FIBRA DE VIDRO TIPO MOSQUETEIRO COM MOLDURA EM MADEIRA SEGUINDO AS MESMAS DIMENSÕES DA TABELA NOS GRADIS DE FERRO. (VER DETALHE)

