

TERRAS BARTOLOMEU GUARRIDO

P2

P4

80

PB-366

TERRAS BARTOLOMEU GUARRIDO

125



P1

P3


TERRAS BARTOLOMEU GUARRIDO

125

PLANTA BAIXA GERAL
Escala 1/400

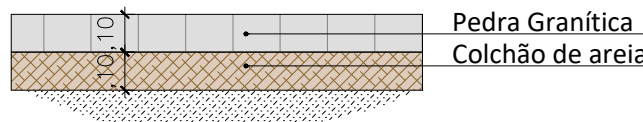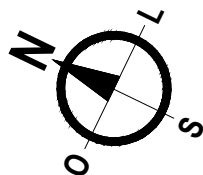


DET. PISO PARALELEPÍPEDO
Escala 1/20

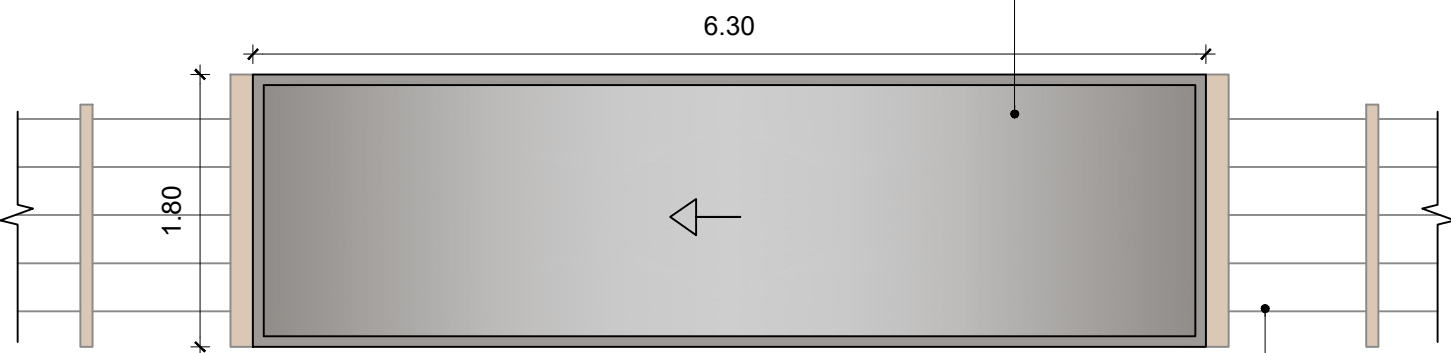

DET. PORTÃO ENTRADA PRINCIPAL
Escala 1/50

Portão de correr
ferro em chapa plana de
aço galvanizado 14GSG

Cerca a ser executada
pela Prefeitura Municipal

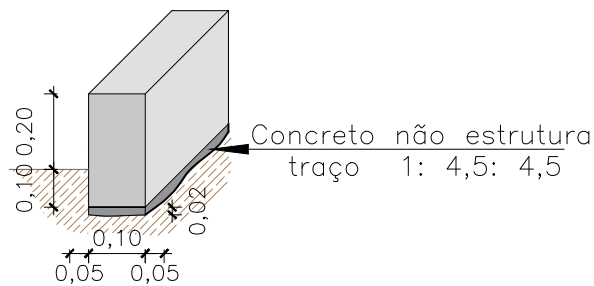

DET. MEIO-FIO GRANÍTICO SOBRE BASE DE
CONCRETO
Escala 1/20

NOTA TÉCNICAS – PROJETO MATADOURO

NT 01: A terraplenagem de toda a área necessária para a execução do Projeto de Construção do Matadouro Público deste município serão executados através de recursos próprios municipais.

LEGENDA

PAV. PARALELEPÍPEDO	260,58 m²
MEIO-FIO GRANÍTICO	92,98 m
A SER EXECUTADO COM RECURSOS DESTE CONVÊNIO	
A SER EXECUTADO COM RECURSOS PRÓPRIOS	
A SER EXECUTADO EM FUTURAS ETAPAS	

Documento assinado digitalmente
gov.br MICHAEL JACKSON MAMEDE SOUZA
Data: 11/03/2024 15:21:02-0300
Verifique em <https://validar.iti.gov.br>

RESPONSÁVEL TÉCNICO:

PROPRIETÁRIO:

PRANCHA	PREFEITURA MUNICIPAL DE COREMAS – PB				
	PROJETO DE CONSTRUÇÃO DE MATADOURO – 9389922022				
	PROJETO ARQUITETÔNICO – GERAL				
DESENHO	DATA	RESPONSÁVEL	RUBRICA		
PROJETO			ÁREA DO TERRENO	ÁREA ÚTIL	ÁREA CONSTRUÍDA
CÓPIA			10.000,00 M²	971,43 M²	871,58 M²
ESCALA:	DESENHO:				
1/400	PLANTA BAIXA GERAL				
1/20	DET. PISO PARALELEPÍPEDO				
1/50	DET. PORTÃO ENTRADA PRINCIPAL				
1/20	DET. MEIO-FIO GRANÍTICO SOBRE BASE DE CONCRETO				