


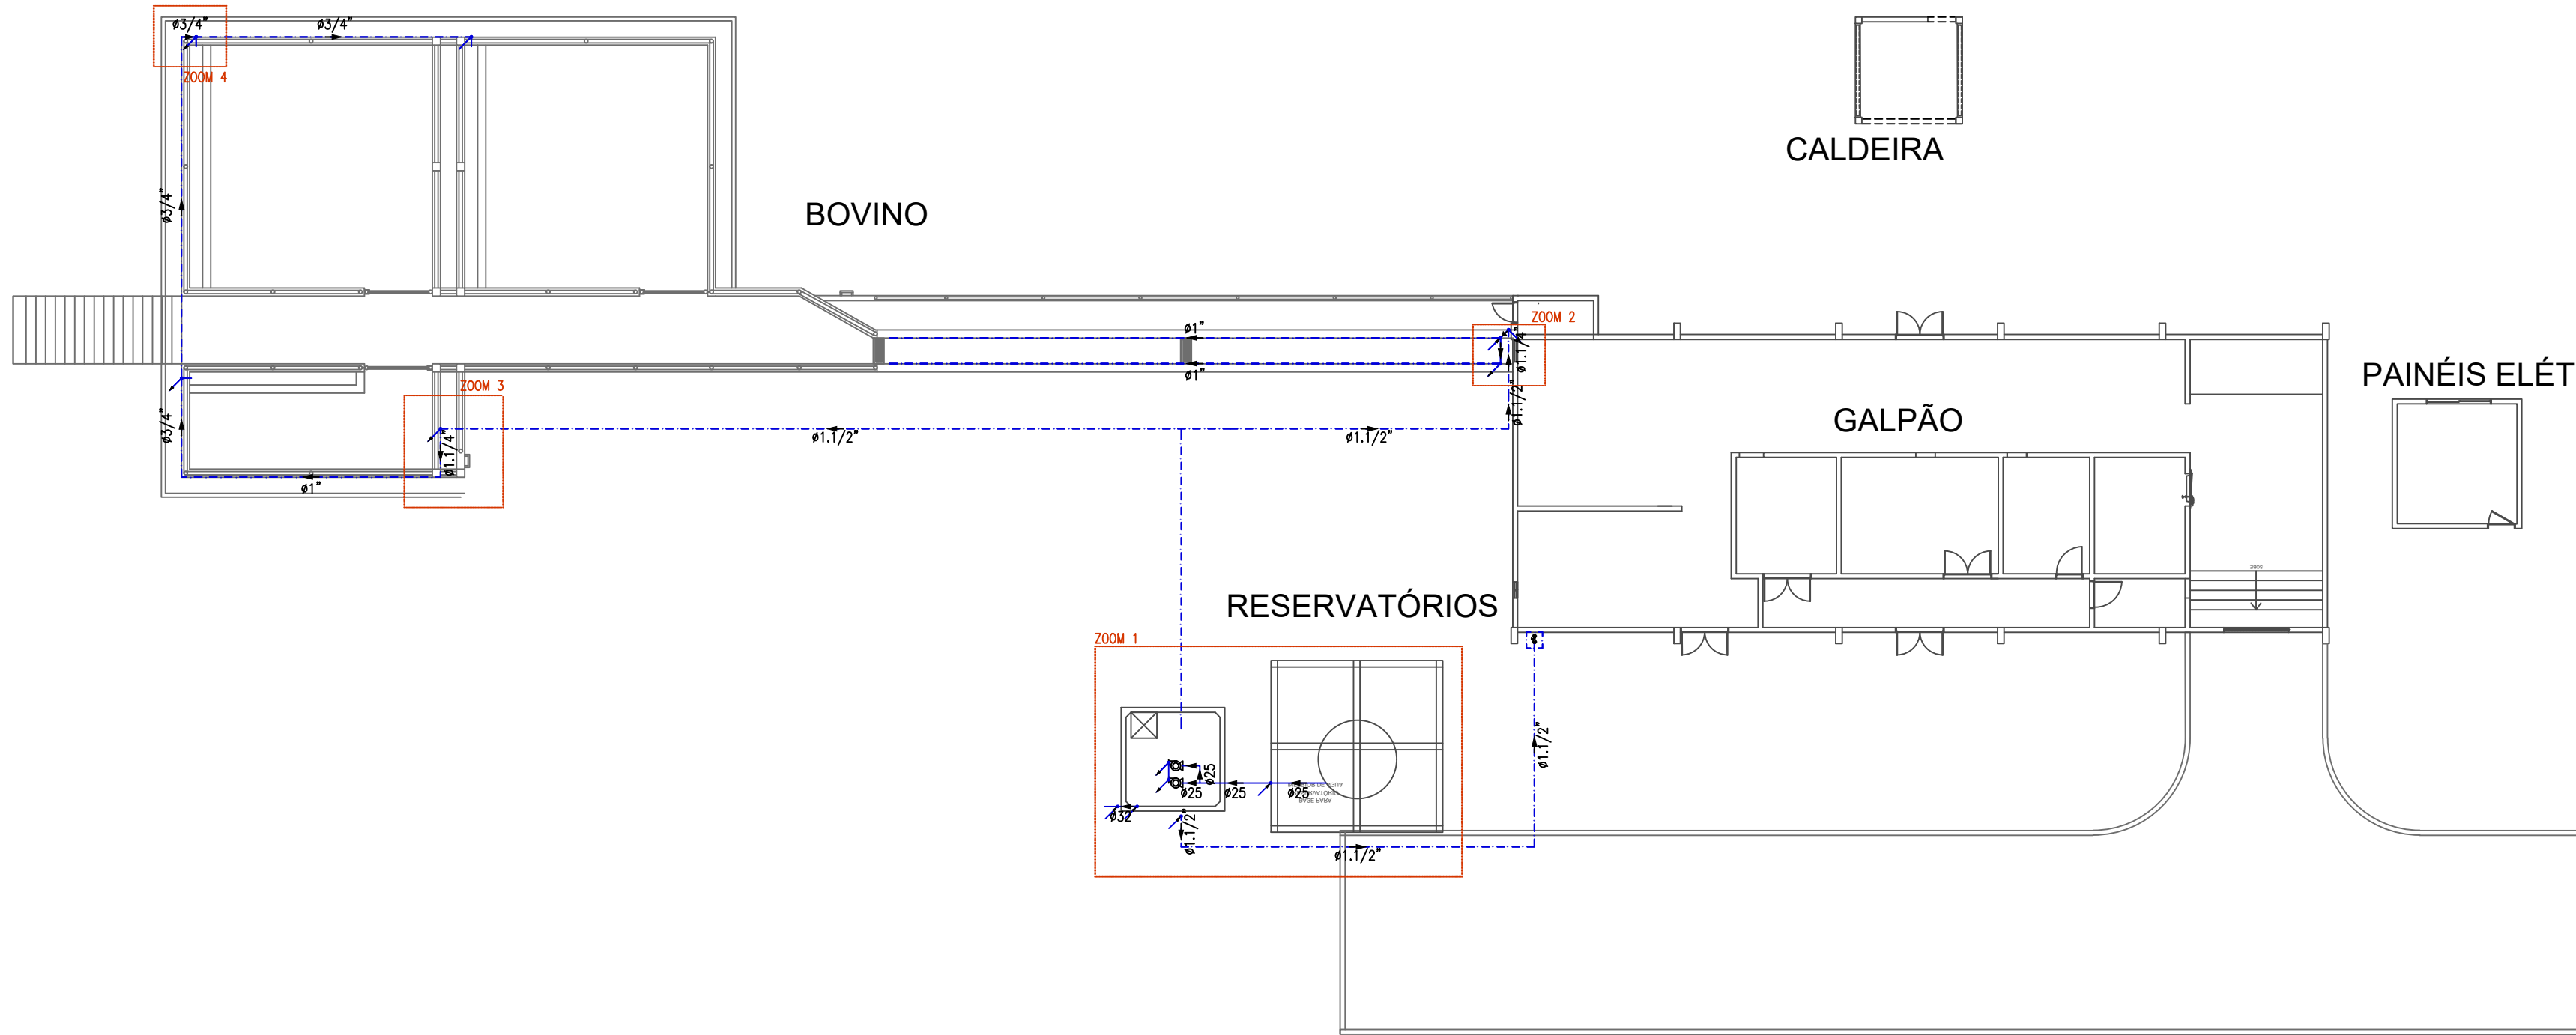

Planta Baixa Hidráulico – Área Externa

escala 1/175

Ø EM MILÍMETROS	Ø EM POLEGADAS
20 mm	3/4"
25 mm	1"
32 mm	1.1/4"
37.5 mm	1.1/2"
50 mm	2"

NOTAS TÉCNICAS - PROJETO HIDRÁULICO MATADOURO PÚBLICO

- **NT 01:** A execução da Instalação Hidráulica desde entrada d'água existente até o Reservatório Inferior, necessário para o Projeto de Construção do Matadouro Público serão executados através de recursos próprios municipais.
- **NT 02:** Os equipamentos necessários para o pleno funcionamento do galpão: As portas guilhotinas, suas instalações elétricas e seus respectivos dispositivos hidrossanitários serão executadas através de recursos próprios municipais.

RESPONSÁVEL TÉCNICO:

PROPRIETÁRIO:

PRANCHA	PREFEITURA MUNICIPAL DE COREMAS – PB				
	PROJETO DE CONSTRUÇÃO DE MATADOURO – 9389922022				
	PROJETO HIDRÁULICO				
	DATA	RESPONSÁVEL		RUBRICA	
DESENHO					
PROJETO				ÁREA DO TERRENO	ÁREA ÚTIL
CÓPIA				10.000,00 M²	971,43 M²
ESCALA:		DESENHO:		ÁREA CONSTRUIDA	
1/175		PLANTA BAIXA HIDRÁULICO - ÁREA EXTERNA		871,58 M²	