


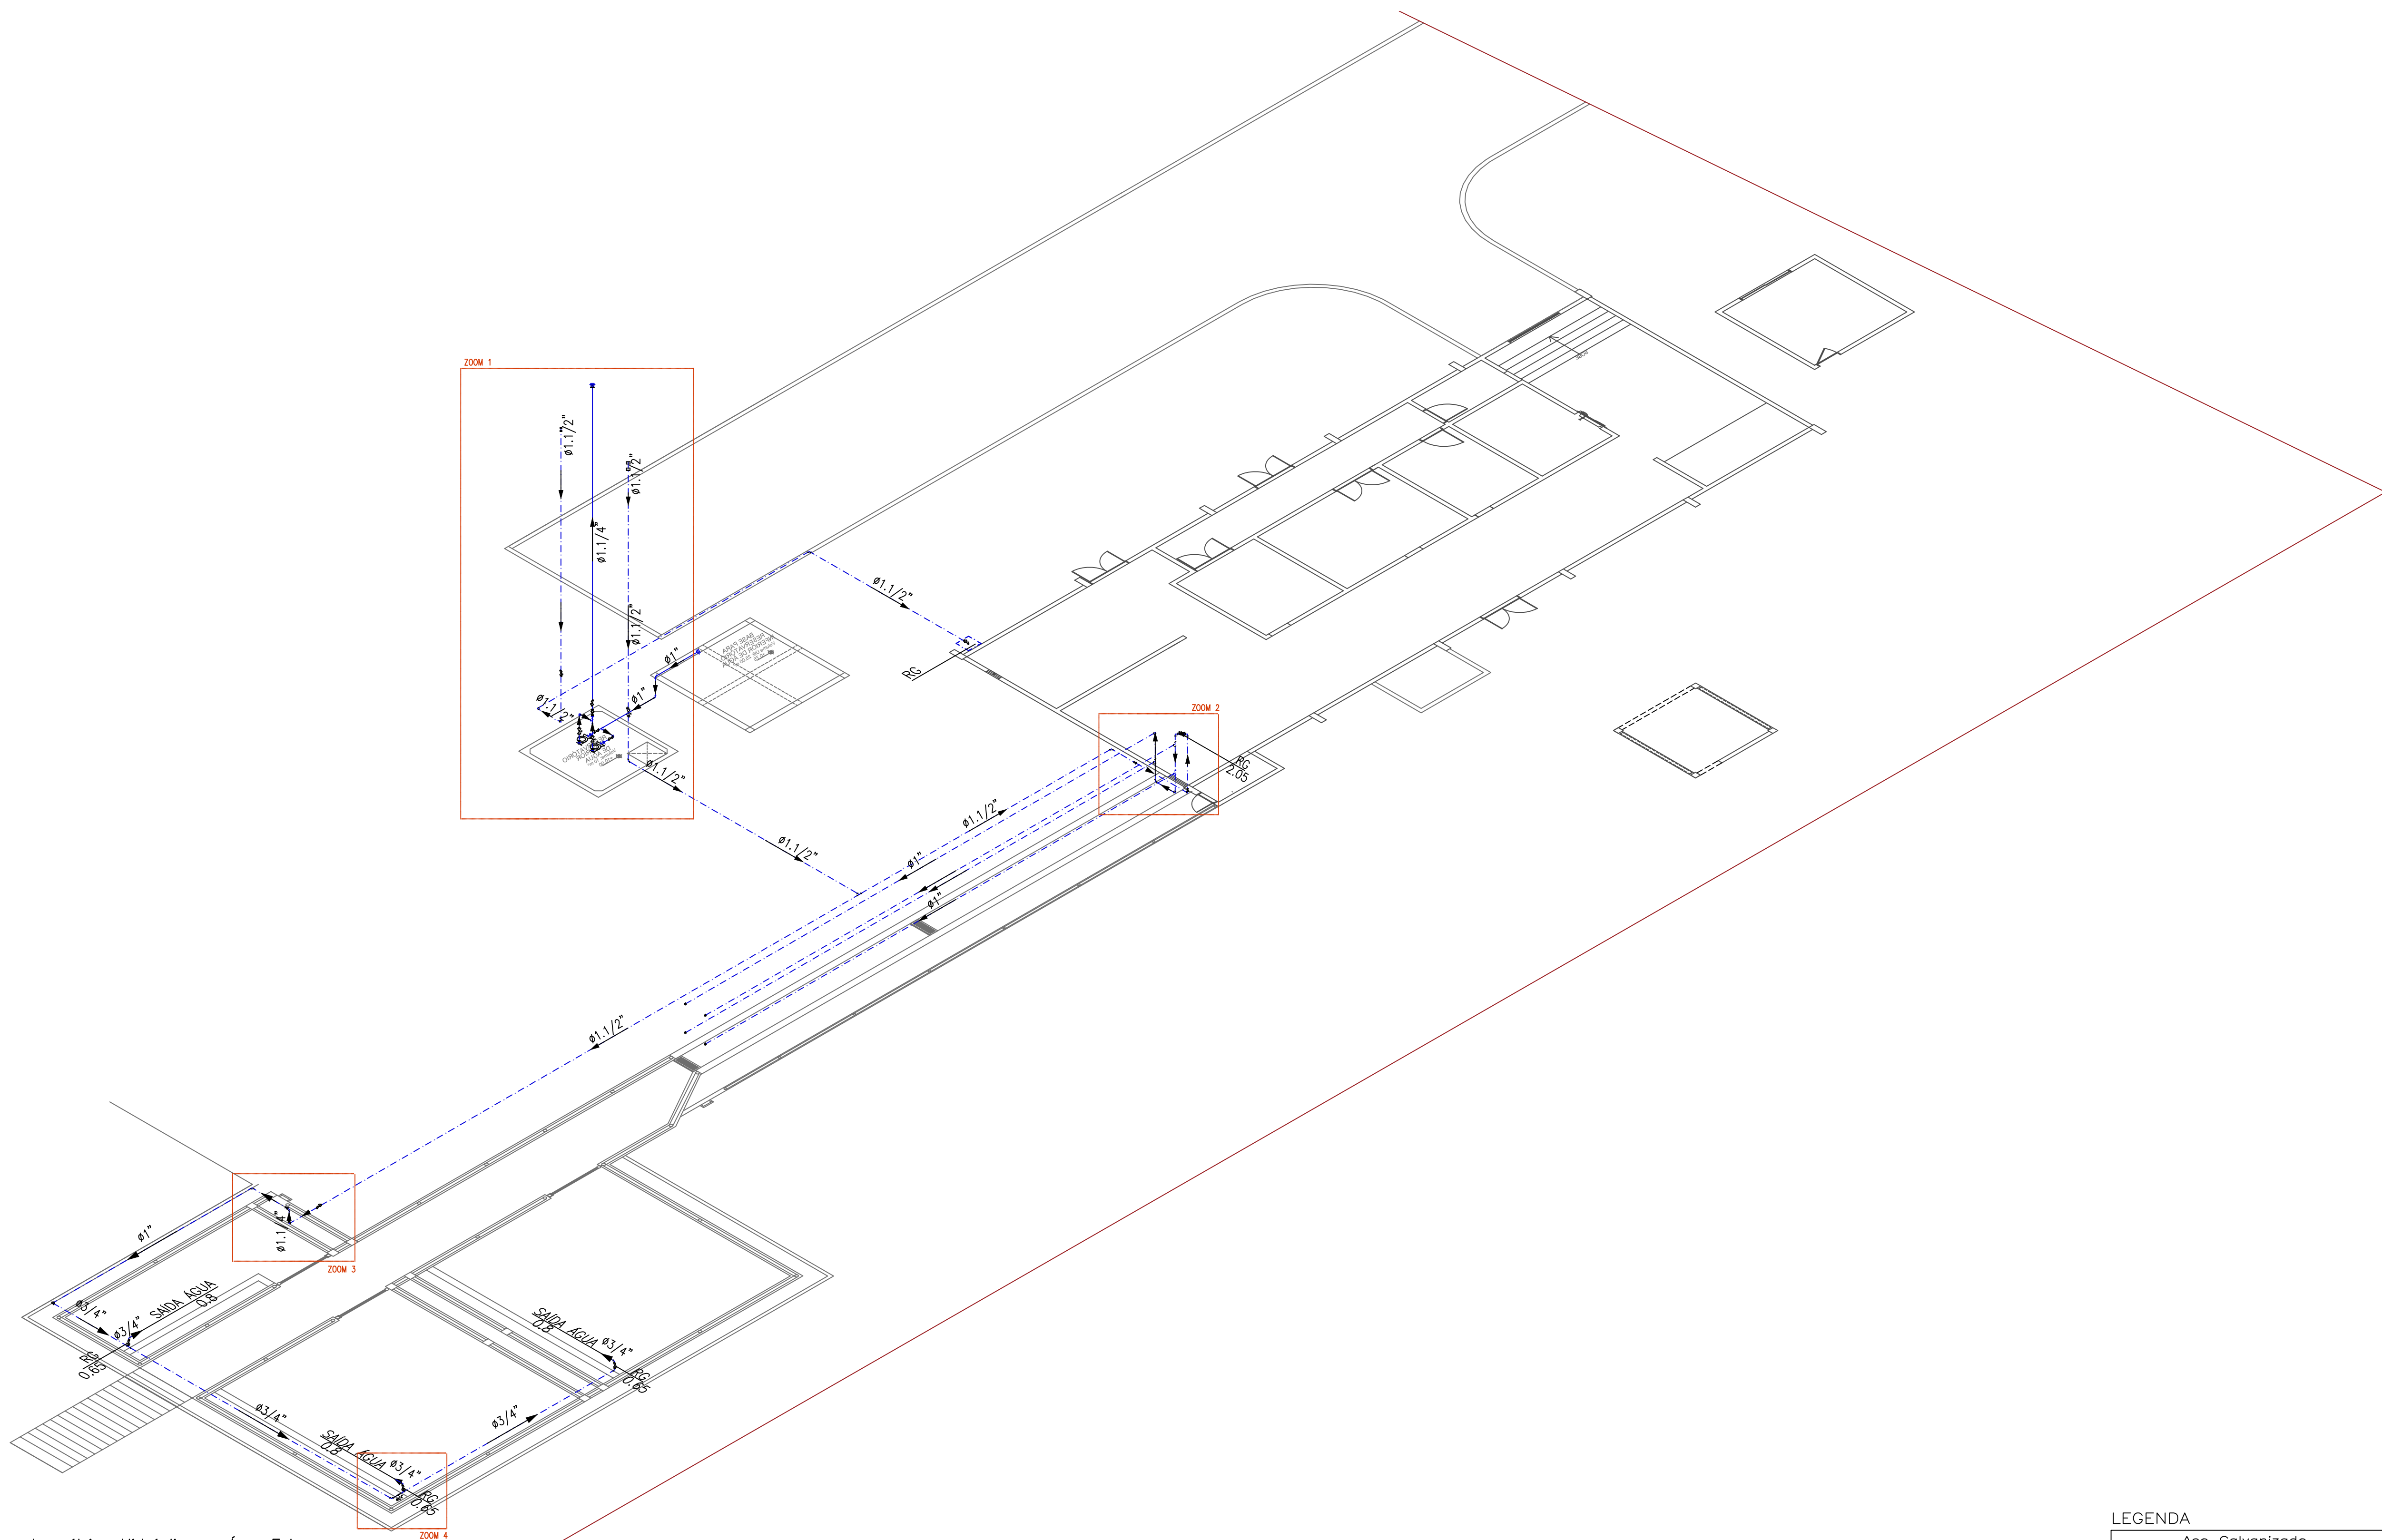

Isométrico Hidráulico – Área Externa

LISTA DE MATERIAIS – ALIMENTAÇÃO RESERV. SUPERIOR

PVC Soldável marrom			
Quant.	Und.	Dimensão	Descrição
8,82	m	25mm	Tubo PVC Soldável marrom (NBR 5648/pe CP19)
13,46	m	32mm	Tubo PVC Soldável marrom (NBR 5648/pe CP19)
1	pc	32mmx1"	Adaptador longo c/ flanges livres-ox.d'água
1	pc	20mmx3/4"	Adaptador longo c/ flanges livres-ox.d'água
8	pc	32mmx1"	Adaptador soldável curto bolsa e rosca
3	pc	25mm	Joelho 90
1	pc	32mm	Joelho 90
1	pc	32mmx1"	Luva com rosca
2	pc	32mmx25mm	Luva de redução
1	pc	25mm	Tê
1	pc	32mm	Tê
2	pc	25mm	União
3	pc	32mm	União
Aço Galvanizado			
Quant.	Und.	Dimensão	Descrição
6	pc	1"	Nípe Duplo
1	pc	3/4"	Torneira com Bola 3/4
Registros,Valv.,Hid			
Quant.	Und.	Dimensão	Descrição
3	pc	1"	Registro de Gaveta bruto
2	pc	3/4"	Registro Esfera Soldável
1	pc	1"	Valvula de retenção
Simbologia – Outros			
Quant.	Und.	Dimensão	Descrição
2	pc	1.1/4"	Bomba D'água 1/2 cv

LISTA DE MATERIAIS – ÁREA EXTERNA

PVC Soldável marrom			
Quant.	Und.	Dimensão	Descrição
14	pc	50mmx1.1/2"	Adaptador soldável curto bolsa e rosca
Aço Galvanizado			
Quant.	Und.	Dimensão	Descrição
2,06	m	1.1/4"	Tubo Aço Galvanizado
80,27	m	1.1/2"	Tubo Aço Galvanizado
4	pc	1"	Tubo Aço Galvanizado
4	pc	1.1/2"	Adaptador g/Colete D'água (parede=18cm)
1	pc	1.1/2"	Cotovelo 90
1	pc	1.1/4"	Cotovelo 90
1	pc	1"	Cotovelo 90
1	pc	1.1/2"x1.1/4"	Luva de Redução
1	pc	1.1/4"x1"	Luva de Redução
1	pc	1.1/2"	Tê 90
Registros,Valv.,Hid			
Quant.	Und.	Dimensão	Descrição
3	pc	1.1/2"	Registro de Gaveta bruto

LISTA DE MATERIAIS – CURRAL BOVINO

PVC Soldável marrom			
Quant.	Und.	Dimensão	Descrição
6	pc	25mmx3/4"	Adaptador soldável curto bolsa e rosca
Aço Galvanizado			
Quant.	Und.	Dimensão	Descrição
1,10	m	1.1/2"	Tubo Aço Galvanizado
0,50	m	1.1/4"	Tubo Aço Galvanizado
90,01	m	3/4"	Tubo Aço Galvanizado
23,73	m	3/4"	Tubo Aço Galvanizado
4	pc	1"	Bujão
2	pc	3/4"	Cotovelo 90
1	pc	1.1/2"	Cotovelo 90
1	pc	1.1/4"	Cotovelo 90
10	pc	1"	Cotovelo 90
1	pc	1.1/2"x1.1/4"	Luva de Redução
1	pc	1.1/4"x1"	Luva de Redução
1	pc	1"x3/4"	Luva de Redução
1	pc	1"	Tê
2	pc	1"	Tê 90
2	pc	3/4"	Tê 90
Registros,Valv.,Hid			
Quant.	Und.	Dimensão	Descrição
3	pc	3/4"	Registro de Gaveta bruto
1	pc	1.1/2"	Registro de Gaveta bruto

LISTA DE MATERIAIS – GALPÃO

PVC Soldável marrom			
Quant.	Und.	Dimensão	Descrição
4	pc	50mmx1.1/2"	Adaptador soldável curto bolsa e rosca
Aço Galvanizado			
Quant.	Und.	Dimensão	Descrição
28,11	m	1.1/2"	Tubo Aço Galvanizado
2	pc	1.1/2"	Adaptador g/Colete D'água (parede=18cm)
3	pc	1.1/2"	Cotovelo 90
Registros,Valv.,Hid			
Quant.	Und.	Dimensão	Descrição
2	pc	1.1/2"	Registro de Gaveta bruto

Ø EM MILÍMETROS	Ø EM POLEGADAS
20 mm	3/4"
25 mm	1"
32 mm	1.1/4"
37,5 mm	1.1/2"
50 mm	2"

LEGENDA

Aço Galvanizado	
⌘	- Bujão 1" (Unifilar/em Planta)
⌘	- Cotovelo 90 1" (Unifilar/em Planta)
⌘	- Cotovelo 90 1" (Unifilar/em Planta)
⌘	- Cotovelo 90 1" (Unifilar/em Planta)
⌘	- Cotovelo 90 1.1/2" (Unifilar/em Planta)
⌘	- Cotovelo 90 1.1/4" (Unifilar/em Planta)
⌘	- Cotovelo 90 1.1/4" (Unifilar/em Planta)
⌘	- Cotovelo 90 3/4" (Unifilar/em Planta)
⌘	- Cotovelo 90 3/4" (Unifilar/em Planta)
⌘	- Luva de Redução 1"x3/4" (Unifilar/em Planta)
⌘	- Luva de Redução 1.1/2"x1.1/4" (Unifilar/em Planta)
⌘	- Luva de Redução 1.1/4"x1" (Unifilar/em Planta)
⌘	- Tê 1" (Unifilar/em Planta)
⌘	- Tê 90 1" (Unifilar/em Planta)
⌘	- Tê 90 3/4" (Unifilar/em Planta)
Registros,Valv.,Hid	
⌘	- Registro de Gaveta bruto 1.1/2" (Unifilar/em Planta)
⌘	- Registro de Gaveta bruto 3/4" (Unifilar/em Planta)
TUBULAÇÃO	
---	- Tubo Aço Galvanizado (Unifilar)
---	- Tubo PVC Soldável marrom (NBR 5648/pe CP19) (Unifilar)

RESPONSÁVEL TÉCNICO:			
PROPRIETÁRIO:			
PRANCHA			
PREFEITURA MUNICIPAL DE COREMAS – PB			
PROJETO DE CONSTRUÇÃO DE MATADOURO – 9389922022			
PROJETO HIDRÁULICO			
DATA	RESPONSÁVEL	RUBRICA	
DESENHO			
PROJETO			
CÓDIGO		ÁREA DO TERRENO	ÁREA GRL. CONSTRUIDA
ESCALA	DESENHO:	10.000,00 M ²	971,43 M ²
1/125	ISOMÉTRICO HIDRÁULICO - ÁREA EXTERNA		