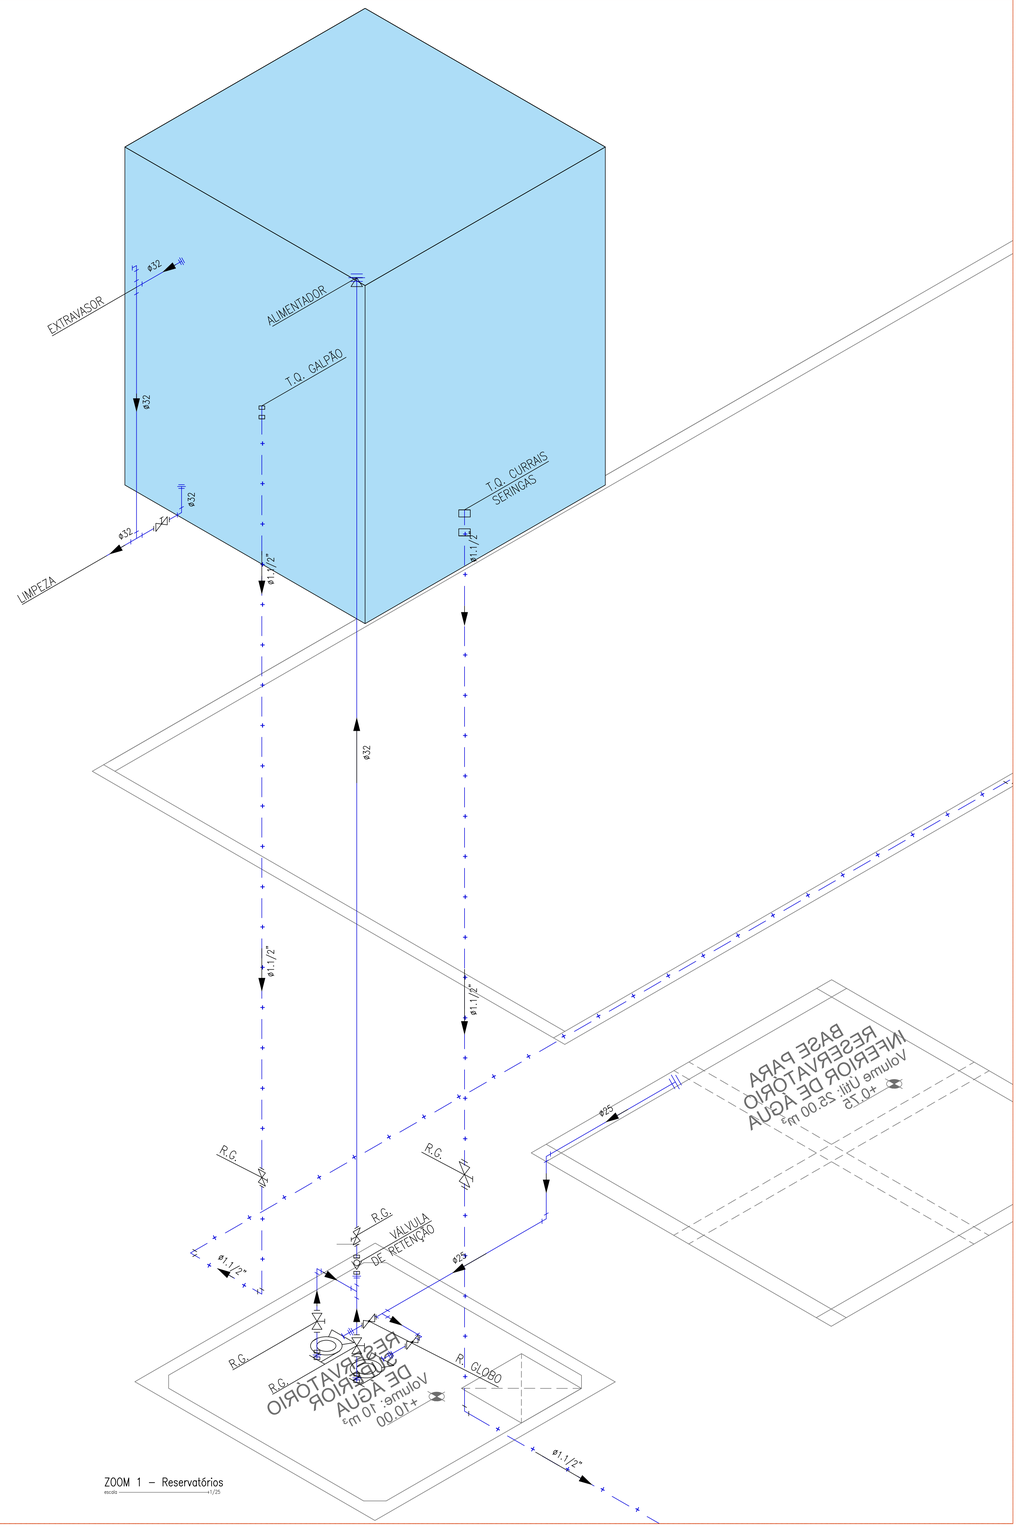

ZOOM 1 – Reservatórios
escala ——————— 1/25

Ø EM MILÍMETROS	Ø EM POLEGADAS
20 mm	3/4"
25 mm	1"
32 mm	1.1/4"
37.5 mm	1.1/2"
50 mm	2"

LEGENDA – ALIMENTAÇÃO RESERV. SUPERIOR

PVC Soldável marrom	
	– Adaptador longo c/flanges livres–cx.d'água 25mmx3/4" (Unifilar/em Planta)
	– Adaptador longo c/flanges livres–cx.d'água 32mmx1" (Unifilar/em Planta)
	– Adaptador soldável curto bolsa e rosca 32mmx1" (Unifilar/em Planta)
	– Joelho 90 25mm (Unifilar/em Planta)
	– Joelho 90 32mm (Unifilar/em Planta)
	– Luva com rosca 32mmx1" (Unifilar/em Planta)
	– Luva de redução 32x25mm (Unifilar/em Planta)
	– Tê 25mm (Unifilar/em Planta)
	– Tê 32mm (Unifilar/em Planta)
	– União 25mm (Unifilar/em Planta)
	– União 32mm (Unifilar/em Planta)
Aço Galvanizado	
	– Niple Duplo 1" (Unifilar/em Planta)
	– Niple Duplo 1" (Unifilar/em Planta)
	– Torneira com Bóia 3/4 3/4" (Unifilar/em Planta)
Registros,Valv.,Hid	
	– Registro de Gaveta bruto 1" (Unifilar/em Planta)
	– Registro Esfera Soldável 3/4" (Unifilar/em Planta)
	– Válvula de retenção 1" (Unifilar/em Planta)
Simbologia – Outros	
	– Bomba D'água 1/2 cv 1.1/4" (Unifilar/em Planta)
TUBULAÇÃO	
	– Tubo PVC Soldável marrom (NBR 5648/pe CP19) (Unifilar)

SAÍDA DE ÁGUA EM RESERVATÓRIO DE CONCRETO

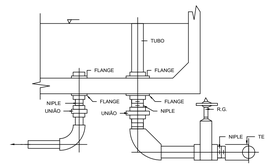

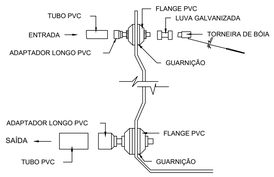

MONTAGEM DAS TUBULAÇÕES DE ENTRADA E SAÍDA COM TUBOS E CONEXÕES DE PVC EM CAIXAS DE ÁGUA COMUNS

Detalhe – Reservatórios
escala ——————— 1/5

Elevatória

Item	Descrição	Dimensões	Unid.
1	TUBO PVC SOLDÁVEL	25 mm	M
2	TE PVC SOLDÁVEL	25 mm	PÇ
3	REGISTRO ESFERA SOLDÁVEL	25 mm	PÇ
4	UNIÃO SOLDÁVEL	25 mm	PÇ
5	BUCHA DE REDUÇÃO SOLDÁVEL	32 mm x 25 mm	PÇ
6	ADAPTADOR SOLDÁVEL PARA REGISTRO	32 mm x 1"	PÇ
7	BOMBA D'AGUA – 1/2 CV	——	PÇ
8	NIPEL DUPLO DE FERRO GALVANIZADO	1"	PÇ
9	UNIÃO ROSCÁVEL PVC	1"	PÇ
10	REGISTRO DE GAVETA BRUTO	1"	PÇ
11	TUBO PVC ROSCÁVEL	1"	M
12	JOELHO 90° ROSCÁVEL	1"	PÇ
13	TE° ROSCÁVEL	1"	PÇ
14	VÁLVULA DE RETENÇÃO, TIPO VERTICAL	1"	PÇ
15	REGISTRO DE GAVETA BRUTO	1"	PÇ

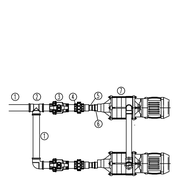

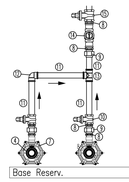

Detalhe – Reservatórios
escala ——————— 1/20

govbr Documento assinado digitalmente
MICHAEL JACKSON MAMEDE SOUZA
Data: 11/10/2024 15:52:08-0300
Verifique em https://validar.iti.gov.br

RESPONSÁVEL TÉCNICO:

PROPRIETÁRIO:

PRANCHA 3/5	PREFEITURA MUNICIPAL DE COREMAS – PB
	PROJETO DE CONSTRUÇÃO DE MATADOURO – 9389922022
	PROJETO HIDRÁULICO

	DATA	RESPONSÁVEL	RUBRICA		
DESENHO					
PROJETO			ÁREA DO TERRENO 10.000,00 M²	ÁREA ÚTIL 971,43 M²	ÁREA CONSTRUÍDA 871,58 M²
CÓPIA					

ESCALA:
1/25
1/20
1/5

DESENHO:
ZOOM 1 - RESERVATÓRIOS
DETALHE - RESERVATÓRIO
DETALHE - RESERVATÓRIO

9389922022_HID