



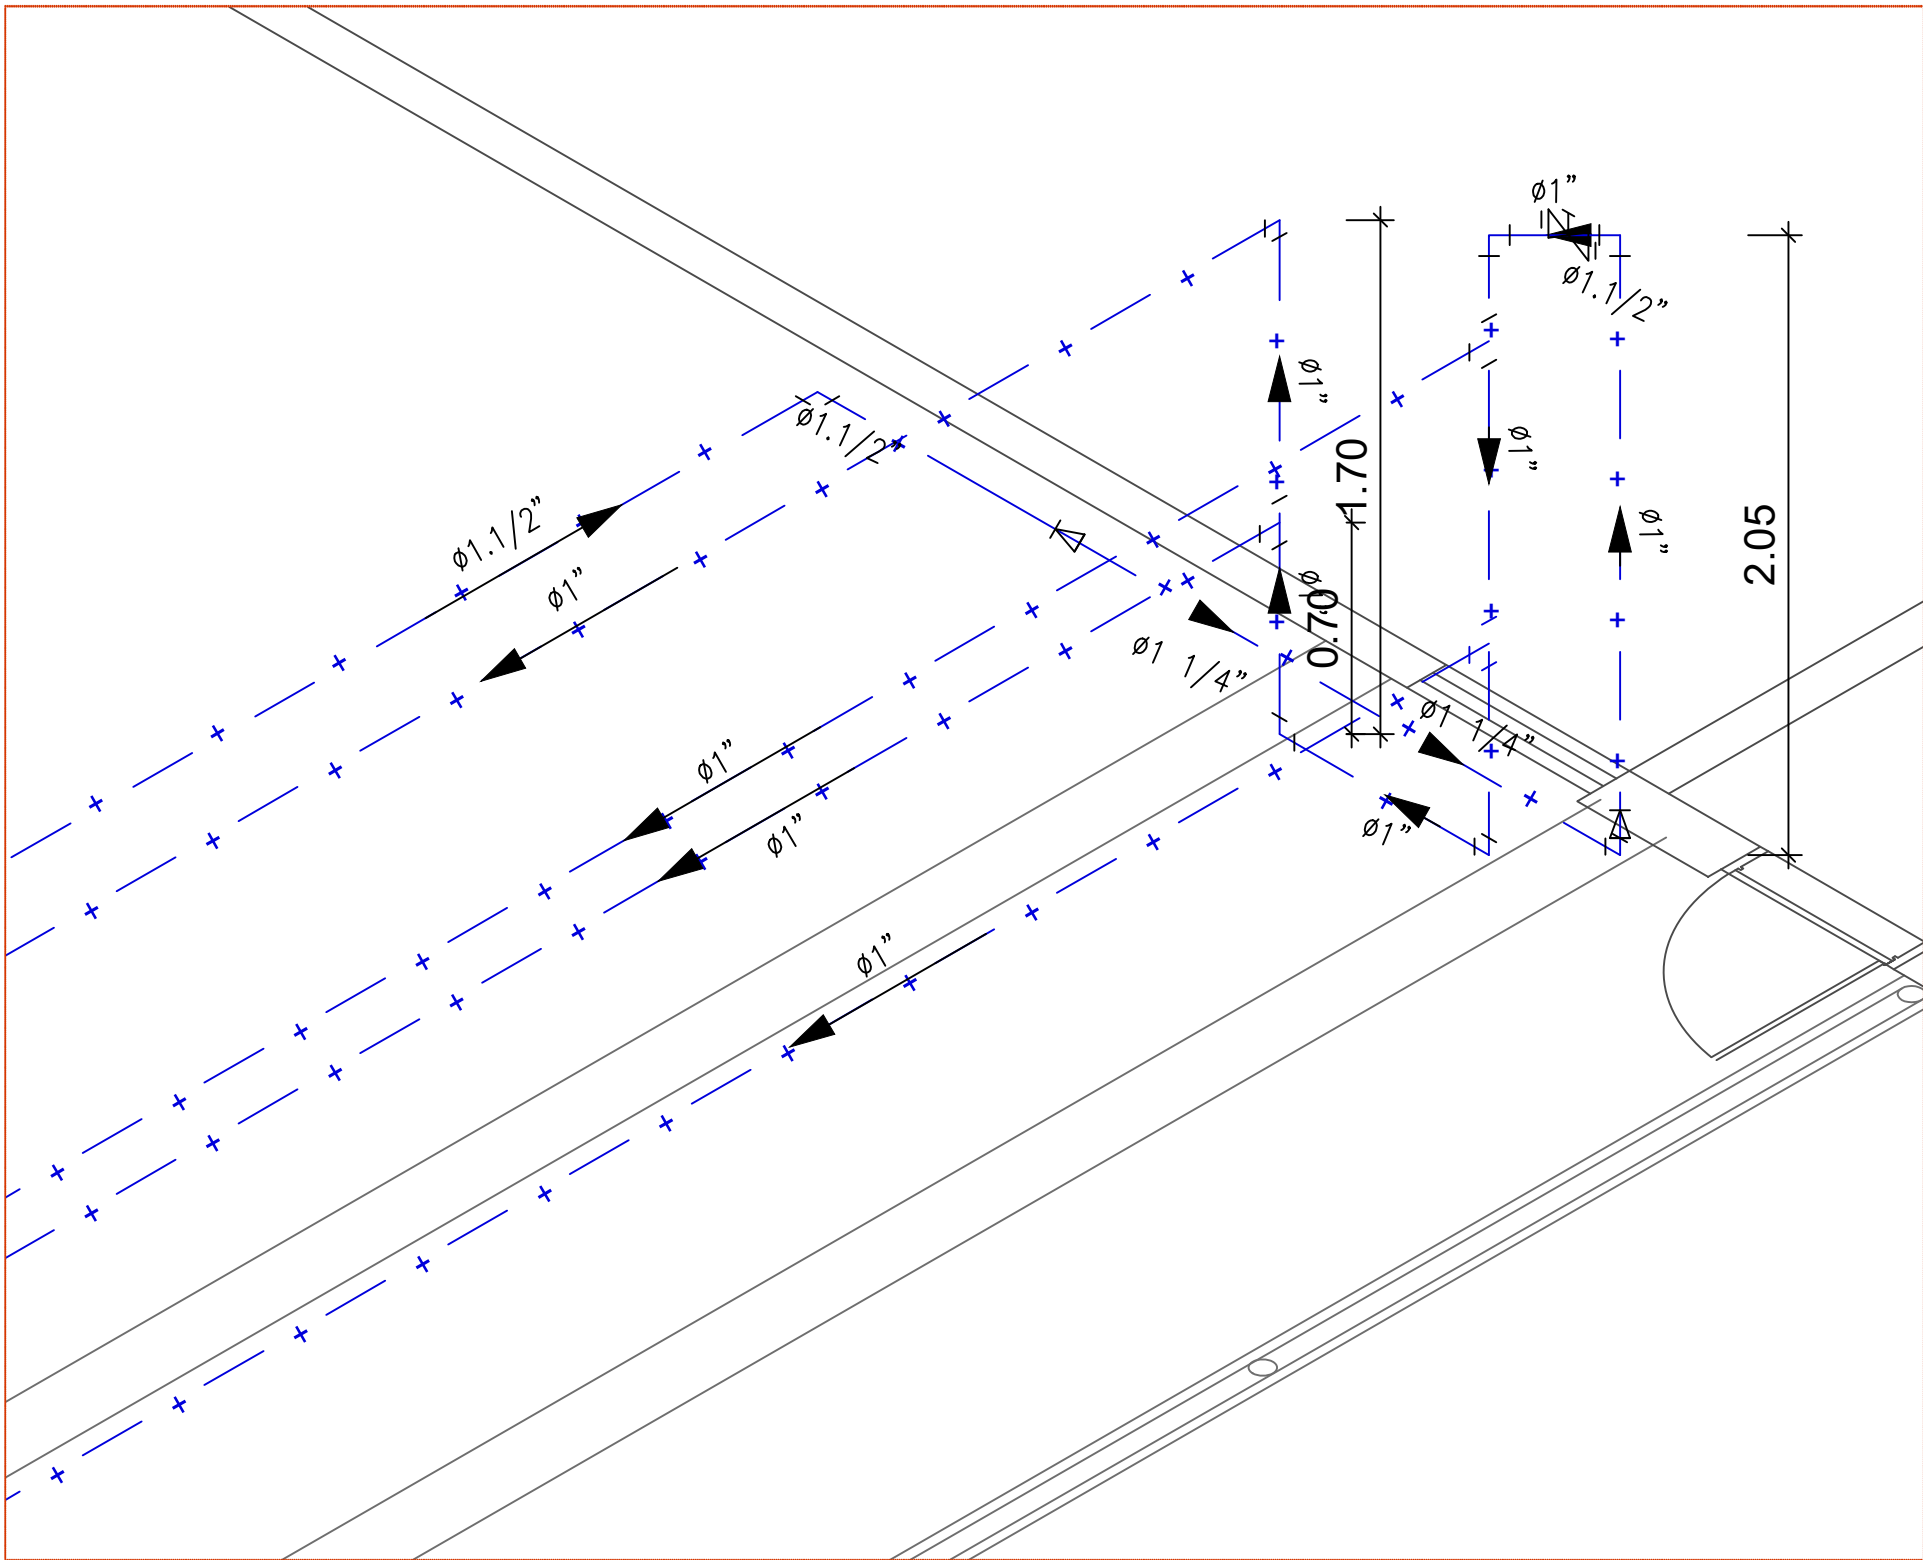


ZOOM 2 – Seringa do Curral Bovino

escala 1/25

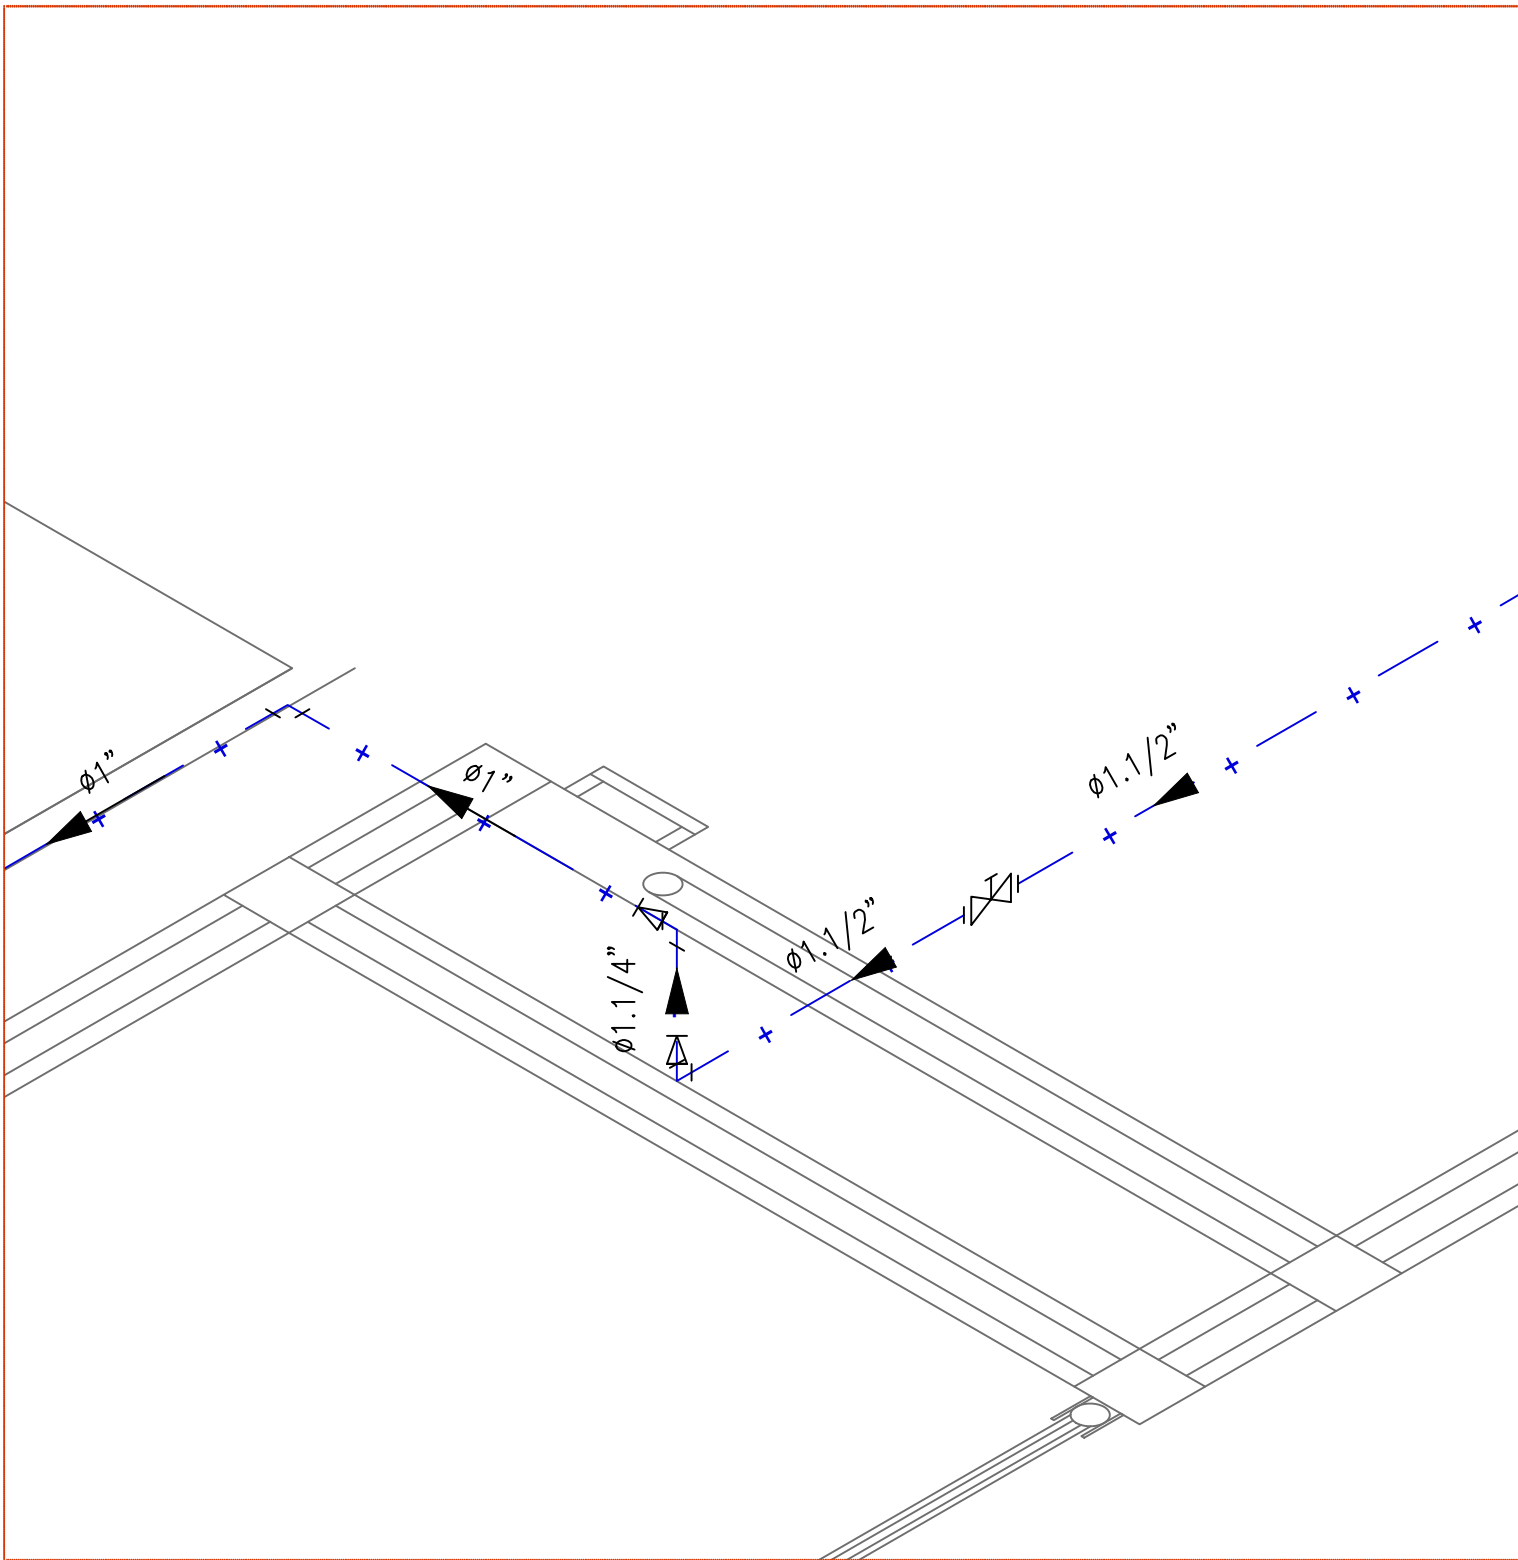

ZOOM 3 – Entrada do curral Bovino

escala 1/25

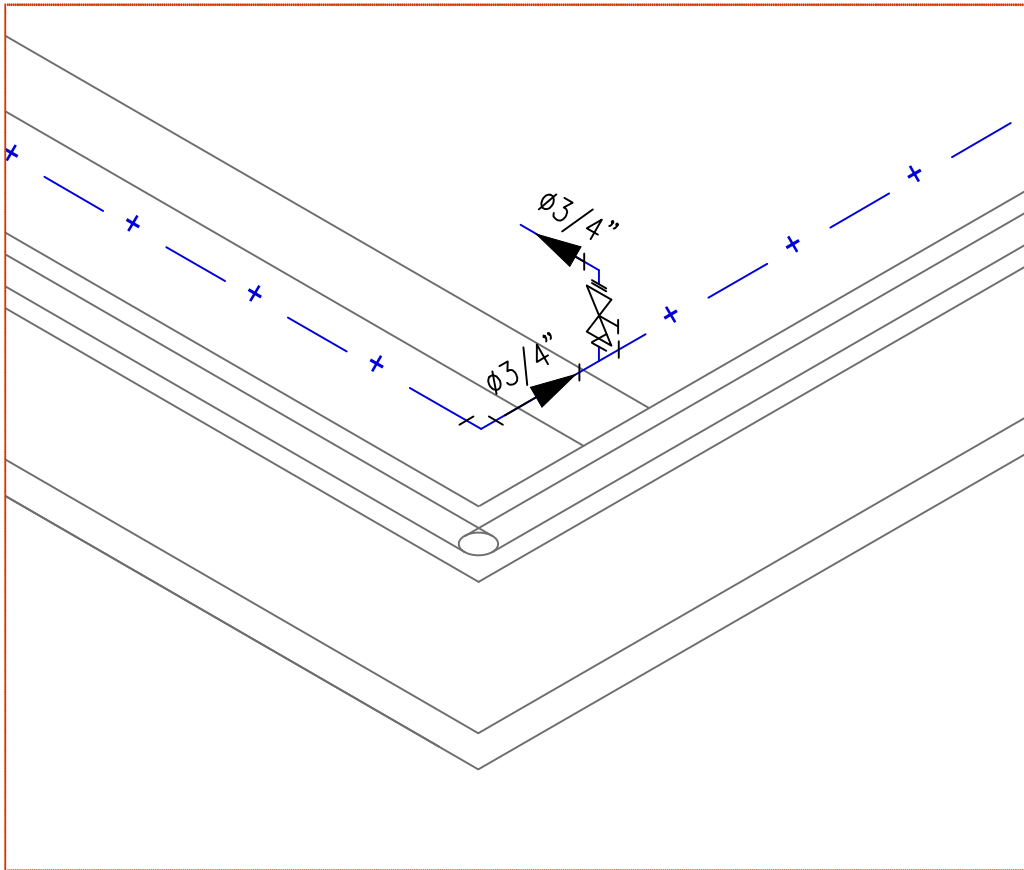

ZOOM 4 – Bebedouro Curral bovino

escala 1/25

LEGENDA

Aço Galvanizado	
	- Bujão 1" (Unifilar/em Planta)
	- Cotovelo 90 1" (Unifilar/em Planta)
	- Cotovelo 90 1" (Unifilar/em Planta)
	- Cotovelo 90 1" (Unifilar/em Planta)
	- Cotovelo 90 1.1/2" (Unifilar/em Planta)
	- Cotovelo 90 1.1/4" (Unifilar/em Planta)
	- Cotovelo 90 1.1/4" (Unifilar/em Planta)
	- Cotovelo 90 3/4" (Unifilar/em Planta)
	- Cotovelo 90 3/4" (Unifilar/em Planta)
	- Luva de Redução 1"x3/4" (Unifilar/em Planta)
	- Luva de Redução 1.1/2"x1.1/4" (Unifilar/em Planta)
	- Luva de Redução 1.1/4"x1" (Unifilar/em Planta)
	- Luva de Redução 1.1/4"x1" (Unifilar/em Planta)
	- Tê 1" (Unifilar/em Planta)
	- Tê 90 1" (Unifilar/em Planta)
	- Tê 90 3/4" (Unifilar/em Planta)
Registros,Valv.,Hid	
	- Registro de Gaveta bruto 1.1/2" (Unifilar/em Planta)
	- Registro de Gaveta bruto 3/4" (Unifilar/em Planta)
TUBULAÇÃO	
	- Tubo Aço Galvanizado (Unifilar)
	- Tubo PVC Soldável marrom (NBR 5648/pe CP19) (Unifilar)

Ø EM MILÍMETROS	Ø EM POLEGADAS
20 mm	3/4"
25 mm	1"
32 mm	1.1/4"
37.5 mm	1.1/2"
50 mm	2"

RESPONSÁVEL TÉCNICO:					
PROPRIETÁRIO:					
PRANCHA	PREFEITURA MUNICIPAL DE COREMAS – PB				
	PROJETO DE CONSTRUÇÃO DE MATADOURO – 9389922022				
	PROJETO HIDRÁULICO				
	DATA	RESPONSÁVEL		RUBRICA	
DESENHO					
PROJETO				ÁREA DO TERRENO	ÁREA ÚTIL
CÓPIA				10.000,00 M²	971,43 M²
ESCALA:		DESENHO:		ÁREA CONSTRUIDA	
1/25		ZOOM 2 - SERINGA DO CURRAL SUÍNO		871,58 M²	
1/25		ZOOM 3 - SERINGA DO CURRAL BOVINO			
1/25		ZOOM 4 E 5 - CURRAL BEBEDOUROS			