


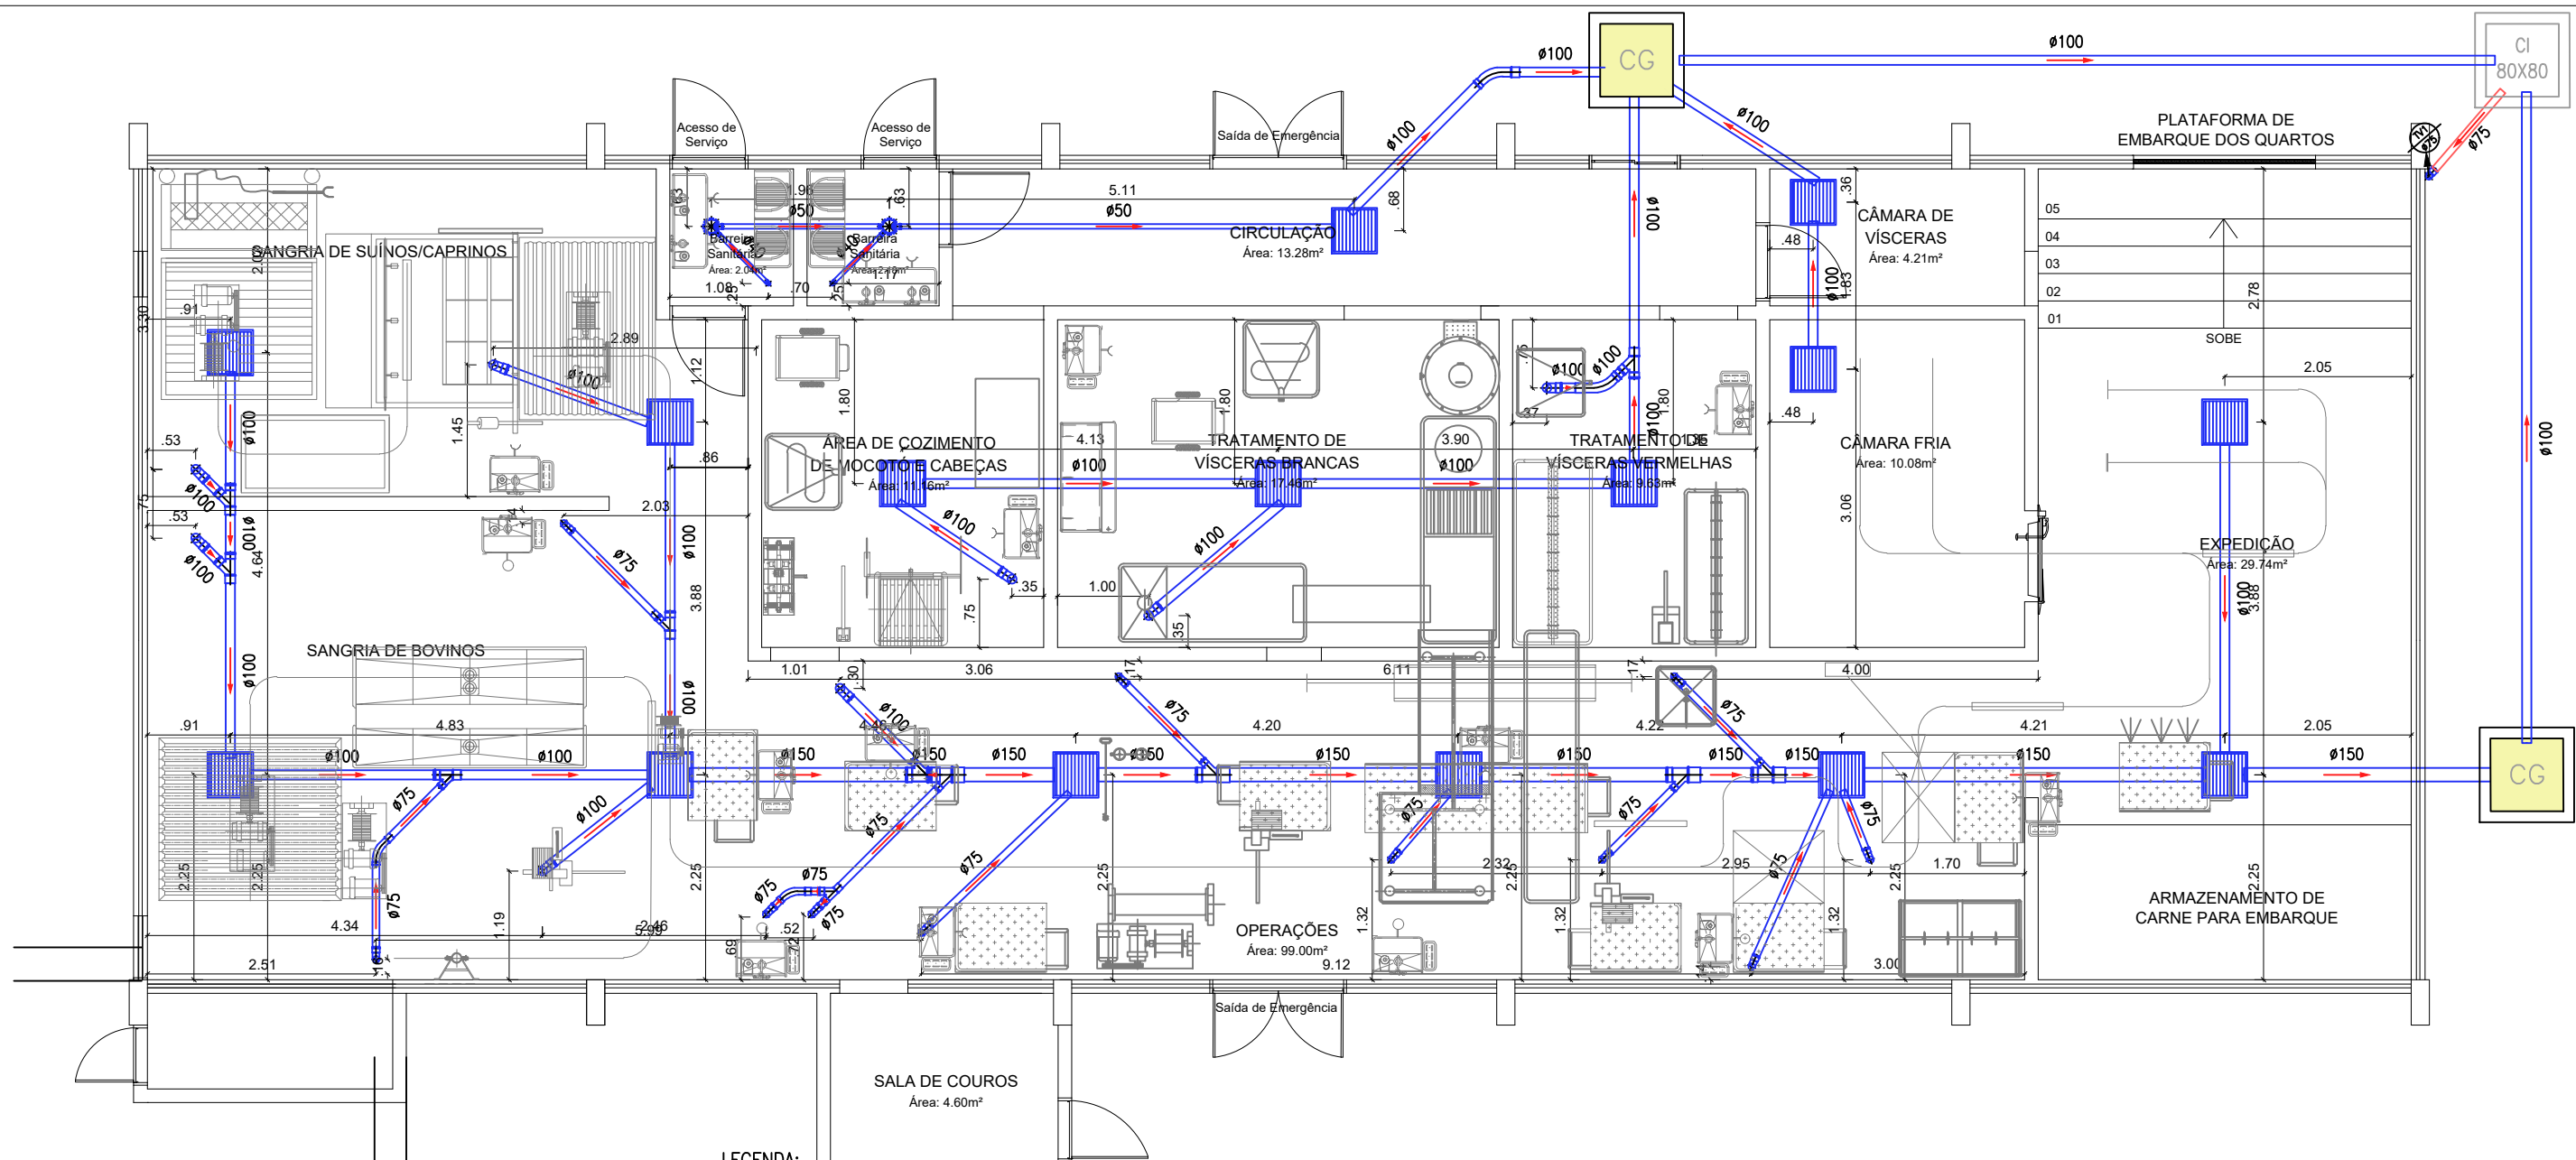

Planta Baixa Sanitário – Galpão

escala 1/75

Quant.	Und.	Dimensão	Descrição
6.47	m	50mm	Tubo PVC Soldável branco
15.89	m	150mm	Tubo PVC Soldável branco
1.44	m	40mm	Tubo PVC Soldável branco
38.95	m	100mm	Tubo PVC Soldável branco
30.38	m	75mm	Tubo PVC Soldável branco
2	pc	150x150x50mm	Caixa Sifonada com grelha
2	pc	75mm	Curva 45
2	pc	100mm	Curva 45
8	pc	100mm	Curva 90
11	pc	75mm	Curva 90
1	pc	75mm	Joelho 90
2	pc	40mm	Joelho 90 secundário
3	pc	100mmx75mm	Junção
1	pc	75mm	Junção
3	pc	100mm	Junção
6	pc	150mmx75mm	Junção
2	pc	40mm	Luva
7	pc	100mm	Luva
4	pc	75mm	Luva
5	pc	150mm	Luva
1	pc	50mmx40mm	Redução
1	pc	75mm	Terminal de ventilação

Quant.	Und.	Dimensão	Descrição
15	pc	—	Grelha (0.5x0.5)m
2.00	unid.	80x80cm	Caixa de gordura em alvenaria de tijolos

LEGENDA:

PVC Soldável branco	
	- Caixa Sifonada com grelha 150x150x50mm (Detalhado/em Planta)
	- Curva 45 100mm (Detalhado/em Planta)
	- Curva 45 75mm (Detalhado/em Planta)
	- Curva 90 100mm (Detalhado/Frontal)
	- Curva 90 75mm (Detalhado/Frontal)
	- Joelho 90 75mm (Detalhado/Frontal)
	- Joelho 90 secundário 40mm (Detalhado/Sobe)
	- Junção 100mm (Detalhado/em Planta)
	- Junção 100x75mm (Detalhado/em Planta)
	- Junção 150x75mm (Detalhado/em Planta)
	- Junção 75mm (Detalhado/em Planta)
	- Luva 100mm (Detalhado/em Planta)
	- Luva 150mm (Detalhado/em Planta)
	- Luva 40mm (Detalhado/em Planta)
	- Luva 75mm (Detalhado/em Planta)
	- Redução 50x40mm (Detalhado/em Planta)
	- Terminal de ventilação 75mm (Detalhado/Sobe)
PRUMADAS	
	Tubo Ventilação
TUBULAÇÃO	
	- Tubo PVC Soldável branco 100mm (Detalhado)
	- Tubo PVC Soldável branco 150mm (Detalhado)
	- Tubo PVC Soldável branco 40mm (Detalhado)
	- Tubo PVC Soldável branco 50mm (Detalhado)
	- Tubo PVC Soldável branco 75mm (Detalhado)
	- Tubo PVC Soldável branco 75mm de Ventilação

RESPONSÁVEL TÉCNICO:

PROPRIETÁRIO:

PRANCHA		PREFEITURA MUNICIPAL DE COREMAS – PB	
2/5		PROJETO DE CONSTRUÇÃO DE MATADOURO – 9389922022	
		PROJETO SANITÁRIO	
	DATA	RESPONSÁVEL	RUBRICA
DESENHO			
PROJETO			
CÓPIA			
ESCALA:			
1:50		DESENHO:	PLANTA BAIXA SANITÁRIO - GALPÃO
		ÁREA DE TERRENO	ÁREA CONSTRUÍDA
		10.000,00 M²	871,58 M²