



CONSTITUENTES

- * BASE DE CONCRETO ARMADO
- * ALVENARIA DE TIJOLOS DE 8 Furos
- * TUBO DE CONCRETO ARMADO PRÉ-MOLDADO
- * TUBO DE CONCRETO; MEIA SEÇÃO; Ø=30 CM
- * ARGAMASSA DE REVESTIMENTO DA ALVENARIA
- * LASTRO DE CONCRETO PARA REGULARIZAÇÃO DE FUNDO

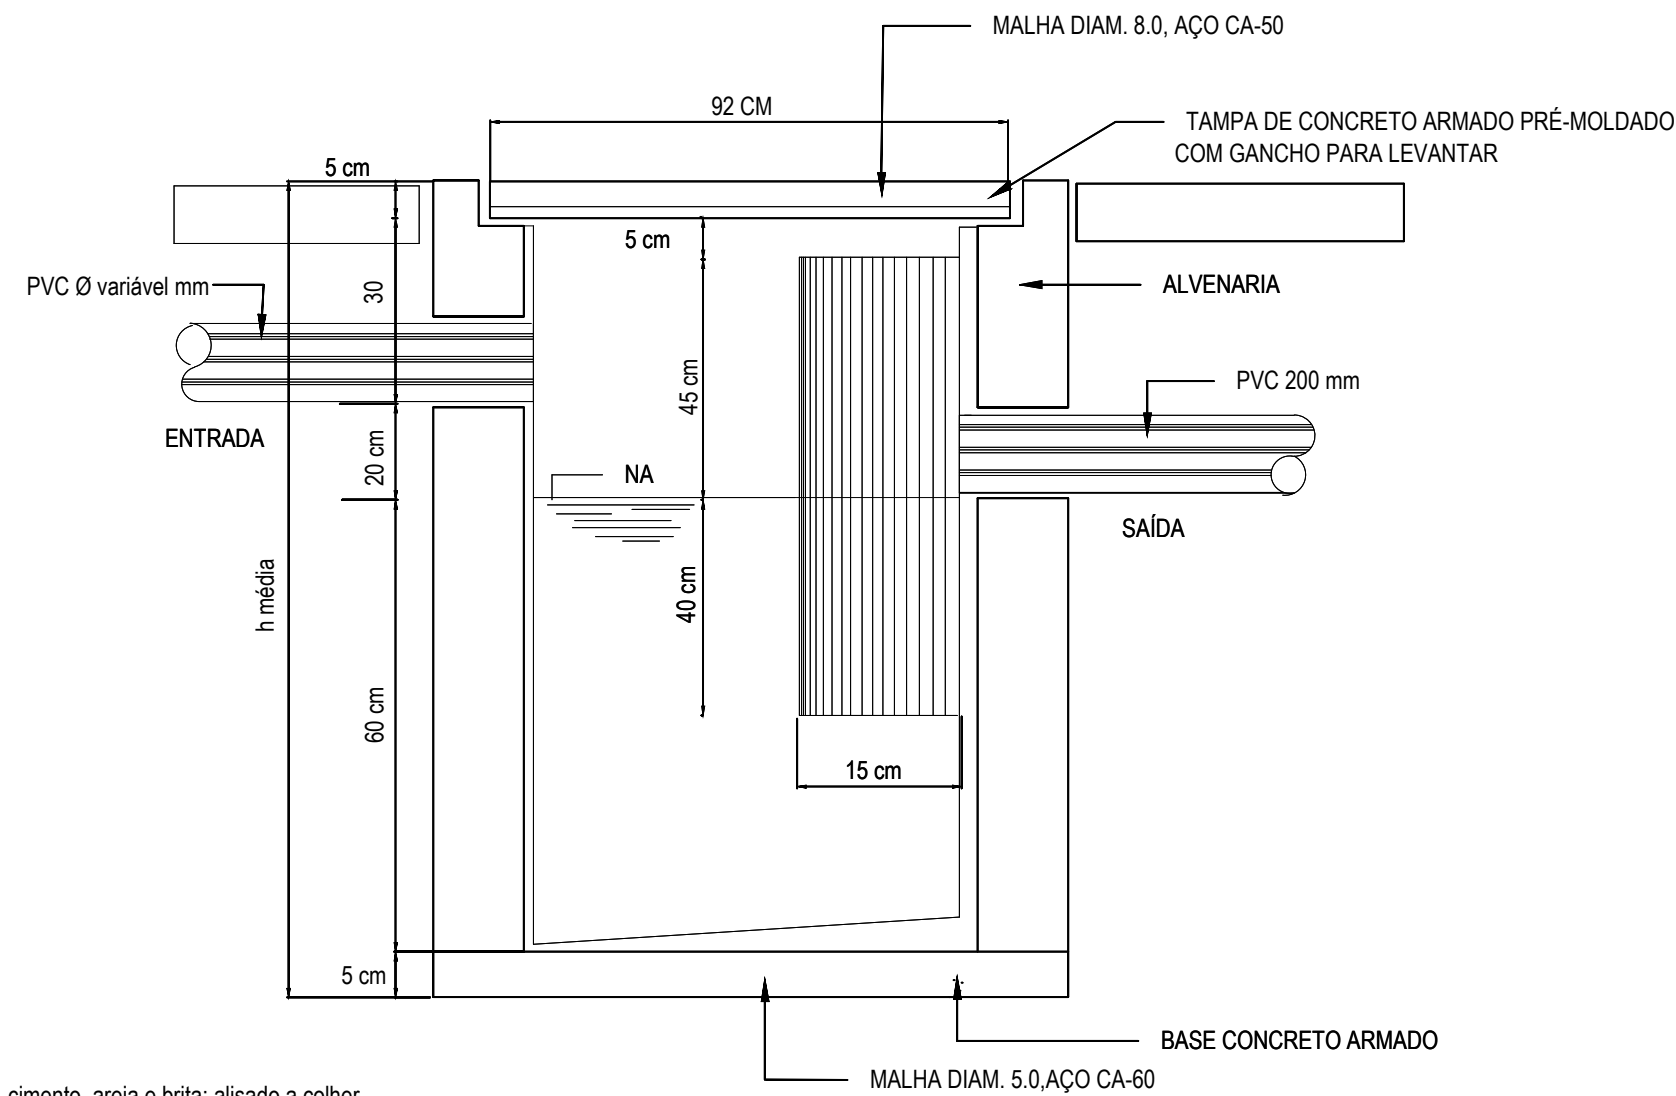


EXECUÇÃO

- * BASE
- Concreto 25 mpa, traco 1:2,3:2,7, cimento, areia e brita; alisado a colher.
 - Armção de aço CA-50; Ø= 5.0 mm, malha 10x10.
- * TAMPA
- Concreto 15 mpa, traco 1:3,4:3,5, cimento, areia e brita; alisado a colher.
 - Armção de aço CA-50; Ø= 8.0 mm.
- * ASSENTAMENTO DOS TIJOLOS: ARGAMASSA TRACO 1:2:8, CIMENTO, CAL E AREIA MÉDIA.
- * REVESTIMENTO DE ALVENARIA, CHAPISCO, TRAÇO 1:1:4 CIMENTO, CAL E AREIA, ARGAMASSA IMPERMEABILIZANTE, TRAÇO 1:3, CIMENTO E AREIA, COM ADIÇÃO DE ADITIVO IMPERMEABILIZANTE PARA ARGAMASSA

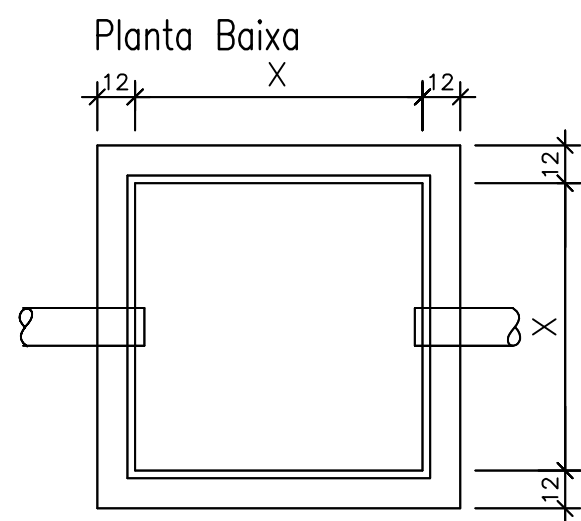


Corte

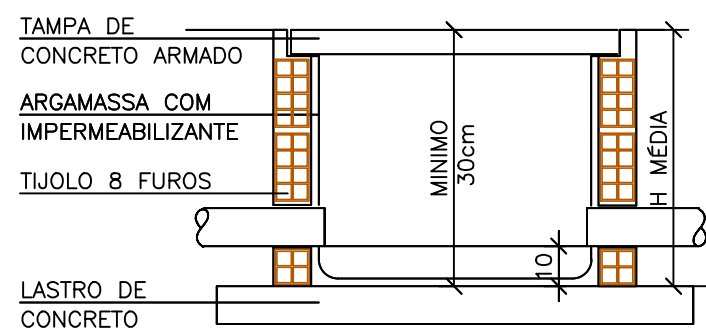

Detalhe – Caixas de Inspeção tipo 1
escala —————+ 1/20

CAIXA DE INSPEÇÃO – TIPO 01		☐
VARIÁVEL X (m)	QUANTIDADE (UNID.)	
1,00 m	02 unid.	
0,80 m	01 unid.	
0,60 m	01 unid.	
OBS.: ALTURA MÉDIA CONSIDERADA = X (m)		

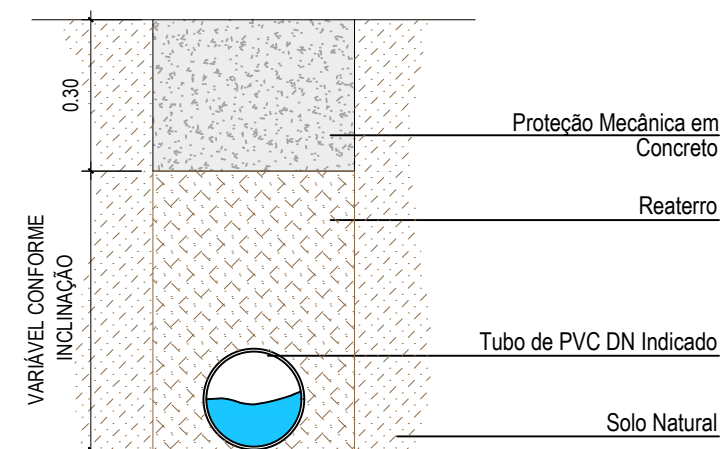

gov.br Documento assinado digitalmente
MICHAEL JACKSON MAMEDE SOUZA
Data: 11/03/2024 15:54:45-0300
Verifique em <https://validar.iti.gov.br>

Verifique em <https://validar.iti.gov.br>

Detalhe – Proteções mecânicas para tubos

escala _____ 1/15

RESPONSÁVEL TÉCNICO:			
PROPRIETÁRIO:			
PRANCHA	PREFEITURA MUNICIPAL DE COREMAS – PB		
	5/5		
	PROJETO DE CONSTRUÇÃO DE MATADOURO – 9389922022		
PROJETO SANITÁRIO			
	DATA	RESPONSÁVEL	RUBRICA
DESENHO			
PROJETO			
CÓPIA			
ESCALA:	DESENHO:	ÁREA DE TERRENO 10.000,00 M² ÁREA CONSTRUÍDA 871,58 M²	
INDICADAS	DETALHES		