




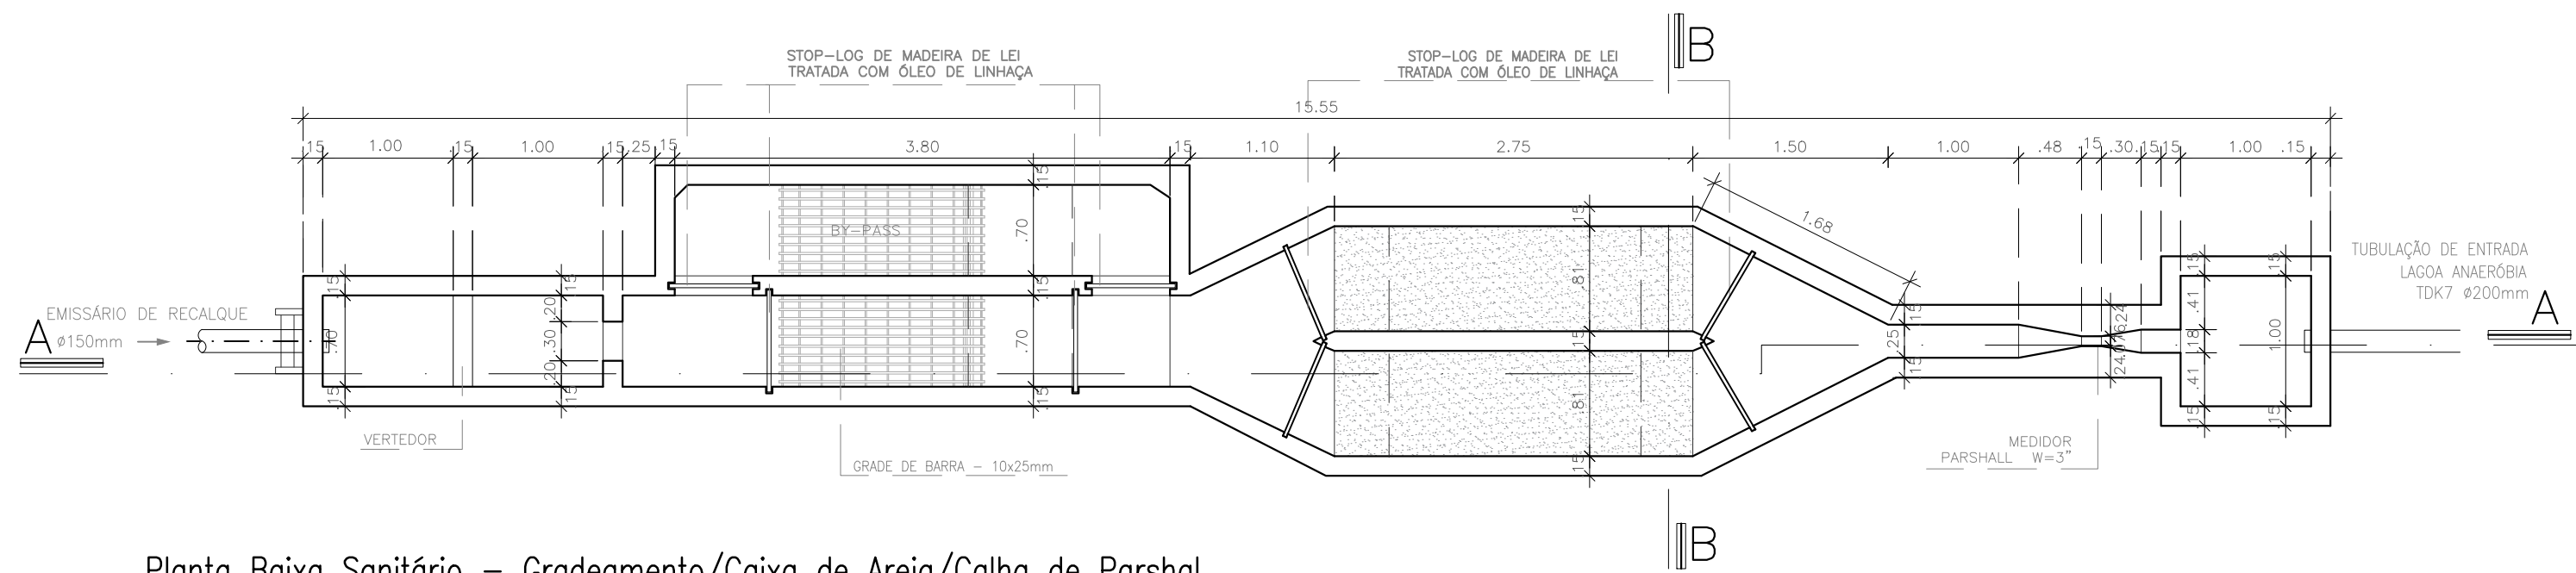


Planta Baixa Sanitário – Gradeamento/Caixa de Areia/Calha de Parshal
escala 1/50

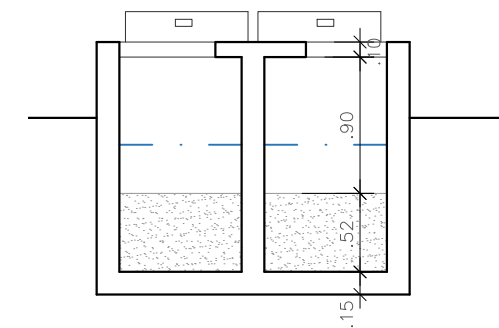


Corte BB – Caixa de Areia
escala 1/50

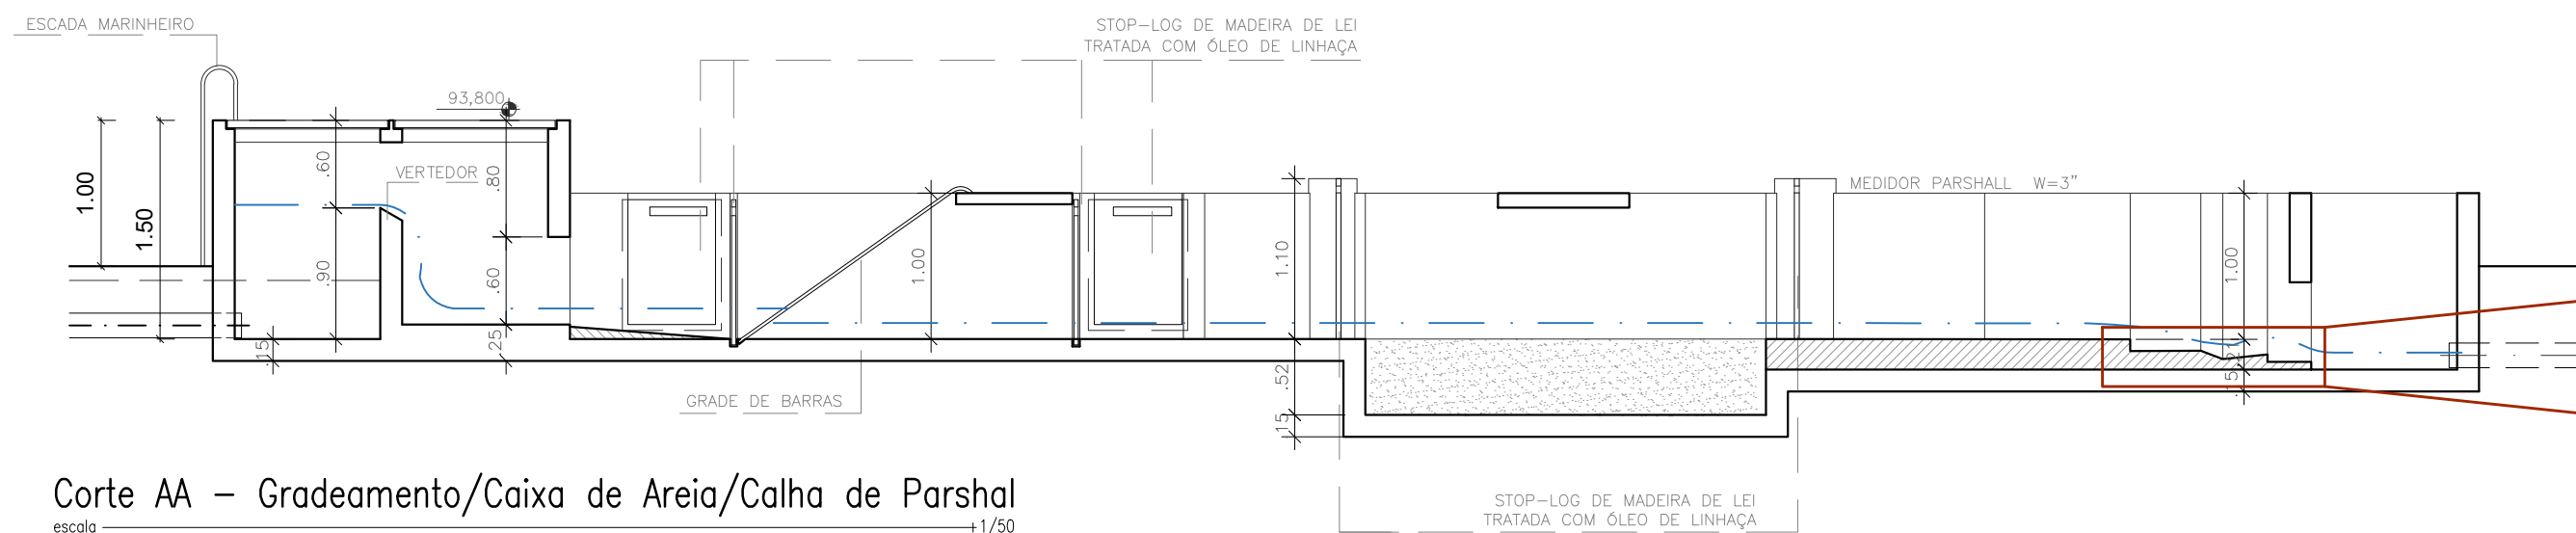


Corte AA – Gradeamento/Caixa de Areia/Calha de Parshal
escala 1/50

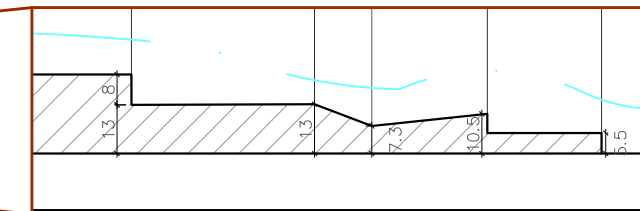


Detalhe – Calha de Parshal
escala 1/20

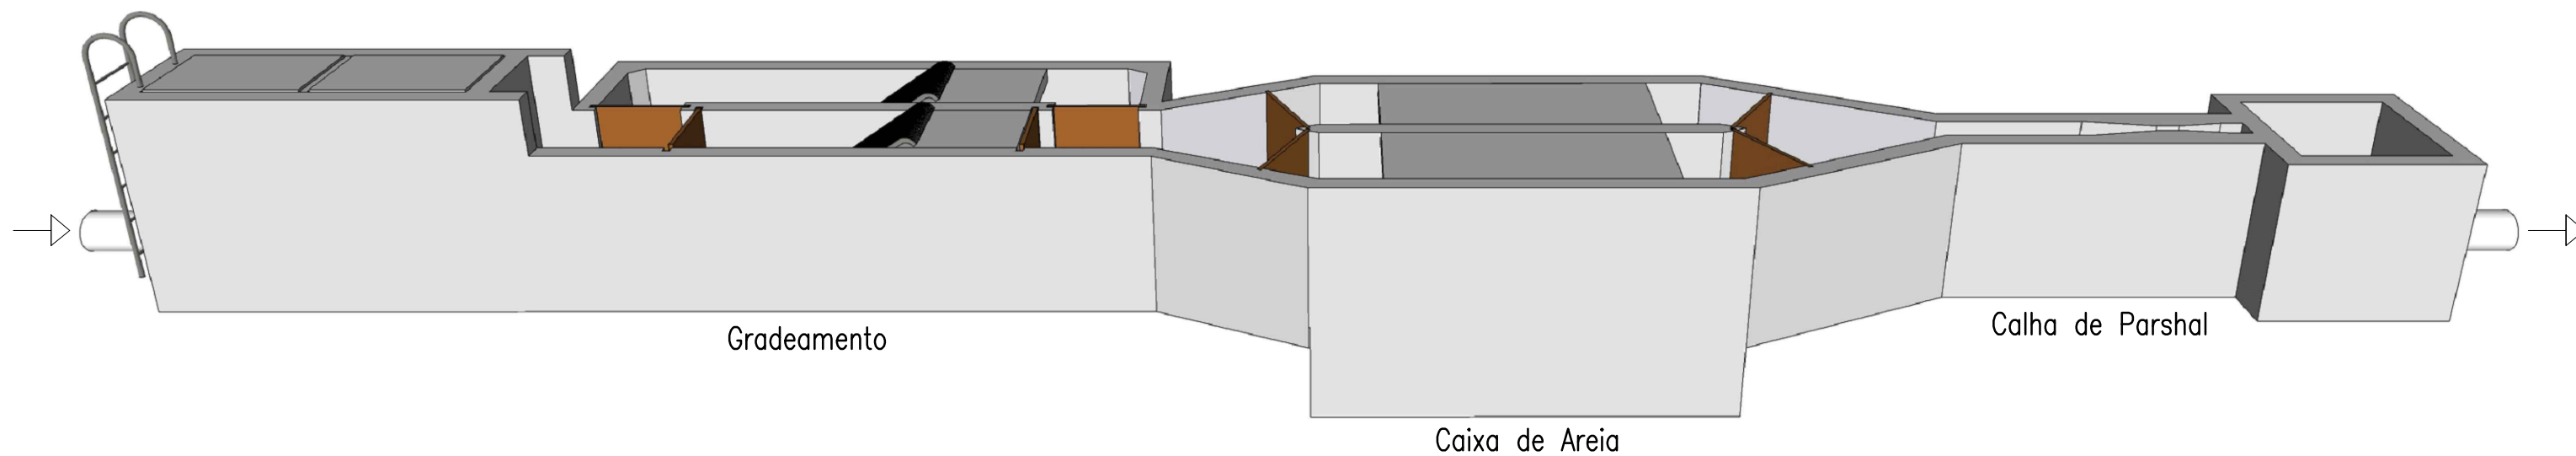


Perspectiva – Gradeamento/Caixa de Areia/Calha de Parshal
escala 1/50

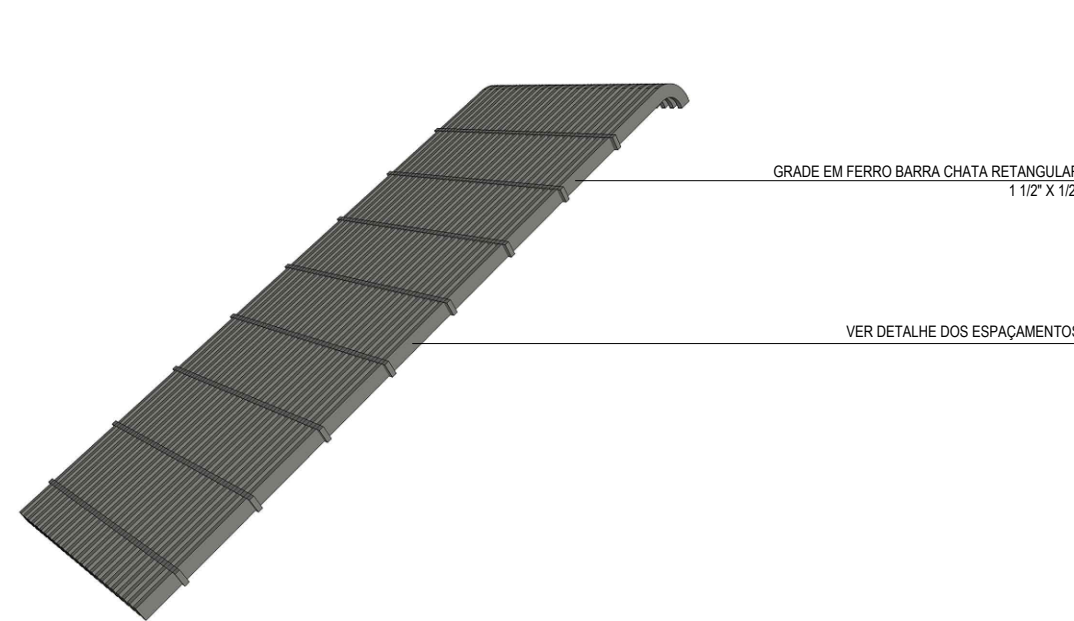

Perspectiva – Gradeamento
escala 1/50

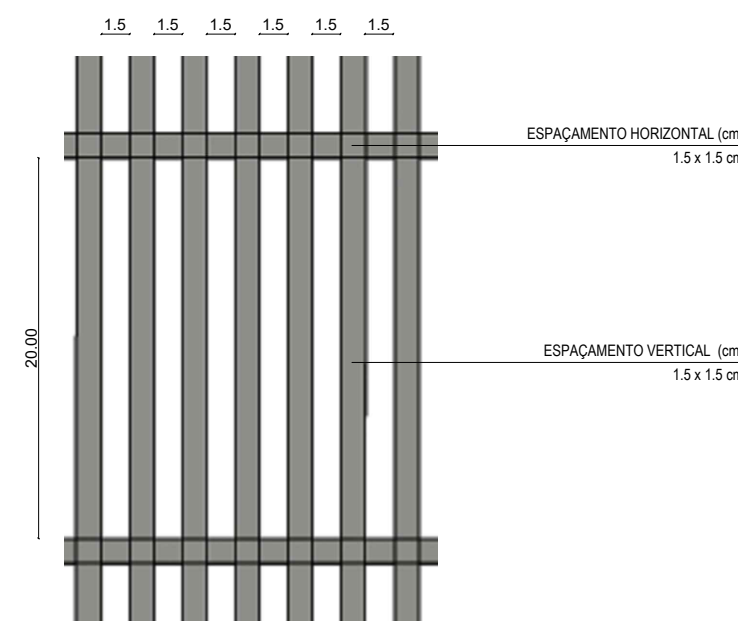

Detalhe – Espaçamento
escala 1/25

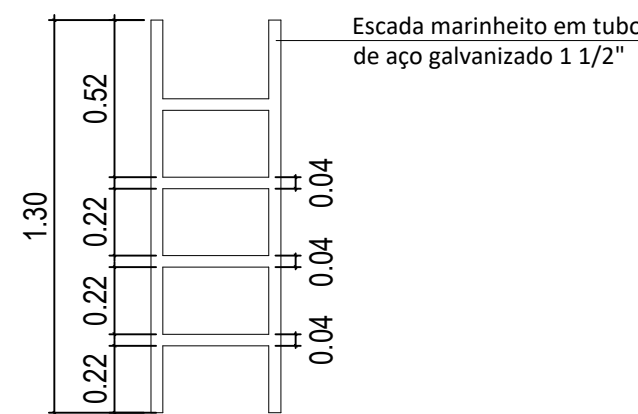

Detalhe – Escada Marinheiro
escala 1/25

Documento assinado digitalmente
gov.br MICHAEL JACKSON MAMEDE SOUZA
Data: 11/03/2024 15:54:45-0300
Verifique em <https://validar.i0.gov.br>

RESPONSÁVEL TÉCNICO:

PROPRIETÁRIO:

PRANCHA		PREFEITURA MUNICIPAL DE COREMAS – PB			
1/1		PROJETO DE CONSTRUÇÃO DE MATADOURO – 9389922022			
		PROJETO SANITÁRIO - GRADEAMENTO/CAIXA DE AREIA/CALHA DE PARSHAL			
DESENHO	DATA	RESPONSÁVEL		RUBRICA	
PROJETO				ÁREA DE TERRENO	ÁREA CONSTRUÍDA
CÓPIA				10.000,00 M²	871,58 M²
ESCALA:	DESENHO:				
1:50	PLANTA BAIXA				
1:50	CORTE AA E BB				
5:ESC	PERSPECTIVAS E DETALHES 3D				