


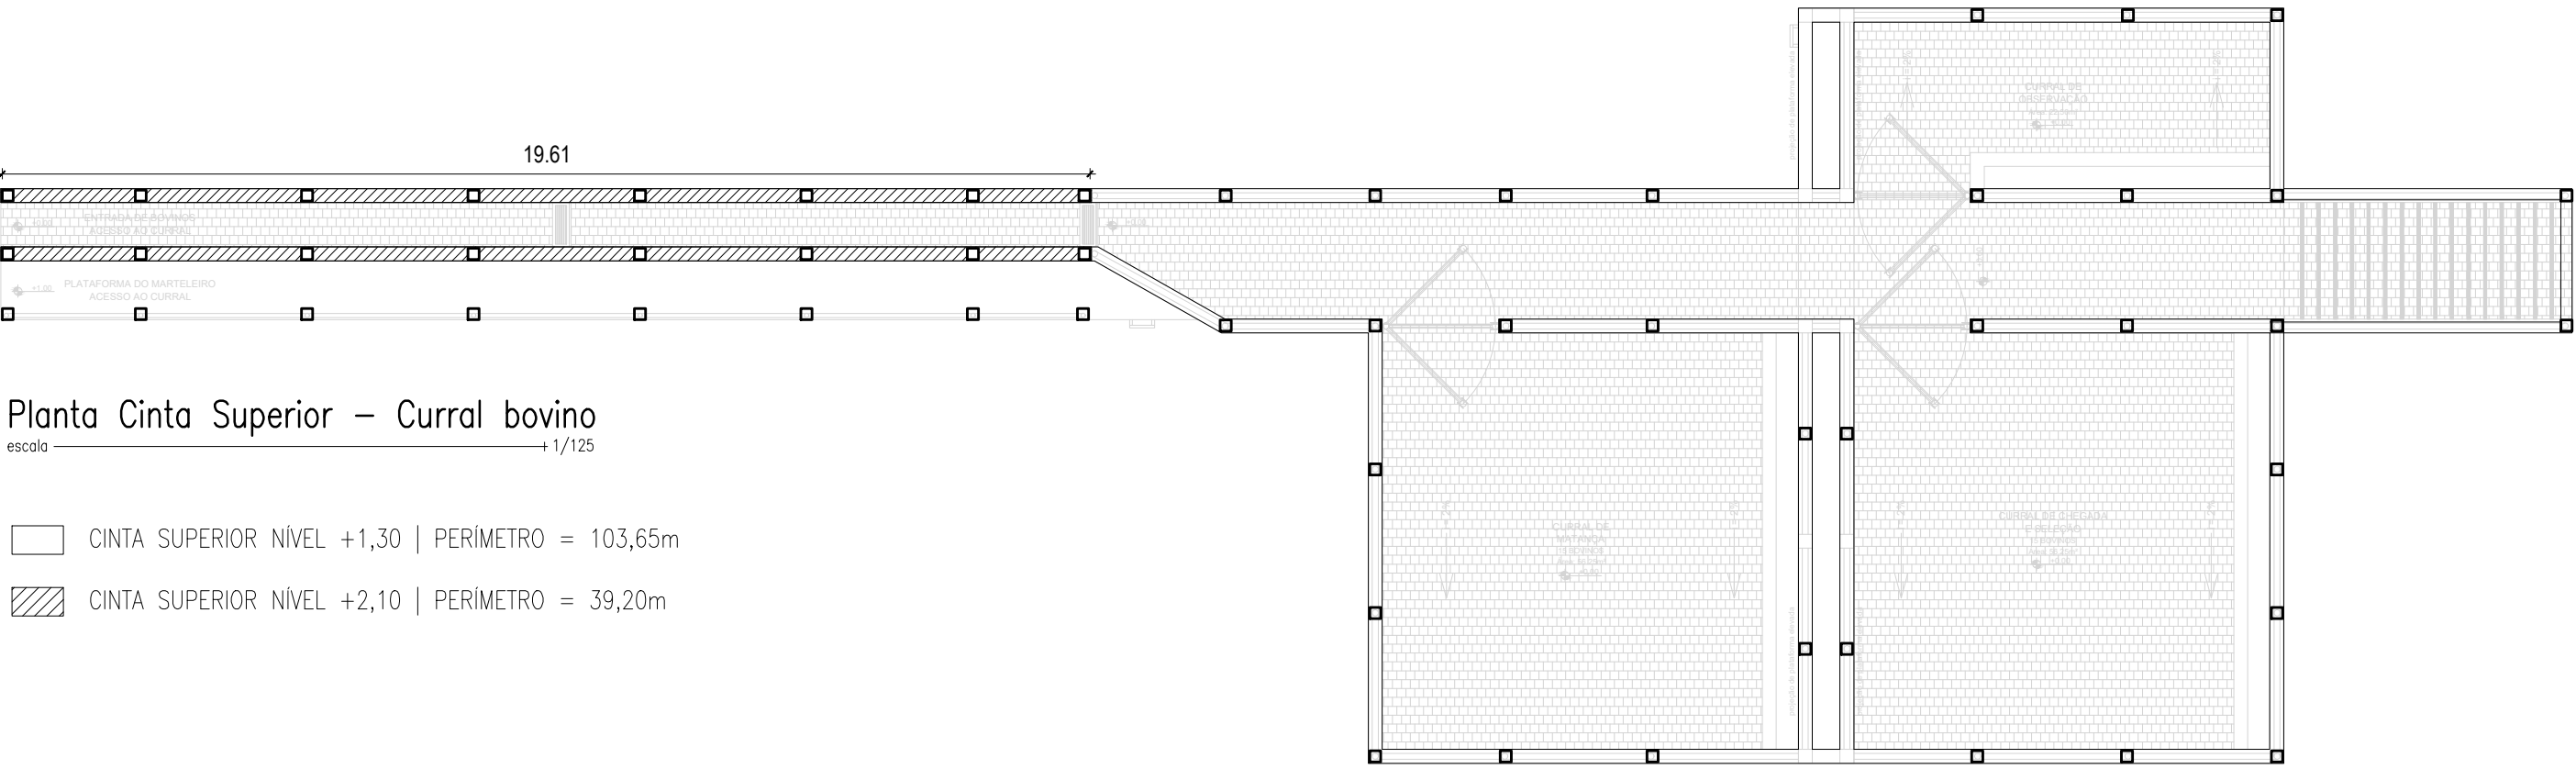

Planta Cinto Superior – Curral bovino


escala 1/125

CINTA SUPERIOR NÍVEL +1,30 | PERÍMETRO = 103,65m

CINTA SUPERIOR NÍVEL +2,10 | PERÍMETRO = 39,20m

CINTA GERAL SUPERIOR - CGS
(PERÍMETRO: 142,85m)

ESC 1:20

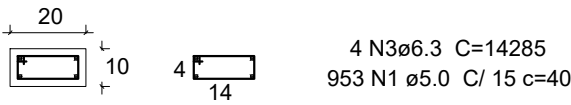


Relação do aço

AÇO	N	DIAM	Q	UNIT (cm)	C.TOTAL (cm)
CA60	1	5.0	953	40	38120
CA50	2	6.3	4	14285	57140

Resumo do aço

AÇO	DIAM	C.TOTAL (m)	PESO + 10 % (kg)
CA50	6.3	571.4	153.9
CA60	5.0	381.2	64.5
PESO TOTAL			
CA50	153.9		
CA60	64.5		

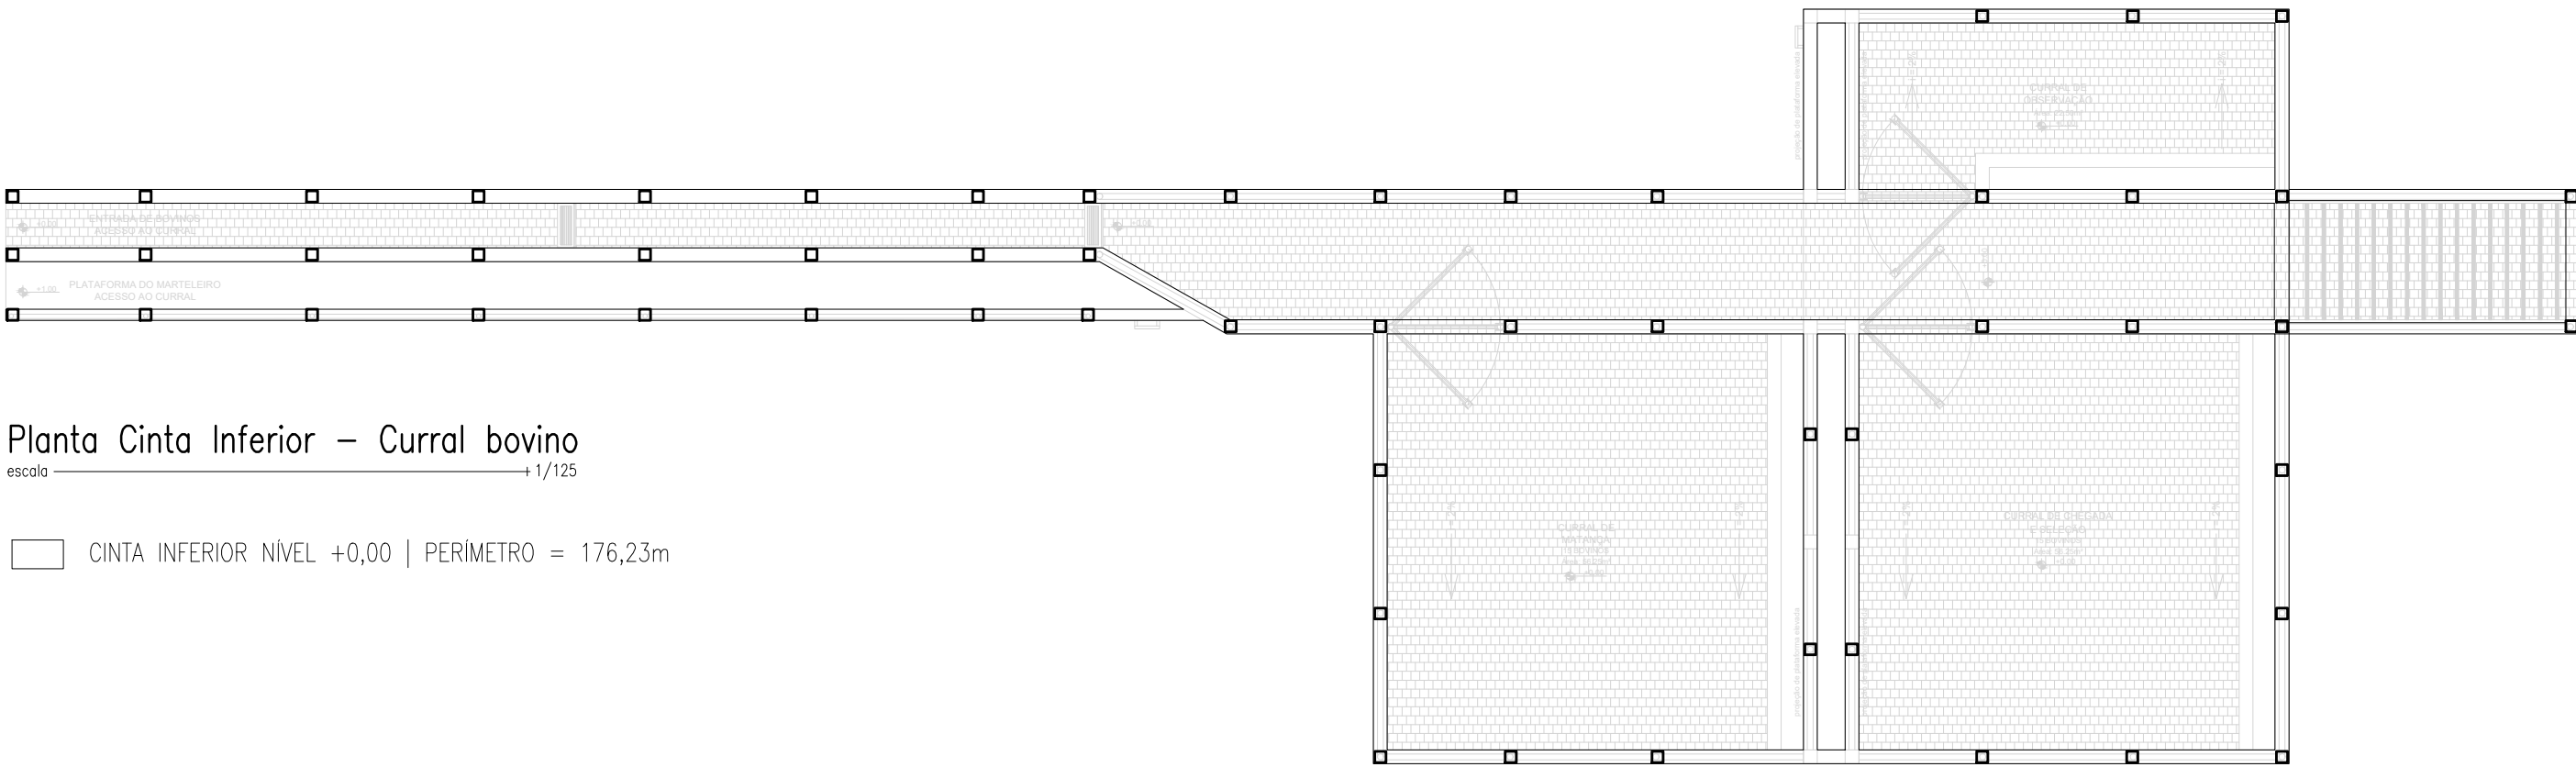


Planta Cinto Inferior – Curral bovino

escala 1/125

CINTA INFERIOR NÍVEL +0,00 | PERÍMETRO = 176,23m

CINTA GERAL INFERIOR - CGI
(PERÍMETRO: 176,23m)

ESC 1:20

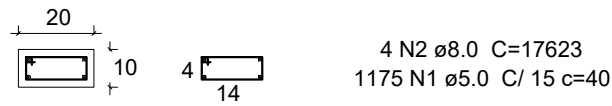


Relação do aço

AÇO	N	DIAM	Q	UNIT (cm)	C.TOTAL (cm)
CA60	1	5.0	1175	40	47000
CA50	2	8.0	4	17623	70492

Resumo do aço

AÇO	DIAM	C.TOTAL (m)	PESO + 10 % (kg)
CA50	8.0	704.9	306.2
CA60	5.0	470.0	79.6
PESO TOTAL			
CA50	306.2		
CA60	79.6		

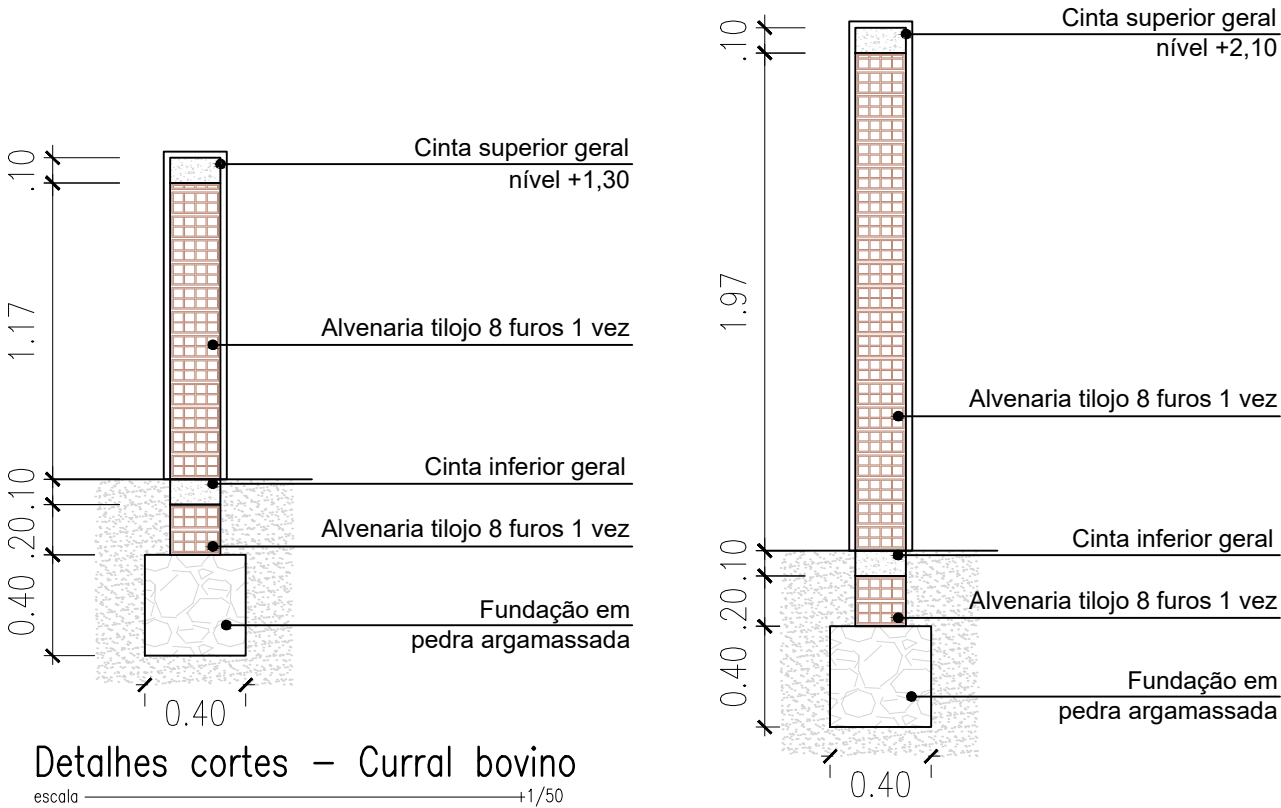

Detalhes cortes – Curral bovino

escala 1/50

RESPONSÁVEL TÉCNICO:

PROPRIETÁRIO:

PRANCHA 6/6	PREFEITURA MUNICIPAL DE COREMAS – PB				
	PROJETO DE CONSTRUÇÃO DE MATADOURO – 9389922022				
	PROJETO ESTRUTURAL - CINTAS E PILARES CURRAL BOVINO				
	DATA	RESPONSÁVEL		RUBRICA	
DESENHO					
PROJETO				ÁREA DO TERRENO	ÁREA ÚTIL
CÓPIA				10.000,00 M²	971,43 M²
ESCALA:		DESENHO:		ÁREA CONSTRUIDA	871,58 M²
1:125 1:125 1:50		PLANTA CINTA INFERIOR - CURRAL BOVINO PLANTA CINTA SUPERIOR - CURRAL BOVINO DETALHES CORTES			