



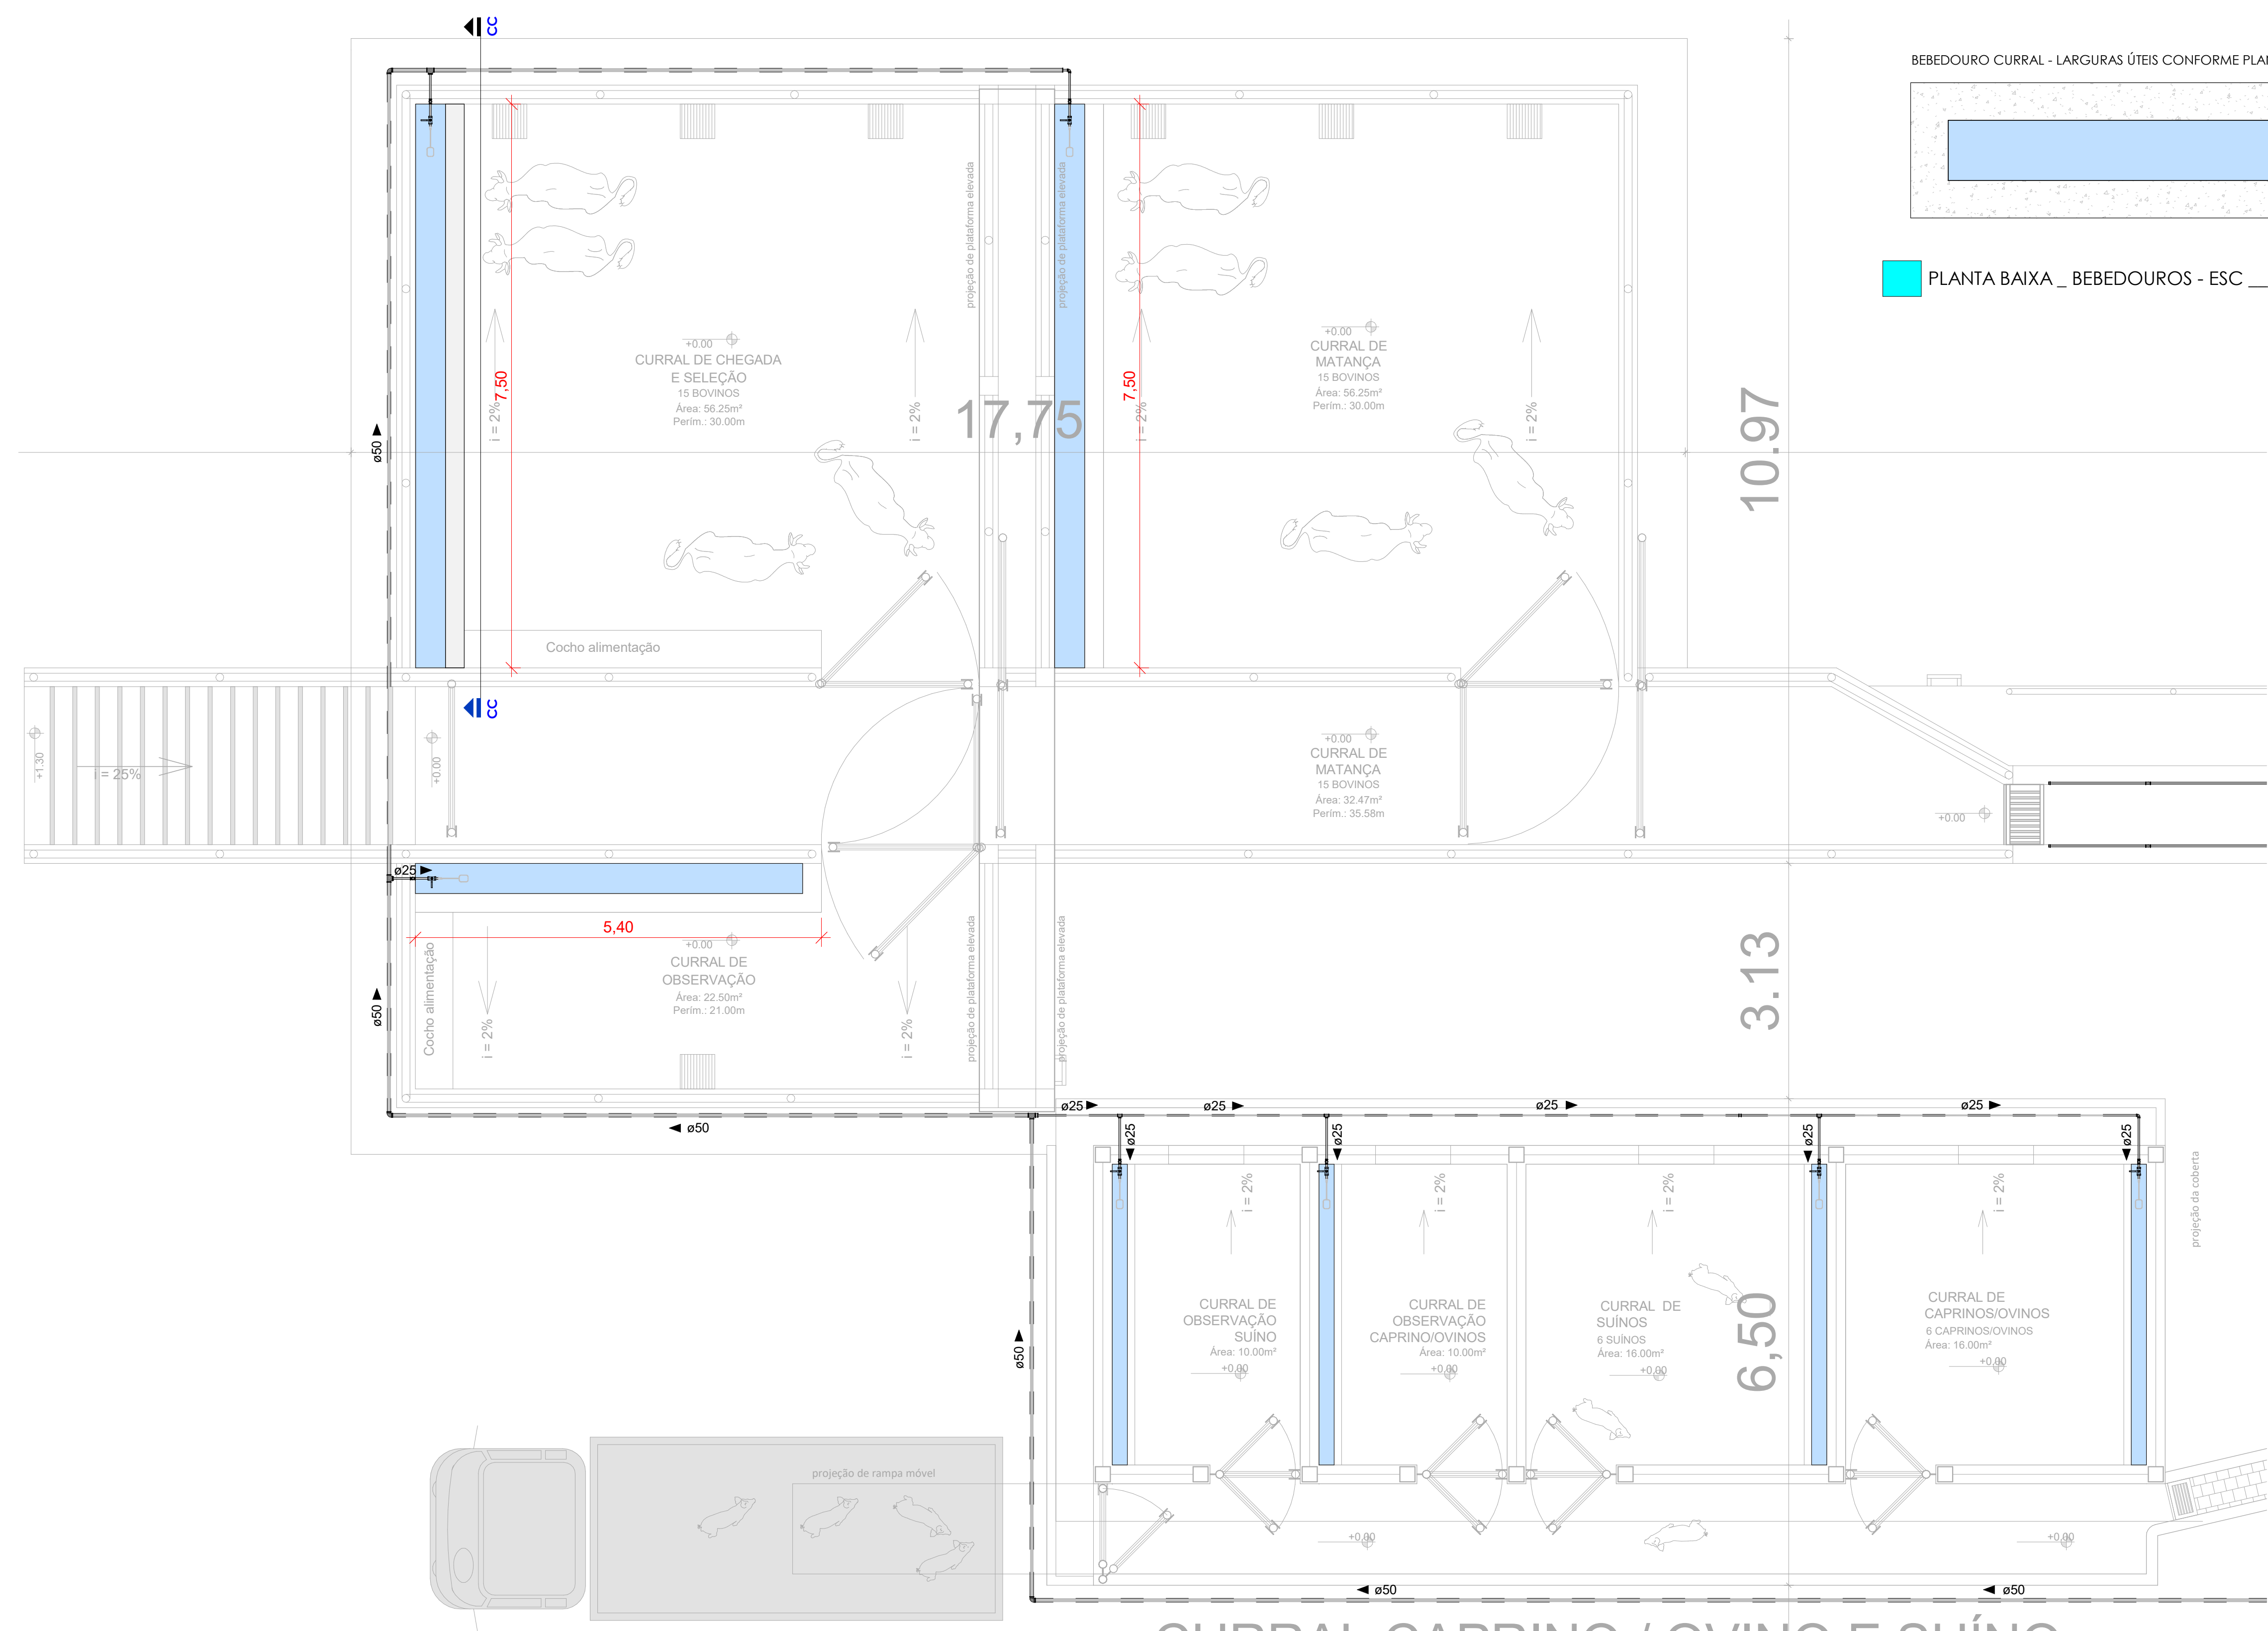

PLANTA BAIXA _ CURRAL_BOVINOS - ESC 1/50


- LEGENDA:**
- TUBULAÇÃO PVC BRANCO - ESGOTO
 - TUBULAÇÃO PVC BRANCO SN - VENTILAÇÃO ESGOTO
 - TUBULAÇÃO AÇO GALVANIZADO - ÁGUA FRIA
 - TUBULAÇÃO AÇO GALVANIZADO - ÁGUA FRIA (PELO PISO)
 - TUBULAÇÃO PVC MARROM - ÁGUA FRIA
 - TUBULAÇÃO PVC MARROM - ÁGUA FRIA (PELO PISO)

- AL-nn
Øxx -ALIMENTAÇÃO DO RESERV. SUPERIOR
nn: número da coluna
xx: diâmetro nominal da coluna
- CV-nn
Øxx -COLUNA DE VENTILAÇÃO
nn: número da coluna
xx: diâmetro nominal da coluna
- AF-nn
Øxx -COLUNA DE ÁGUA FRIA (BARRILETE)
nn: número da coluna
xx: diâmetro nominal da coluna

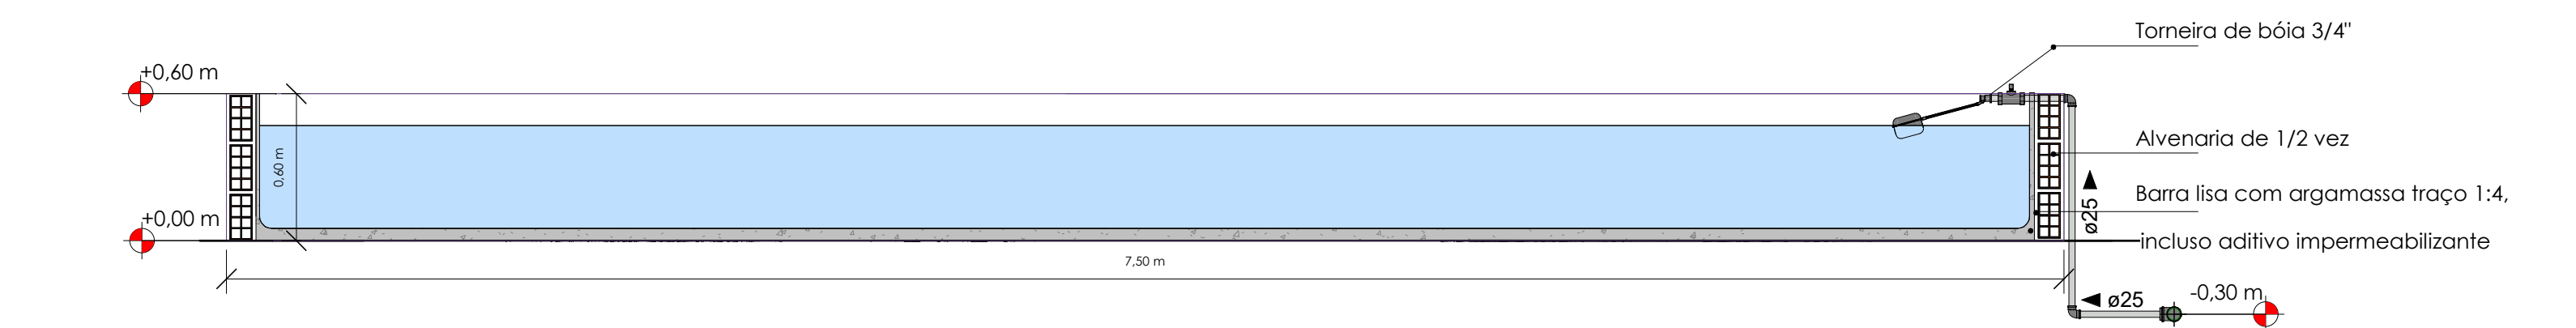


CORTE CC ESC 1/25

BEBEDOURO CURRAL - LARGURAS ÚTEIS CONFORME PLANTA BAIXA

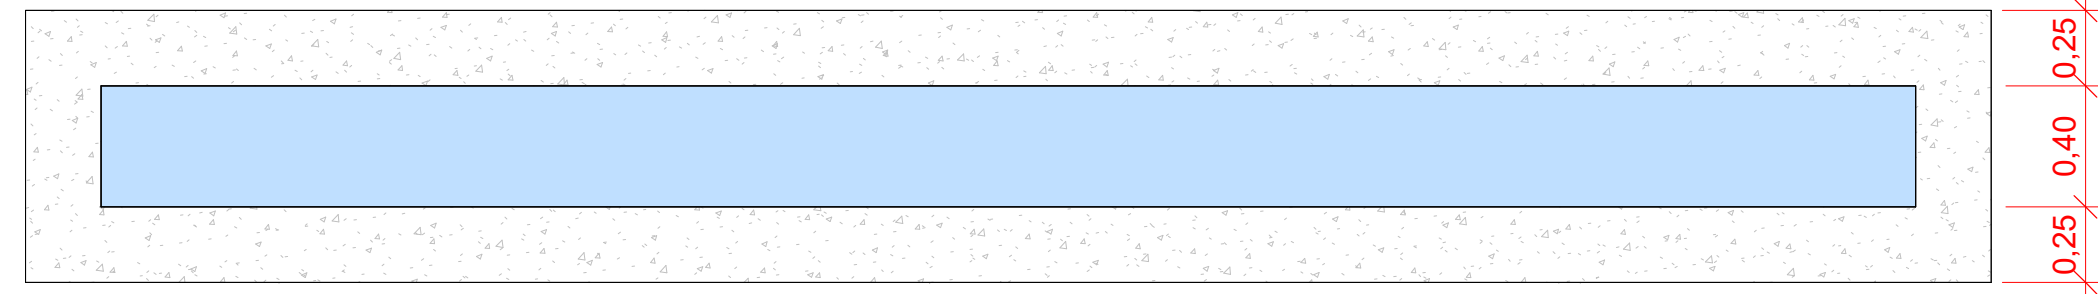

PLANTA BAIXA _ BEBEDOUROS - ESC 1/25

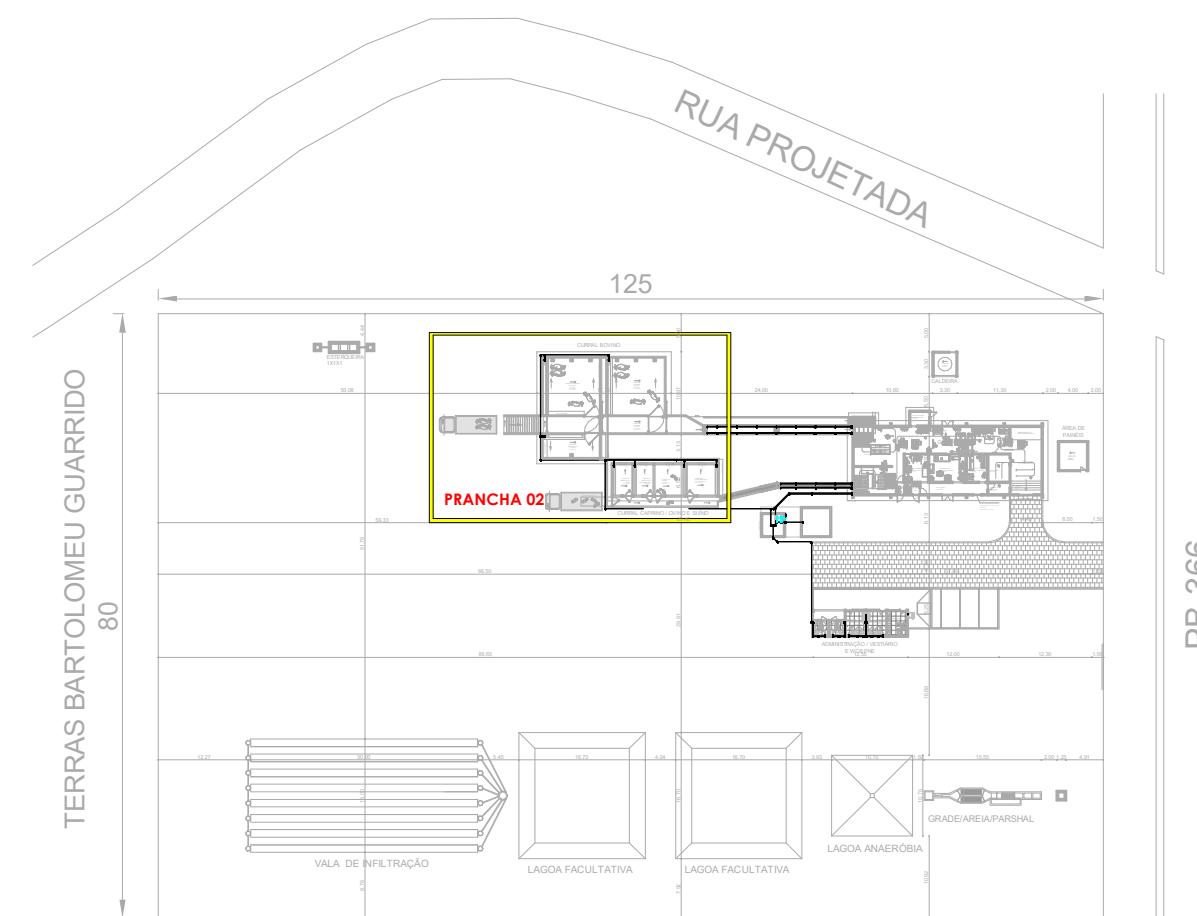

PLANTA BAIXA _ MATADOURO_COREMAS - ESC 1/1000

PROPRIETÁRIO: PREFEITURA MUNICIPAL DE COREMAS - PB			
PROJETO: LINCOLN CARTAXO DE LIRA JÚNIOR		CREA 160.814.689-8	
PROJETO:		INSTALAÇÕES HIDRÁULICAS, MATADOURO DE COREMAS	
CONCEDENTE:		PREFEITURA MUNICIPAL DE COREMAS - PB	
CONVENIENTE:		MUNICÍPIO DE COREMAS - PB	
LOCAL:		COREMAS - PB	
RESPONSÁVEL TÉCNICO		RUBRICA	DADOS
DATA	14/05/2025	LINCOLN CARTAXO	CREA 160.814.689-8
CÓPIA			
VISTO			
PRANCHA:		DESCRIÇÃO:	ESCALA:
02		PLANTA BAIXA CURRAL, BOVINOS, GERAL E BEBEDOUROS	INDICADA
/ 04		CORTE CC	



Av. Gov. Flavio R. Coutinho, 500, sl. 601
Jd. Oceania, 58037-005 - João Pessoa (PB)
Tel +55 99924.4447
e-mail: contato@lclprojetos.com