



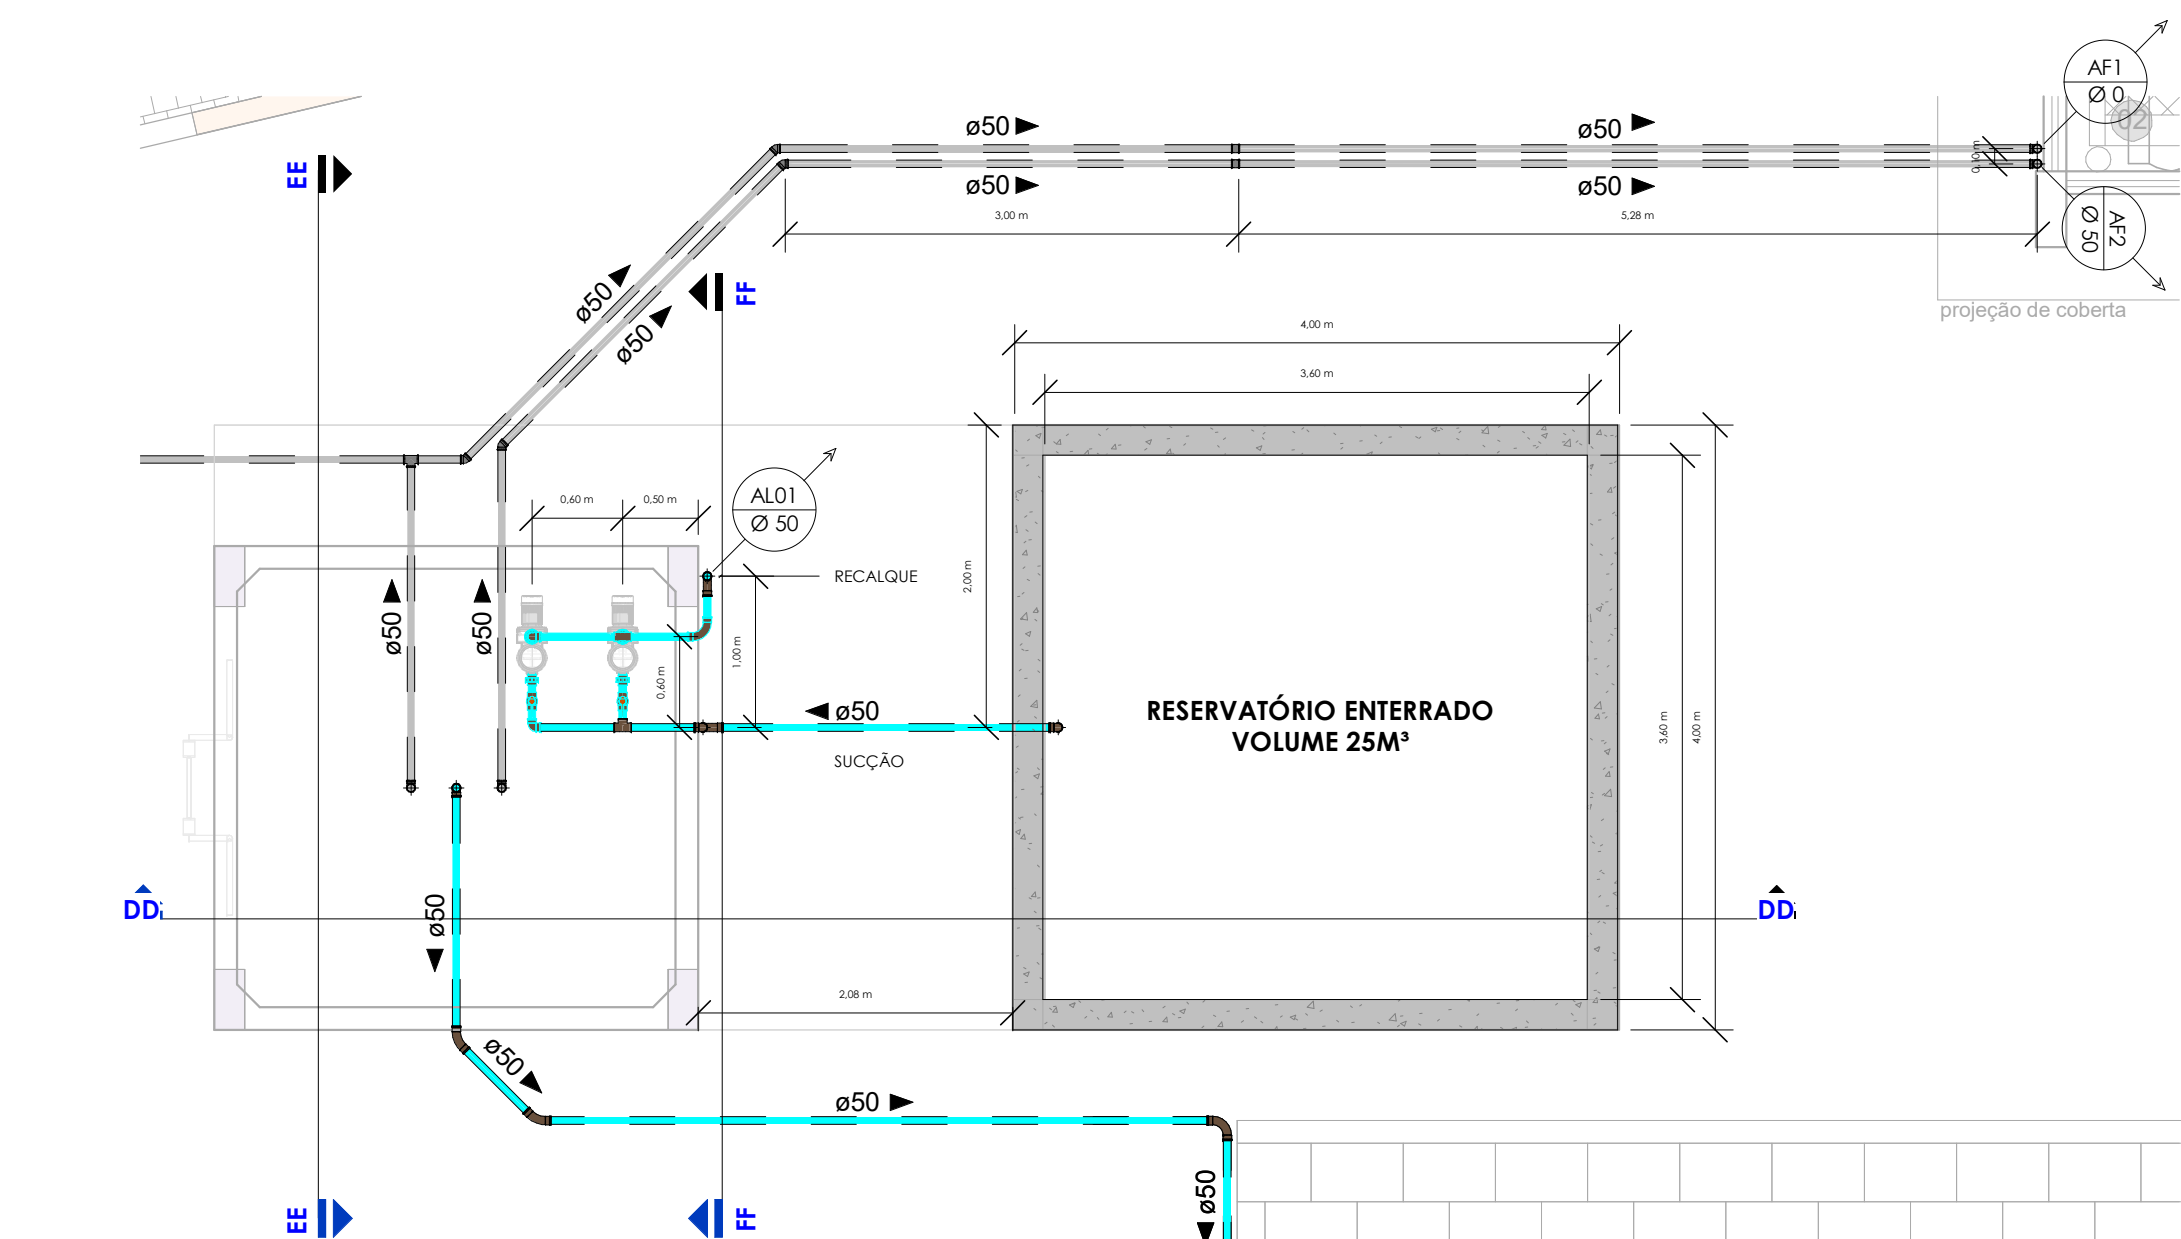


LEGENDA:

- TUBULAÇÃO PVC BRANCO - ESGOTO
- TUBULAÇÃO PVC BRANCO SN - VENTILAÇÃO ESGOTO
- TUBULAÇÃO AÇO GALVANIZADO - ÁGUA FRIA
- TUBULAÇÃO AÇO GALVANIZADO - ÁGUA FRIA (PELO PISO)
- TUBULAÇÃO PVC MARROM - ÁGUA FRIA
- TUBULAÇÃO PVC MARROM - ÁGUA FRIA (PELO PISO)
- ALIMENTAÇÃO DO RESERV. SUPERIOR
AL-nn
nn: número da coluna
xx: diâmetro nominal da coluna
- COLUNA DE VENTILAÇÃO
CV-nn
nn: número da coluna
xx: diâmetro nominal da coluna
- COLUNA DE ÁGUA FRIA (BARRILETE)
AF-nn
nn: número da coluna
xx: diâmetro nominal da coluna

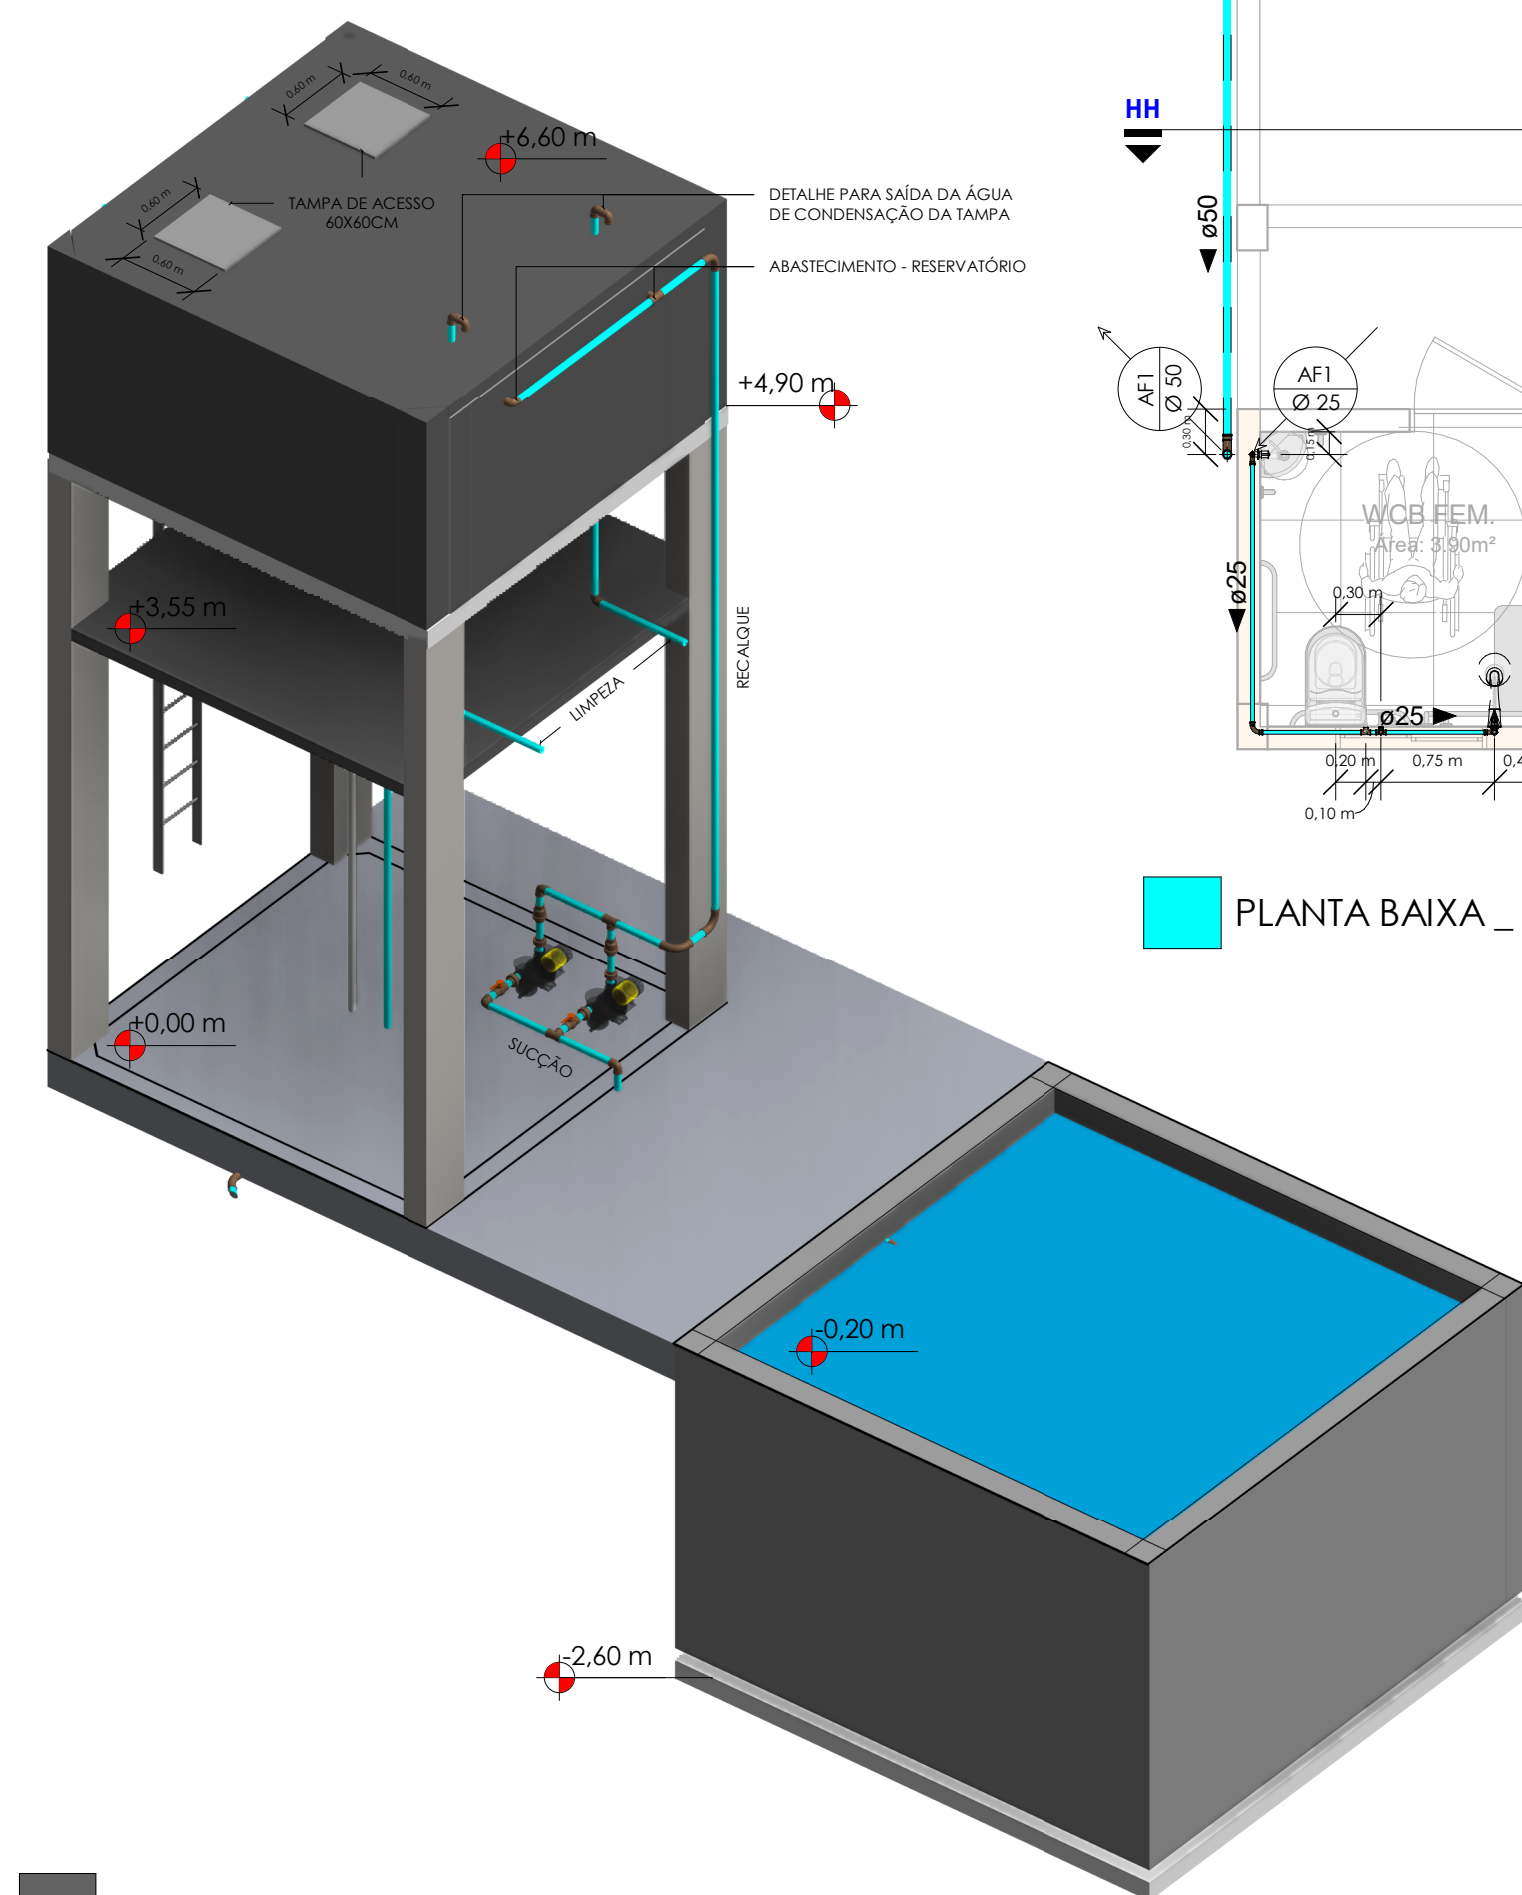

ISOMÉTRICA 01 - CAIXA D'ÁGUA E TANQUE - ESC

1/50

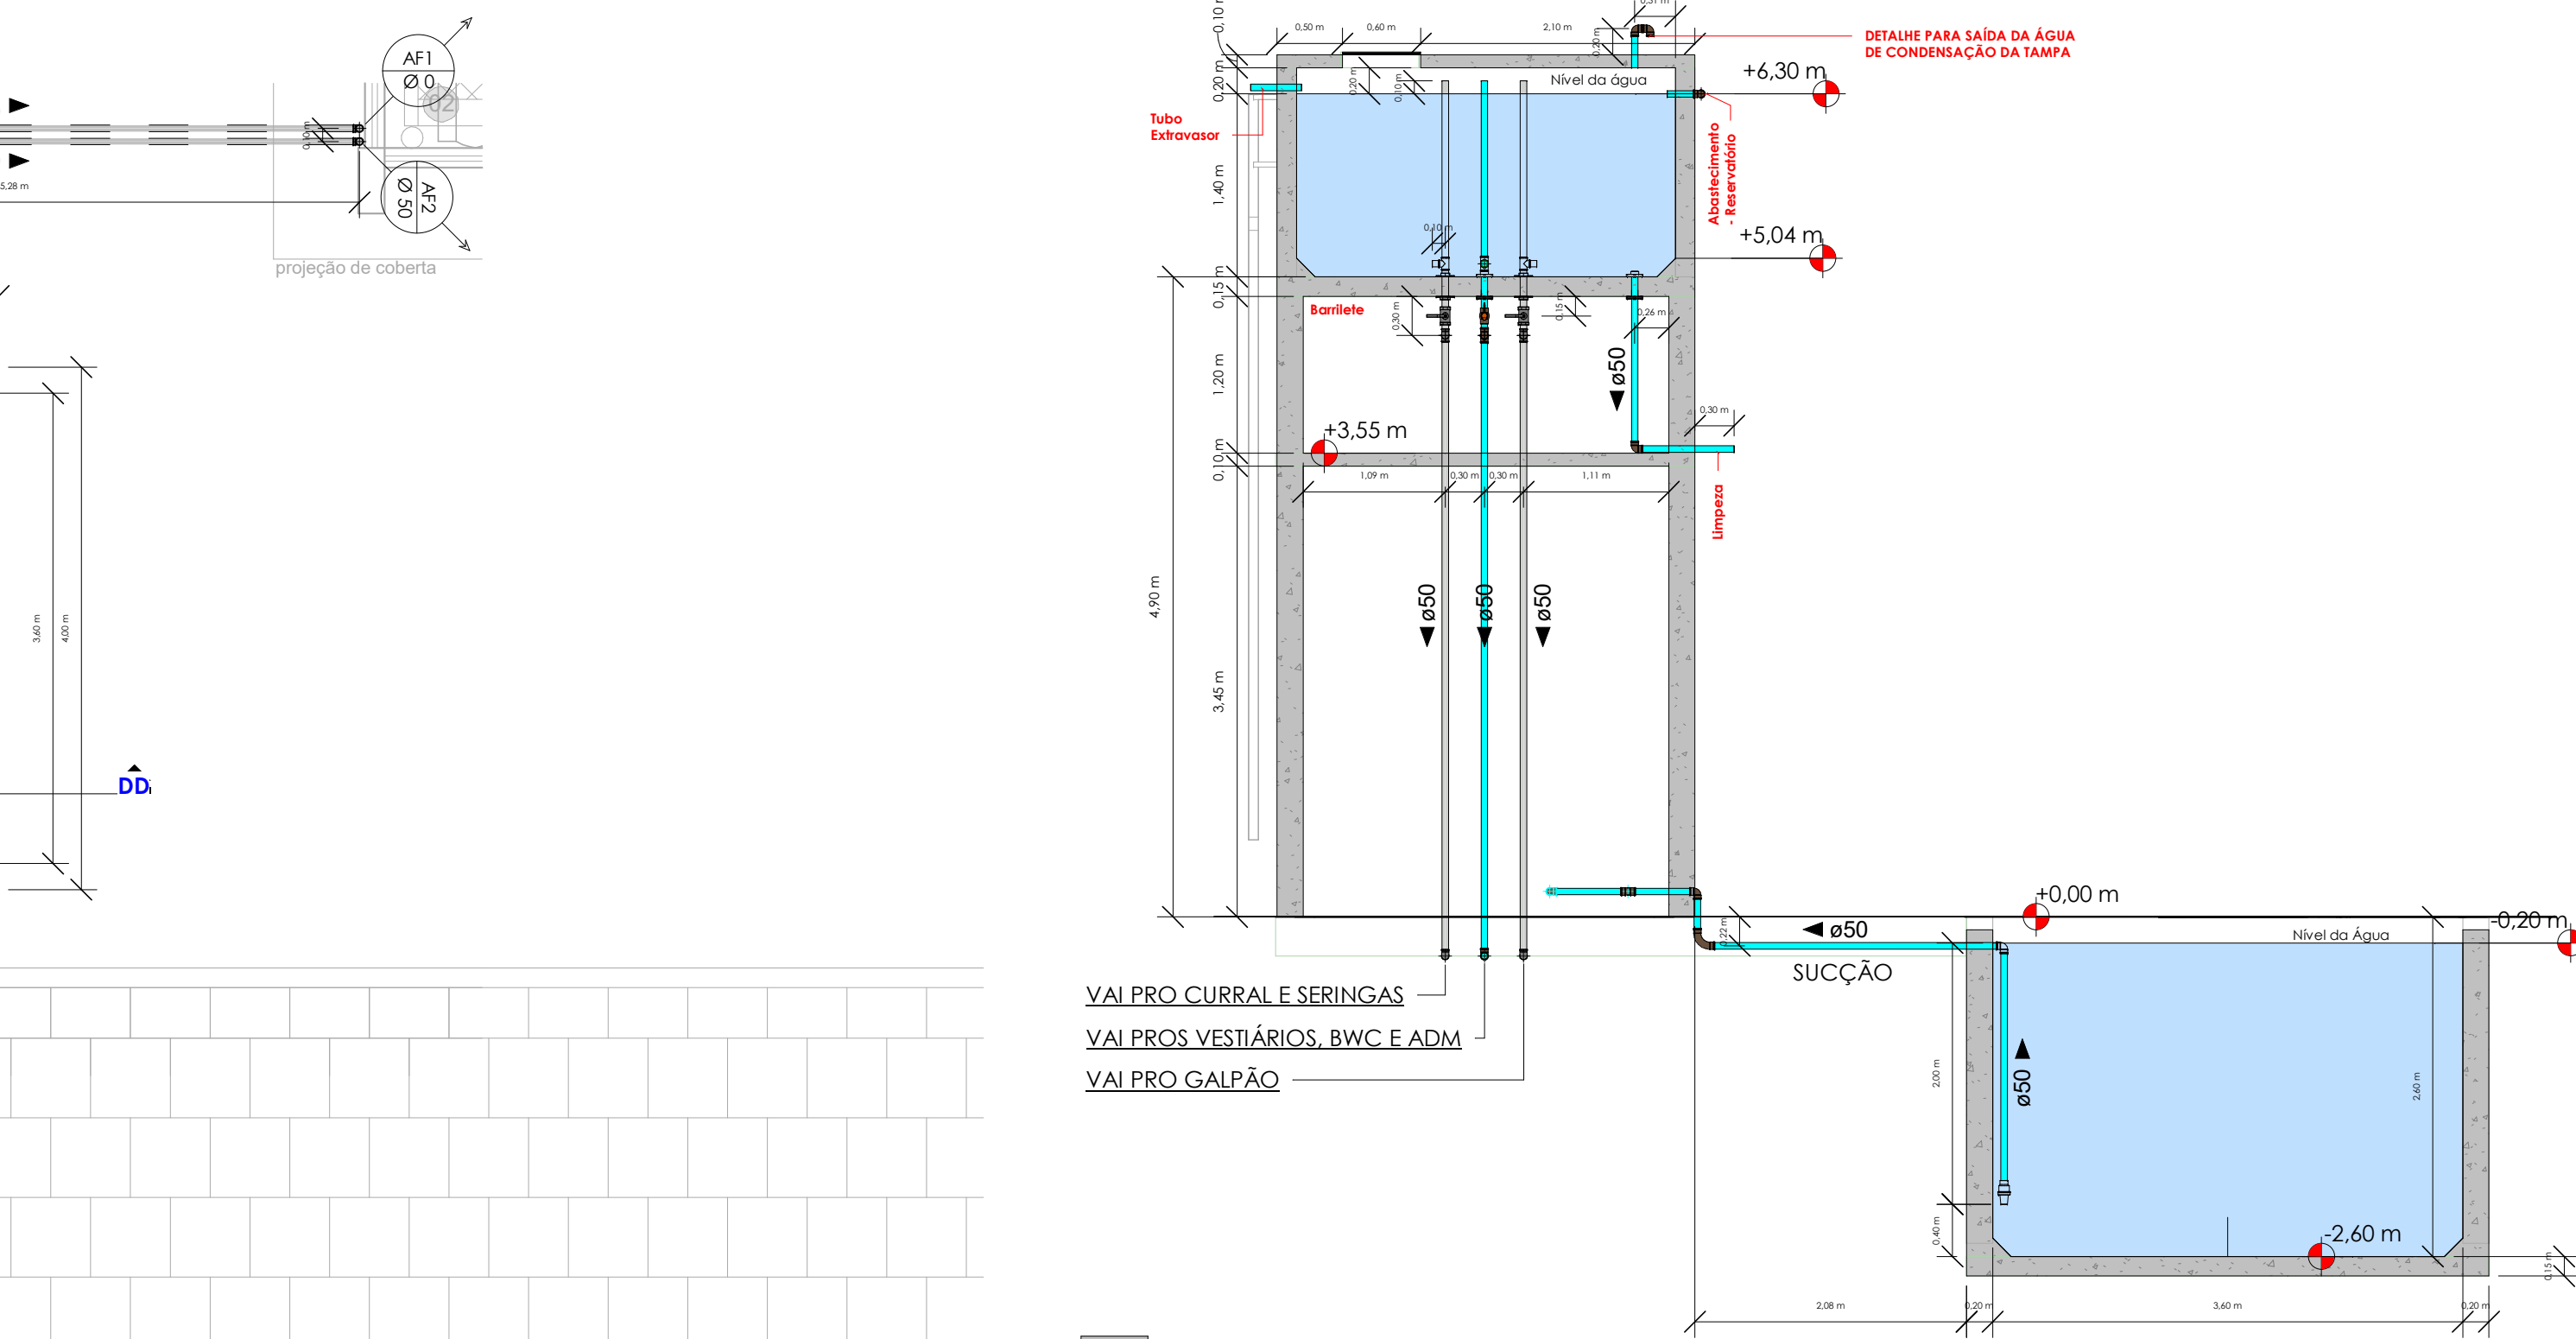


CORTE DD

ESC 1/50


PLANTA BAIXA _CAIXA_D'ÁGUA - ESC

1/25

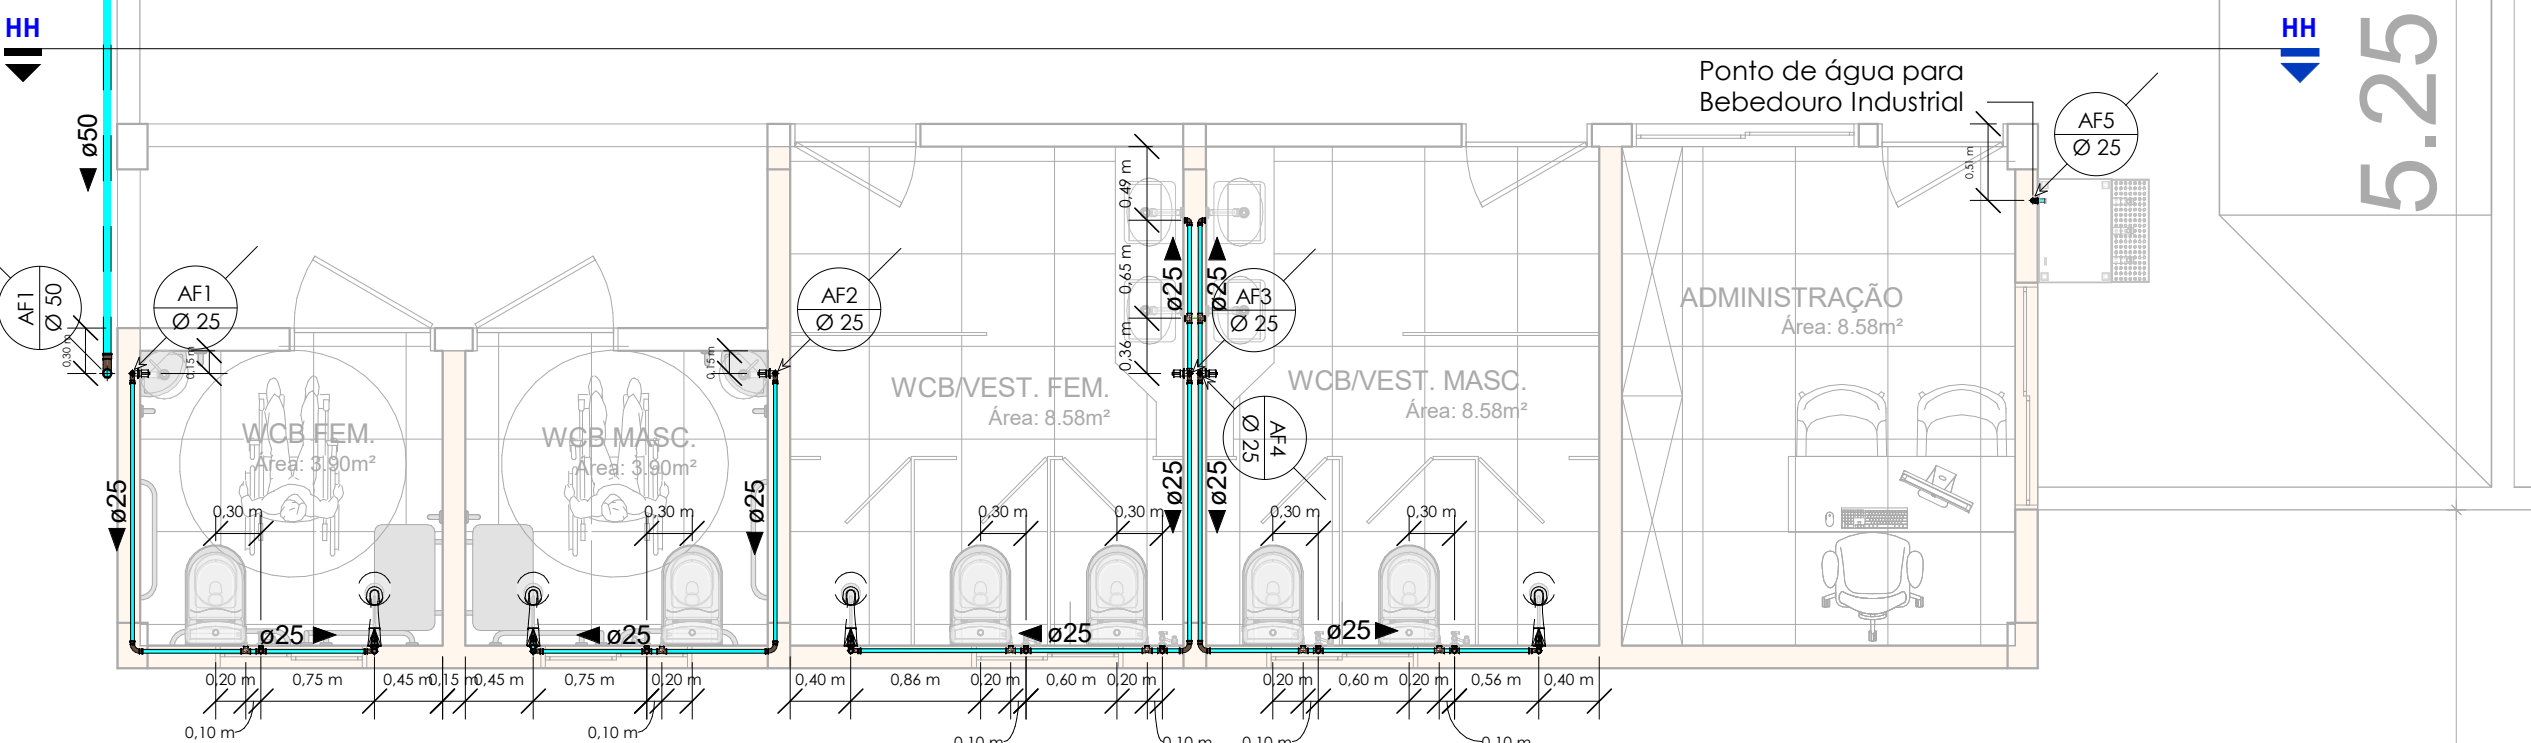


PLANTA BAIXA _BWC'S_VESTIÁRIOS_ADM - ESC

1/20

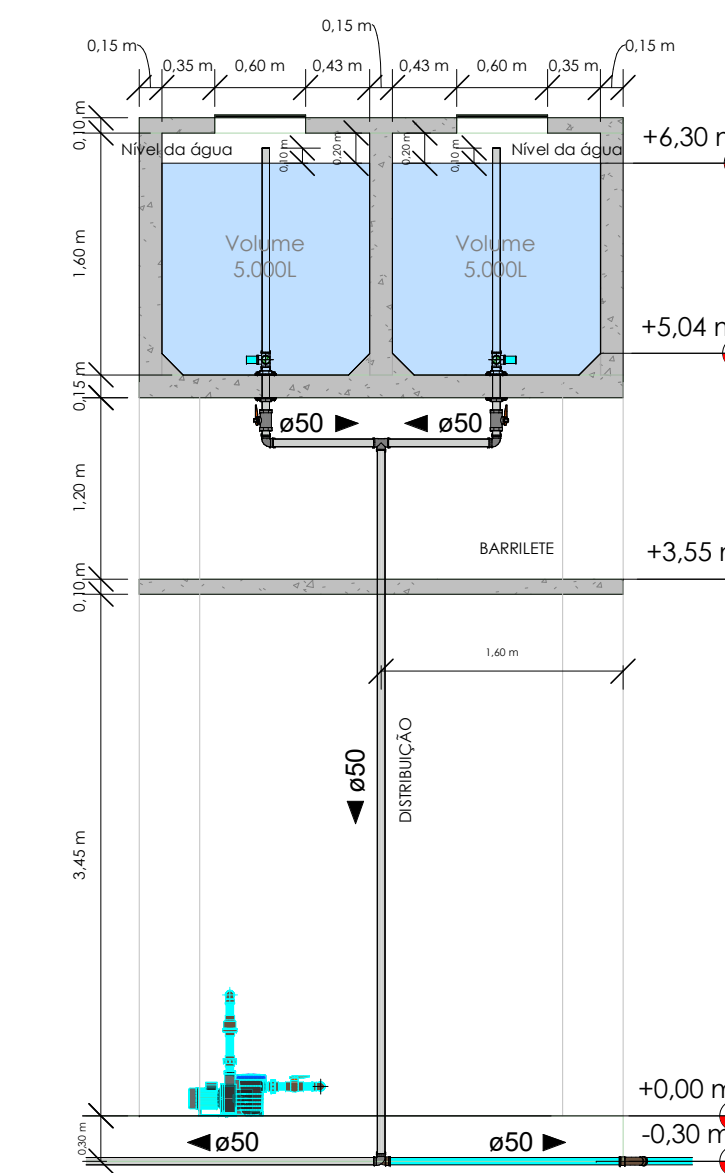


CORTE EE

ESC 1/50

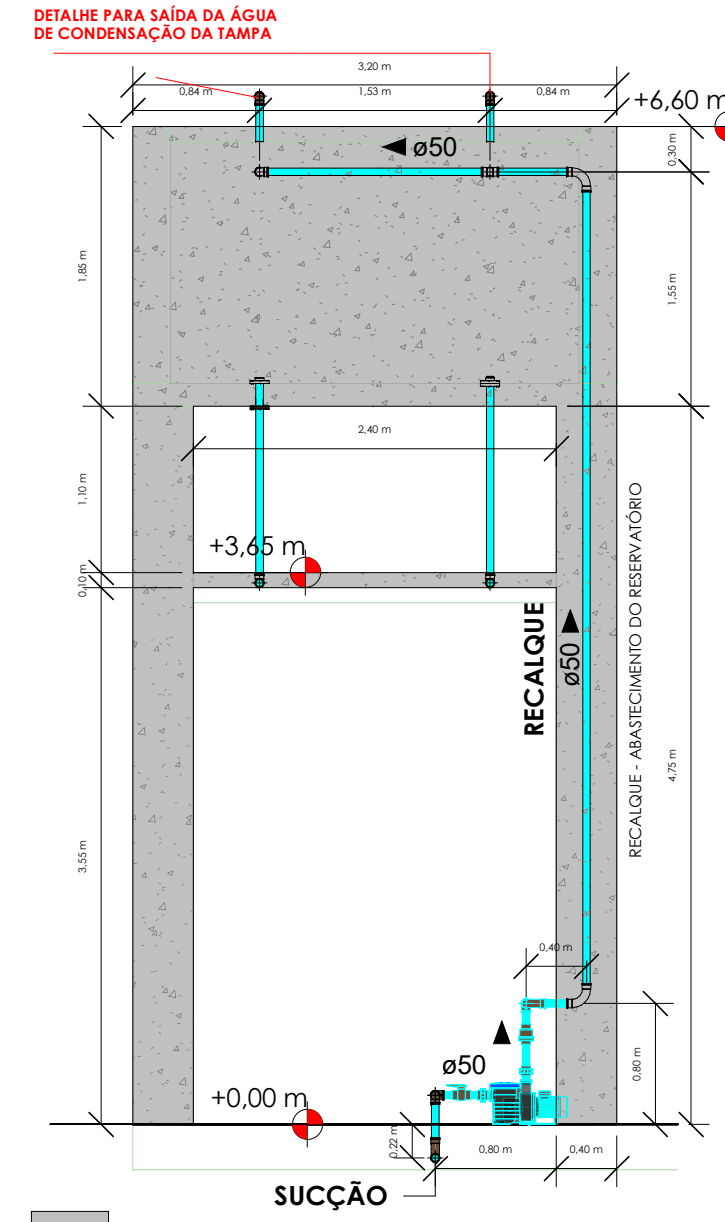

CORTE FF

ESC 1/50

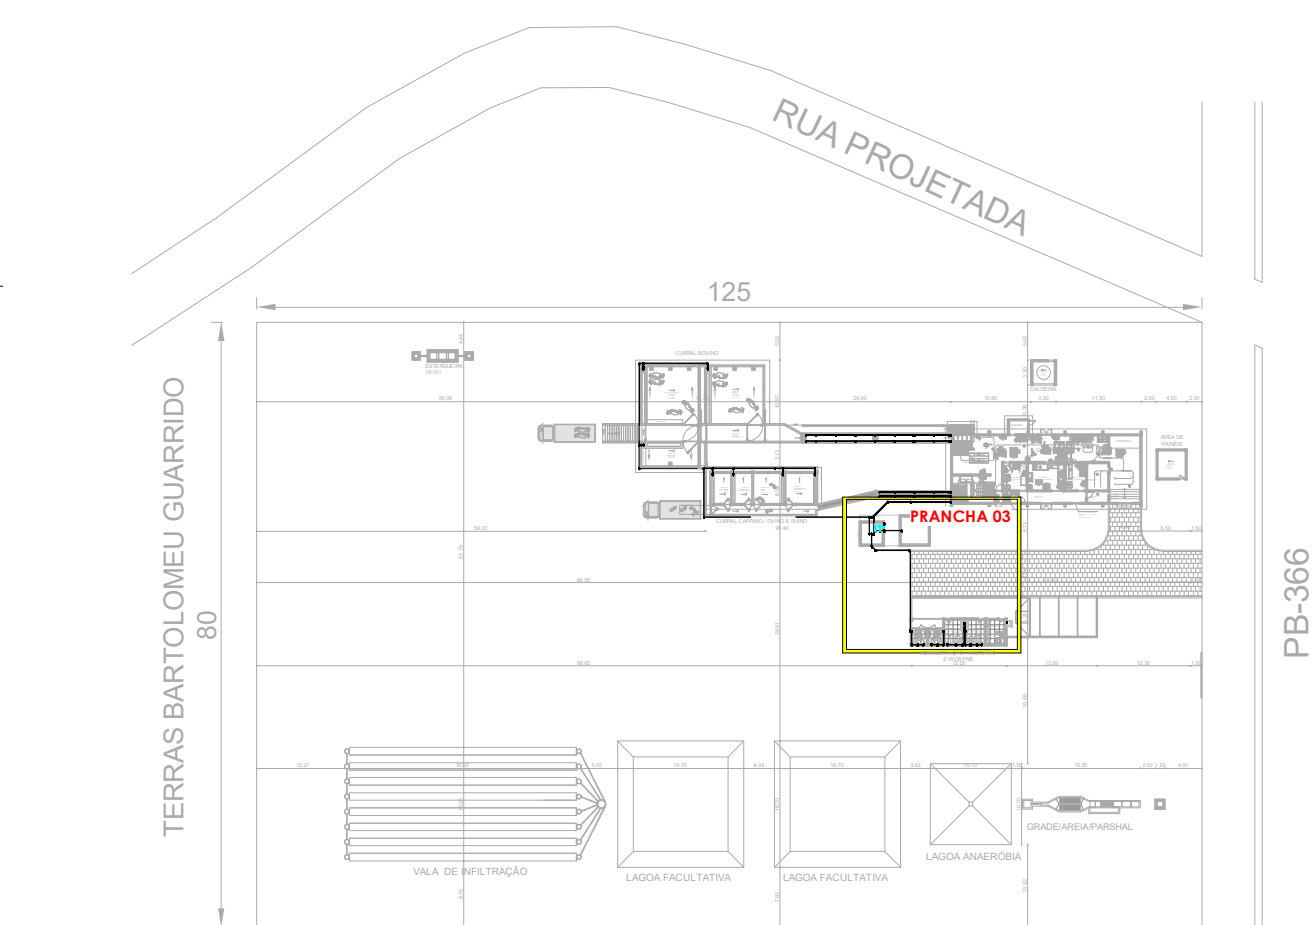

PLANTA BAIXA _MATADOURO_COREMAS - ESC

1/1000

PROPRIETÁRIO: PREFEITURA MUNICIPAL DE COREMAS - PB

PROJETO: LINCOLN CARTAXO DE LIRA JÚNIOR CREA 160.814.689-8

PROJETO: INSTALAÇÕES HIDRÁULICAS, MATADOURO DE COREMAS

CONCEDENTE: PREFEITURA MUNICIPAL DE COREMAS - PB

CONVENIENTE: MUNICÍPIO DE COREMAS - PB

LOCAL: COREMAS - PB

DATA: 14/05/2025

CÓPIA

VISTO

PRANCHA:

03

/ 04

DESCRIÇÃO:

PLANTA BAIXA CAIXA D'ÁGUA, BWC, VESTIÁRIOS E RESERVATÓRIO ENTERRADO

CORTES E ISOMÉTRICA

ESCALA:

INDICADA



Av. Gov. Flavio R. Coutinho, 500, sl. 601
Jd. Oceania, 58037-005 - João Pessoa (PB)
Tel +55 99924.4447
e-mail: contato@lclprojetos.com