



CORTE BB

ESC 1/25

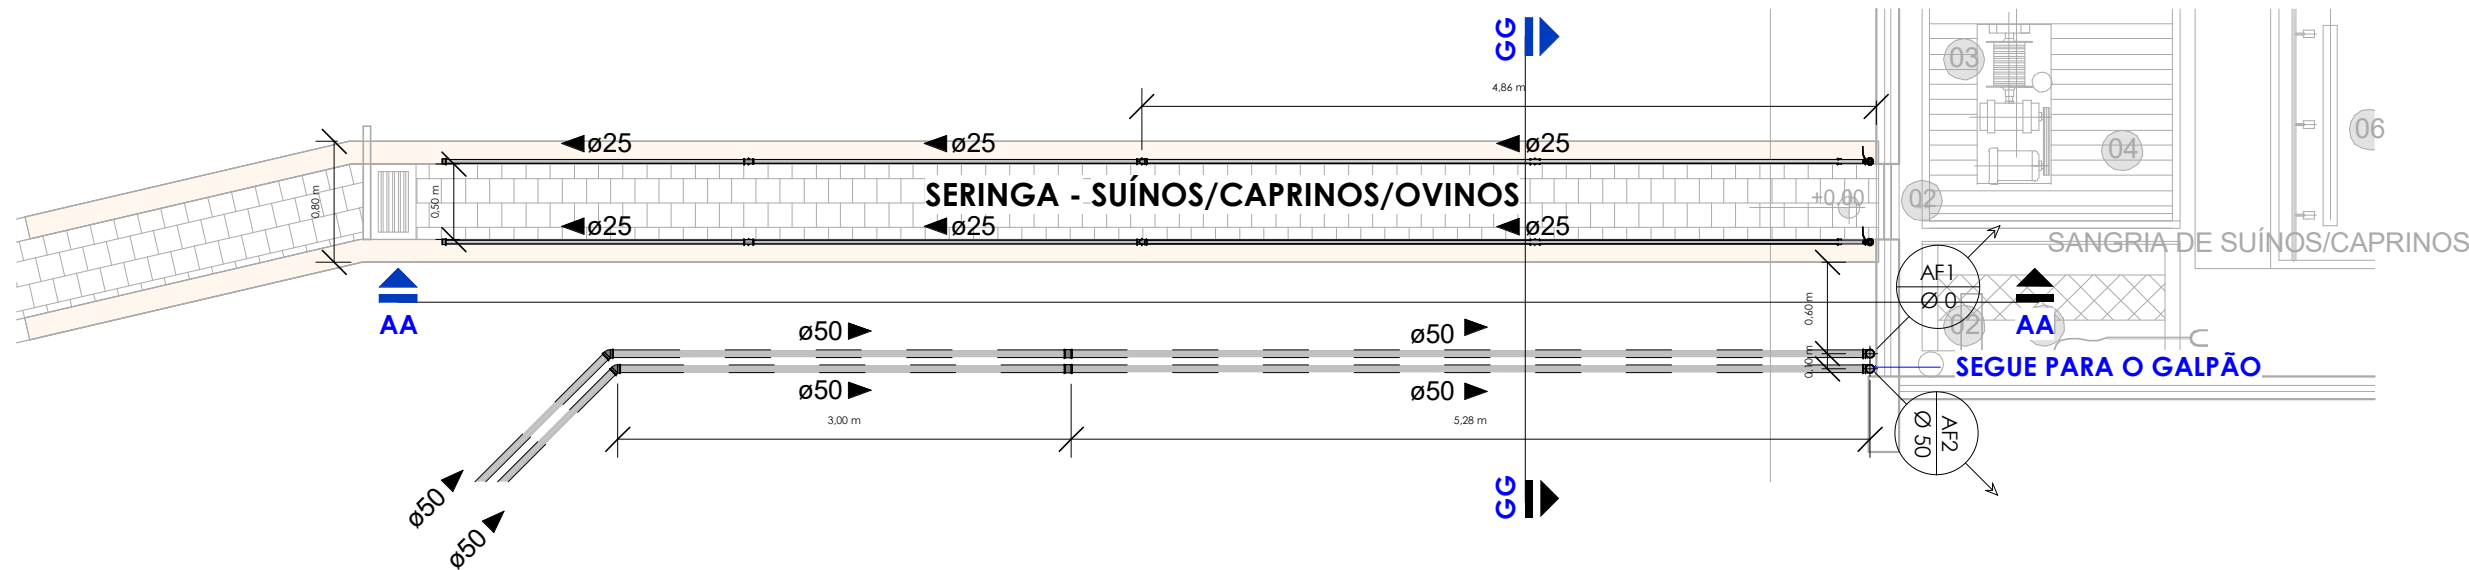


PLANTA BAIXA _ SERINGA - SUÍNOS/CAPRINOS/OVINOS - ESC

1/50

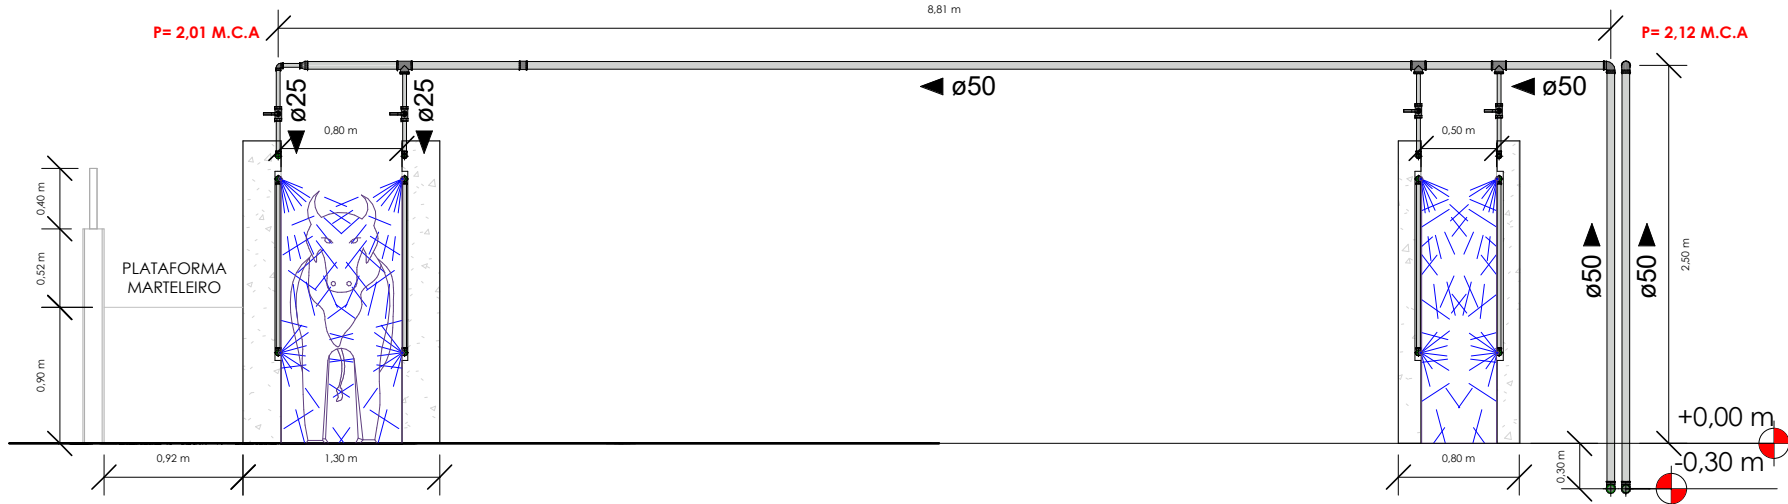


CORTE GG

ESC 1/50

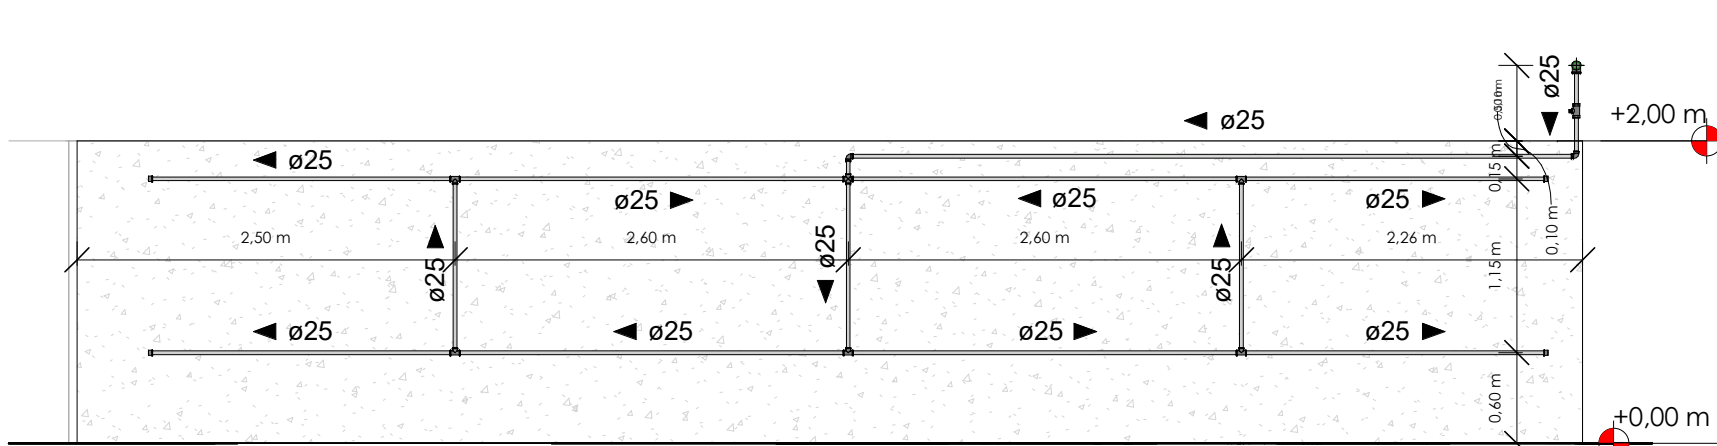

CORTE AA

ESC 1/25

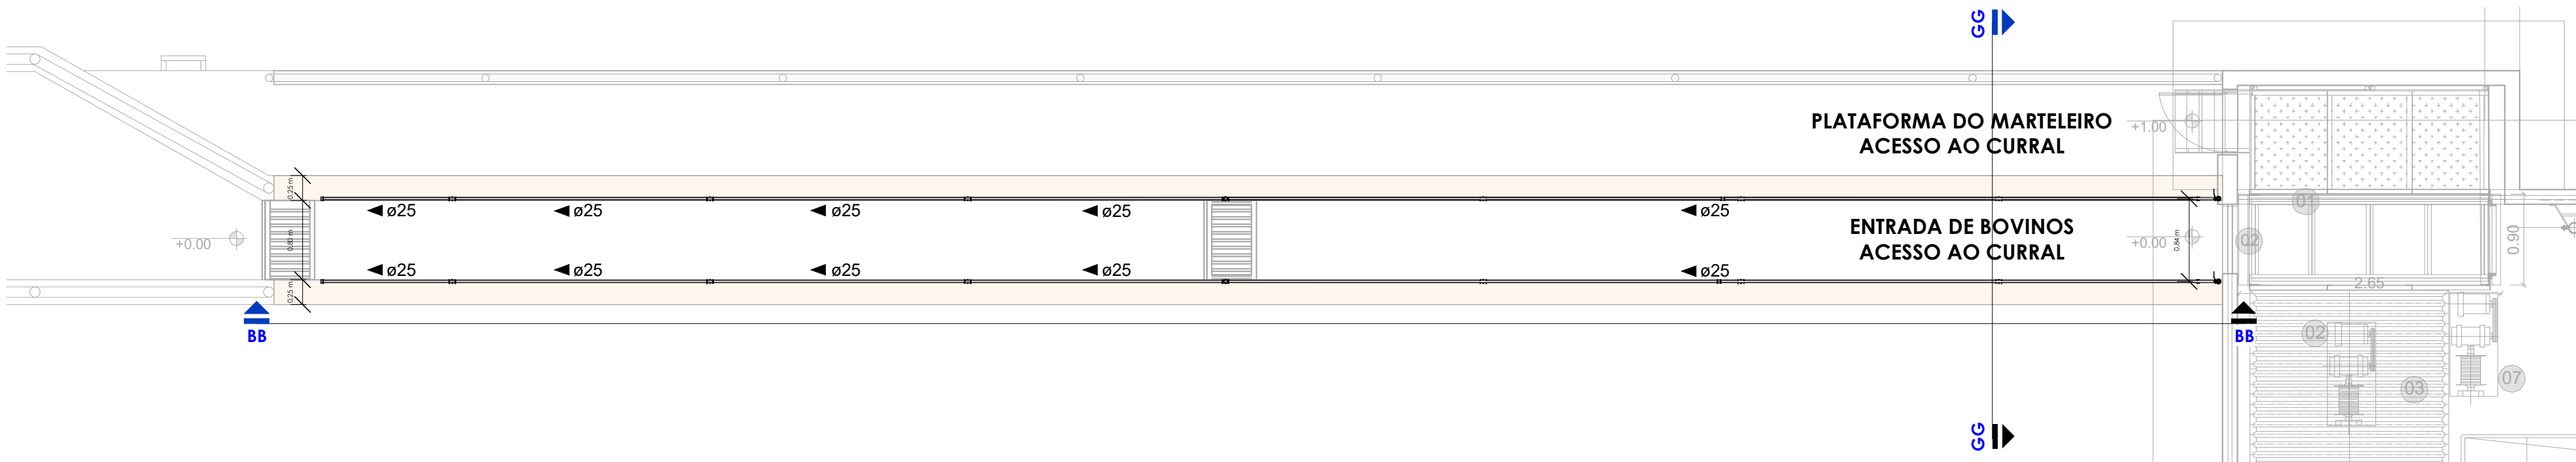


PLANTA BAIXA _ SERINGA_BOVINOS - ESC

1/50

LEGENDA:

- TUBULAÇÃO PVC BRANCO - ESGOTO
- TUBULAÇÃO PVC BRANCO SN - VENTILAÇÃO ESGOTO
- TUBULAÇÃO AÇO GALVANIZADO - ÁGUA FRIA
- TUBULAÇÃO AÇO GALVANIZADO - ÁGUA FRIA (PELO PISO)
- TUBULAÇÃO PVC MARROM - ÁGUA FRIA
- TUBULAÇÃO PVC MARROM - ÁGUA FRIA (PELO PISO)
- ALIMENTAÇÃO DO RESERV. SUPERIOR
- COLUNA DE VENTILAÇÃO
- COLUNA DE ÁGUA FRIA (BARRILETE)

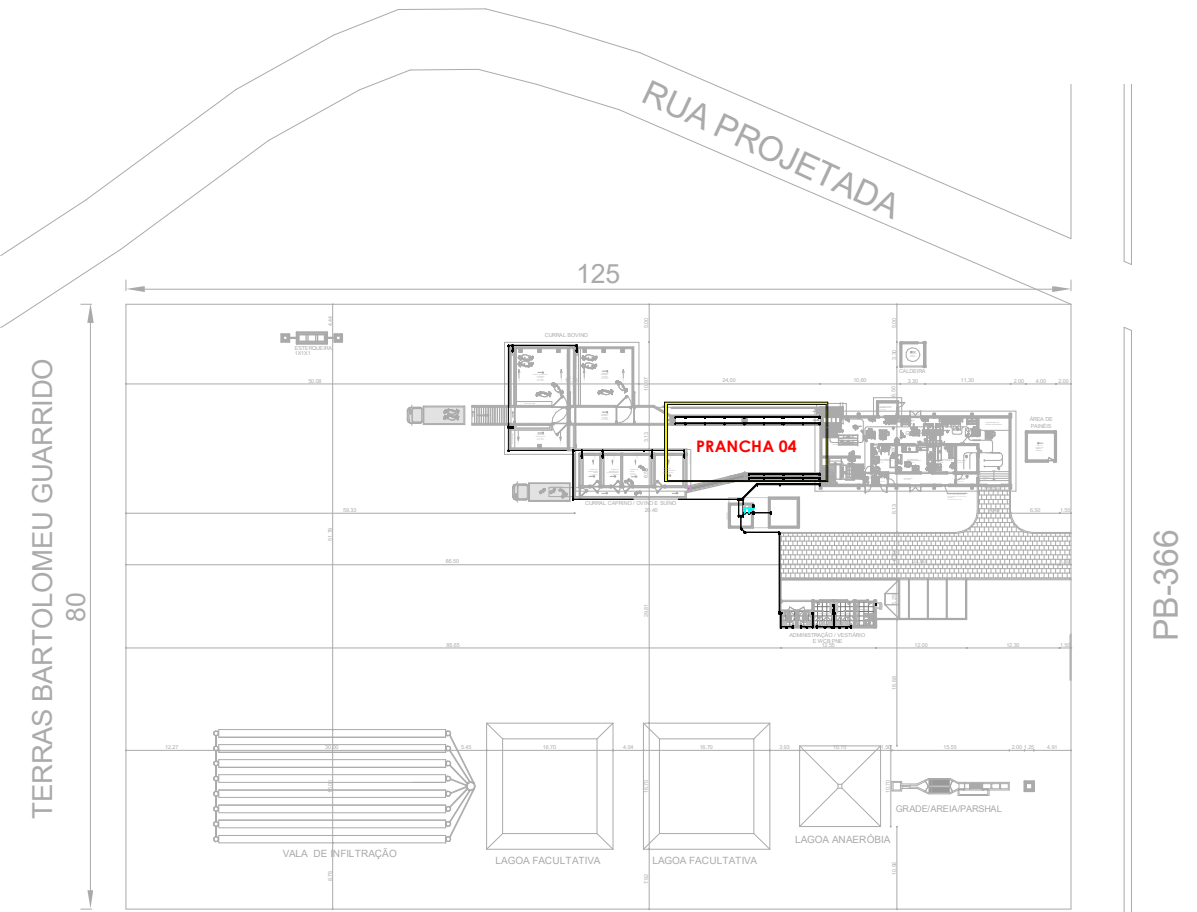

PLANTA BAIXA _ MATADOURO_COREMAS - ESC

1/1000

LINCOLN CARTAXO DE LIRA JUNIOR:06897861405

Assinado de forma digital por LINCOLN CARTAXO DE LIRA JUNIOR:06897861405
Dados: 2025.05.28 09:21:07 -03'00'

PROPRIETÁRIO: PREFEITURA MUNICIPAL DE COREMAS - PB

PROJETO: LINCOLN CARTAXO DE LIRA JÚNIOR CREA 160.814.689-8

PROJETO: INSTALAÇÕES HIDRÁULICAS, MATADOURO DE COREMAS
CONCEDENTE: PREFEITURA MUNICIPAL DE COREMAS - PB
CONVENIENTE: MUNICÍPIO DE COREMAS - PB
LOCAL: COREMAS - PB

DATA	14/05/2025	RESPONSÁVEL TÉCNICO	LINCOLN CARTAXO	RUBRICA	DADOS	CREA 160.814.689-8
CÓPIA						
VISTO						

PRANCHA: 04 / 04
DESCRIÇÃO: PLANTA BAIXA SERINGAS CORTES
ESCALA: INDICADA



Av. Gov. Flavio R. Coutinho, 500, sl. 601
Jd. Oceania, 58037-005 - João Pessoa (PB)
Tel +55 99924.4447
e-mail: contato@lclprojetos.com