



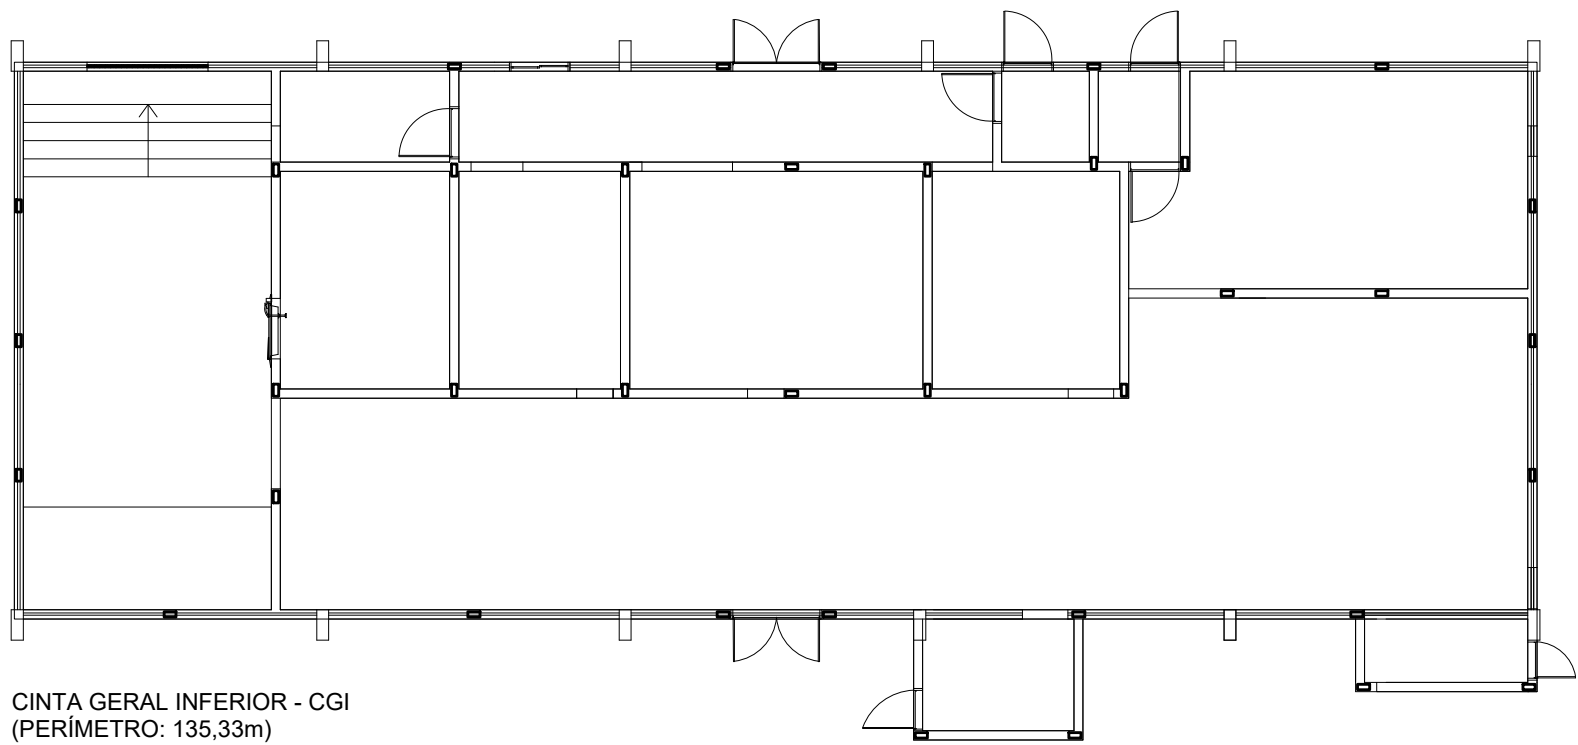

CINTA GERAL INFERIOR - CGI
(PERÍMETRO: 135,33m)

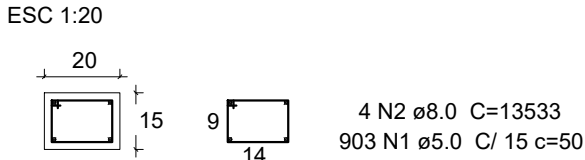

Planta Cinta Inferior – Curral bovino
escala + 1/125


Relação do aço

CGI



AÇO	N	DIAM	Q	UNIT (cm)	C.TOTAL (cm)
CA60	1	5.0	903	50	45150
CA50	2	8.0	4	13533	54132

Resumo do aço


AÇO	DIAM	C.TOTAL (m)	PESO + 10 % (kg)
CA50	8.0	541.3	235.2
CA60	5.0	451.5	76.4
PESO TOTAL			
CA50	235.2		
CA60	76.4		

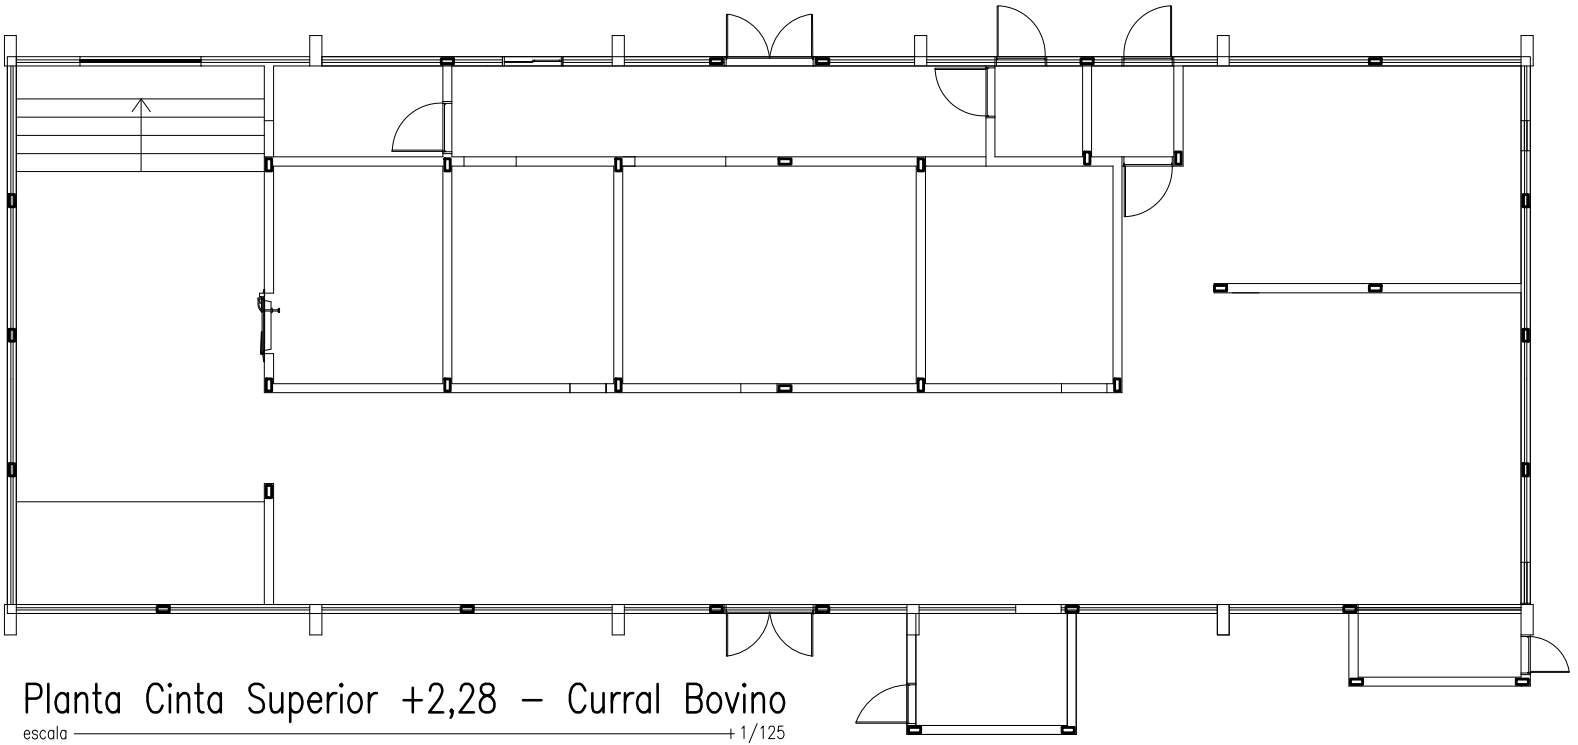




Planta Cinta Superior +2,28 – Curral Bovino
escala + 1/125

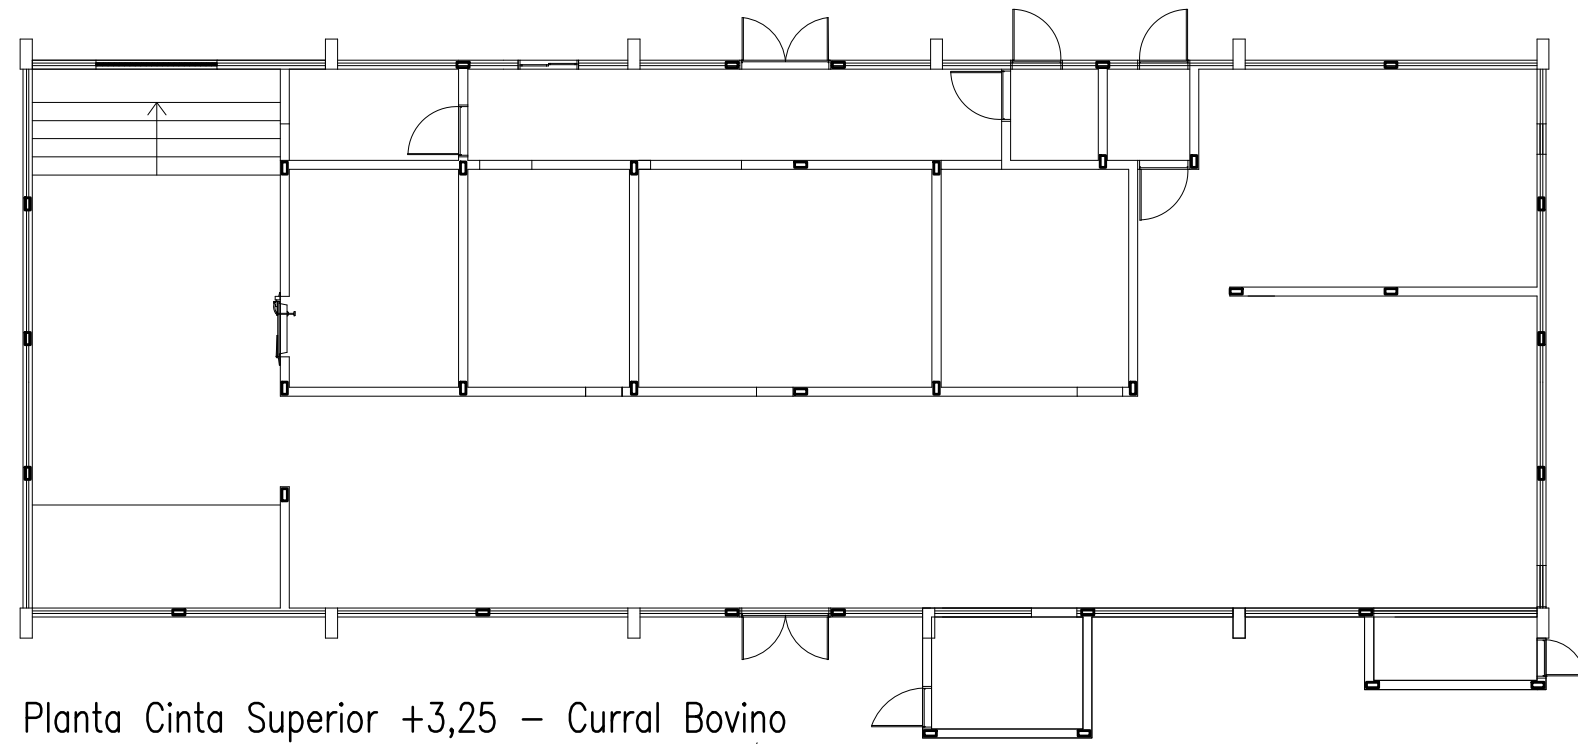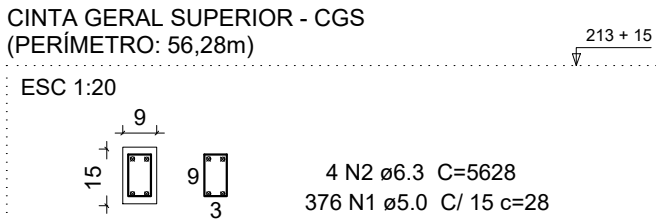


Planta Cinta Superior +3,25 – Curral Bovino
escala + 1/125

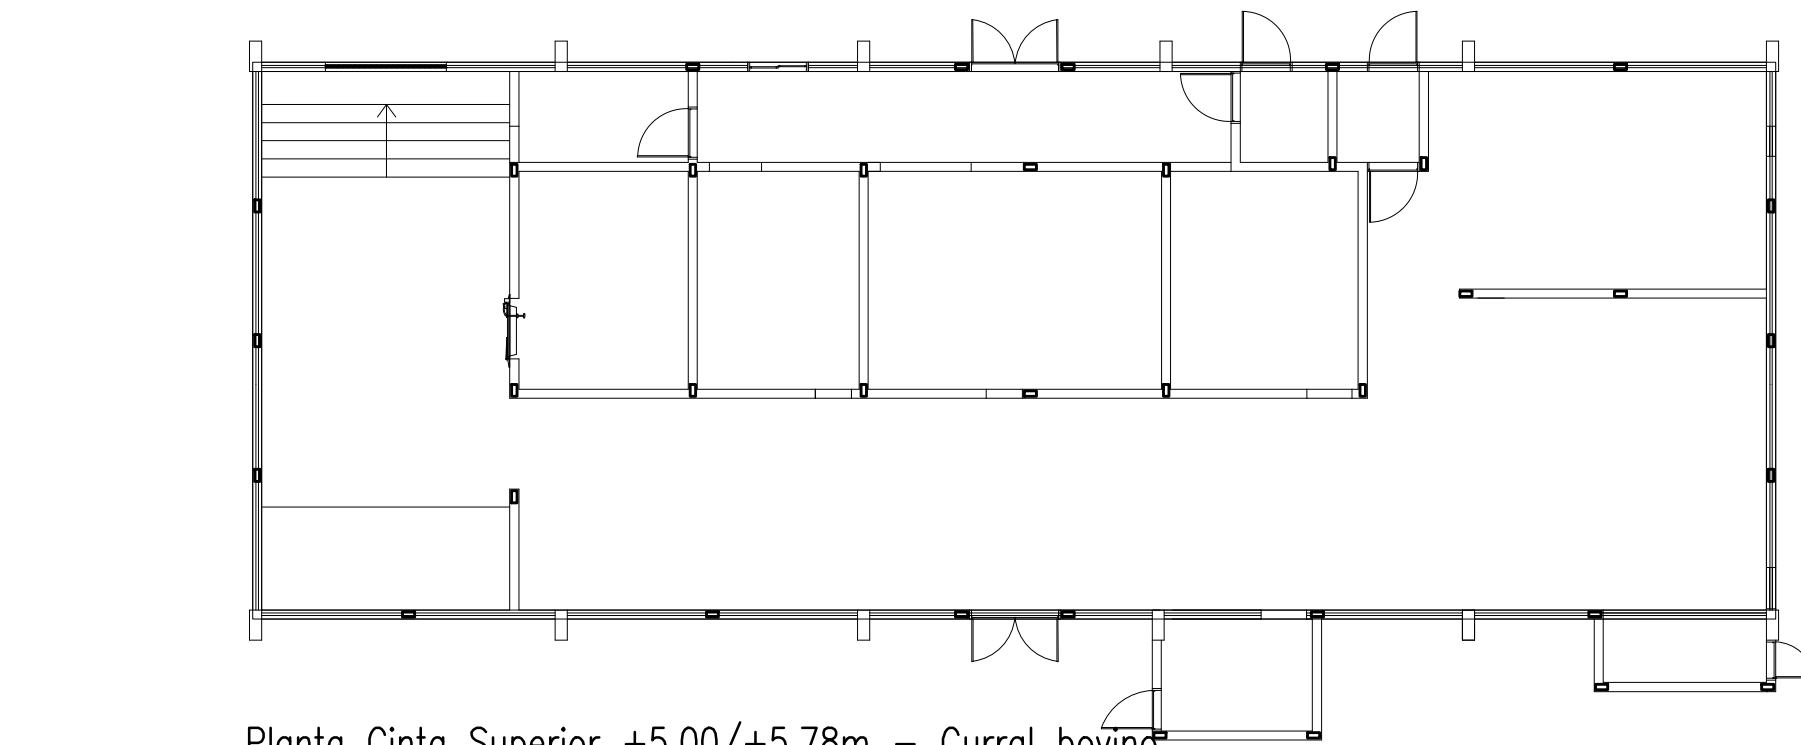

Planta Cinta Superior +5,00/+5,78m – Curral bovino
escala + 1/125

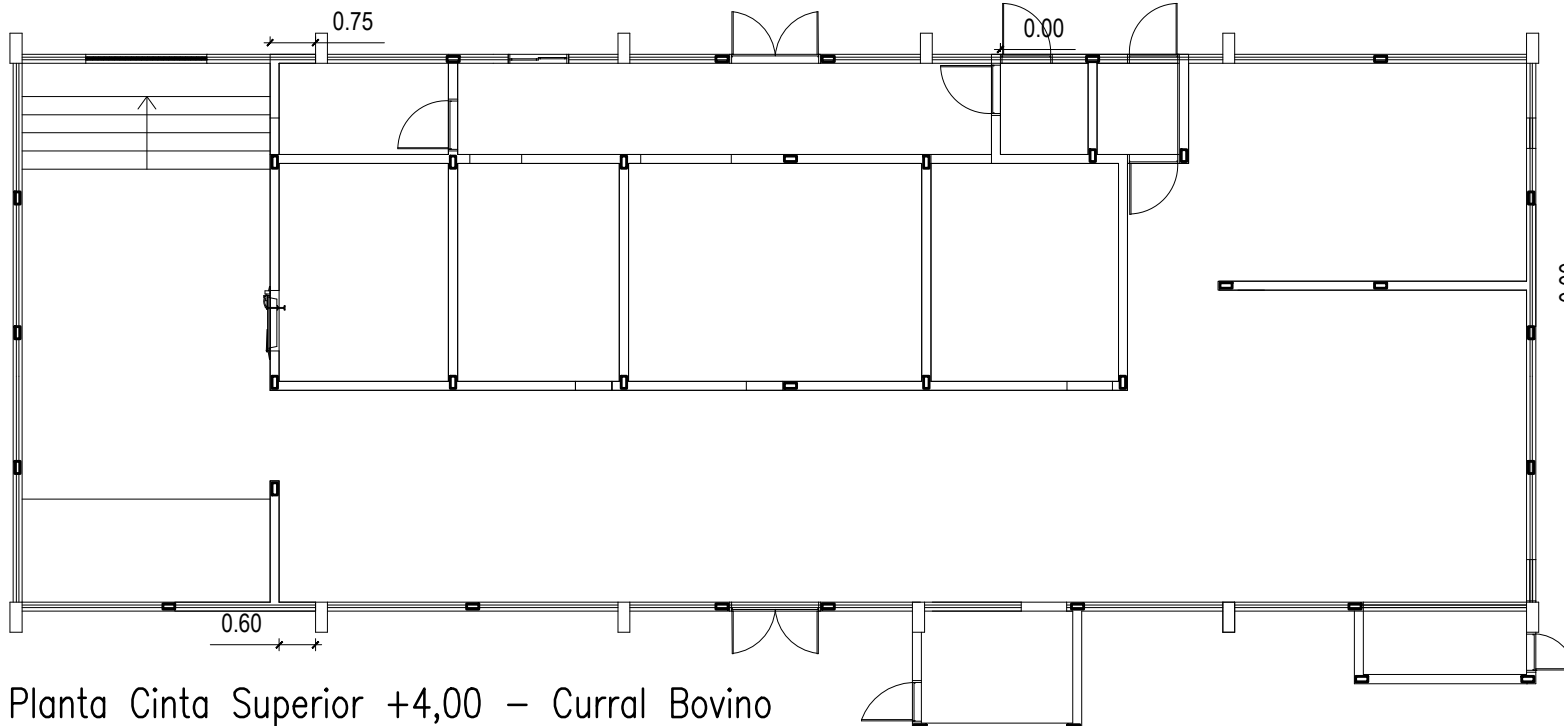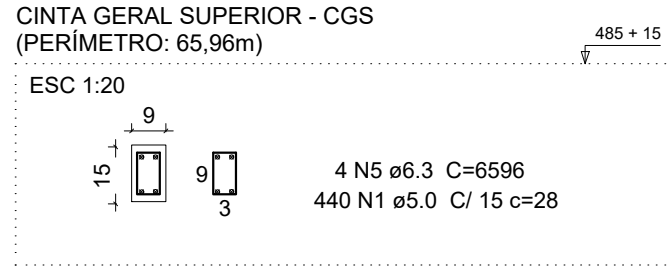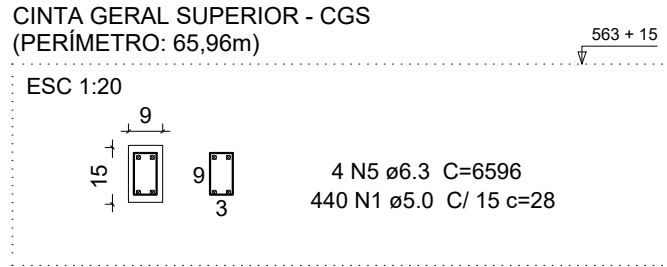

Planta Cinta Superior +4,00 – Curral Bovino
escala + 1/125

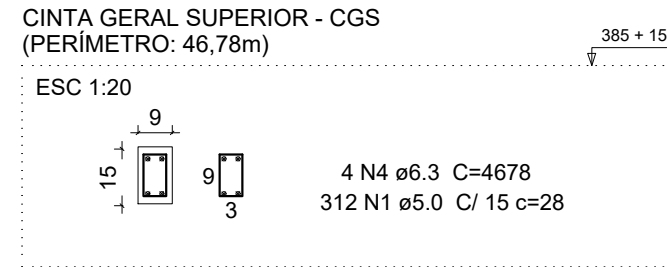

Documento assinado digitalmente
gov.br MICHAEL JACKSON MAMEDE SOUZA
Data: 11/03/2024 15:47:50-0300
Verifique em <https://validar.it.gov.br>

RESPONSÁVEL TÉCNICO:

PROPRIETÁRIO:

PRANCHA		PREFEITURA MUNICIPAL DE COREMAS – PB			
2/2		PROJETO DE CONSTRUÇÃO DE MATADOURO – 9389922022			
		PROJETO ESTRUTURAL - CINTAS E PILARES GALPÃO			
	DATA	RESPONSÁVEL		RUBRICA	
DESENHO					
PROJETO				ÁREA DO TERRENO	ÁREA ÚTIL
CÓPIA				10.000,00 M²	971,43 M²
ESCALA:		DESENHO:		ÁREA CONSTRUIDA	
1:1 25 1:1 25		PLANTA CINTA INFERIOR PLANTAS CINTA SUPERIOR		871,58 M²	