



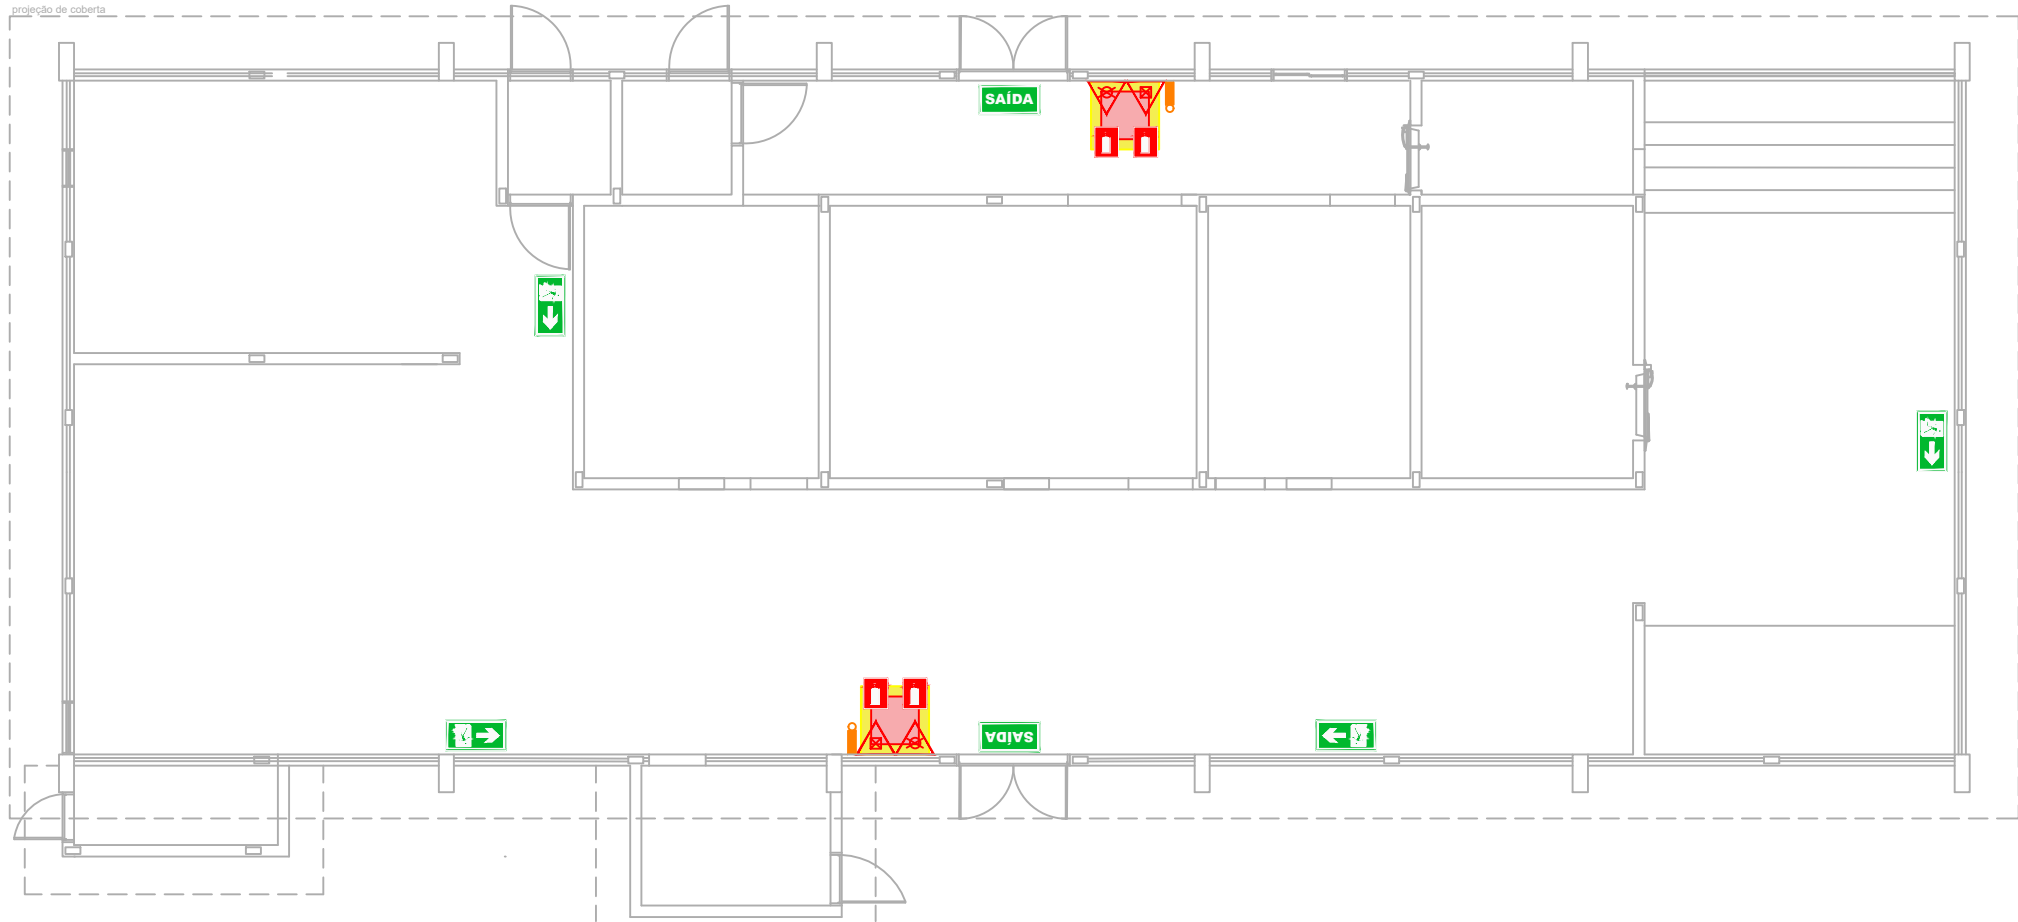

Planta Baixa – Galpão
escala 1/100

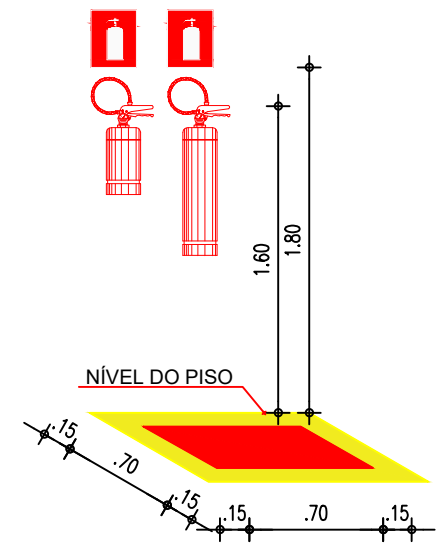

DETALHE EXTINTOR - INSTALAÇÃO PERSPECTIVA

- OBS:
- 1- Quando se tratar de hidrante e extintor de incêndio instalados em garagem, área de fabricação, depósito e locais utilizados para movimentação de mercadorias e de grande varejo deve ser implantada sinalização de piso.
 - 2- A sinalização de piso consiste em uma área quadrada de 1m de lado, sendo composta internamente por um quadrado de aresta 0,70m na cor vermelha contornado por borda de 0,15m de largura na cor amarela.
 - 3- O suporte de fixação do extintor deverá ser instalada com a previsão de suportar 2,5 vezes o seu peso total.

OBSERVAÇÕES

01	AS PLACAS DEVERÃO SER FIXADAS ACIMA DAS PORTAS A UMA DISTÂNCIA DE NO MÁXIMO 10cm DA VERGA OU PENDURADAS NO TETO , PERPENDICULAR AO SENTIDO DE FUGA E RESPEITANDO-SE A ALTURA PARA VISIBILIDADE, NESTE CASO DEVERÃO SER DUPLA FACE.
02	DEVERÁ SER PREVISTO UM CIRCUITO ELÉTRICO EXCLUSIVO PARA AS LUMINÁRIAS DE EMERGÊNCIA

SINALIZAÇÃO

	S1 - SAÍDA DE EMERGÊNCIA		S2 - SAÍDA DE EMERGÊNCIA
	S3 - SAÍDA DE EMERGÊNCIA		S12 - SAÍDA DE EMERGÊNCIA
	E5 - EXTINTOR DE INCÊNDIO		
	E17 - SINALIZAÇÃO DE SOLO PARA EQUIPAMENTOS DE COMBATE A INCÊNDIO (HIDRANTES E EXTINTORES)		

SIMBOLOGIA

	EXTINTOR PORTÁTIL 4kg PQS ABC (2-A : 20-BC)		PONTO DE ILUMINAÇÃO DE EMERGÊNCIA
	EXTINTOR PORTÁTIL 10 LITROS DE ÁGUA PRESSUR. (2A)		SINALIZAÇÃO DE SOLO


[Handwritten signature]
Engenheiro Civil
CREA-PB 161778178-9

RESPONSÁVEL TÉCNICO:


PROPRIETÁRIO:

PRANCHA		PREFEITURA MUNICIPAL DE COREMAS – PB	
1/3		PROJETO DE CONSTRUÇÃO DE MATADOURO – 9389922022	
		PROJETO ARQUITETÔNICO – GERAL	
	DATA	RESPONSÁVEL	RUBRICA
DESENHO			
PROJETO			
CÓPIA			
ESCALA:	DESENHO:		
1/100	PLANTA BAIXA - GALPÃO		
S/ESC	DETALHE EXTINTOR		


CORPO DE BOMBEIROS MILITAR DA PARAÍBA - AN / 54345/2023
Data e hora: 22/02/2024 10:36:34 Pág. 1/3 U:171 L:TA: 00029252/2024
Assinatura Digital: 90a81ef6161aaee2eb7b2b49b4d737844b583d145
Autenticar: bombeiros.pb.gov.br/regularize-sua-edificacao/

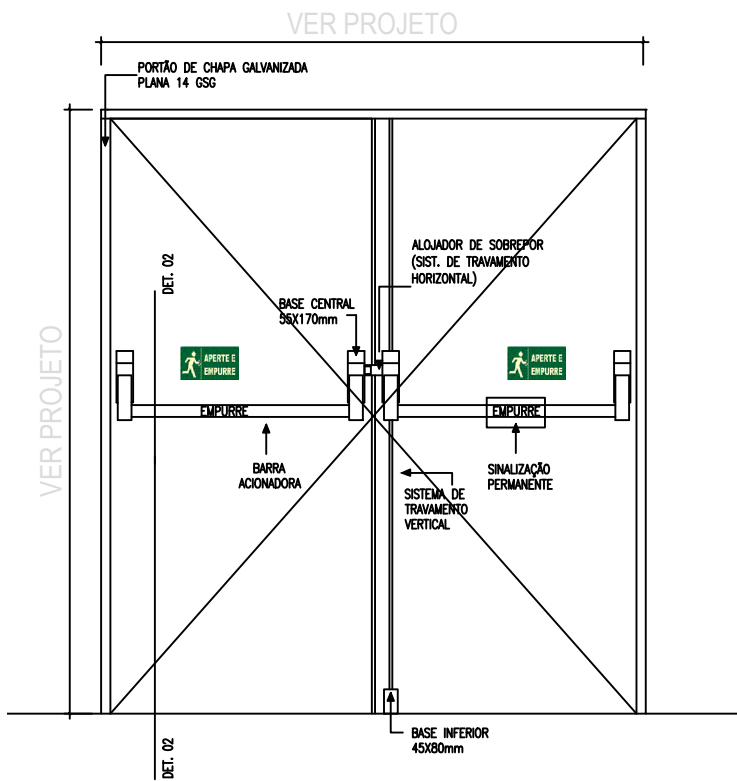

Detalhe em Vista – Portões de Saída de Emergência
escala 1/25

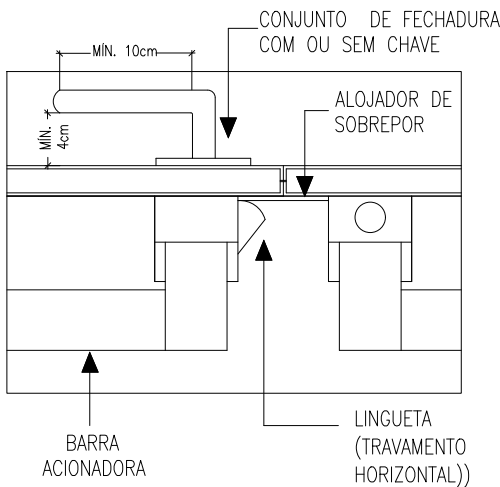

Detalhe 01
escala 1/5

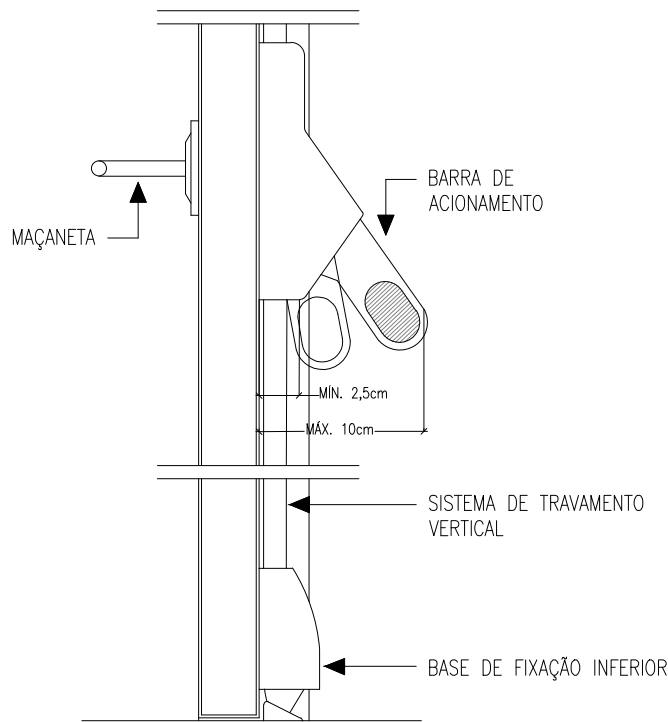

Detalhe 02
escala 1/5

Handwritten signature of the technical responsible.
Arquiteto Responsável de Sala:
Engenheiro Civil
CREA-PB 161778178-9

RESPONSÁVEL TÉCNICO:

PROPRIETÁRIO:

PRANCHA 2/3	PREFEITURA MUNICIPAL DE COREMAS – PB		
	PROJETO DE CONSTRUÇÃO DE MATADOURO – 9389922022		
	PROJETO ARQUITETÔNICO – GERAL		


	DATA	RESPONSÁVEL	RUBRICA
DESENHO			
PROJETO			
CÓPIA			

ESCALA:	DESENHO:
1/25 1/25 1/5 1/5	PLANTA BAIXA - PORTÃO SAÍDA EMERGÊNCIA DETALHE VISTA - PORTÃO SAÍDA EMERGÊNCIA DETALHE 01 DETALHE 02




CORPO DE BOMBEIROS MILITAR DA PARAÍBA - AN / 54845/2023
Data e hora: 22/02/2024 10:36:34 Pág. 2/3 U:171 L:TA: 00029252/2024
Assinatura Digital: 90a81ef6164aae2eb7b2b49b4d737844b583d145
Autenticar: bombeiros.pb.gov.br/regularize-sua-edificacao/




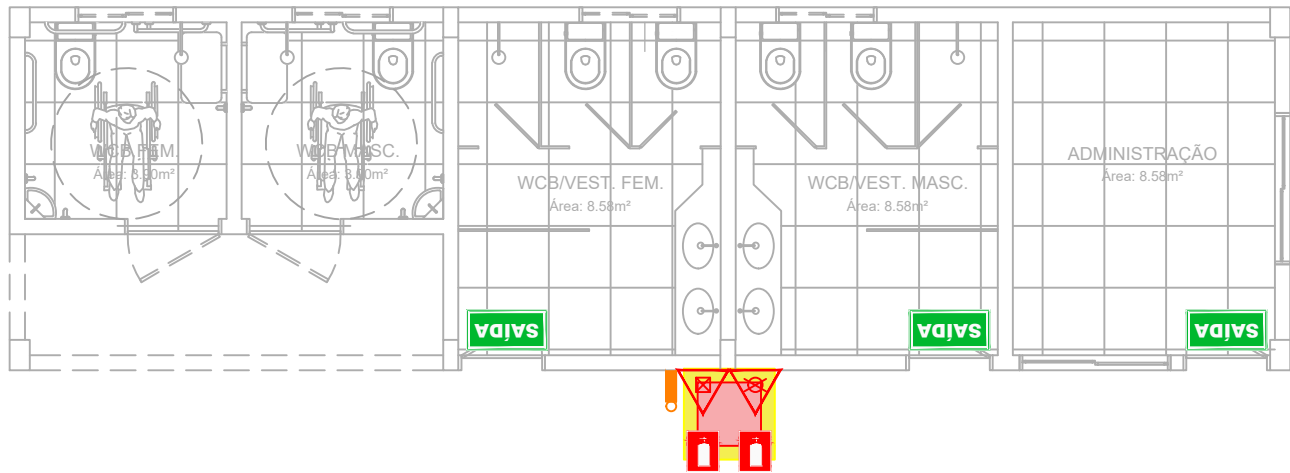


Planta Baixa – Administração/Vestiários/WCB PNE
escala 1/75

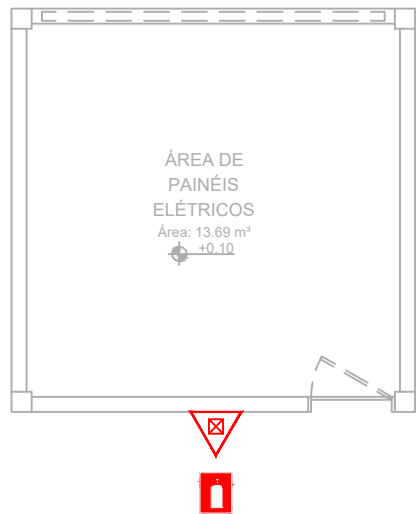

Planta Baixa – Área de Painéis Elétricos
escala 1/75

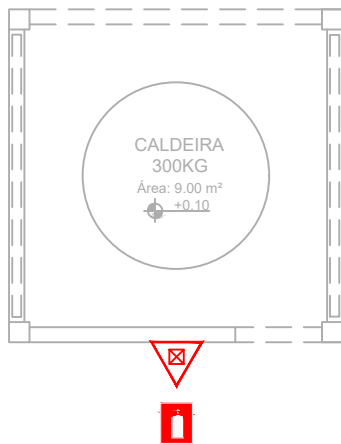

Planta Baixa – Área de Caldeira
escala 1/75

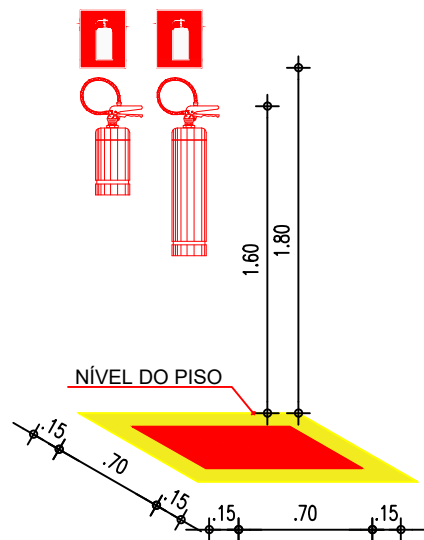

DETALHE EXTINTOR - INSTALAÇÃO PERSPECTIVA

- OBS:
- Quando se tratar de hidrante e extintor de incêndio instalados em garagem, área de fabricação, depósito e locais utilizados para movimentação de mercadorias e de grande varejo deve ser implantada sinalização de piso.
 - A sinalização de piso consiste em uma área quadrada de 1m de lado, sendo composta internamente por um quadrado de aresta 0,70m na cor vermelha contornado por borda de 0,15m de largura na cor amarela.
 - O suporte de fixação do extintor deverá ser instalada com a previsão de suportar 2,5 vezes o seu peso total.

[Assinatura]
Engenheiro Civil
CREA-PA 141778-9

RESPONSÁVEL TÉCNICO:

PROPRIETÁRIO:

PRANCHA	PREFEITURA MUNICIPAL DE COREMAS – PB		
	PROJETO DE CONSTRUÇÃO DE MATADOURO – 9389922022		
	PROJETO ARQUITETÔNICO – GERAL		

	DATA	RESPONSÁVEL	RUBRICA
DESENHO			
PROJETO			
CÓPIA			
ESCALA:		DESENHO:	
1/75		PLANTA BAIXA - ADM./VESTIÁRIOS/WCB PNE	
1/75		PLANTA BAIXA - ÁREA DE CALDEIRA	
1/75		PLANTA BAIXA - ÁREA DE PAINÉIS ELÉTRICOS	
S/ESC		DETALHE EXTINTOR	



CORPO DE BOMBEIROS MILITAR DA PARAÍBA - AN / 54345/2023
Data e hora: 22/02/2024 10:36:34 Pág. 3/3 U:171 L:TA: 00029252/2024
Assinatura Digital: 90a81ef6164aee2eb7b2b49b4d737844b836145
Autenticar: bombeiros.pb.gov.br/regularize-sua-edificacao/

