




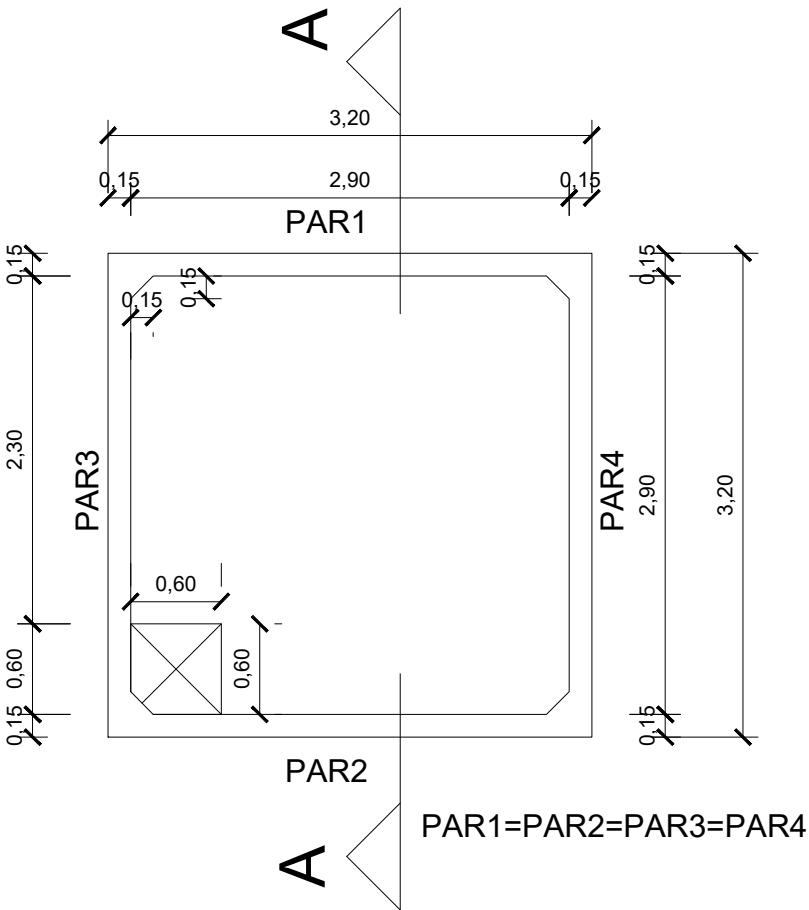

Forma Reservatório – Reservatório Superior
escala 1/50

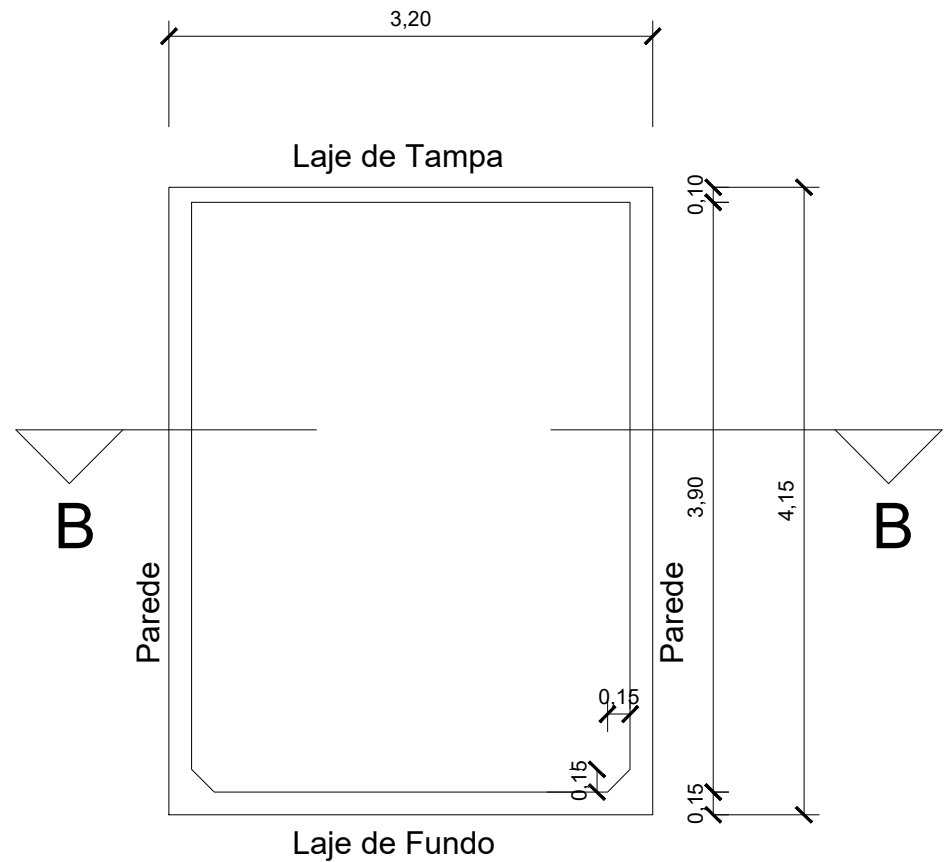


Corte Vertical AA
escala 1/50

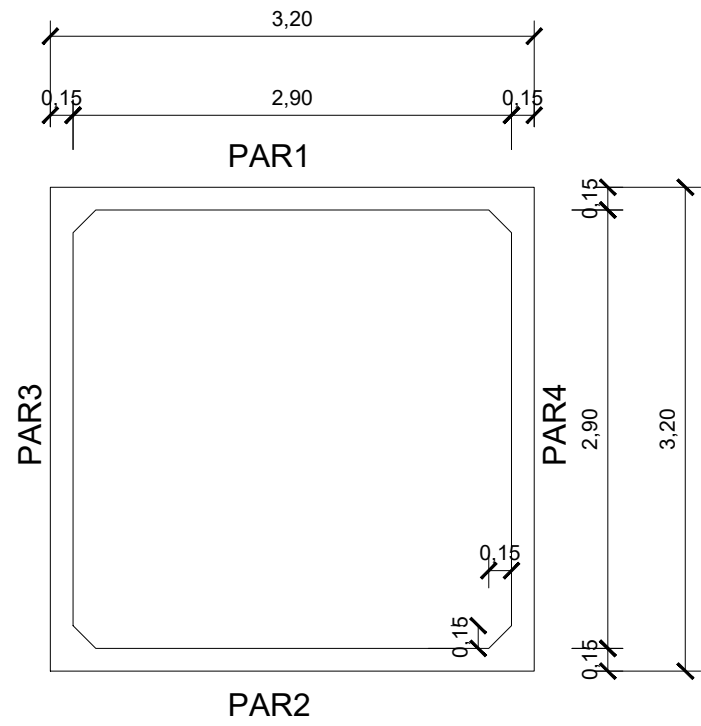


Corte Horizontal BB
escala 1/50

Vigas de Travamento
Escala 1:50


Vigas de Travamento
Cobrimeto Nominal: 2,5cm

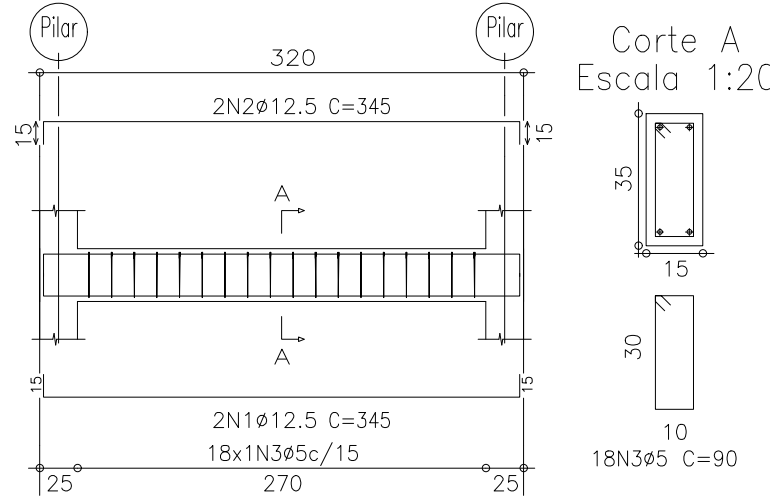


Elemento	Pos.	Diam.	Q.	Dob. (cm)	Reta (cm)	Dob. (cm)	Comp. (cm)	Total (cm)	CA-50-A (kg)	CA-60-B (kg)
V 1=V 2=V 3=V 4	1	Ø12.5	2	15	315	15	345	690	6.8	
	2	Ø12.5	2	15	315	15	345	690	6.8	
	3	Ø5	18				90	1620		2.5
	Total+10%: (x4):								15.0 60.0	2.8 11.2
Ø5:									0.0	11.2
Ø12.5:									60.0	0.0
Total por nível de travamento:									60.0	11.2
Total (x4 nível de travamento):									240.0	44.8

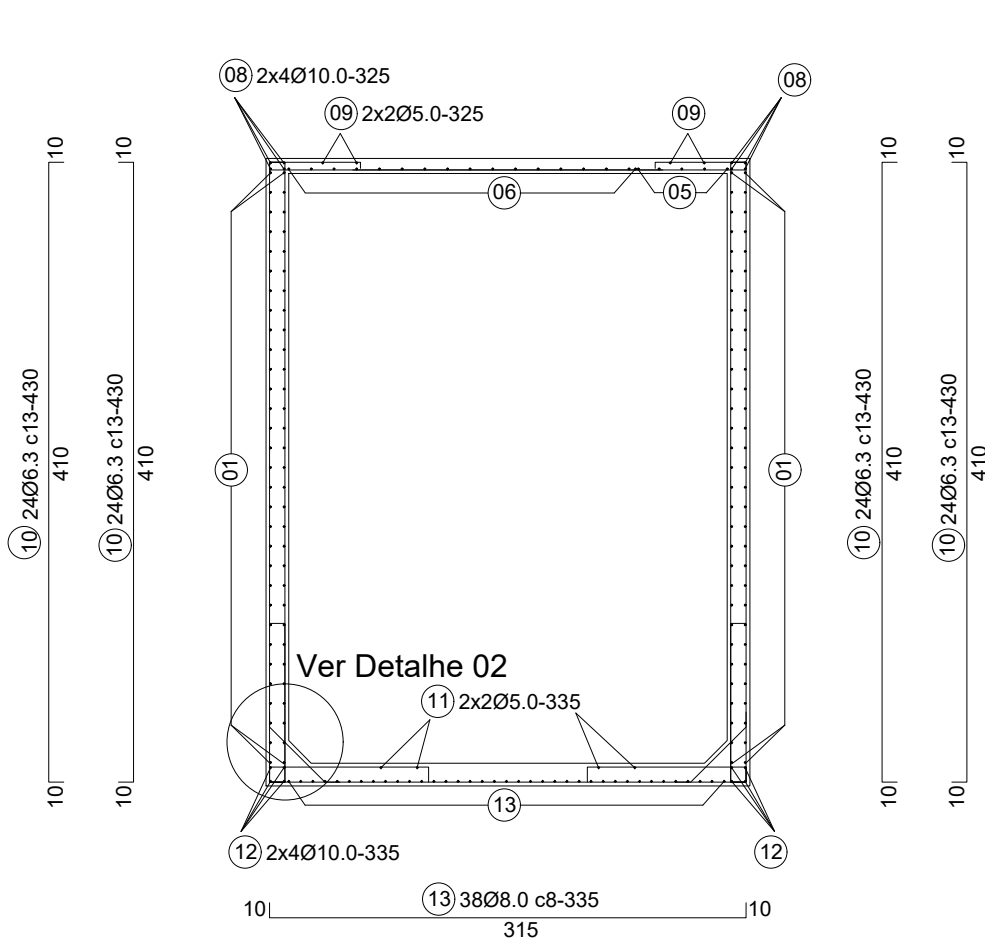


Armação do Corte Vertical AA
escala 1/50

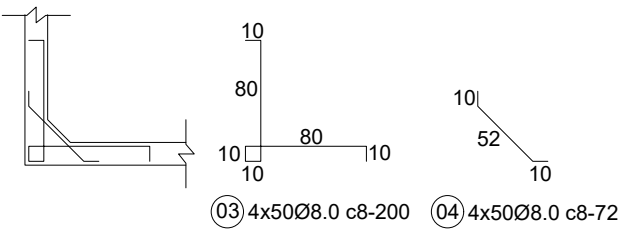


Detalhe 01: Ligação Parede = Parede
escala 1/50

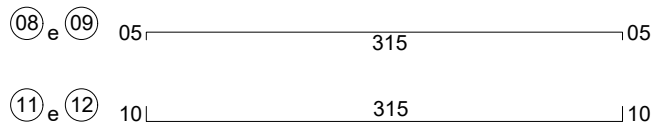

Detalhe das Armadura – 8,9,11 e 12
escala 1/50

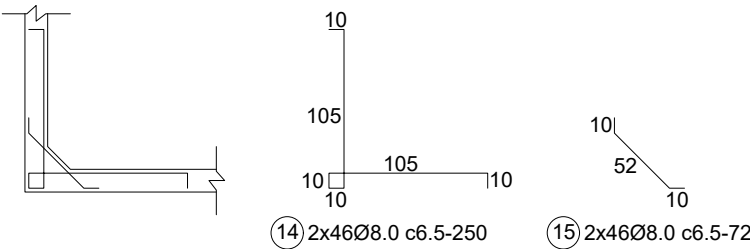

Detalhe 02: Ligação Fundo – Parede
escala 1/50

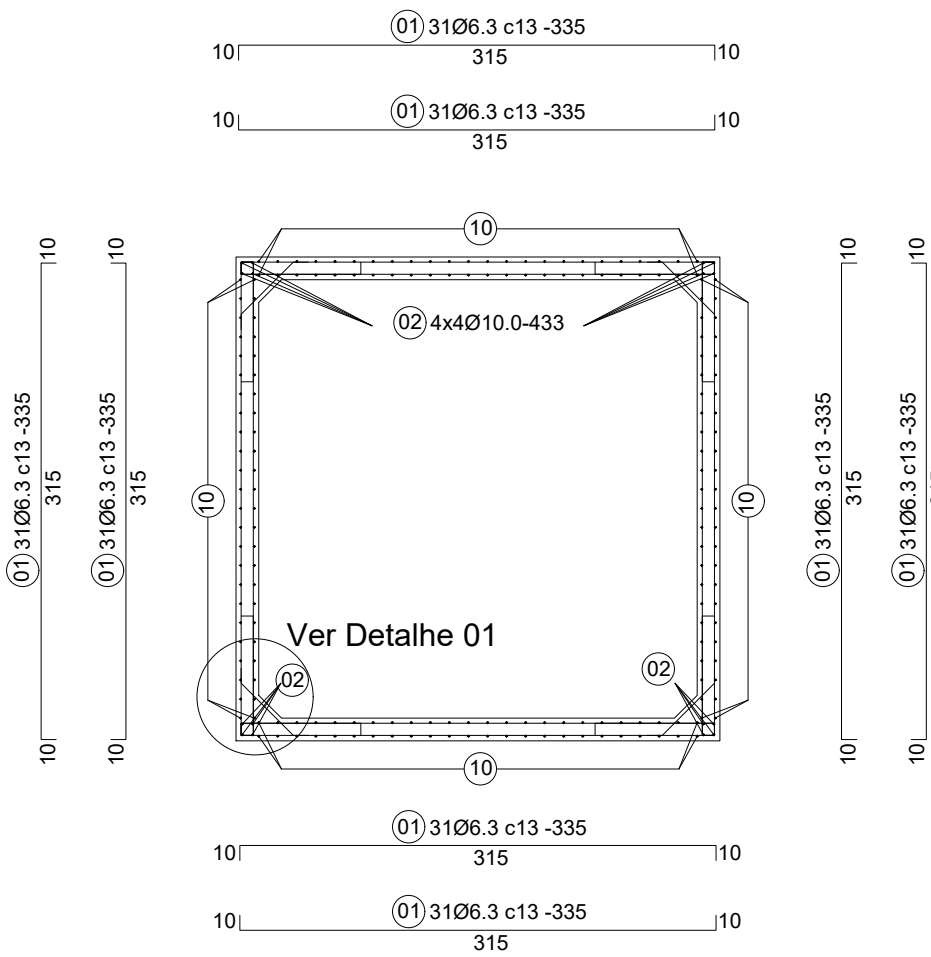

Armação do Corte Horizontal BB
escala 1/50

Resumo Aço Baldrames Vigas	Comp. total (m)	Peso+10% (kg)	Total
CA-50-A Ø12.5	220.8	240.0	240.0
CA-60-B Ø5	259.2	44.8	44.8
Total			285

QUADRO DE FERROS - Lajes do reservatório

AÇO CA 50 - 60				
Nº	Ø (mm)	Quantidade	Comprimento(m)	
			Unitário	Total
01	6.3	248	3,35	830,80
02	10.0	16	4,33	69,28
03	8.0	200	2,00	400,00
04	8.0	200	0,72	144,00
05	6.3	10	2,70	27,00
06	6.3	34	3,30	112,20
07	10.0	8	1,20	9,60
08	10.0	16	3,25	52,00
09	5.0	8	3,25	26,00
10	6.3	192	4,30	825,60
11	5.0	8	3,35	26,80
12	10.0	16	3,35	53,60
13	8.0	76	3,35	254,60
14	8.0	184	2,50	460,00
15	8.0	184	0,72	132,48

RESPONSÁVEL TÉCNICO:

PROPRIETÁRIO:

PRANCHA		PREFEITURA MUNICIPAL DE COREMAS – PB			
1/2		PROJETO DE CONSTRUÇÃO DE MATADOURO – 9389922022			
		PROJETO ESTRUTURAL - RESERVATÓRIO DE ASTECIMENTO DE ÁGUA			
	DATA	RESPONSÁVEL		RUBRICA	
DESENHO					
PROJETO				ÁREA DO TERRENO	ÁREA ÚTIL
CÓPIA				10.000,00 M²	971,43 M²
				ÁREA CONSTRUÍDA	871,58 M²
ESCALA:		DESENHO:			
1:50		FORMA RESERVATÓRIO			
1:50		CORTE AA E BB			
1:50		ARMAÇÃO DOS CORTES			
1:50		DETALHES ARMADURA E LIGAÇÕES			