


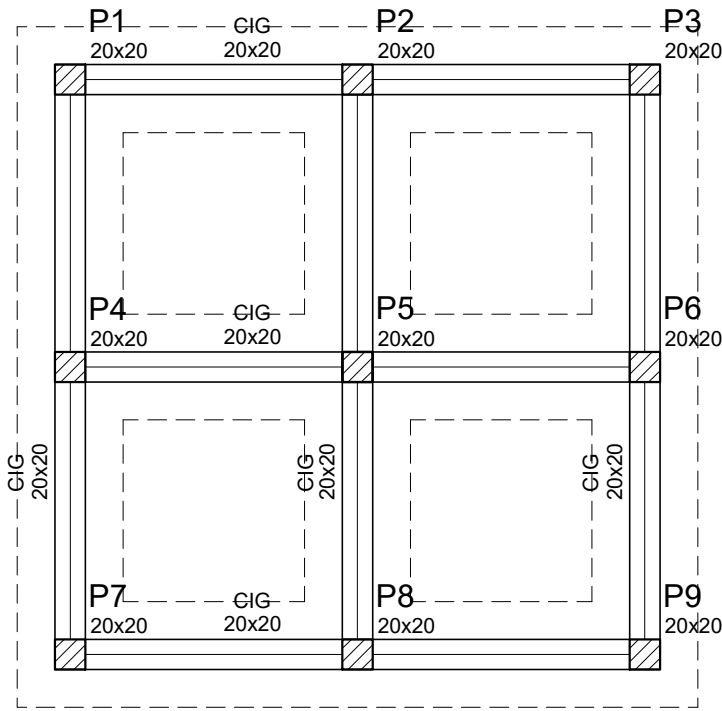

Forma Base de Reservatório Inferior
escala 1/50

Legenda dos Pilares

Pilar que morre

Pilar que passa

Pilar que nasce

Pilar com mudança de seção

Características dos materiais

fck (kgf/cm²)	Ecs (kgf/cm²)
250	238000

Cinta geral


Nome	Seção (cm)	Elevação (cm)	Nível (cm)
CIG	20x20	0	0
CIG	20x20	0	0
CIG	20x20	0	0
CIG	20x20	0	0
CIG	20x20	0	0
CIG	20x20	0	0

CIG

SEÇÃO A-A

ESC 1:25

Detalhe – Cintas
escala 1/25

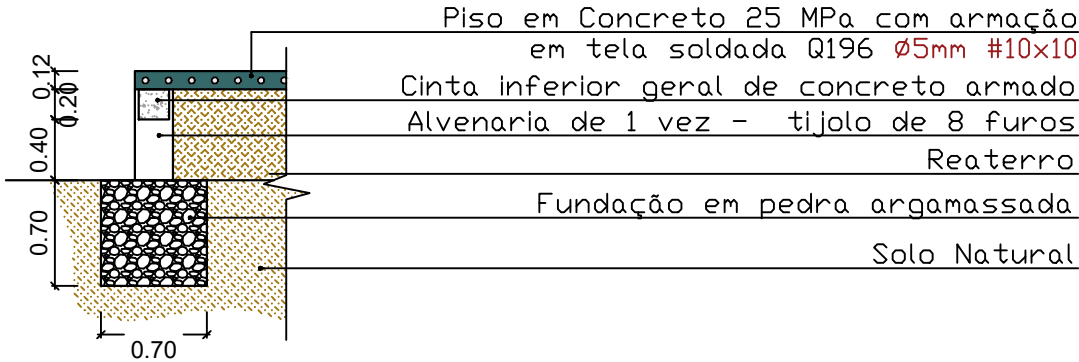

Detalhe – Corte
escala 1/50

Relação do aço

SIG

AÇO	N	DIAM	Q	UNIT (cm)	C.TOTAL (cm)
CA60	1	5.0	99	68	6732
CA50	2	5.0	170	68	11560
	3	10.0	24	394	9456
	4	12.5	36	122	4392

Resumo do aço

AÇO	DIAM	C.TOTAL (m)	PESO + 10 % (kg)
CA50	10.0	94.5	64.1
	12.5	43.9	46.5
CA60	5.0	182.9	30.9
PESO TOTAL			
CA50	110.6		
CA60	30.9		

P1=P2=P3=P4=P5
=P6=P7=P8=P9

NÍVEL SOLO

ESC 1:20

CORTE

ESC 1:25

Detalhe – Pilares
escala 1/50

Pilares

Nome	Seção (cm)	Elevação (cm)	Nível (cm)
P1	20 x 20	0	0
P2	20 x 20	0	0
P3	20 x 20	0	0
P4	20 x 20	0	0
P5	20 x 20	0	0
P6	20 x 20	0	0

RESPONSÁVEL TÉCNICO:

PROPRIETÁRIO:

PRANCHA

1/1

PREFEITURA MUNICIPAL DE COREMAS – PB

PROJETO DE CONSTRUÇÃO DE MATADOURO – 9389922022

PROJETO ESTRUTURAL - BASE DE RESERVATÓRIO INFERIOR

	DATA	RESPONSÁVEL	RUBRICA		
DESENHO					
PROJETO			ÁREA DO TERRENO	ÁREA ÚTIL	ÁREA CONSTRUÍDA
CÓPIA			10.000,00 M²	971,43 M²	871,58 M²

ESCALA:

1:50
1:25
1:50

DESENHO:

FORMA BASE DE RESERVATÓRIO INFERIOR
DETALHE PILARES E CINTAS
DETALHE CORTE

9389922022_BaseCxAgua_Estrutural