



ELEVAÇÃO SUPERIOR | BANCO 02
ESCALA 1/75




ELEVAÇÃO LATERAL | BANCO 02
ESCALA 1/75

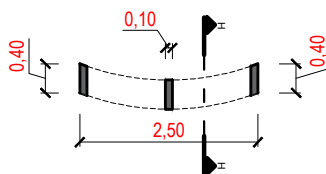


PLANTA BAIXA | BANCO 02
ESCALA 1/75

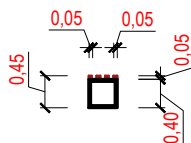


CORTE HH | BANCO 02
ESCALA 1/75

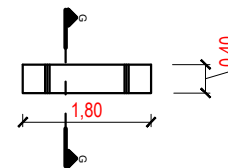


ELEVAÇÃO SUPERIOR | BANCO 01
ESCALA 1/75

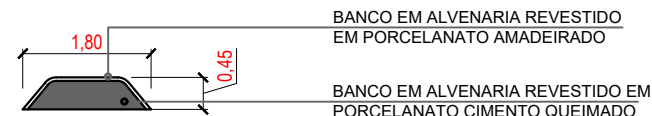

ELEVAÇÃO LATERAL | BANCO 01
ESCALA 1/75

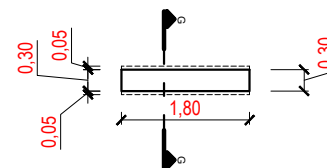

PLANTA BAIXA | BANCO 01
ESCALA 1/75

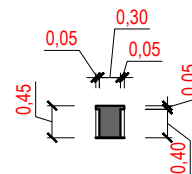

CORTE GG | BANCO 01
ESCALA 1/75