


PLANTA BAIXA | VESTIÁRIO
ESCALA 1/100


PISO REVESTIDO EM
CERÂMICA ACETINADO TIPO
CIMENTO QUEIMADO

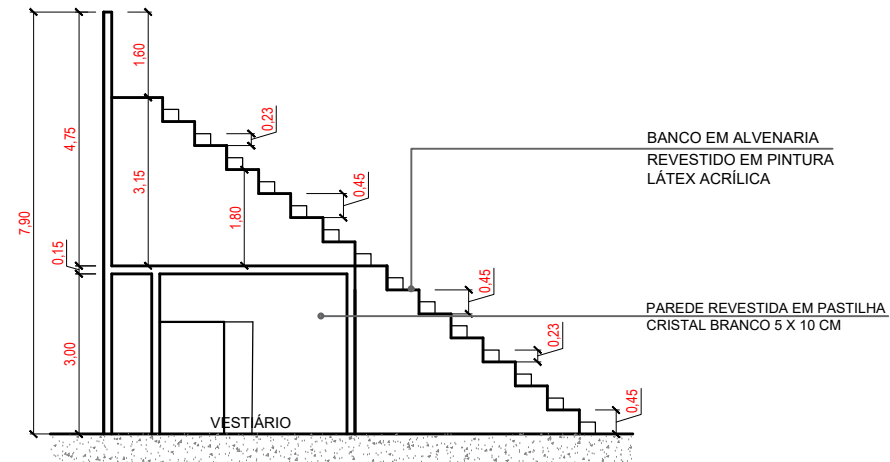

CORTE | CC
ESCALA 1/100

QUADRO DE ESQUADRIA

TIPO	DESCRIÇÃO	LARGURA	ALTURA	FOLHAS	PEITORIL	QUANT.:
P1	PORTA DE ALUMÍNIO	0.80	2.10	1	-	19
P2	PORTA DE MADEIRA	0.80	2.10	1	-	2
P3	PORTA DE MADEIRA	0.80	2.10	1	-	2
P4	PORTA DE ALUMÍNIO	0.80	2.10	1	-	10
P5	PORTÃO DE AÇO	4.00	2.10	1	-	1
P6	PORTÃO DE AÇO	1.20	2.10	1	-	2
P7	PORTÃO DE AÇO	3.50	2.10	1	-	1
J1	JANELA DE VIDRO - BASCULANTE	0.80	0.40	2	1.70	6
J2	JANELA DE MADEIRA - BASCULANTE	4.15	1.00	3	1.10	2
J3	JANELA DE MADEIRA - BASCULANTE	0.80	1.00	1	1.10	2
J4	JANELA DE MADEIRA - BASCULANTE	1.60	1.00	2	1.10	2
J5	JANELA DE CONCRETO - COBOGÓ	3.00	0.40	1	1.70	4
J6	JANELA DE CONCRETO - COBOGÓ	2.00	0.40	1	1.70	3
J7	JANELA DE CONCRETO - COBOGÓ	1.25	0.40	1	1.70	2
J8	JANELA DE VIDRO - CORRER	0.90	1.00	2	1.10	2
J9	JANELA DE VIDRO - CORRER	3.35	1.00	4	1.10	1

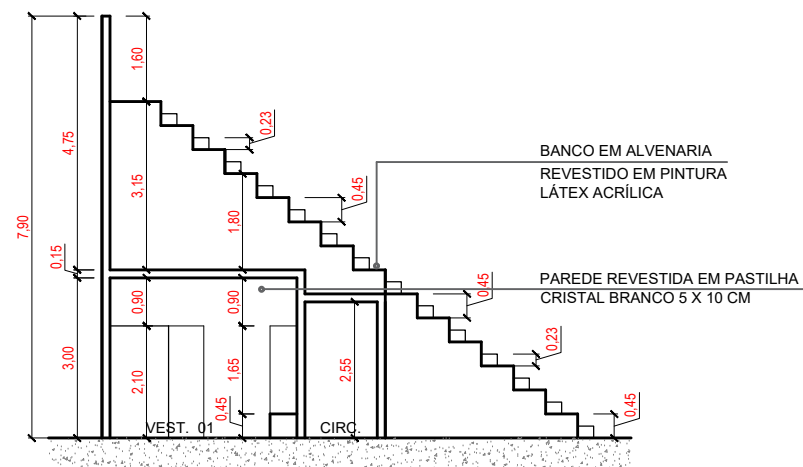

CORTE | AA
ESCALA 1/100