



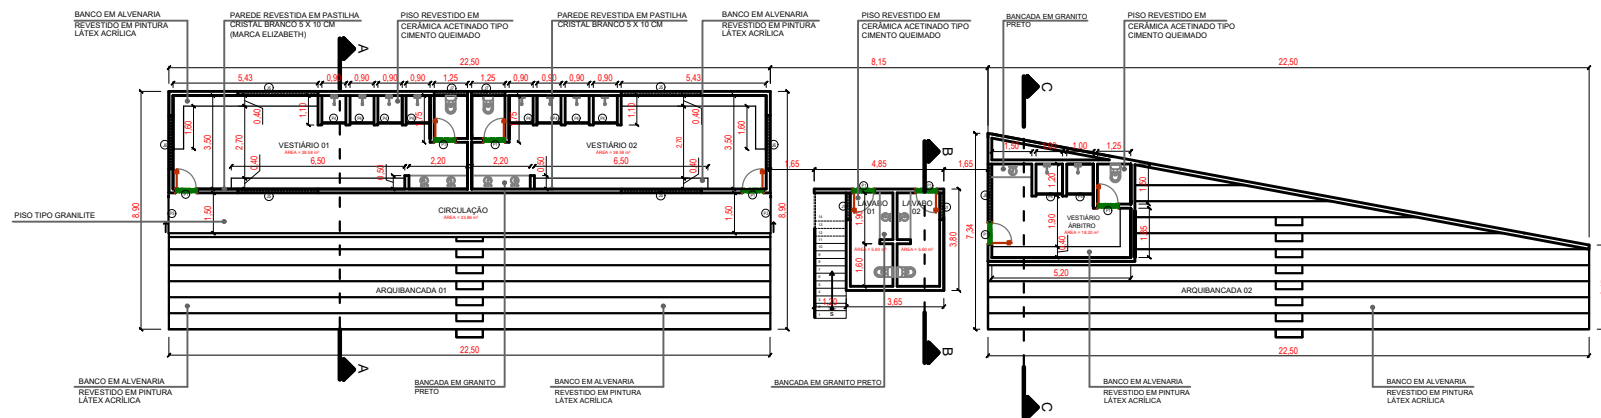

PLANTA BAIXA | VESTIÁRIOS | LAVABOS
ESCALA 1/200

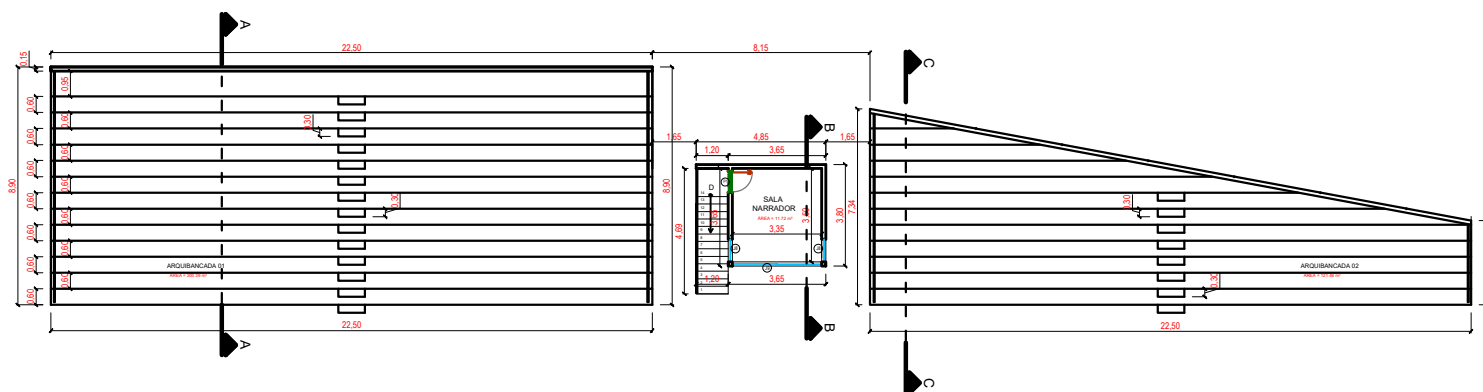

PLANTA BAIXA | ARQUIBANCADA | SALA NARRADOR
ESCALA 1/200