
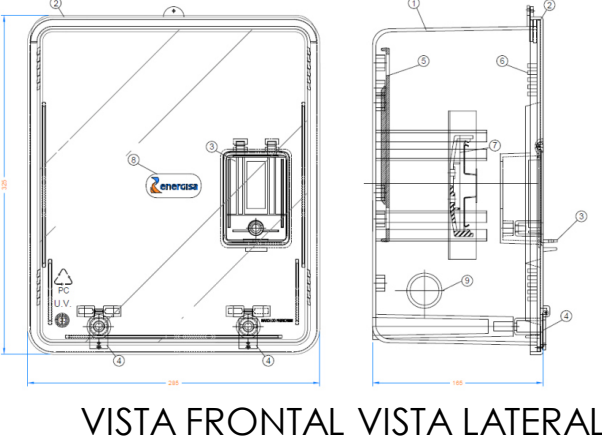
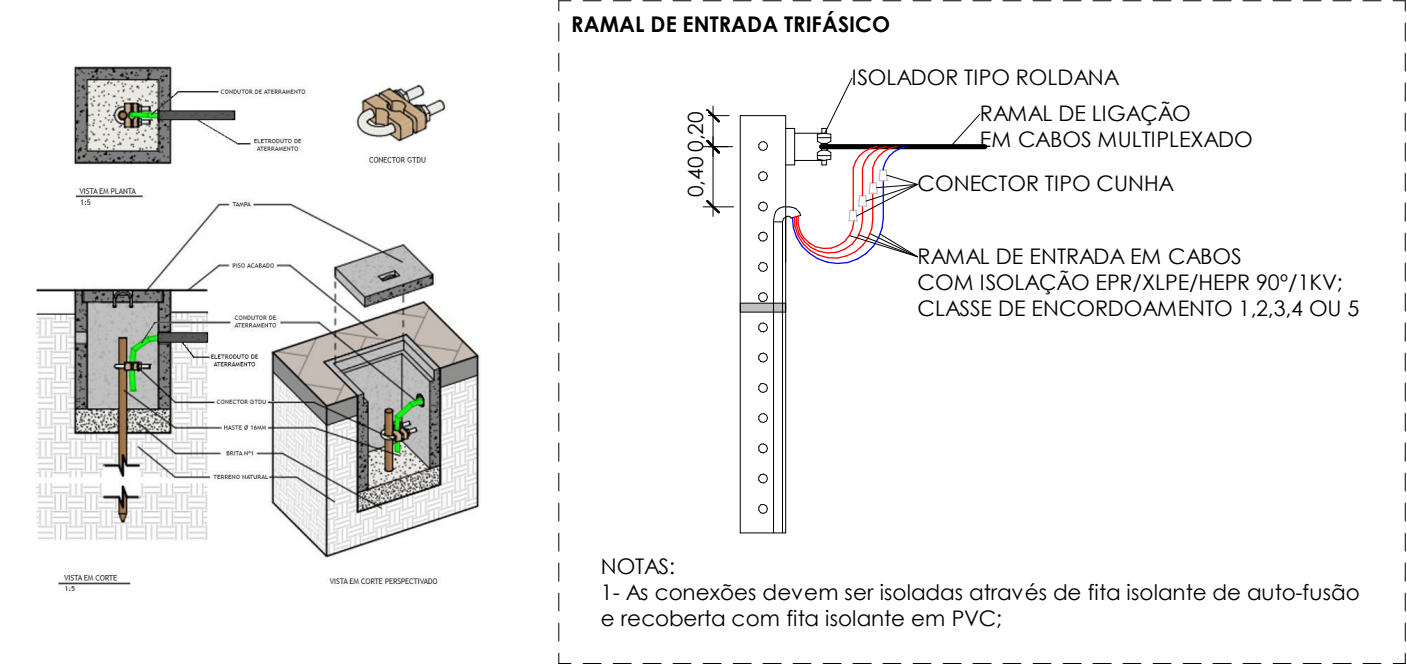


TODOS OS POSTES E ESTRUTURAS METÁLICAS, DEVEM SER DEVIDAMENTE ATERRADOS.

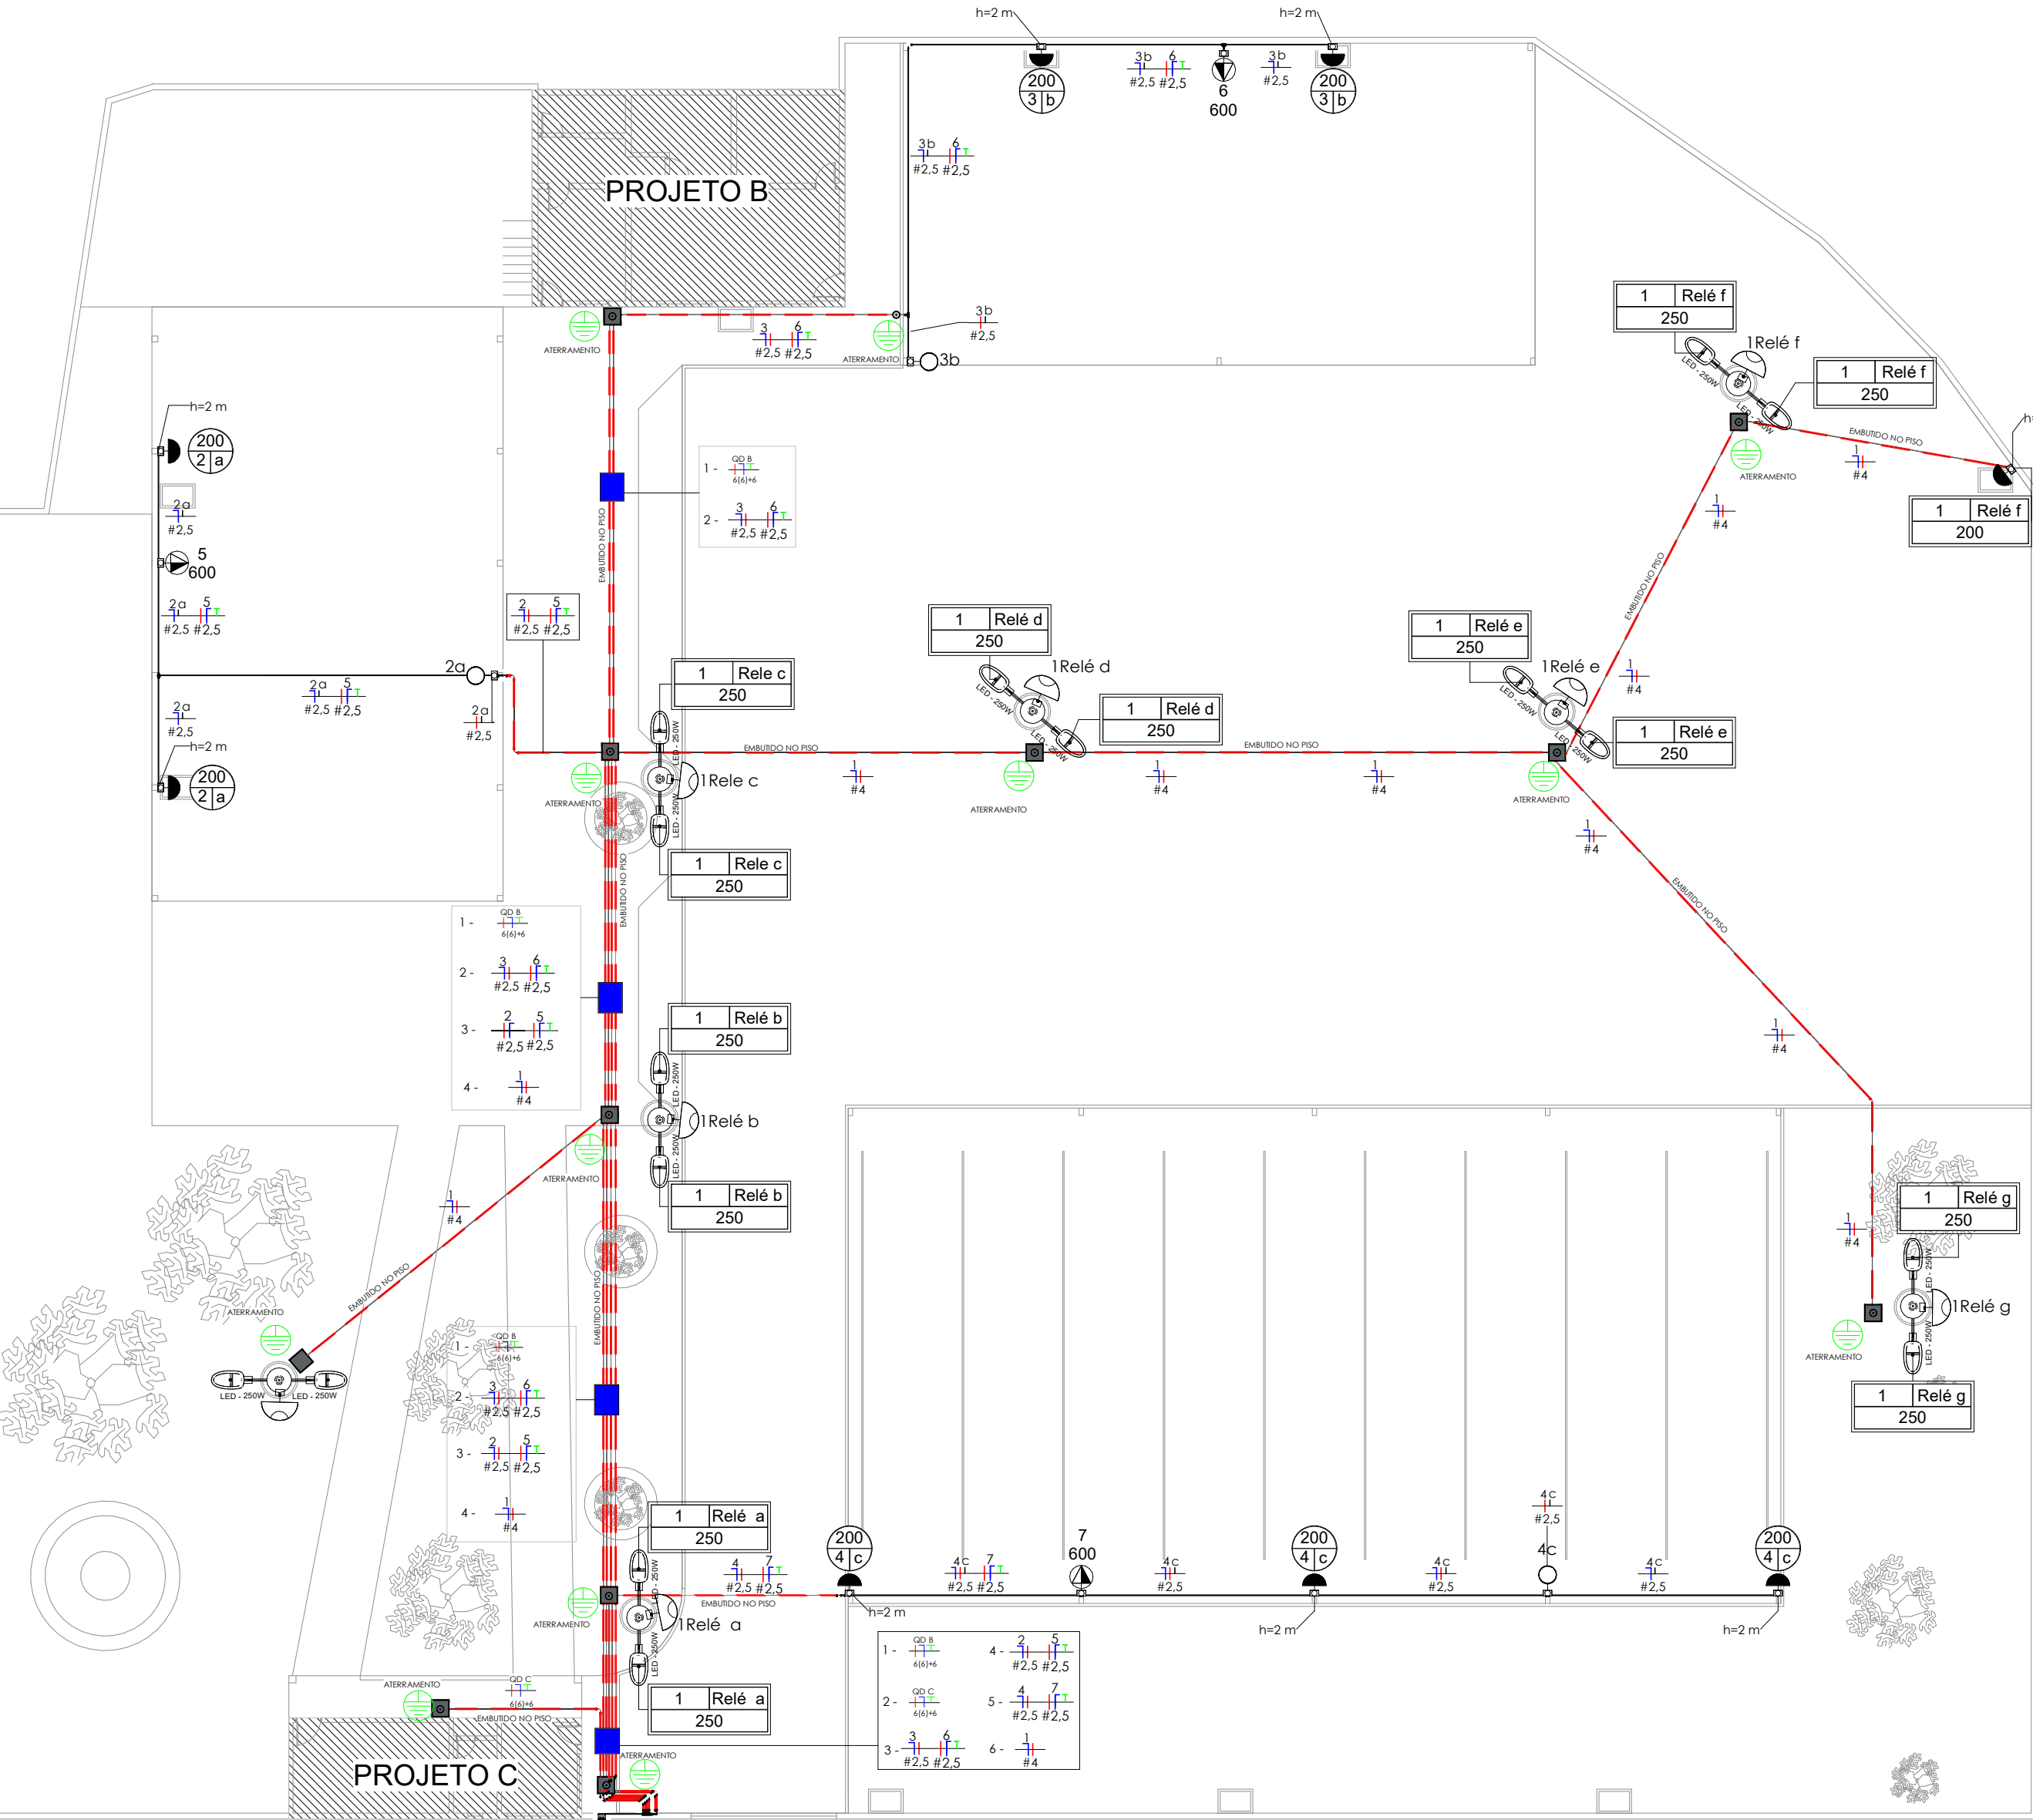

PLANTA BAIXA - PLANTA GERAL

ESCALA_____ 1 : 200

PROPRIETÁRIO:		PREFEITURA MUNICIPAL DE COREMAS - PB		
PROJETO:		LINCOLN CARTAXO DE LIRA JÚNIOR CREA 160.814.689-8		
PROJETO:		PROJETO A - ELÉTRICO GARAGEM COREMAS-PB		
PROPRIETÁRIO:		PREFEITURA MUNICIPAL DE COREMAS - PB		
		MUNICÍPIO DE COREMAS - PB		
LOCAL:		COREMAS-PB		
		RESPONSÁVEL TÉCNICO	RUBRICA	DADOS
DATA	JUN/2025	LINCOLN CARTAXO		CREA 160.814.689-8
CÓPIA				
VISTO				
PRANCHA:		DESCRIÇÃO:		ESCALA:
01 /04		PROJETO ELÉTRICO - PLANTA BAIXA		INDICADA



Av. Gov. Flavio R. Coutinho, 500, sl. 601
Jd. Oceania, 58037-005 - João Pessoa (PB)
Tel +55 99924.4447
e-mail: contato@lclprojetos.com