


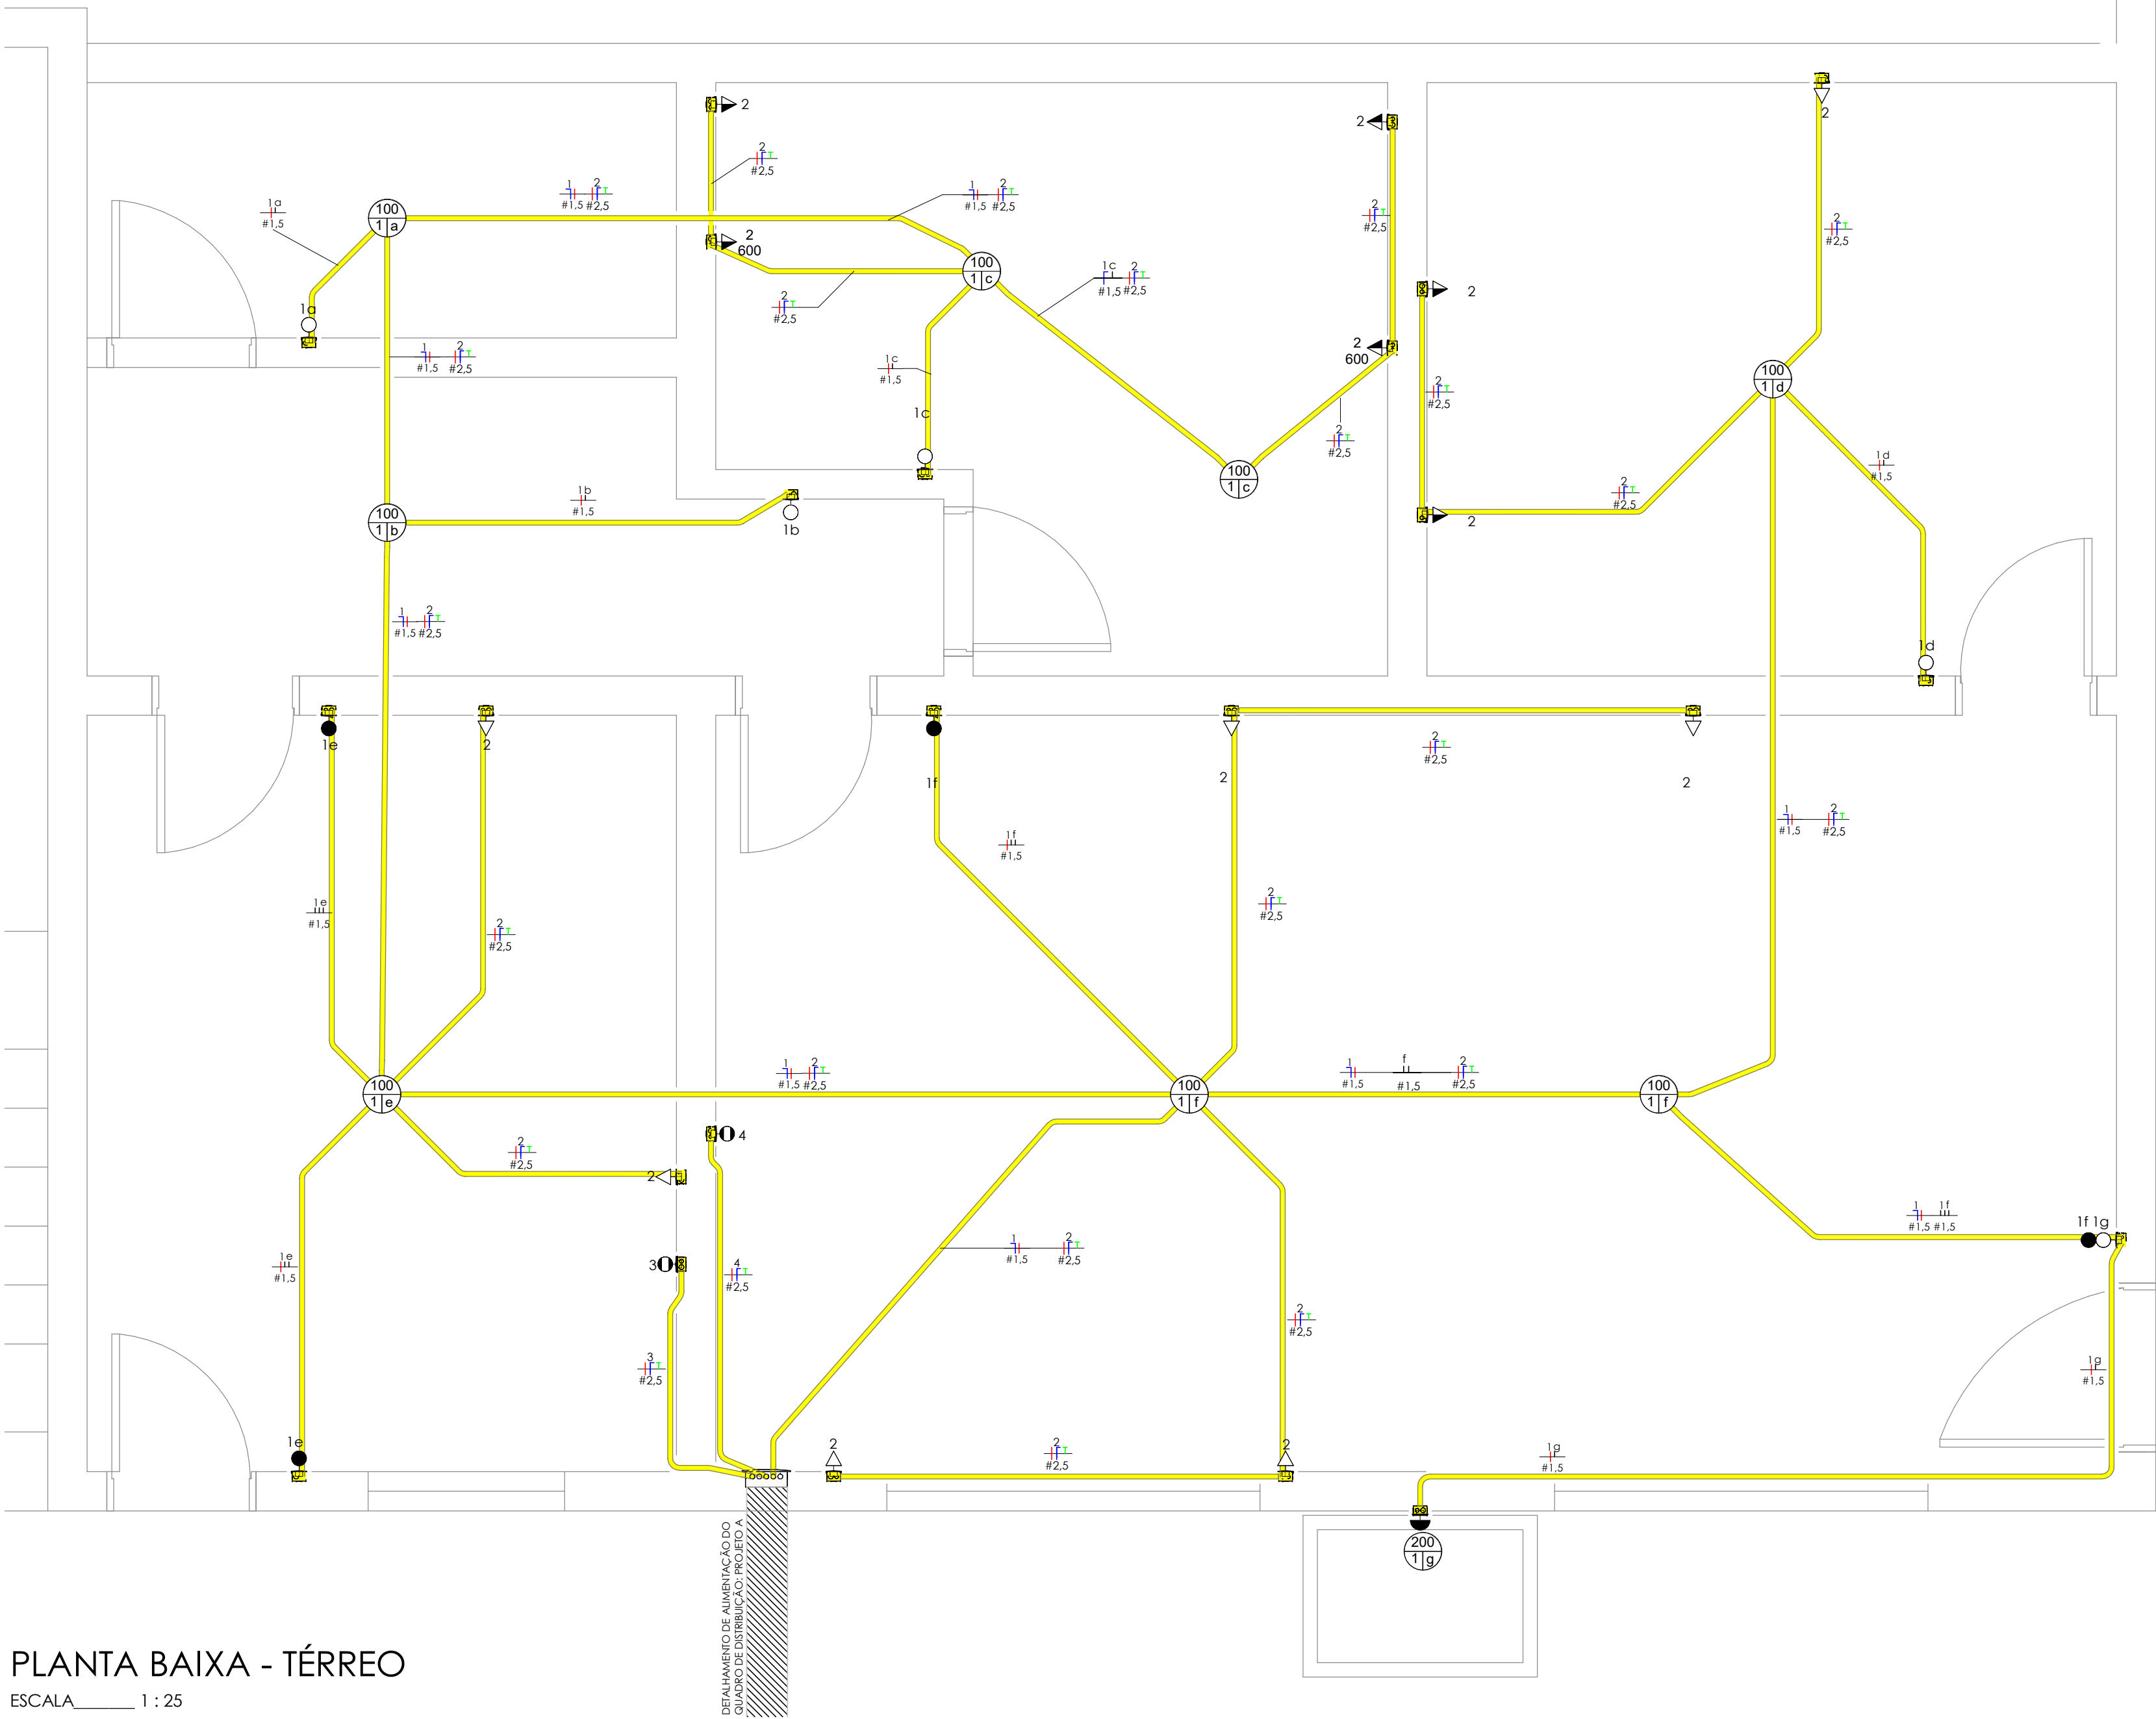

PLANTA BAIXA - TÉRREO
ESCALA_____ 1 : 25

Painel: QDC

Localização:

Alimentado por:

Montagem:

Notas:

Alimentação: 220V/380V Monofásico (F+N+T)

Circuito	Descrição	Tensão (V)	Esquema	Potência Total (VA)	FP	Potência Total (W)	Corrente Nominal (A)	FCA	FCT	Ib: Corrente de Projeto Corrigida (A)	In: Disjuntor (A)	Tipo de Instalação	Condutor Pré-Dimensionado (Seção e Iz: Capacidade de condução de Corrente)	Seção do Condutor Adotado (mm²)	L Aprox. (m)	L Considerado (m)	Queda de Tensão (%)	Potência
1	Iluminação	220,00	FNT	1000 VA	0,92	920 W	4,55 A	0,8	1	5,68 A	10,00 A	[Cu/PVC/750V/70"]-Un-B1-2Cc (Ilum.)	1-#1,5(17,5A), 1-#1,5(17,5A), 1-#1,5	1,5	13,53	15	0,84	1000 VA
2	Tomadas	220,00	FNT	2300 VA	0,92	2116 W	10,45 A	0,8	1	13,07 A	20,00 A	[Cu/PVC/750V/70"]-Un-B1-2Cc	1-#2,5(24A), 1-#2,5(24A), 1-#2,5	2,5	17,64	20	1,54	2300 VA
3	Ar-Condicionado 01	220,00	FNT	1370 VA	0,92	1260 W	6,23 A	1	1	6,23 A	10,00 A	[Cu/PVC/750V/70"]-Un-B1-2Cc	1-#2,5(24A), 1-#2,5(24A), 1-#2,5	2,5	4,37	10	0,46	1370 VA
4	Ar-Condicionado 02	220,00	FNT	1370 VA	0,92	1260 W	6,23 A	1	1	6,23 A	10,00 A	[Cu/PVC/750V/70"]-Un-B1-2Cc	1-#2,5(24A), 1-#2,5(24A), 1-#2,5	2,5	4,84	10	0,46	1370 VA
5																		
Totais:																		6039 VA

Legenda:

FP: Fator de Potência

FCA:Fator de Correção por Agrupamento

FCT:Fator de Correção por Temperatura

Ib: Corrente de Projeto Corrigida(A)

In:Corrente Nominal do Disjuntor (A)


Iz: Capacidade de condução de corrente do condutor(A)

Tipo de Carga	Potência Instalada (VA)	Fator de Demanda	Potência Demandada (VA)	Totais do Pannel
Iluminação+TUGs (Residencial)	3300 VA	0,40	1320 VA	
Ar Condicionado	2739 VA	0,88	2410 VA	
				Potência Instalada: 6039 VA
				Potência Demandada: 3730 VA
				Corrente Total: 27,45 A
				Corrente Total Demandada: 16,96 A

Notas:

GERAL - LISTA DE MATERIAIS - COMPONENTES		
Descrição do Material	Dimensões	Quantidade (peças)
Disjuntores e Proteções		
IDR Interruptor Diferencial Residual Bipolar In=40A, 30mA	In=40 A, 30mA	1
Mini Disjuntor Monopolar 10A Curva C, conforme ABNT NBR NM 60898, encaixe perfil DIN 35mm	C 10A	3
Mini Disjuntor Monopolar 20A Curva C, conforme ABNT NBR NM 60898, encaixe perfil DIN 35mm	C 20A	1
Interruptores		
Conjunto montado com 1 Interruptor paralelo, 10A 250V~, 4"x2"	1P, 4"x2"	3
Conjunto montado com 1 Interruptor simples, 10A 250V~, 4"x2"	1S, 4"x2"	4
Conjunto montado de Interruptor com 1 tecla simples e 1 tecla paralelo, 4"x2"	1S+1P, 4"x2"	1
Ponto de Ar Condicionado		
Ponto em caixa 4x2	Ponto de Ar Condicionado	2
Quadros		
Quadro de Distribuição 6/8 Disjuntores, de embutir, fabricado em PVC antichamas, com barramento de terra e neutro, porta branca, dimensões 245x190x78,7mm.	6/8 Disjuntores	1
Tomadas		
Conjunto montado de 1 Tomada 2P+T, 10A, posto horizontal, 4"x2"	10A, 4"x2"	13

QUANTITATIVO DE CABOS EM METROS (Cobre/Un/Iso. PVC/750V/70°C)					
(F- Condutor Fase), (N - Condutor Neutro), (T - Condutor Terra), (Re - Condutor de Retorno)					
Sugestão de Cores para os condutores- F: Vermelho, N: Azul Claro, PE: Verde, Re - Branco					
F-1,5mm²	F-2,5mm²	N-1,5mm²	N-2,5mm²	T-2,5mm²	R -1,5mm²
59,9	78,7	32,3	78,7	78,7	73
					Tipo de Condutor
					CABO COBRE PVC 70°C 450/750V

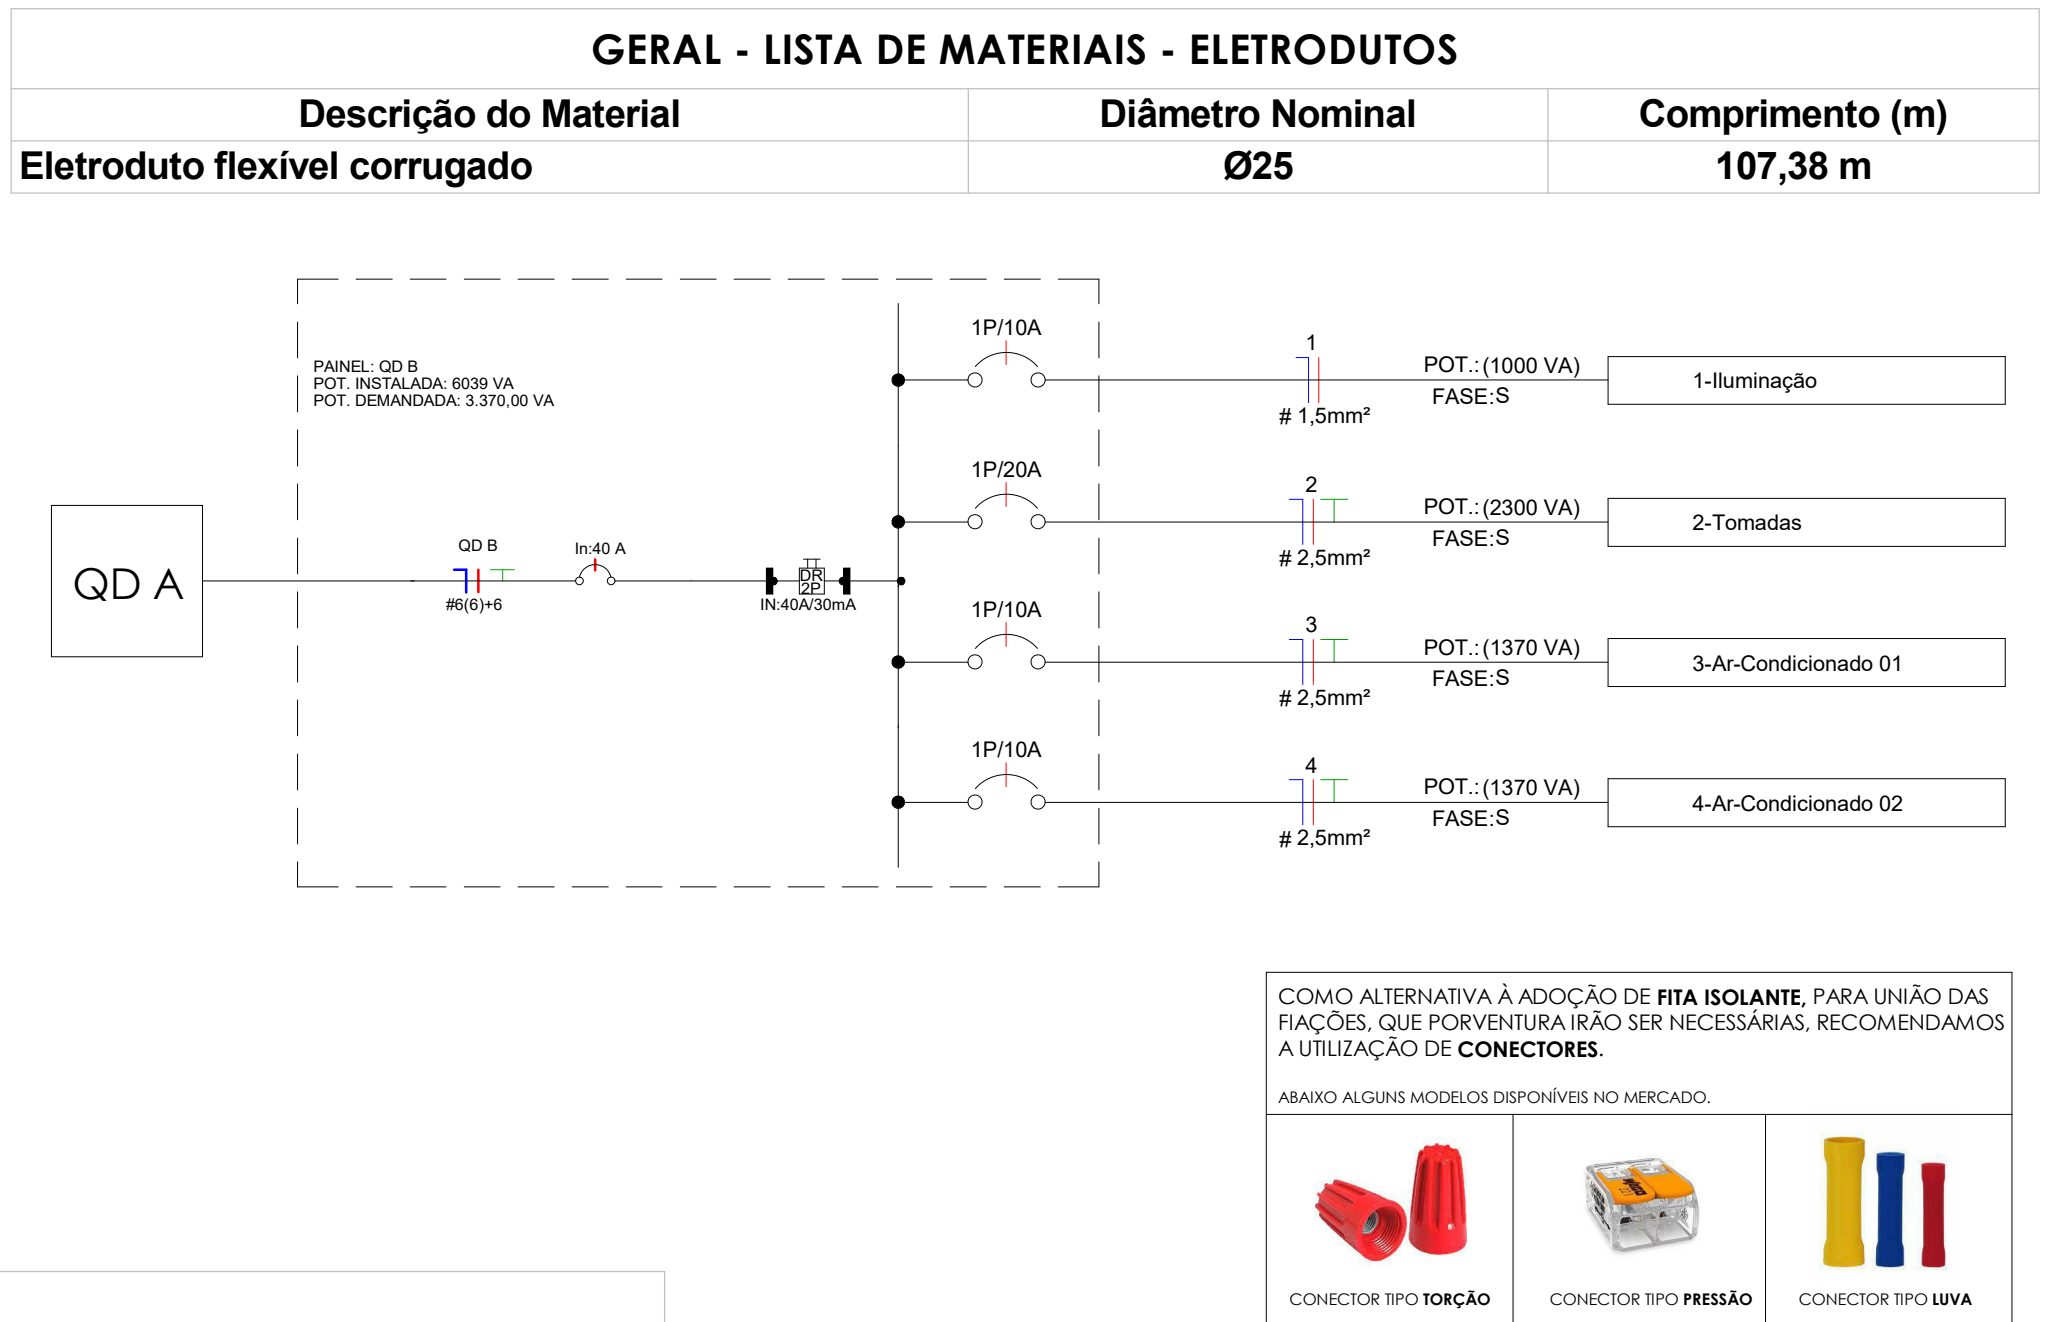

LINCOLN CARTAXO DE LIRA JUNIOR:06897861405

Assinado de forma digital por LINCOLN CARTAXO DE LIRA JUNIOR:06897861405
Dados: 2025.06.16 10:35:07 -03'00'

PROPRIETÁRIO:		PREFEITURA MUNICIPAL DE COREMAS-PB	
PROJETO:		LINCOLN CARTAXO DE LIRA JÚNIOR CREA 160.814.689-8	
PROJETO:		PROJETO B - ELÉTRICO GARAGEM COREMAS-PB	
CONCEDENTE:		PREFEITURA MUNICIPAL DE COREMAS - PB	
CONVENIENTE:		MUNICÍPIO DE COREMAS - PB	
LOCAL:		COREMAS-PB	
DESENHO	DATA	RESPONSÁVEL TÉCNICO	RUBRICA
CÓPIA	JUN/2025	LINCOLN CARTAXO	DADOS
VISTO			CREA 160.814.689-8
PRANCHA:		DESCRIÇÃO:	
03/04		PROJETO ELÉTRICO - PLANTA BAIXA - QUANTITATIVOS -DETALHAMENTOS	
		ESCALA:	
		INDICADA	



Av. Gov. Flavio R. Coutinho, 500, sl. 601
Jd. Oceania, 58037-005 - João Pessoa (PB)
Tel +55 99924.4447
e-mail: contato@lclprojetos.com