




VS100
ESC 1:50

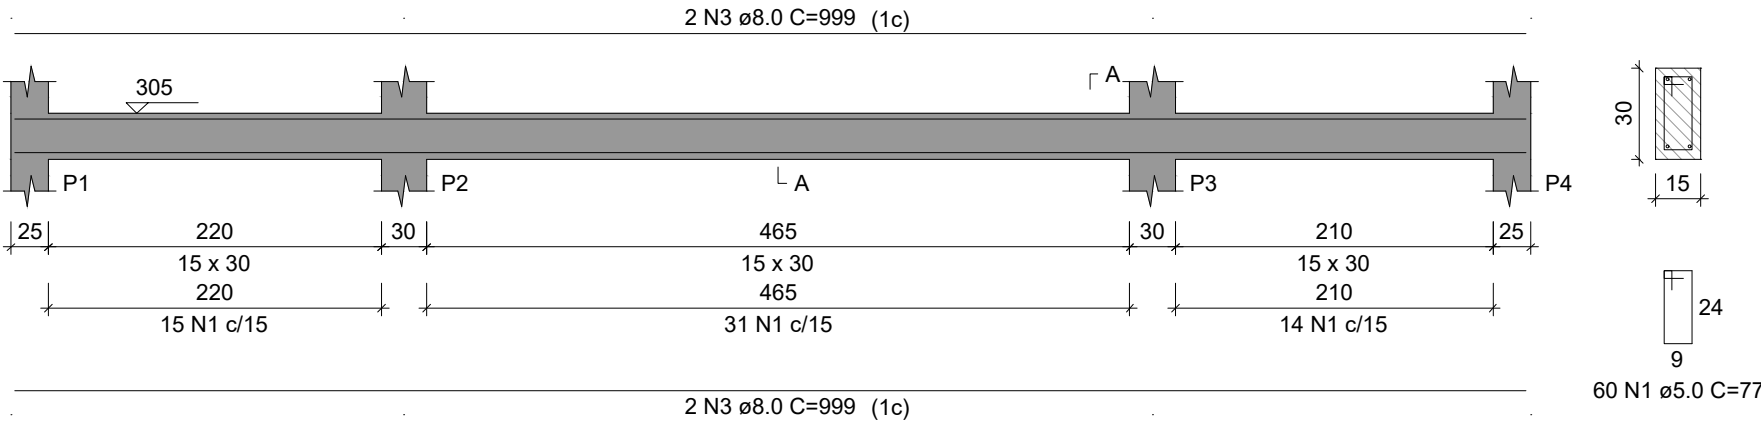


SEÇÃO A-A
ESC 1:25

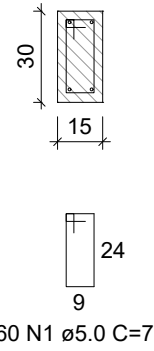


VS101
ESC 1:50

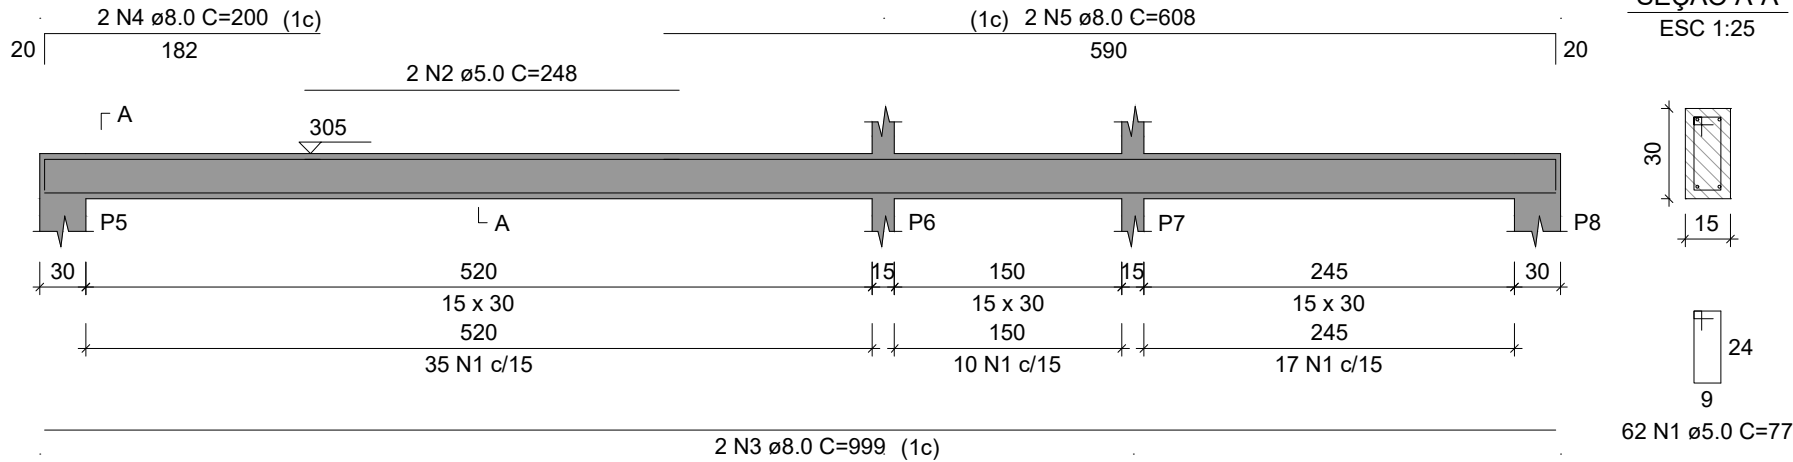


SEÇÃO A-A
ESC 1:25

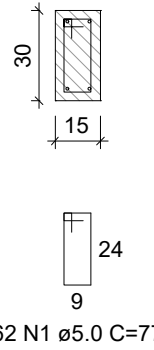


VS102
ESC 1:50

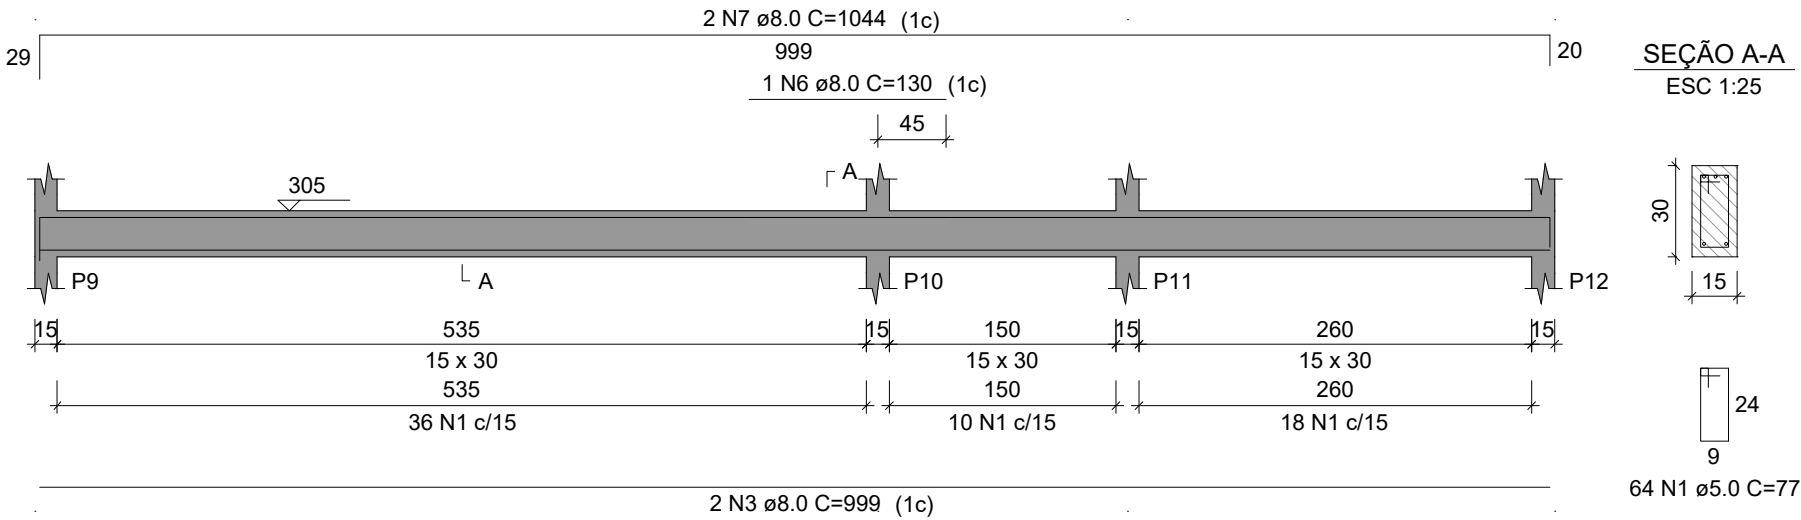


SEÇÃO A-A
ESC 1:25

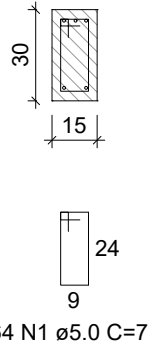

VS103
ESC 1:50

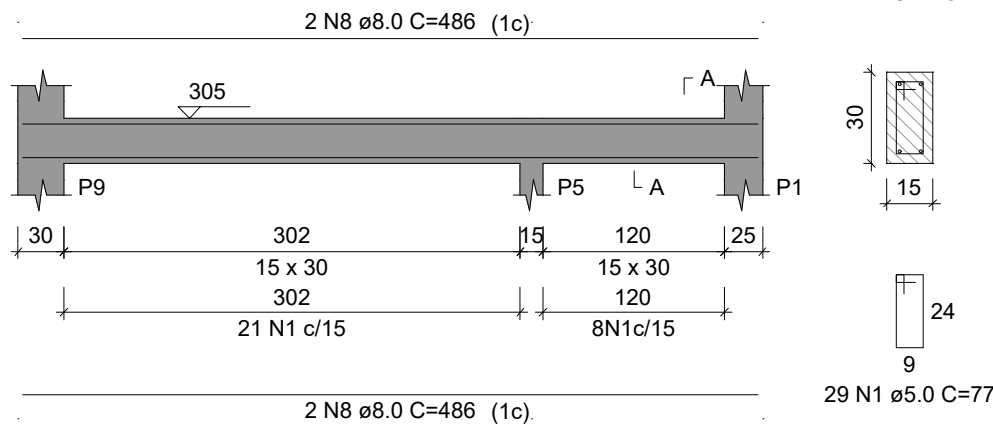

SEÇÃO A-A
ESC 1:25

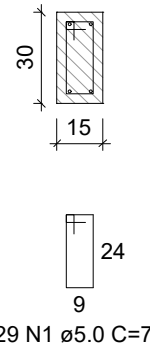

RELAÇÃO DO AÇO

VS100 VS101 VS102
VS103 VS104


AÇO	N	DIAM (mm)	QUANT	C.UNIT (cm)	C.TOTAL (cm)
CA60	1	5.0	244	77	18788
	2	5.0	2	248	496
CA50	3	8.0	8	999	7992
	4	8.0	2	200	400
	5	8.0	2	608	1216
	6	8.0	1	130	130
	7	8.0	2	1044	2088
	8	8.0	8	486	3888

RESUMO DO AÇO


AÇO	DIAM (mm)	C.TOTAL (m)	PESO + 10% (kg)
CA50	8.0	157.1	68.2
CA60	5.0	192.8	32.7
PESO TOTAL (kg)			
CA50	68.2		
CA60	32.7		

Volume de concreto (C-25) = 1.80 m³
Área de forma = 29.99 m²

VS104
ESC 1:50

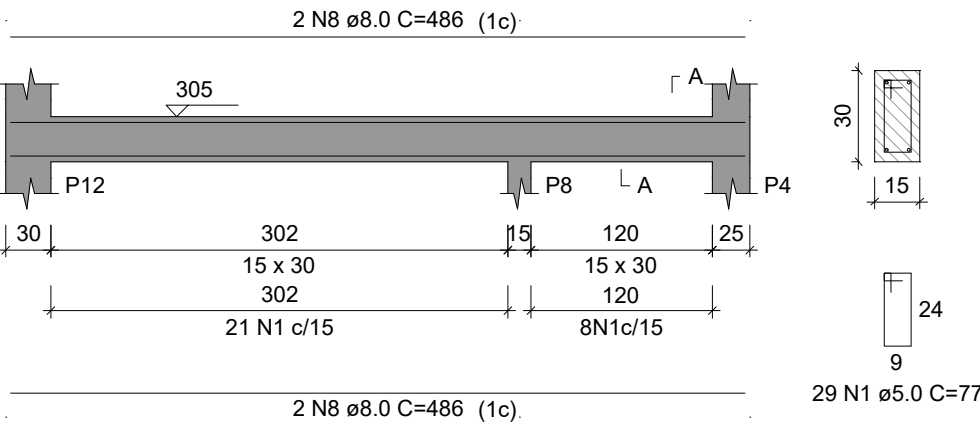

SEÇÃO A-A
ESC 1:25

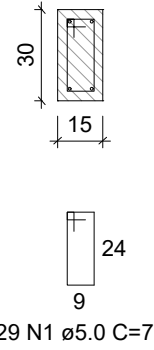

PROPRIETÁRIO: PREFEITURA MUNICIPAL DE COREMAS- PB

LINCOLN CARTAXO DE LIRA JÚNIOR:06897861405
Assinado de forma digital por LINCOLN CARTAXO DE LIRA JÚNIOR:06897861405
Dados: 2025.07.14 11:27:36 -03'00'

PROJETO: LINCOLN CARTAXO DE LIRA JÚNIOR CREA 160.814.689-8

FOLHA PROJETO: GARAGEM COREMAS (ESTRUTURAL ANEXO I)

CONVENENTE: PREFEITURA MUNICIPAL DE COREMAS-PB

CONCENDENTE: PREFEITURA MUNICIPAL DE COREMAS-PB

LOCALIDADE: COREMAS- PB

	DATA	RESPONSÁVEL	RUBRICA	DADOS
DESENHO	JUN/2025	LINCOLN CARTAXO		
CÓPIA				
VISTO				

ESCALAS	DESENHOS	CONVÊNIO
INDICADO	- VIGAS (Nv. +305)	ARQUIVO

Aprovações: