



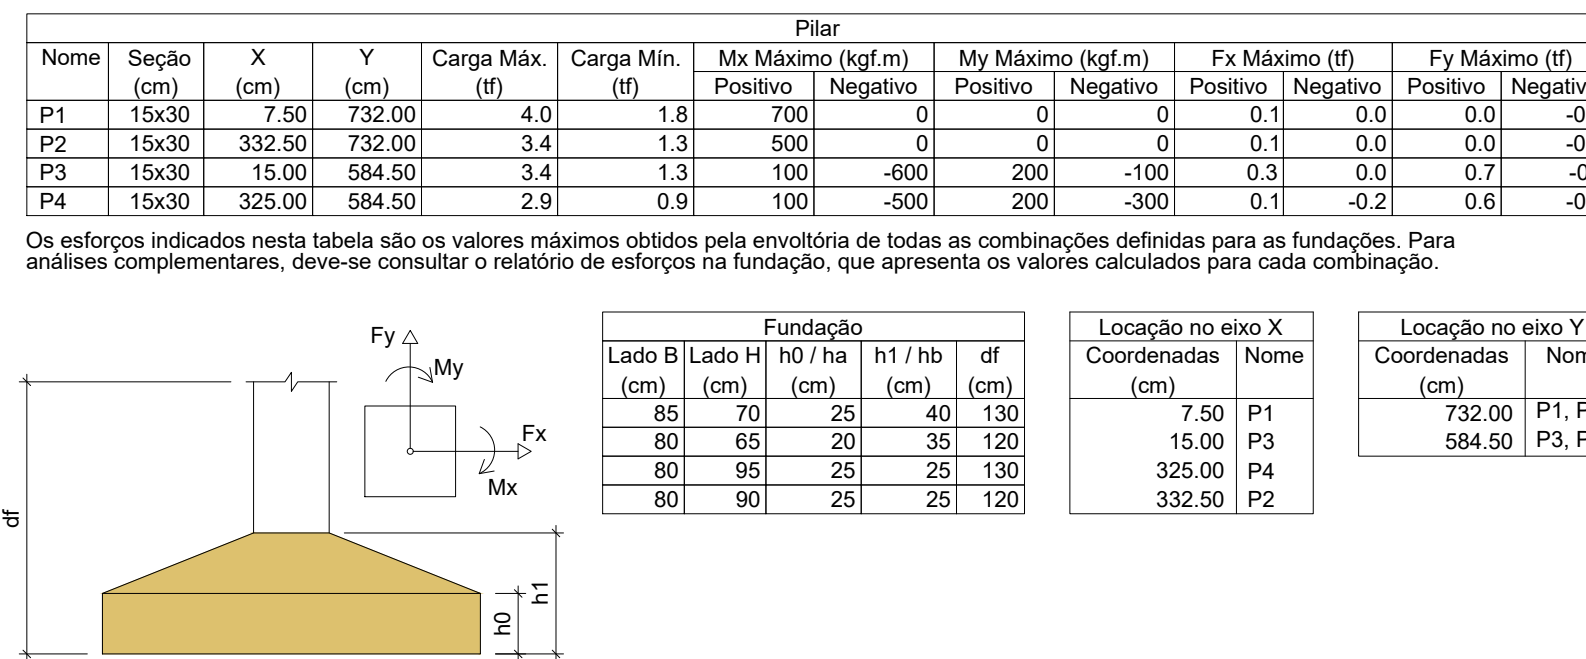


Planta de locação

escala 1:50

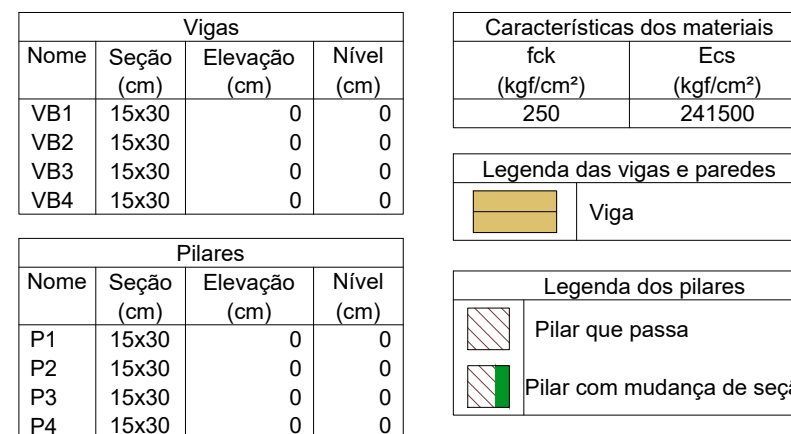

Forma do pavimento +0 (Nível 0)
escala 1:50

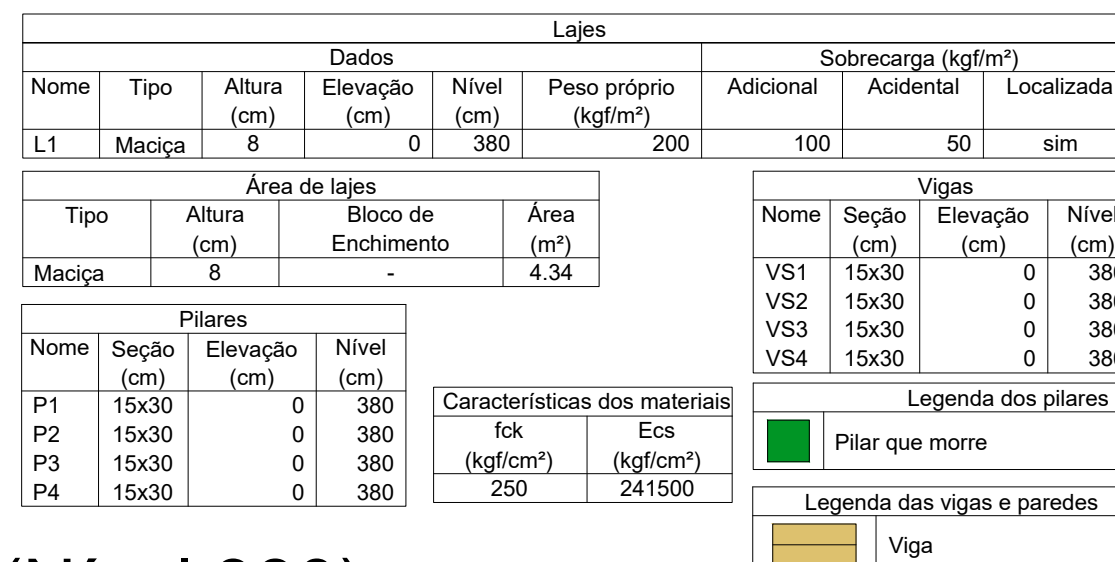

Forma do pavimento +380 (Nível 380)
escala 1:50

