




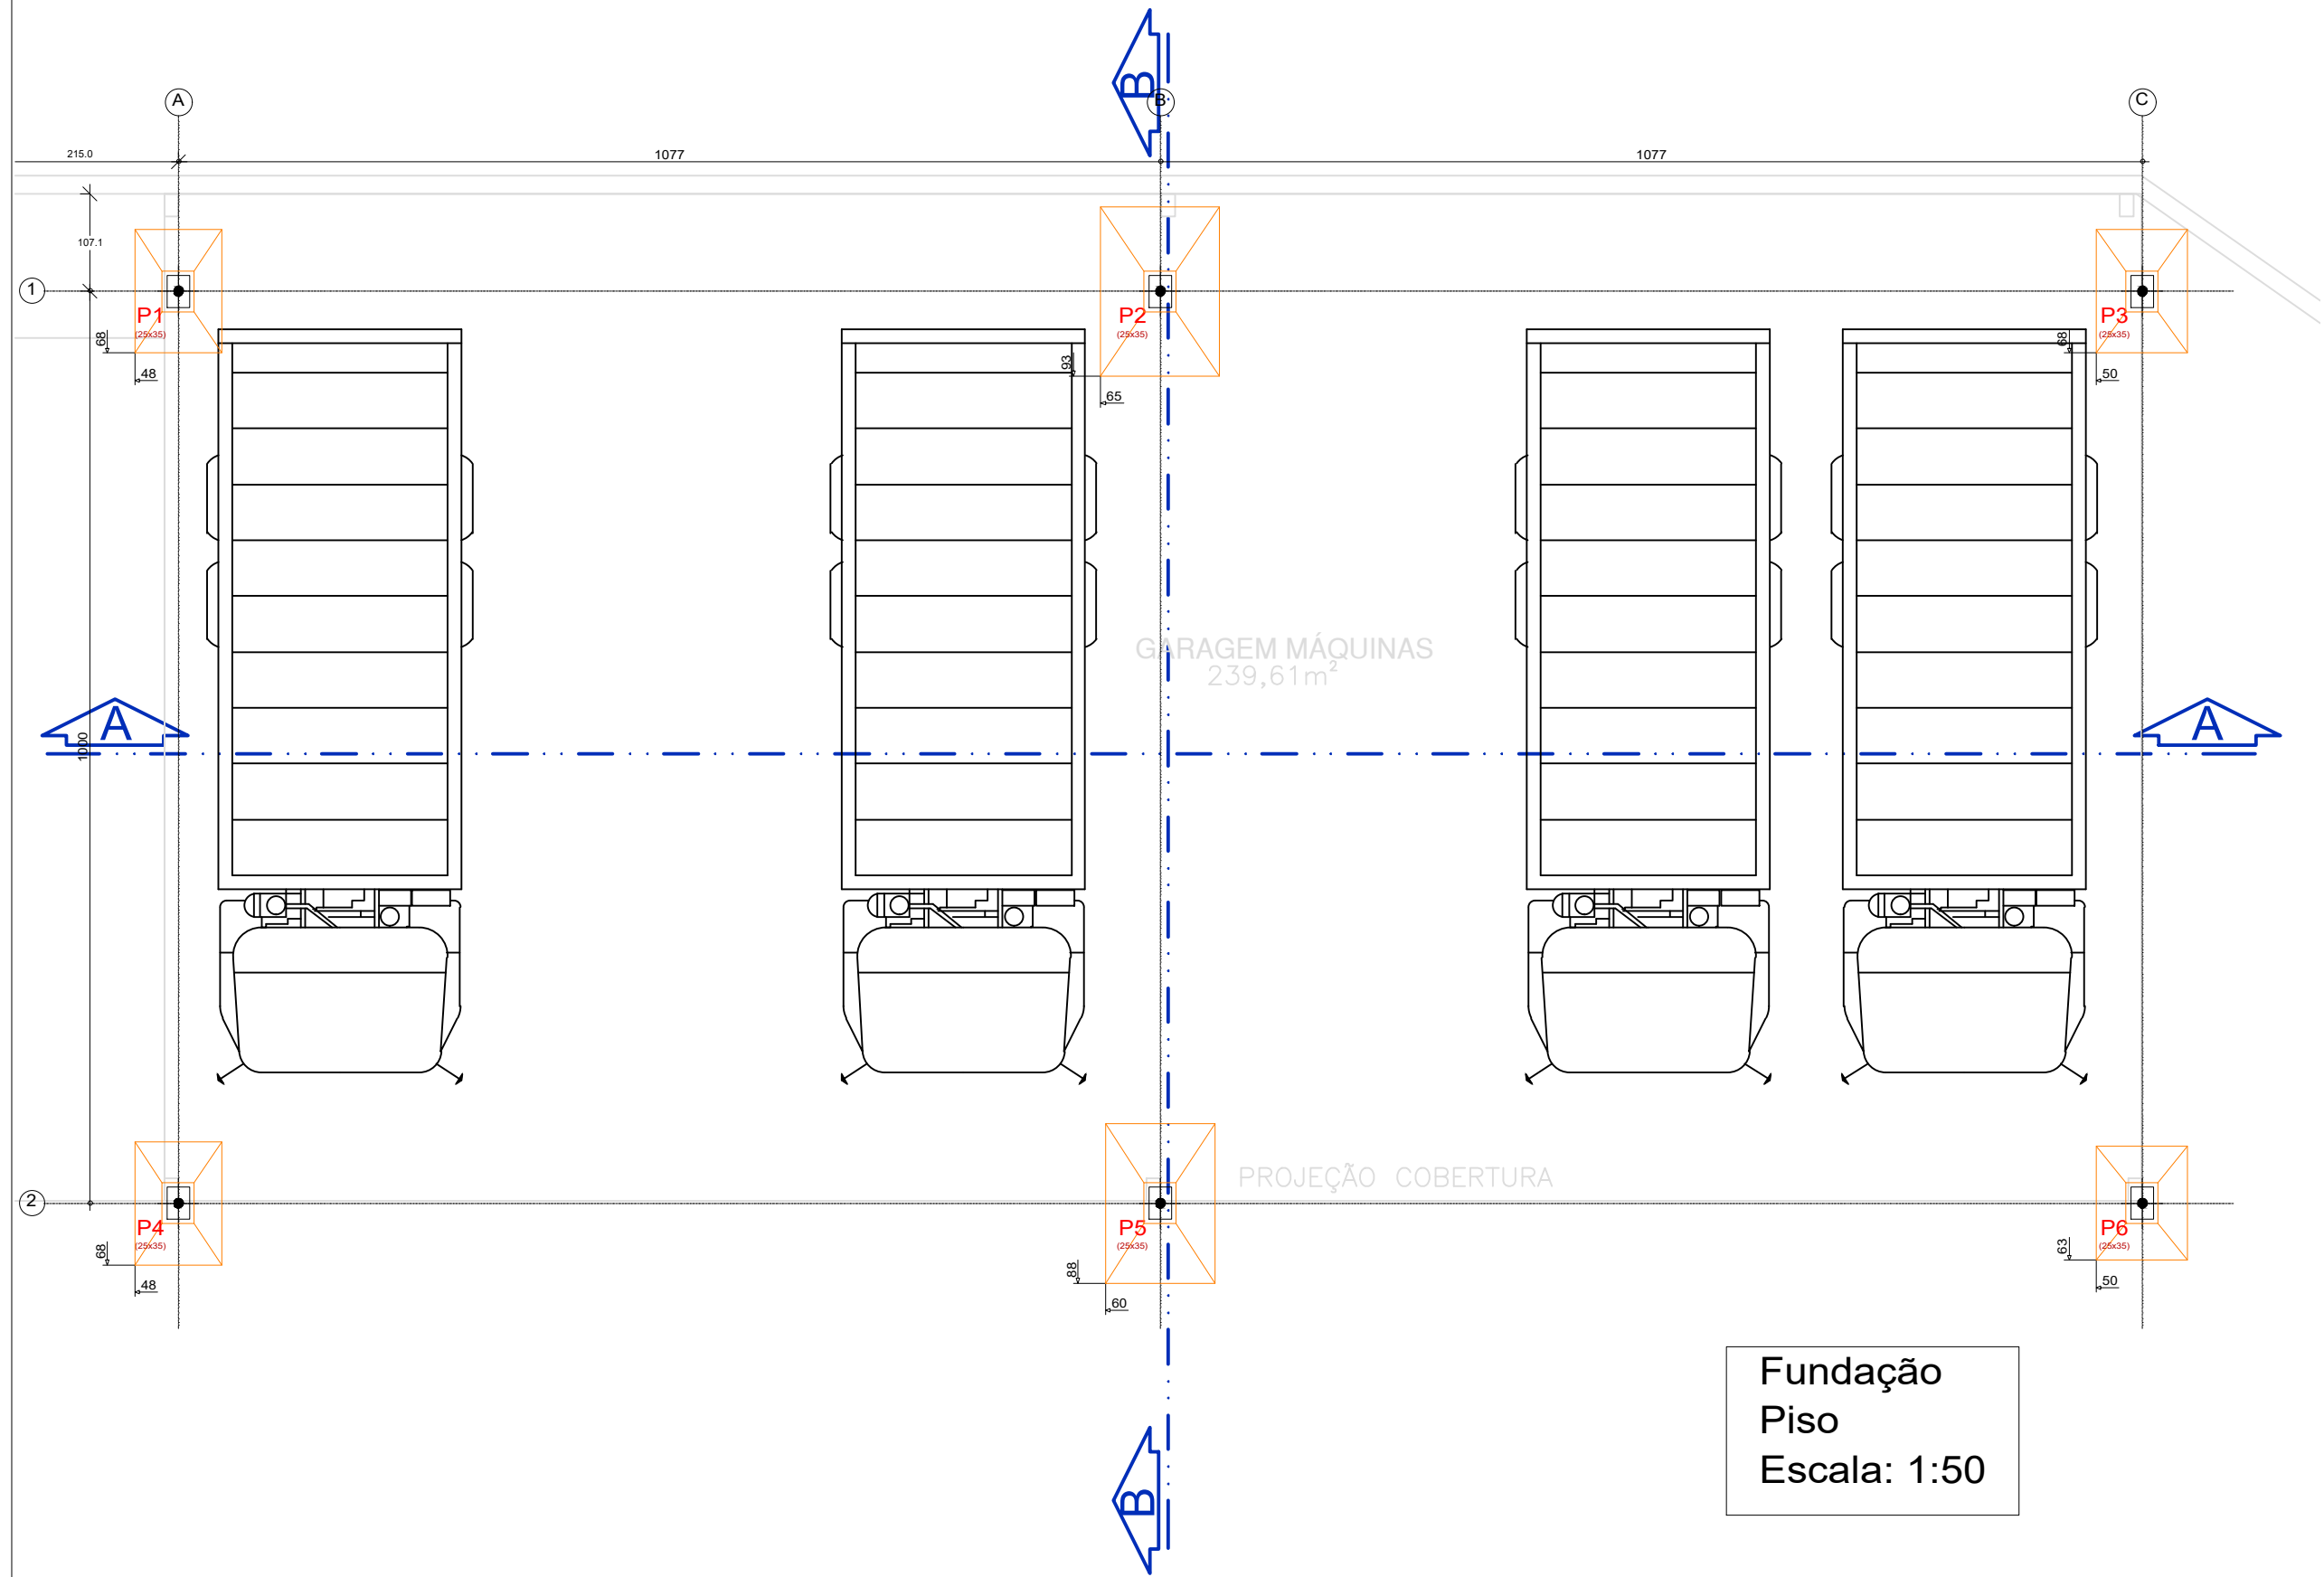


S1 e S4

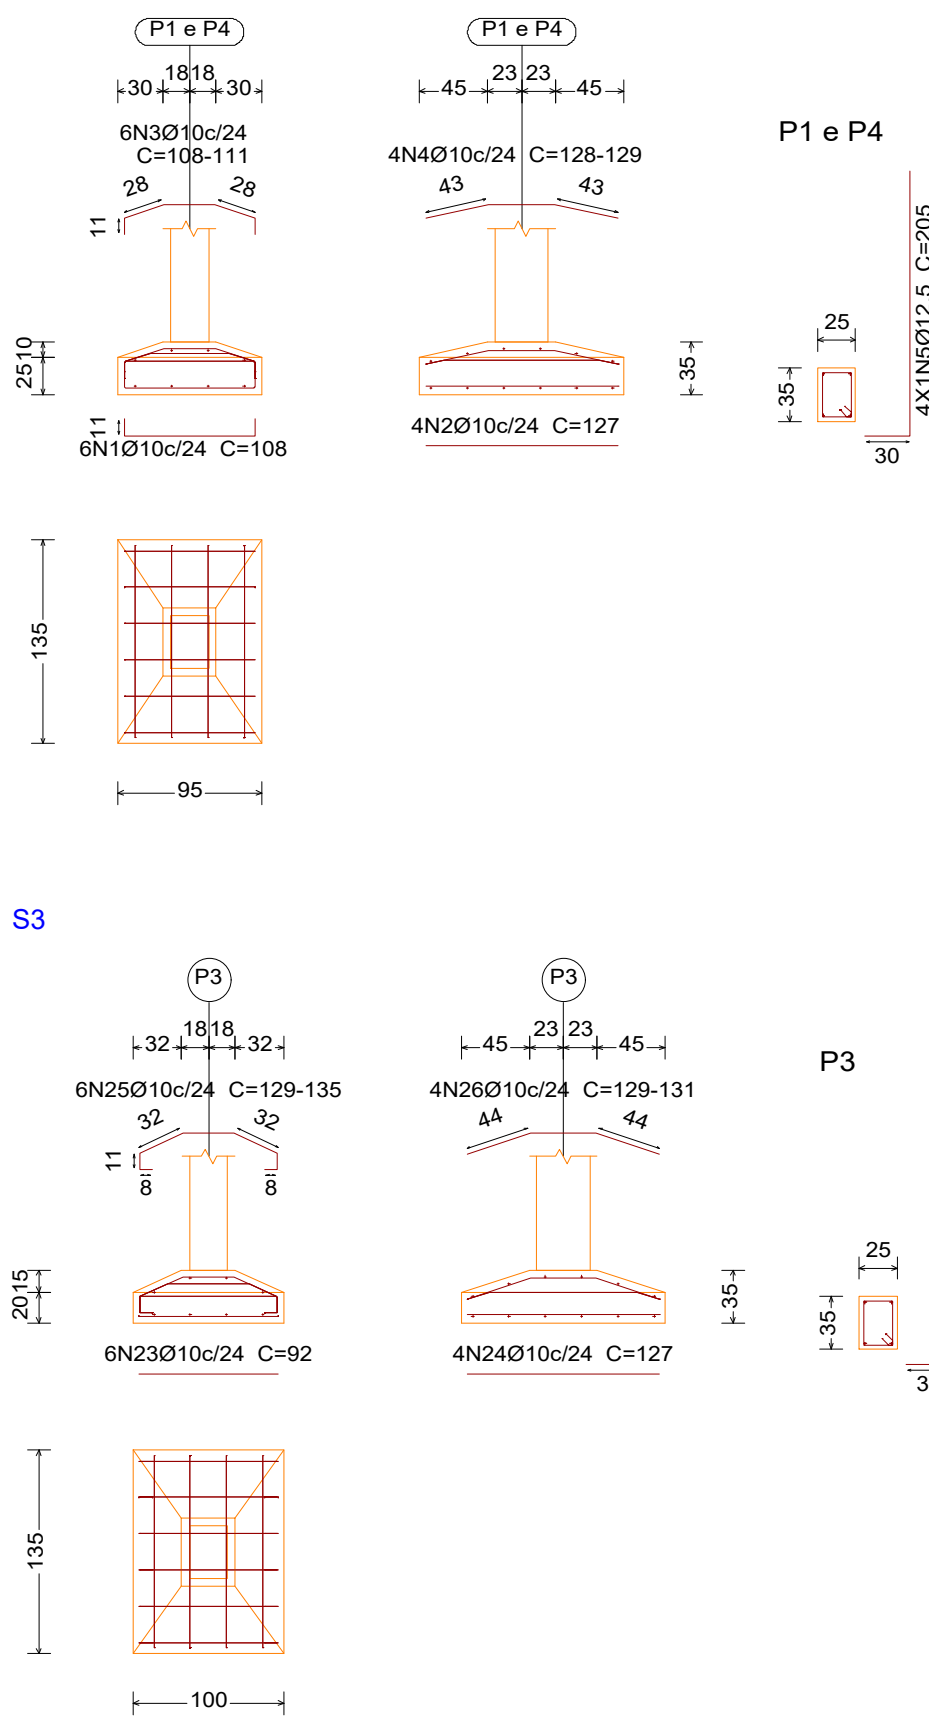


S2

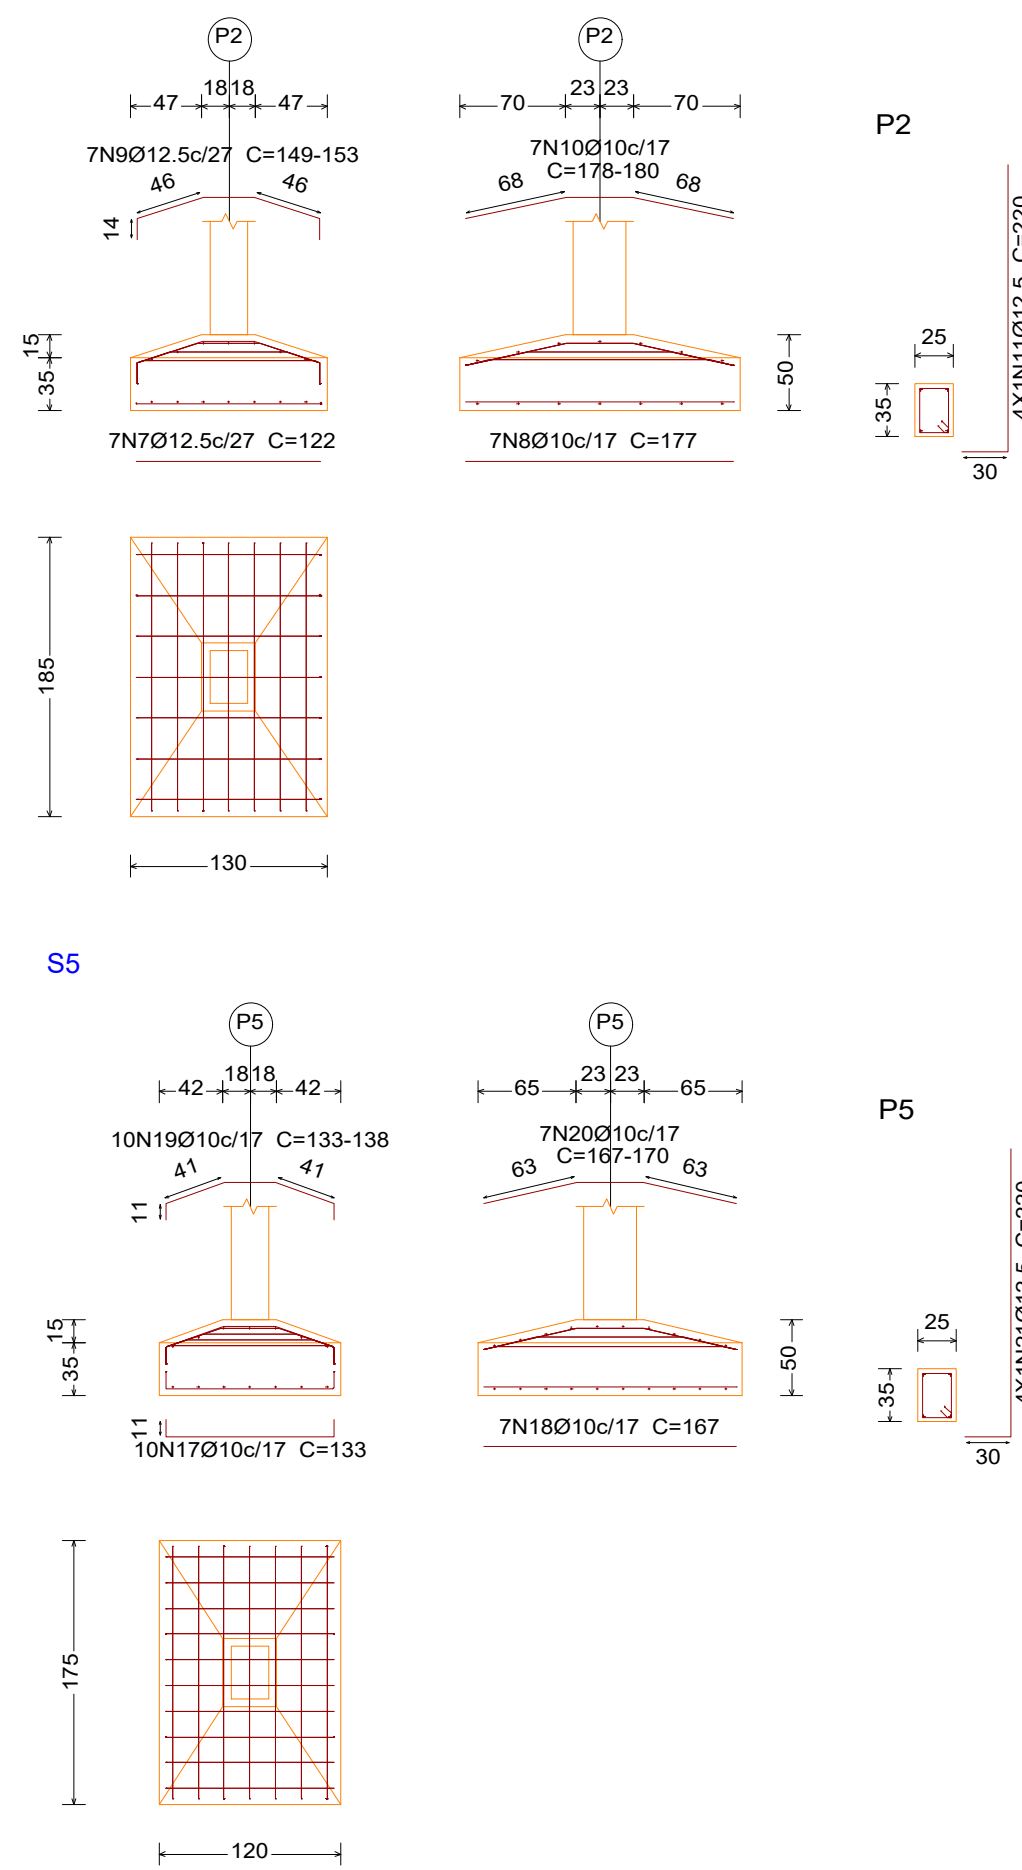


S3

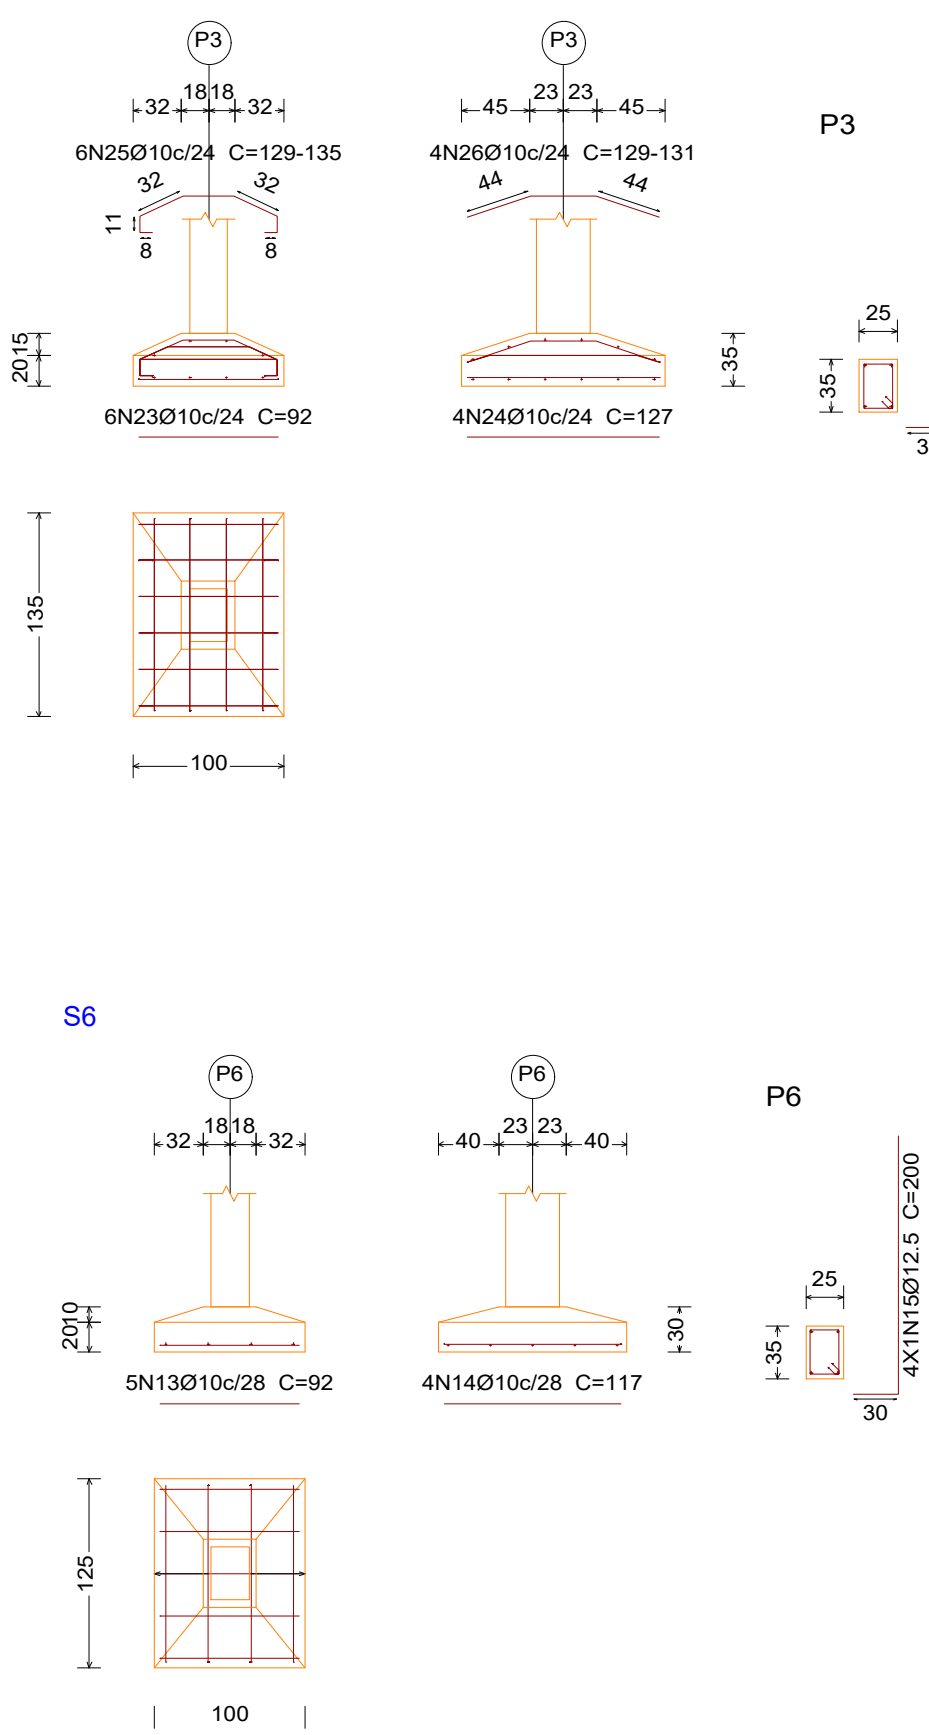





S5

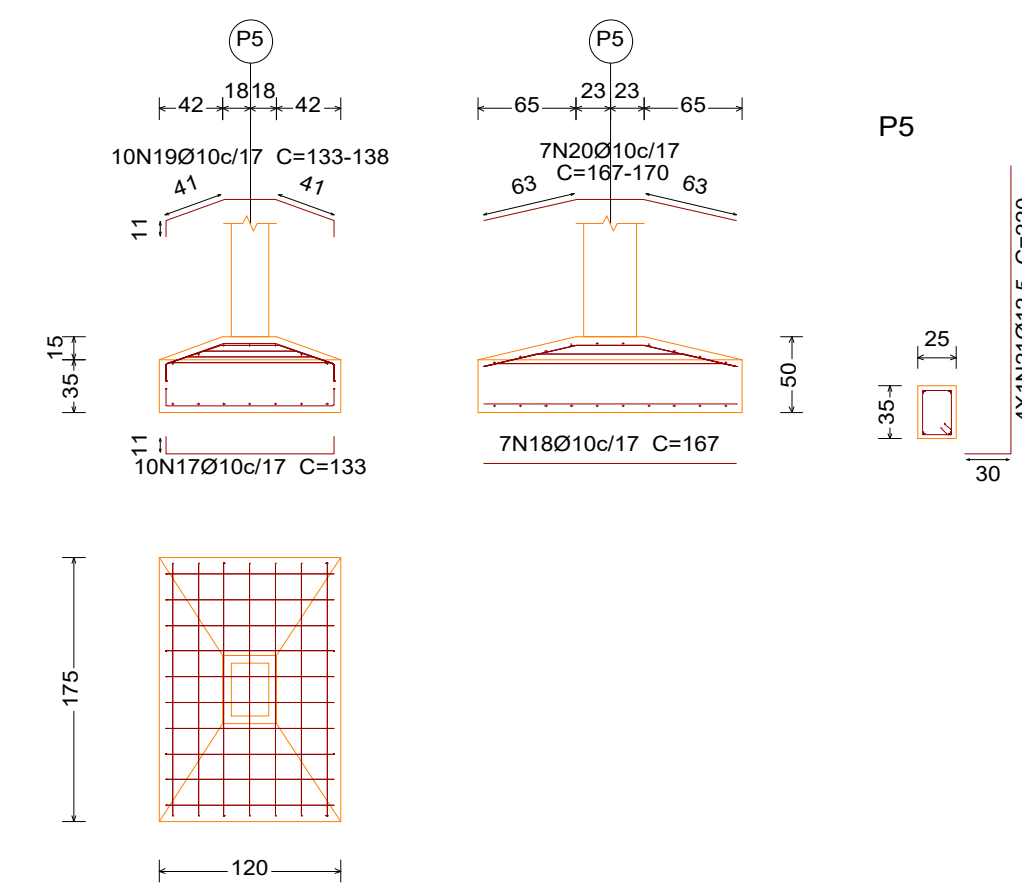

S6

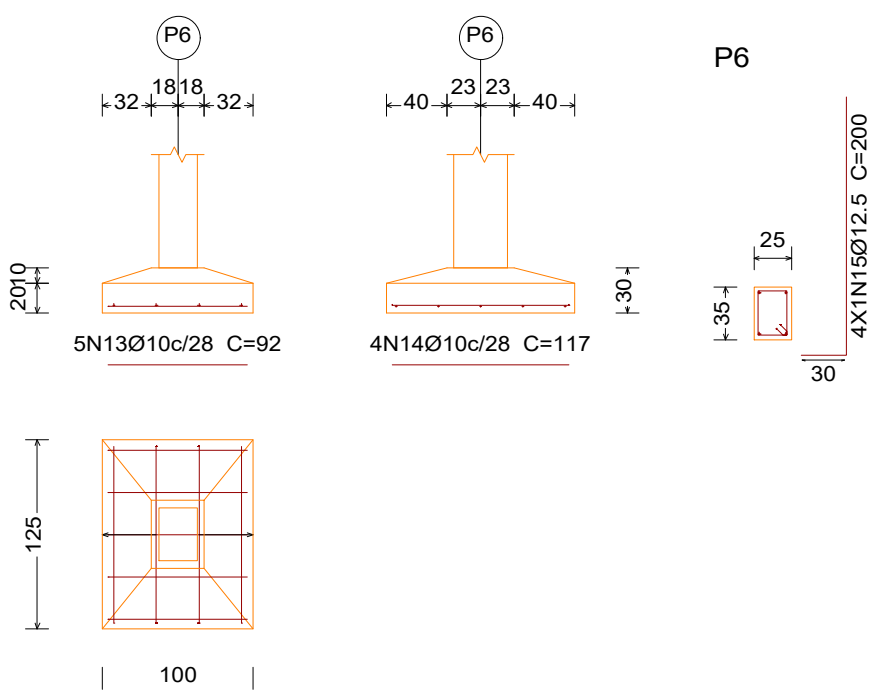


FUNDAÇÕES FORAM
DIMENSIONADAS PARA SOLO
COM TENSÃO ADMISSÍVEL
MAIOR OU IGUAL A 1.5 kgf/cm²

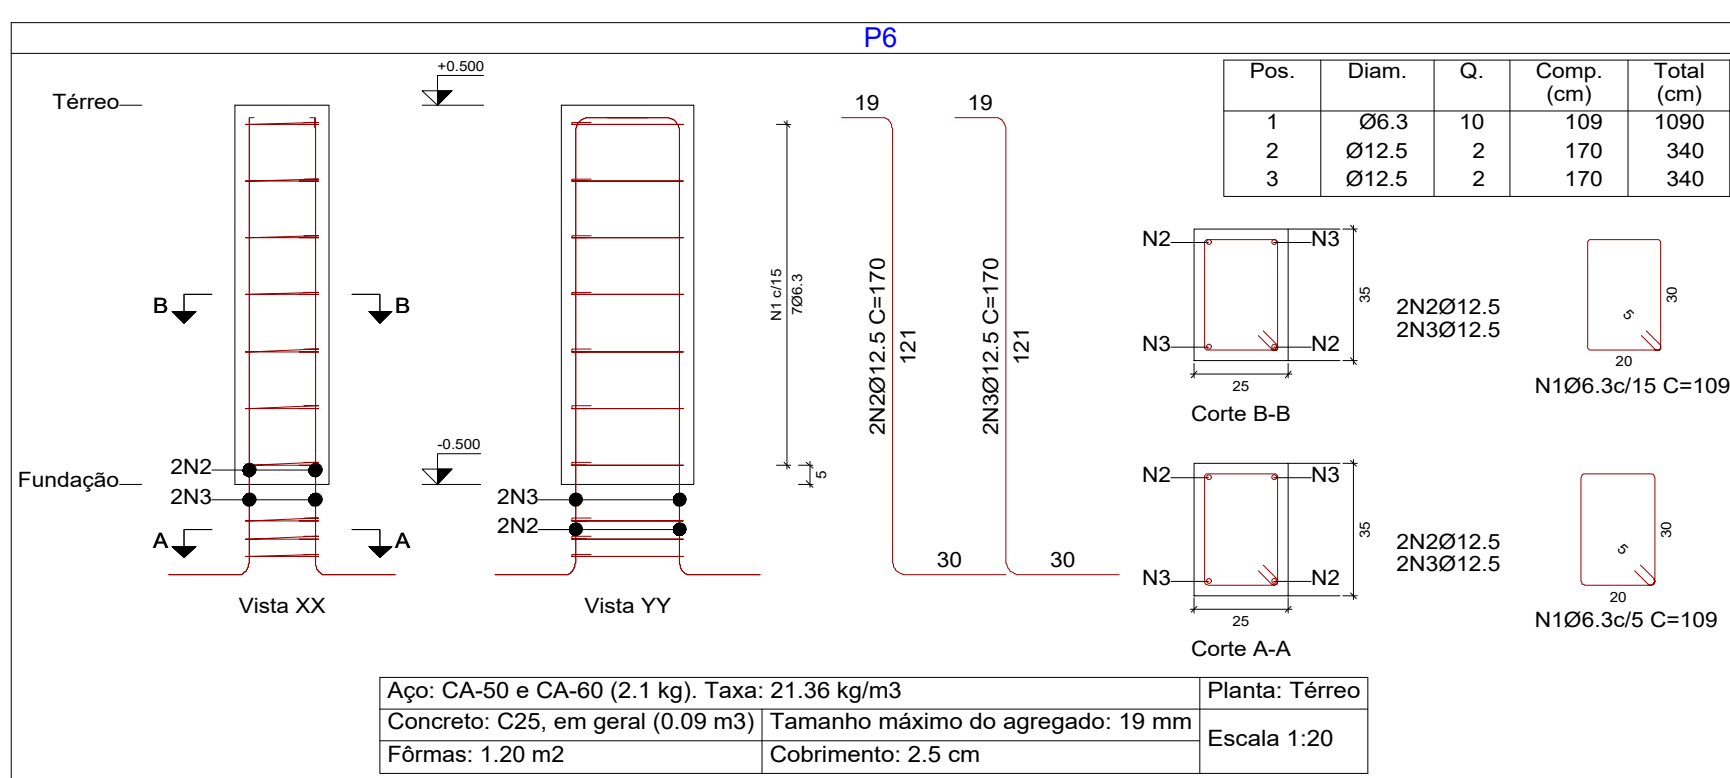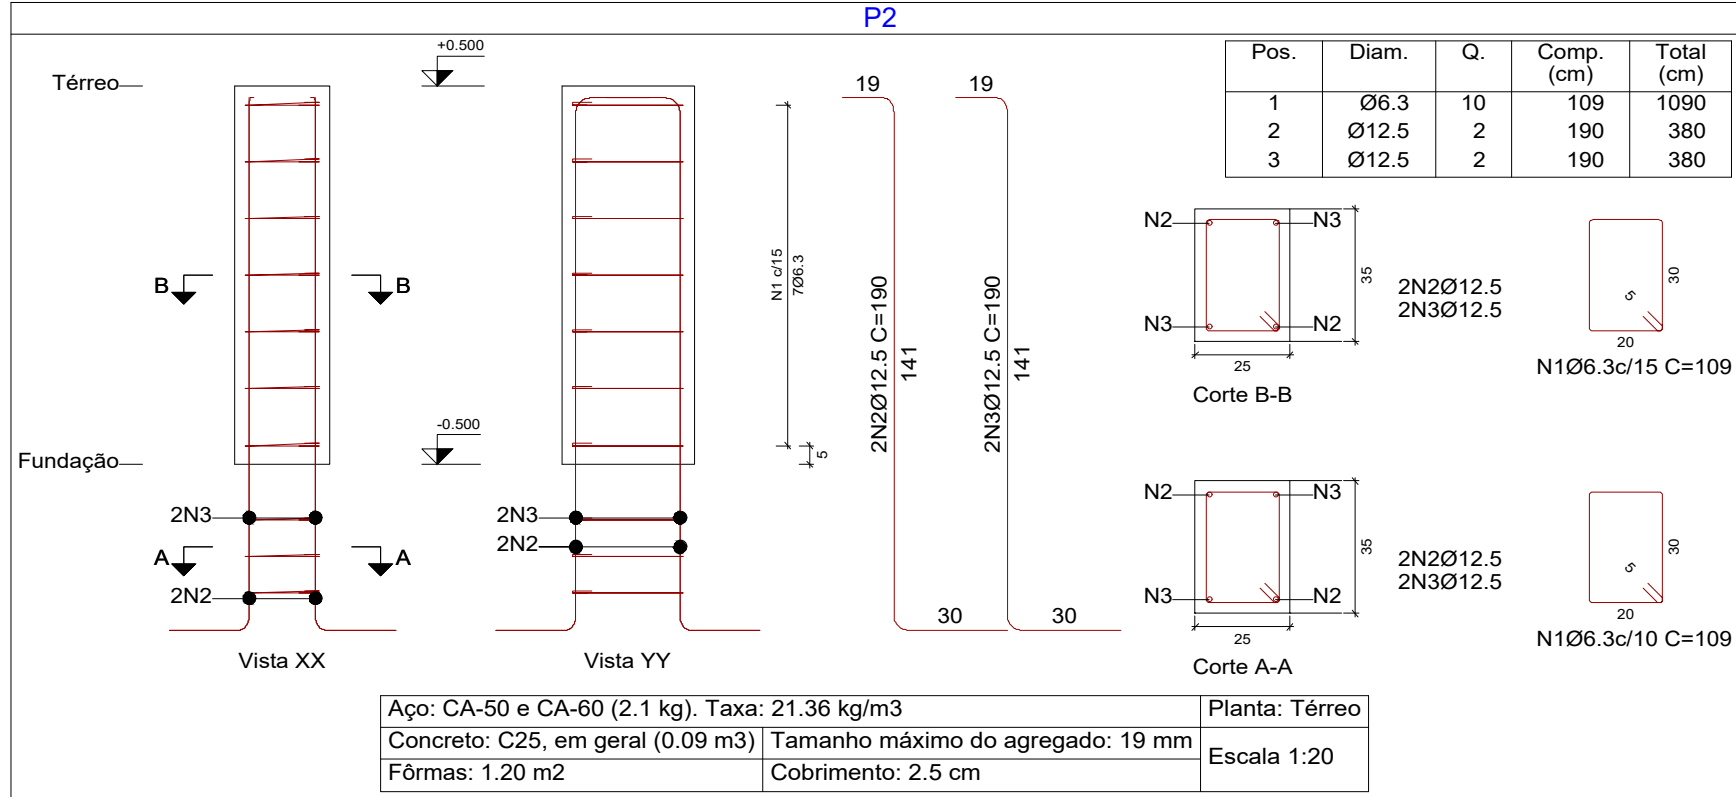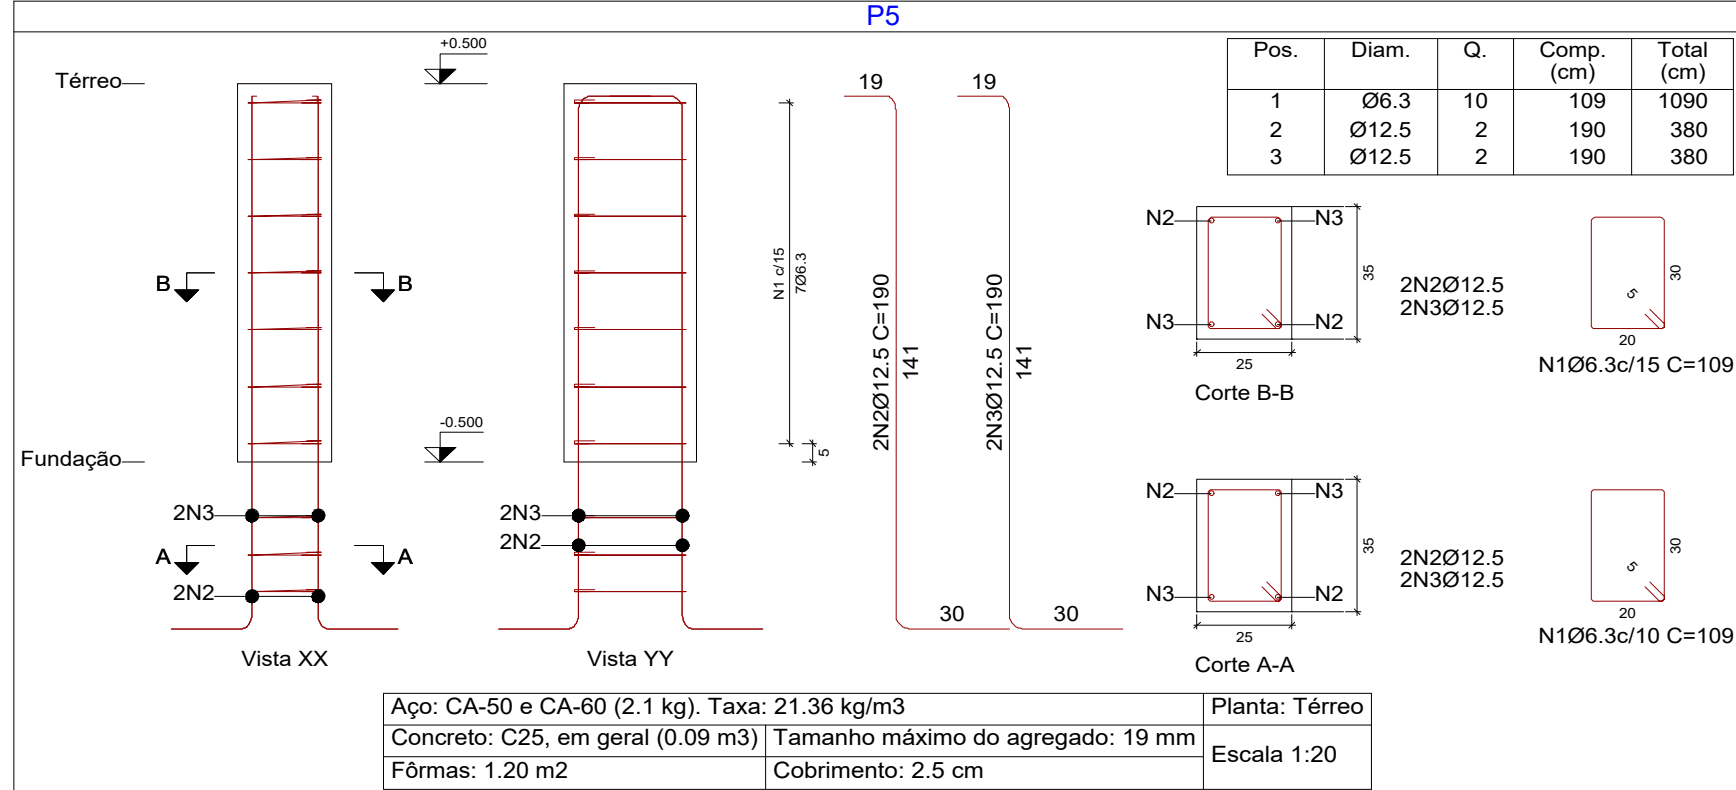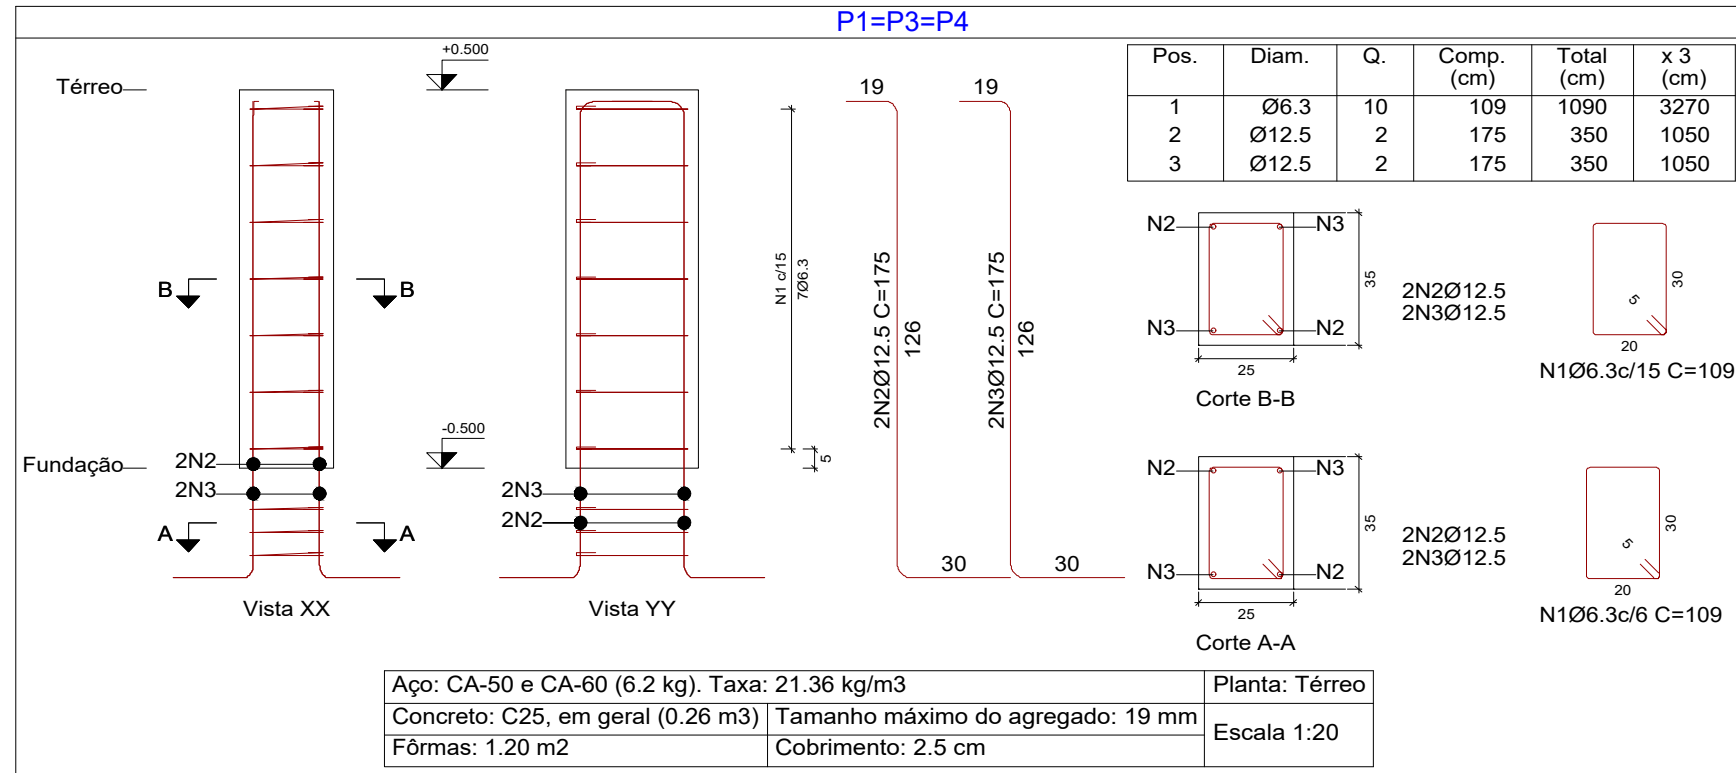

Elemento	Pos.	Diam.	Q.	Esquema (cm)	Comp. (cm)	Total (cm)	CA-50 (kg)	CA-60 (kg)
P1=P3=P4	1	Ø6.3	10		109	1090	2.7	
	2	Ø12.5	2	Consultar o desenho	175	350	3.4	
	3	Ø12.5	2	Consultar o desenho	175	350	3.4	
Total+10%:					10.5 (x3):	31.5		
P5	1	Ø6.3	10		109	1090	2.7	
	2	Ø12.5	2	Consultar o desenho	190	380	3.7	
	3	Ø12.5	2	Consultar o desenho	190	380	3.7	
Total+10%:					11.1			
P6	1	Ø6.3	10		109	1090	2.7	
	2	Ø12.5	2	Consultar o desenho	170	340	3.3	
	3	Ø12.5	2	Consultar o desenho	170	340	3.3	
Total+10%:					10.2			
P2	1	Ø6.3	10		109	1090	2.7	
	2	Ø12.5	2	Consultar o desenho	190	380	3.7	
	3	Ø12.5	2	Consultar o desenho	190	380	3.7	
Total+10%:					11.1			
							Ø6.3:	18.0 0.0
							Ø12.5:	45.9 0.0
							Total:	63.9 0.0

Elemento	Pos.	Diam.	Q.	Dob. (cm)	Reta (cm)	Dob. (cm)	Comp. (cm)	Total (cm)	CA-50 (kg)	CA-60 (kg)
S1=S4	1	Ø10	6	11	95	11	108	648	4.0	
	2	Ø10	4		127		508	3.1		
	3	Ø10	6		VAR.		VAR.	660	4.1	
	4	Ø10	4		VAR.		VAR.	516	3.2	
	5	Ø12.5	4	30	175		205	820	7.9	
	6	Ø6.3	3		110		330	0.8		
Total+10%:									25.4	
(x2):									50.8	
S2	7	Ø12.5	7		122		122	854	8.2	
	8	Ø10	7		VAR.		VAR.	1239	7.6	
	9	Ø12.5	7		VAR.		VAR.	1064	10.2	
	10	Ø10	7		VAR.		VAR.	1260	7.8	
	11	Ø12.5	4	30	190		220	880	8.5	
	12	Ø6.3	3		110		110	330	0.8	
Total+10%:									47.4	
S6	13	Ø10	5		92		92	460	2.8	
	14	Ø10	4		117		117	468	2.9	
	15	Ø12.5	4	30	170		200	800	7.7	
	16	Ø6.3	3		110		110	330	0.8	
Total+10%:									15.6	
(x2):									31.2	
S5	17	Ø10	10	11	111	11	133	1330	8.2	
	18	Ø10	7		167		167	1169	7.2	
	19	Ø10	10		VAR.		VAR.	1360	8.4	
	20	Ø10	7		VAR.		VAR.	1183	7.3	
	21	Ø12.5	4	30	190		220	880	8.5	
	22	Ø6.3	3		110		110	330	0.8	
Total+10%:									44.4	
(x2):									88.8	
S3	23	Ø10	6		92		92	552	3.4	
	24	Ø10	4		127		127	508	3.1	
	25	Ø10	6		VAR.		VAR.	798	4.9	
	26	Ø10	4		VAR.		VAR.	520	3.2	
	27	Ø12.5	4	30	174		204	816	7.9	
	28	Ø6.3	3		110		110	330	0.8	
Total+10%:									25.6	
(x2):									51.2	0.0
									Ø10:	105.1 0.0
									Ø12.5:	73.5 0.0
									Total:	183.8 0.0

Resumo Aço	Comp. total (m)	Peso+10% (kg)	Total
Fundação			
CA-50	Ø6.3	19.8	5
	Ø10	155.1	105
	Ø12.5	69.3	73
			183

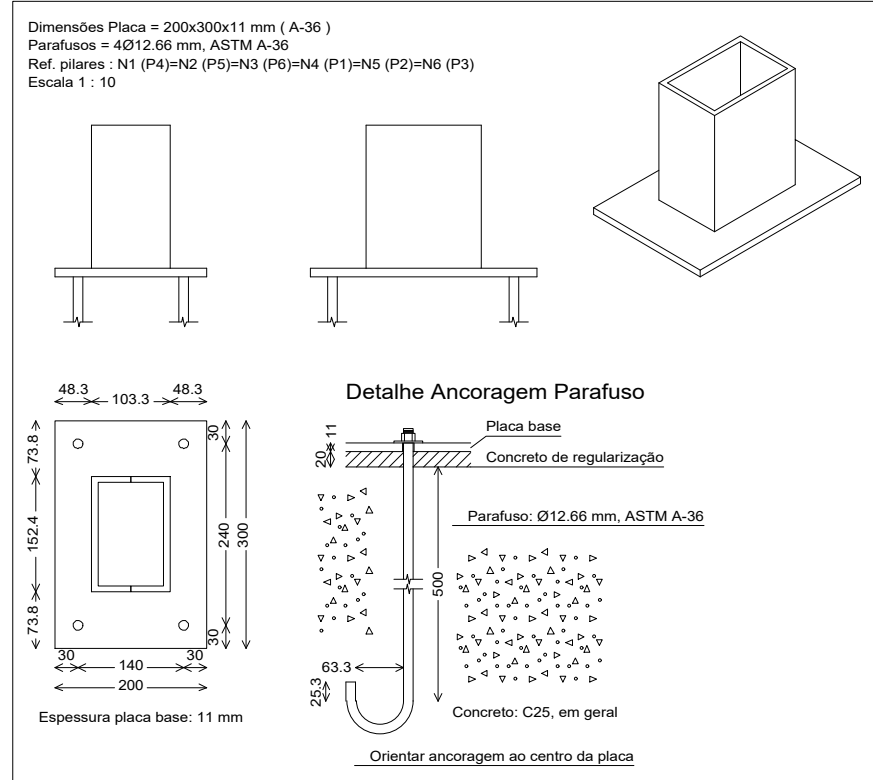

PROPRIETÁRIO: PREFEITURA MUNICIPAL DE COREMAS - PB

PROJETO: LINCOLN CARTAXO DE LIRA JÚNIOR CREA 160.814.689-8

CONSTRUÇÃO: PROJETO DE ESTRUTURAL - GARAGEM DAS MÁQUINAS - COREMAS/PB

FOLHA: PROJETO DE ESTRUTURAL - GARAGEM DAS MÁQUINAS - COREMAS/PB

(1)/03 LOCALIDADE: MUNICÍPIO DE COREMAS - PB

DATA: JUL/2025 RESPONSÁVEL: LINCOLN CARTAXO RUBRICA: DADOS

CÓPIA: VISTO: CONVENI

ESCALAS: DESENHOS: • Planta de Locação • Detalhamento das Sapatas • Detalhamento de arranjos dos pilares • Detalhamento de chumbamento e chapa base

INDICADAS: ARQUIVO:

Aprovações: