



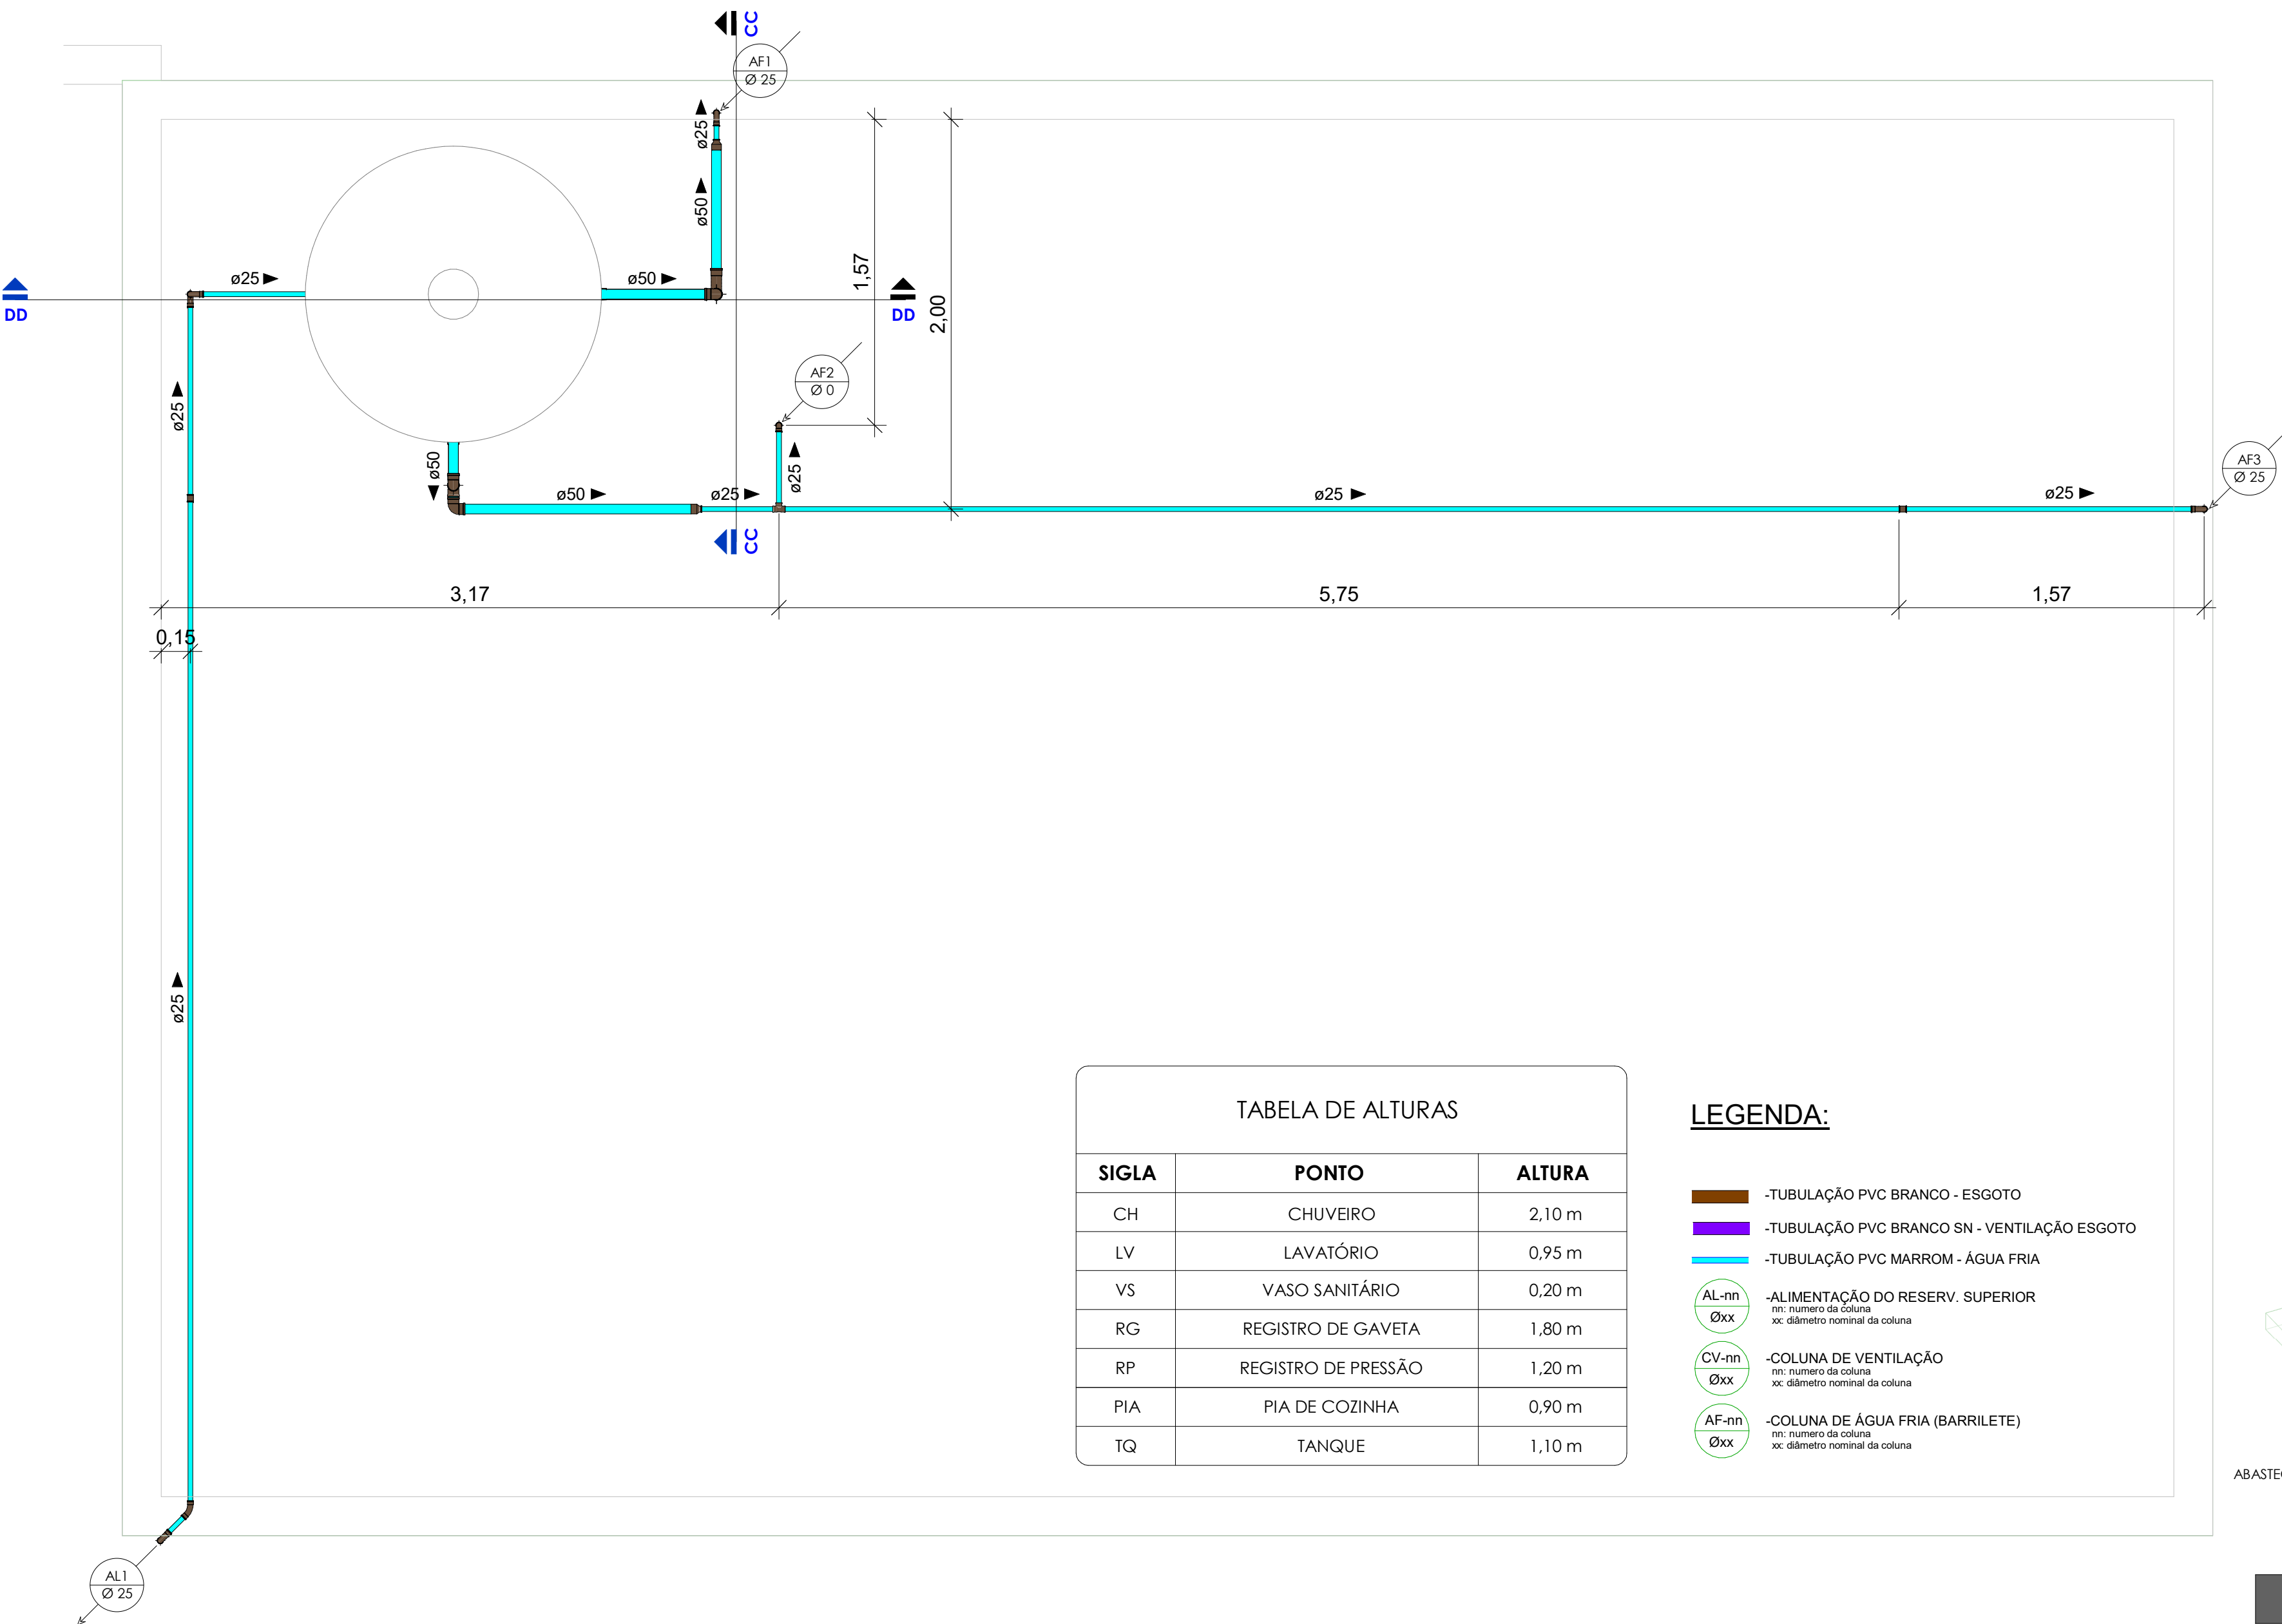


TABELA DE ALTURAS		
SIGLA	PONTO	ALTURA
CH	CHUVEIRO	2,10 m
LV	LAVATÓRIO	0,95 m
VS	VASO SANITÁRIO	0,20 m
RG	REGISTRO DE GAVETA	1,80 m
RP	REGISTRO DE PRESSÃO	1,20 m
PIA	PIA DE COZINHA	0,90 m
TQ	TANQUE	1,10 m

LEGENDA:


- TUBULAÇÃO PVC BRANCO - ESGOTO
- TUBULAÇÃO PVC BRANCO SN - VENTILAÇÃO ESGOTO
- TUBULAÇÃO PVC MARROM - ÁGUA FRIA
- AL-nn
Øxx - ALIMENTAÇÃO DO RESERV. SUPERIOR
nn: número da coluna
xx: diâmetro nominal da coluna
- CV-nn
Øxx - COLUNA DE VENTILAÇÃO
nn: número da coluna
xx: diâmetro nominal da coluna
- AF-nn
Øxx - COLUNA DE ÁGUA FRIA (BARRILETE)
nn: número da coluna
xx: diâmetro nominal da coluna

PLANTA BAIXA_CAIXA D'ÁGUA_02 - ESC 1/25

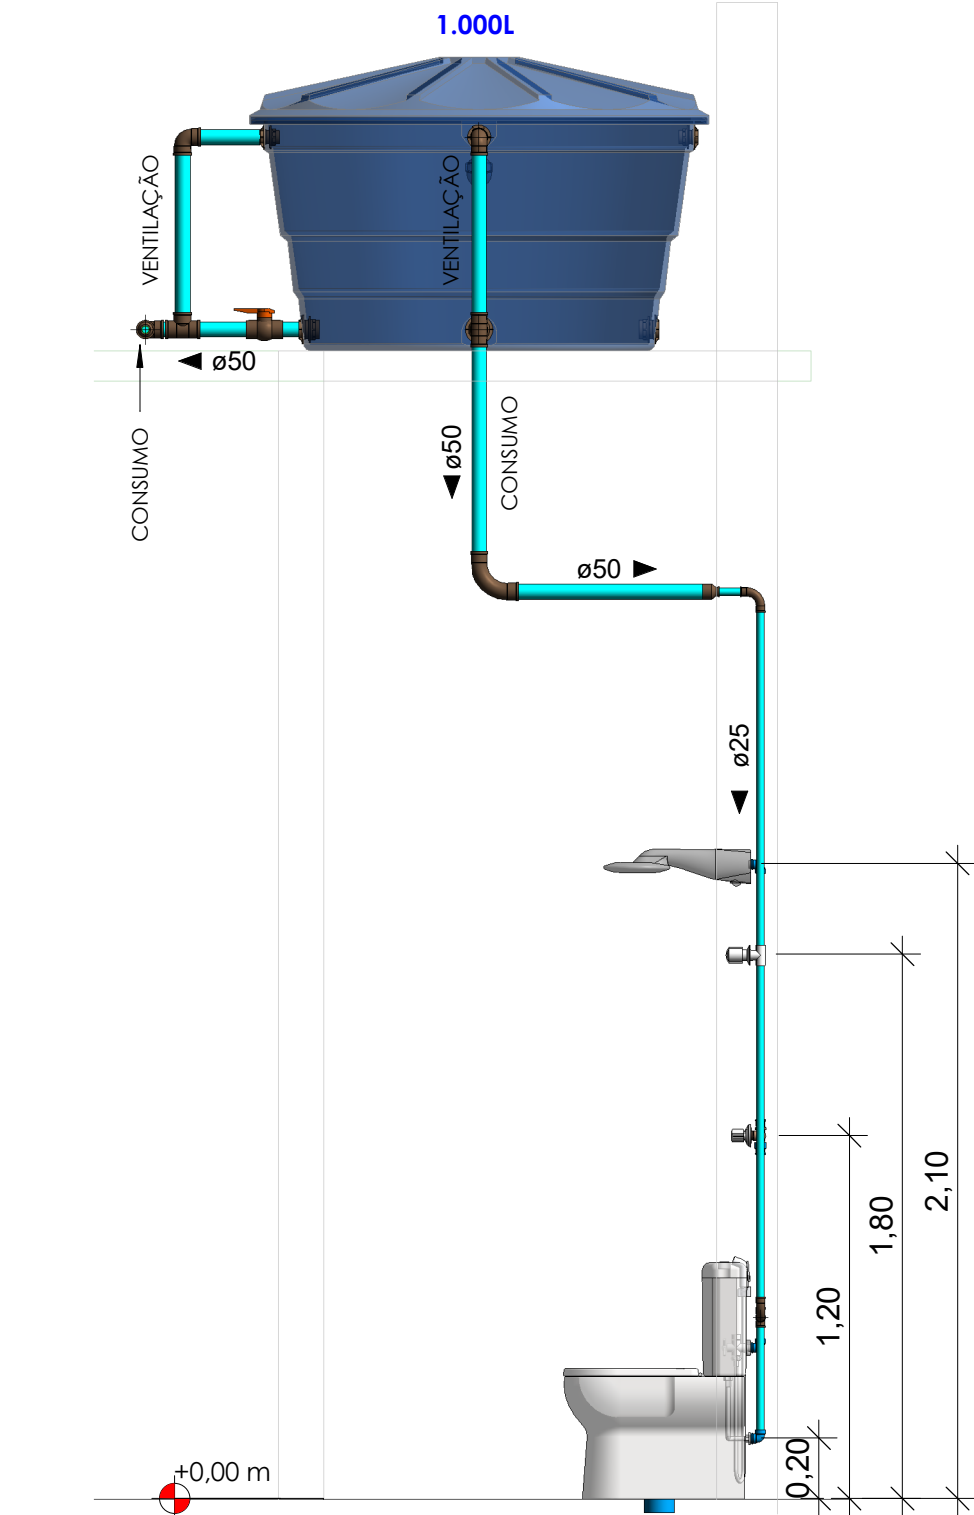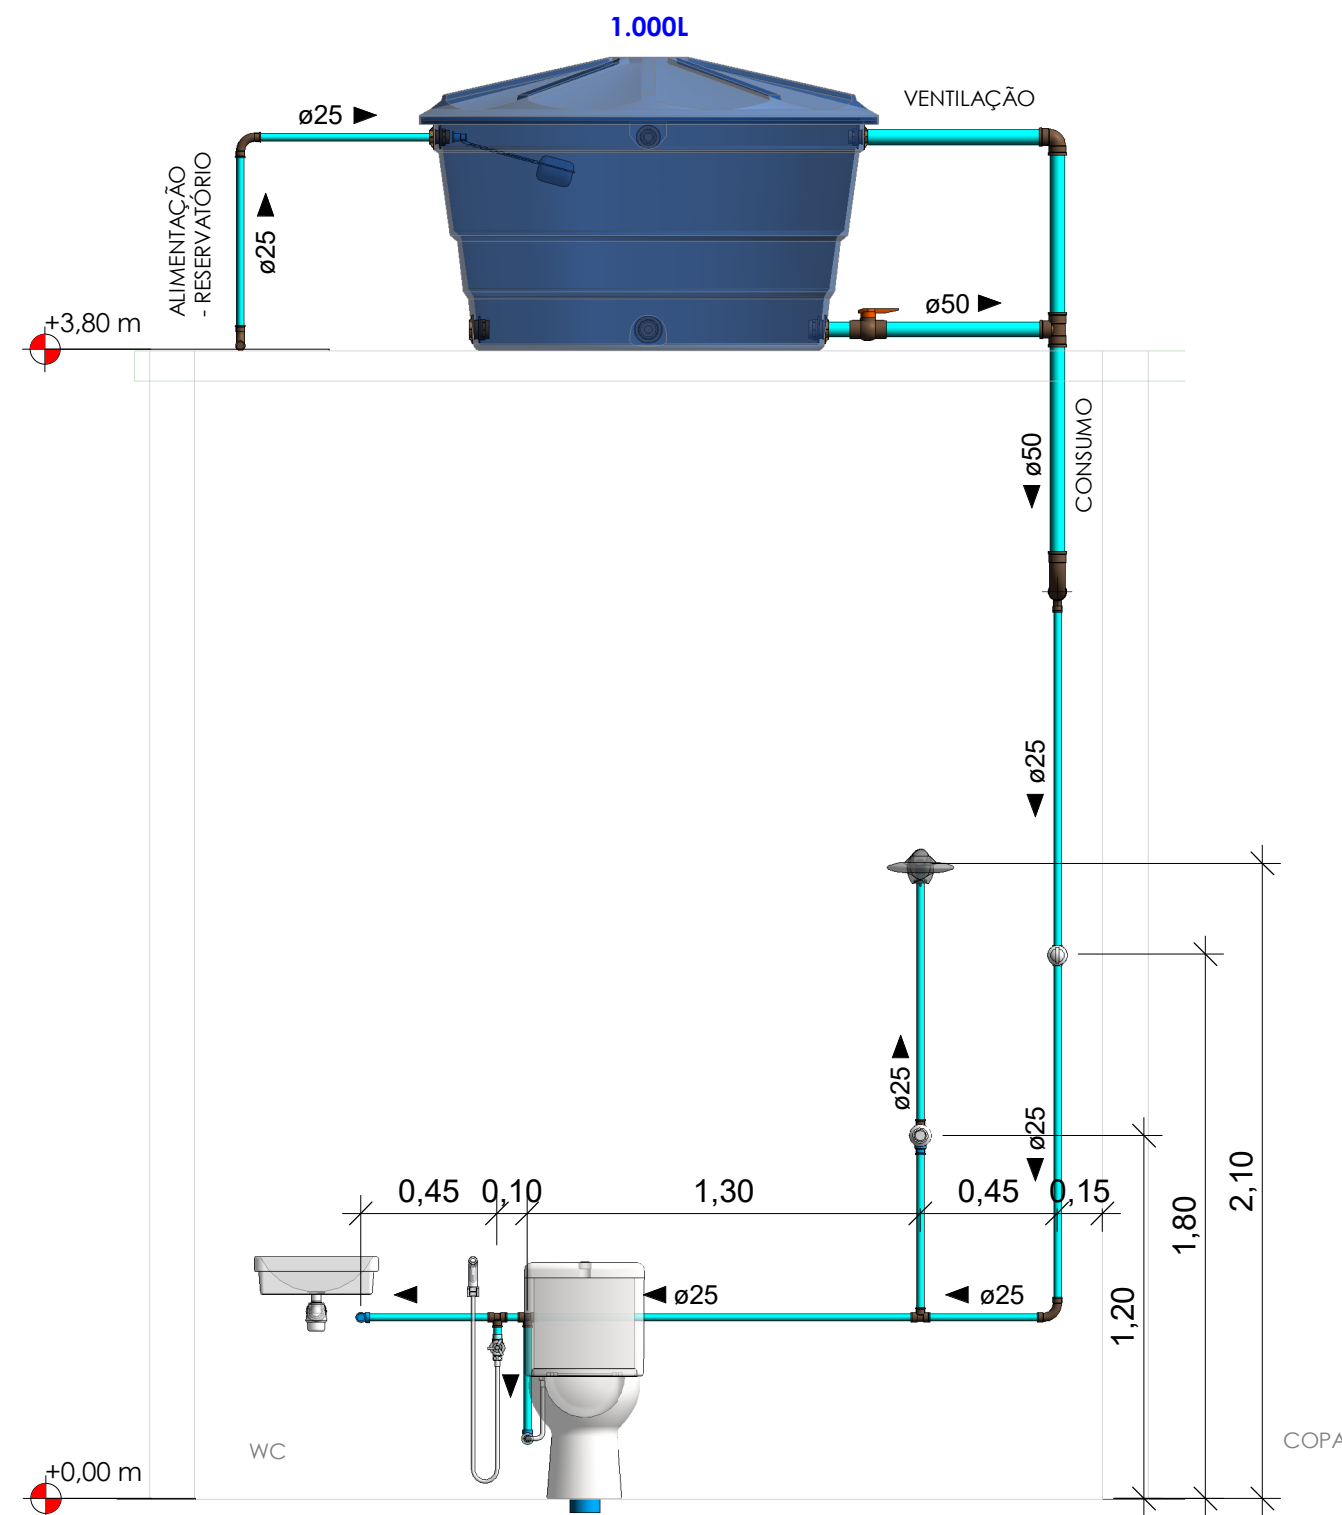


CORTE DD ESC 1/25


CORTE CC ESC 1/25

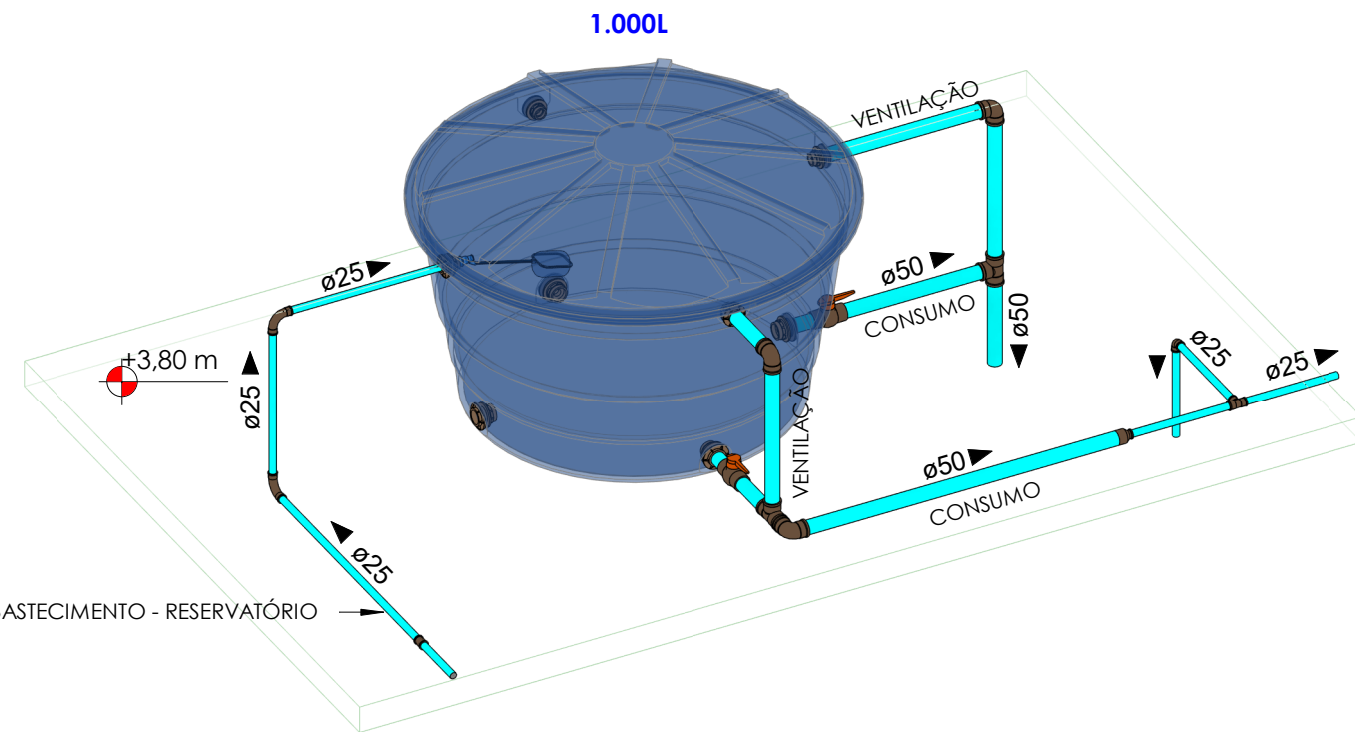


ISOMÉTRICA 05 - CAIXA D'ÁGUA - ESC 1/25

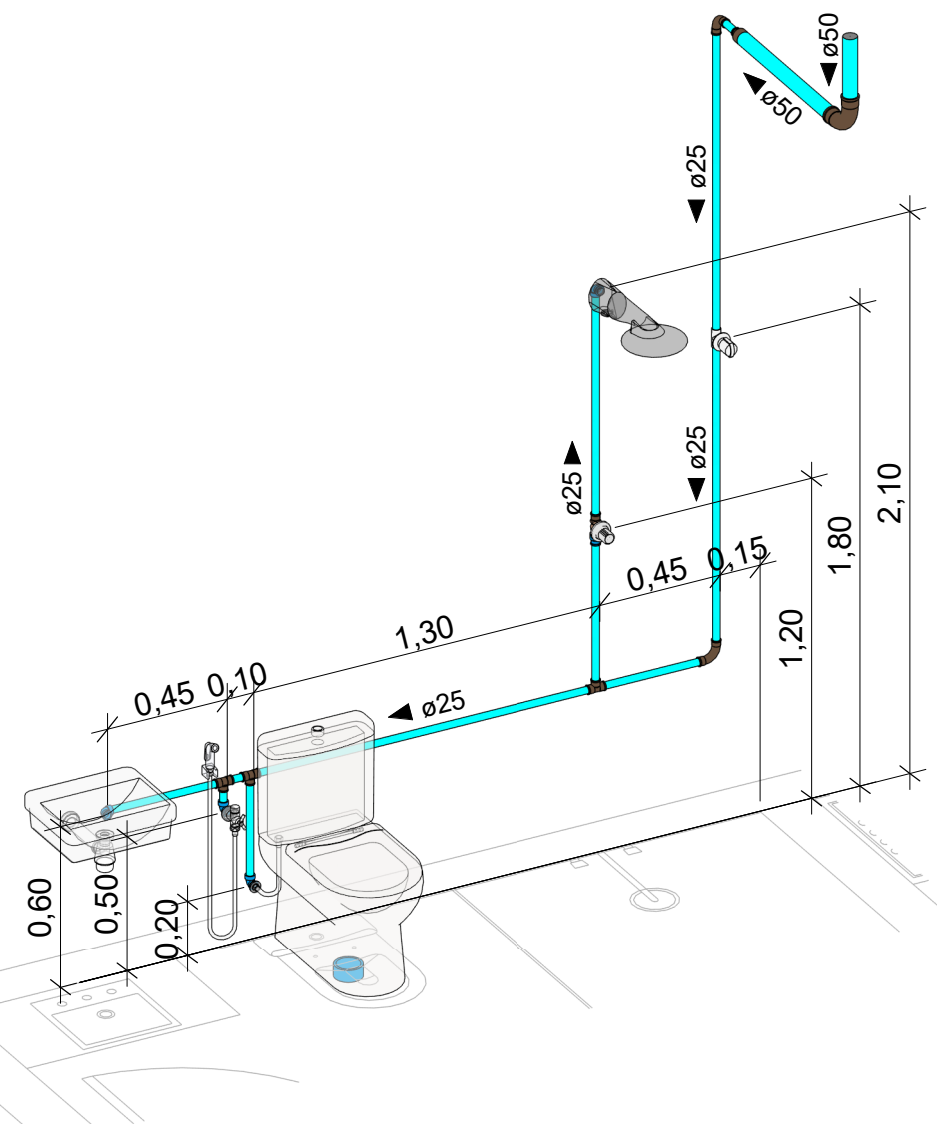

ISOMÉTRICA 03 - WC - ESC 1/25

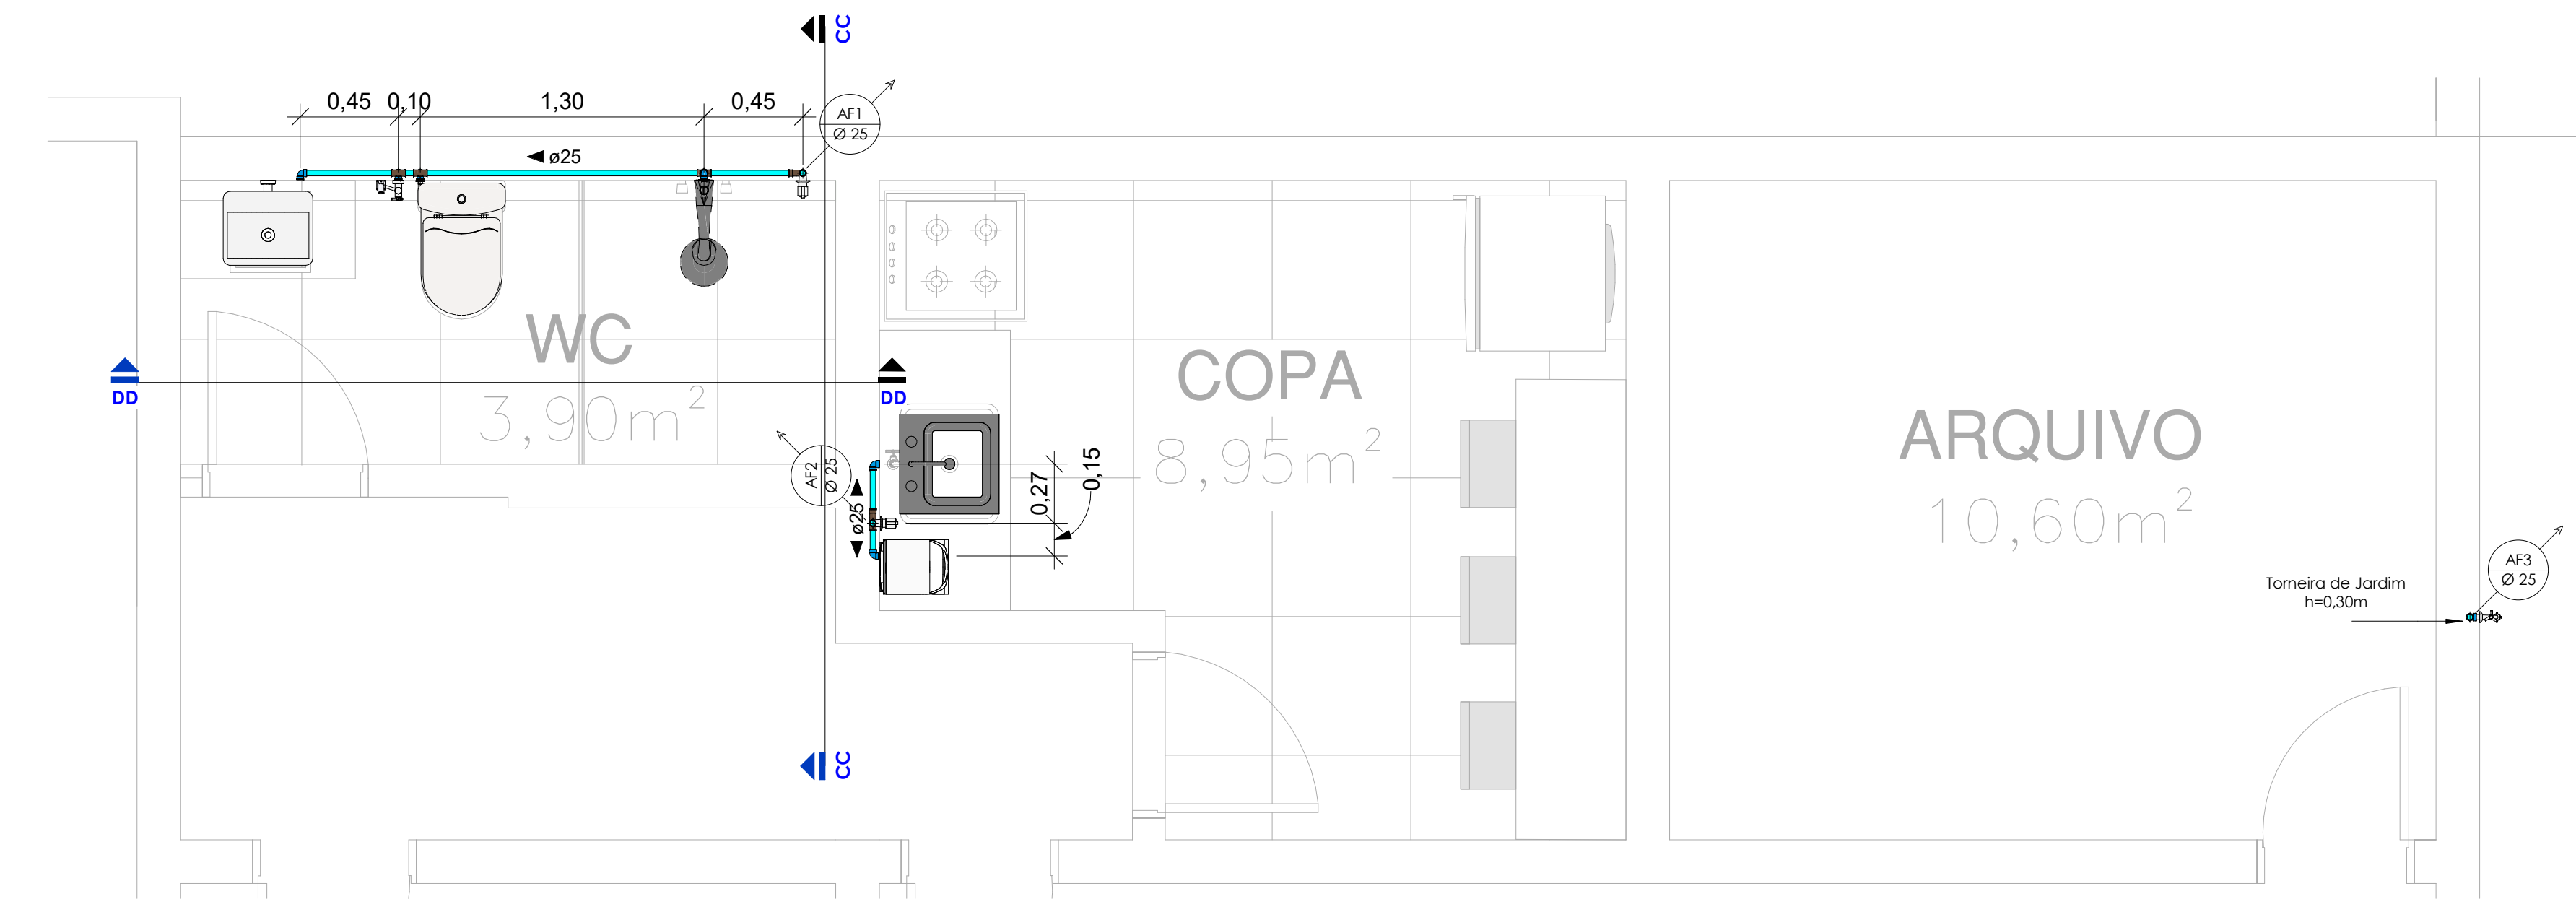

PLANTA BAIXA_REFORMA_GARAGEM_COREMAS_TÉRREO_COPA_WC_ARQUIVO - ESC 1/25

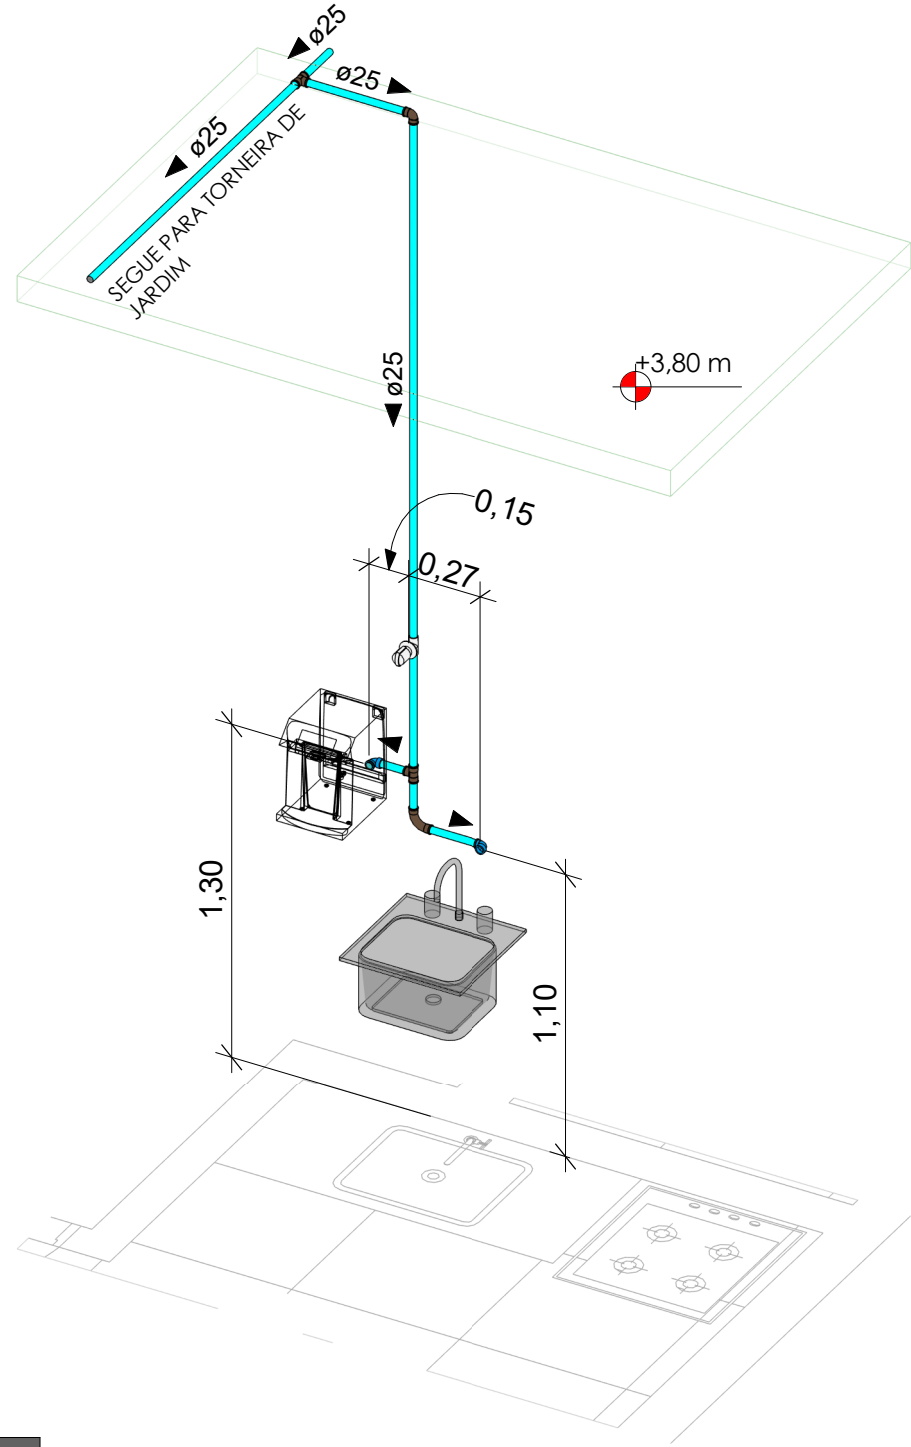

ISOMÉTRICA 04 - COPA - ESC 1/25

PROPRIETÁRIO: PREFEITURA MUNICIPAL DE COREMAS - PB			
PROJETO: LINCOLN CARTAXO DE LIRA JÚNIOR CREA 160.814.689-8			
PROJETO:		INSTALAÇÕES HIDRÁULICAS DA REFORMA DA GARAGEM	
CONCEDENTE:		PREFEITURA MUNICIPAL DE COREMAS - PB	
CONVENIENTE:		MUNICÍPIO DE COREMAS - PB	
LOCAL:		COREMAS - PB	
DATA	17/06/2025	LINCOLN CARTAXO	CREA 160.814.689-8
CÓPIA			
VISTO			
PRANCHA:		DESCRIÇÃO:	
01 / 03		PLANTA BAIXA - CAIXA D'ÁGUA, TÉRREO CORTES E ISOMÉTRICAS	
		ESCALA:	
		INDICADA	



Av. Gov. Flavio R. Coutinho, 500, sl. 601
Jd. Oceania, 58037-005 - João Pessoa (PB)
Tel +55 99924.4447
e-mail: contato@lclprojetos.com