


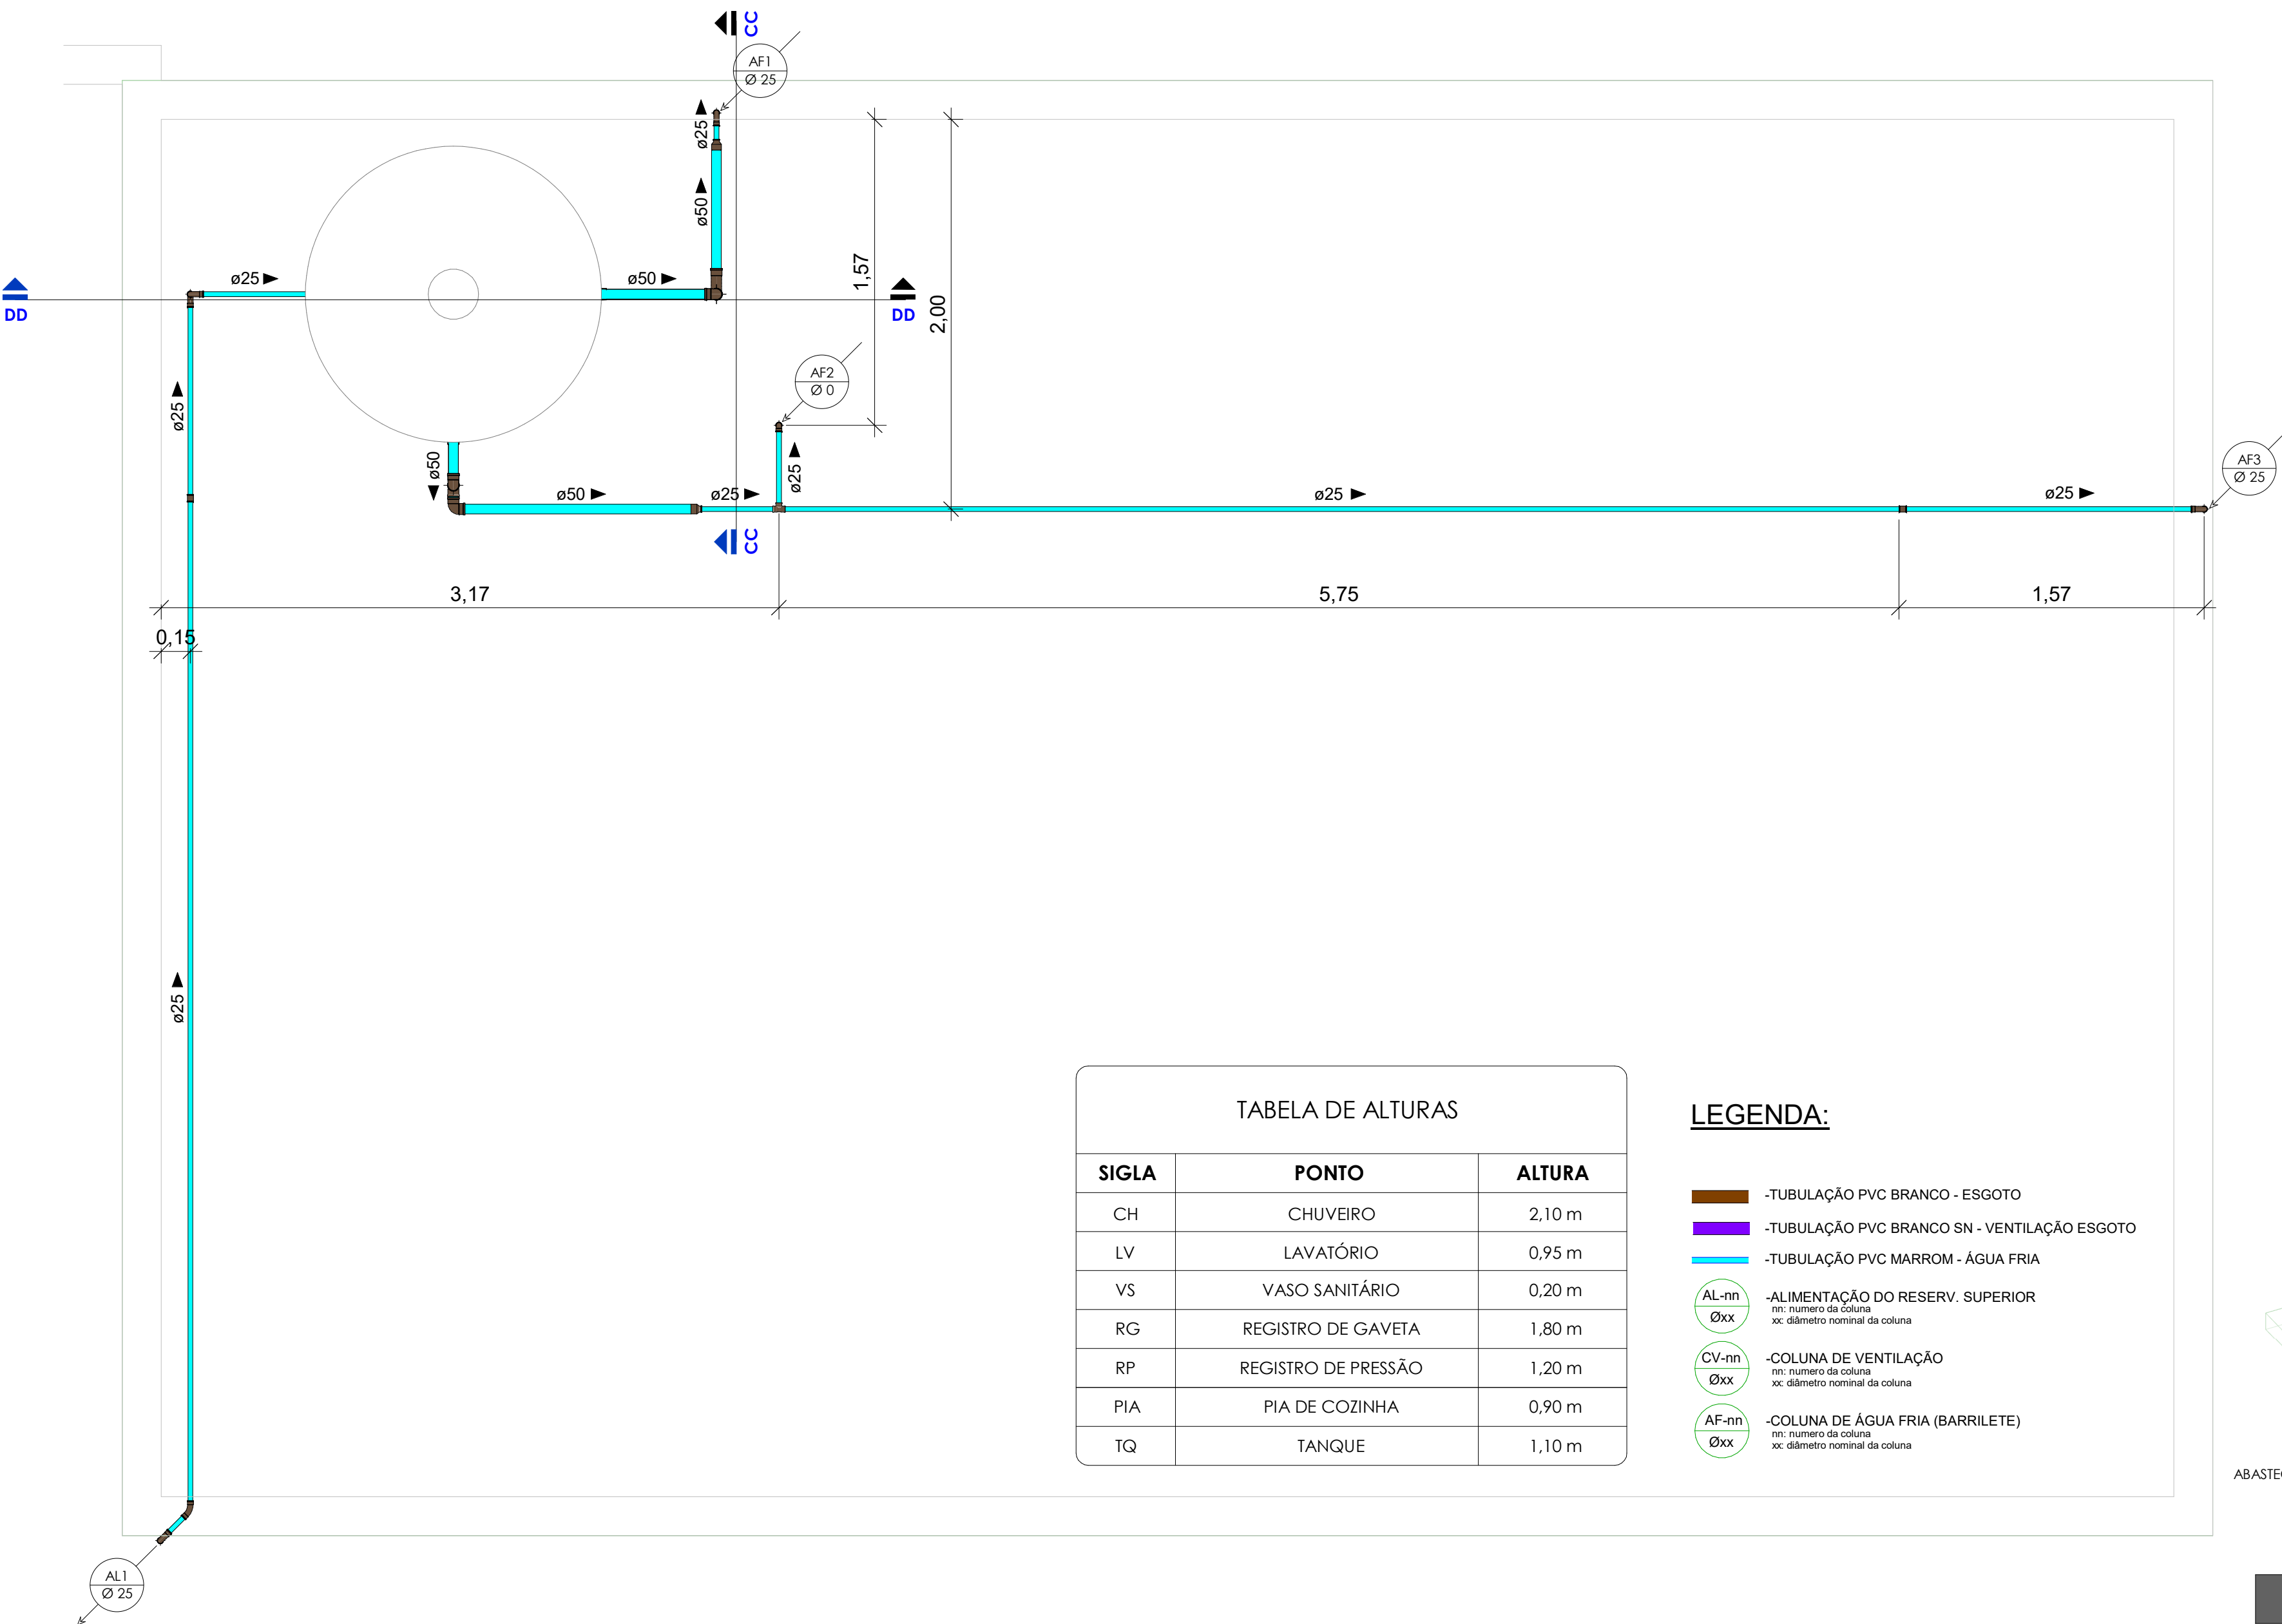



TABELA DE ALTURAS		
SIGLA	PONTO	ALTURA
CH	CHUVEIRO	2,10 m
LV	LAVATÓRIO	0,95 m
VS	VASO SANITÁRIO	0,20 m
RG	REGISTRO DE GAVETA	1,80 m
RP	REGISTRO DE PRESSÃO	1,20 m
PIA	PIA DE COZINHA	0,90 m
TQ	TANQUE	1,10 m

- LEGENDA:**
- TUBULAÇÃO PVC BRANCO - ESGOTO
 - TUBULAÇÃO PVC BRANCO SN - VENTILAÇÃO ESGOTO
 - TUBULAÇÃO PVC MARROM - ÁGUA FRIA
 - AL-nn
Øxx - ALIMENTAÇÃO DO RESERV. SUPERIOR
nn: número da coluna
xx: diâmetro nominal da coluna
 - CV-nn
Øxx - COLUNA DE VENTILAÇÃO
nn: número da coluna
xx: diâmetro nominal da coluna
 - AF-nn
Øxx - COLUNA DE ÁGUA FRIA (BARRILETE)
nn: número da coluna
xx: diâmetro nominal da coluna


PLANTA BAIXA_CAIXA_D'ÁGUA_02 - ESC 1/25

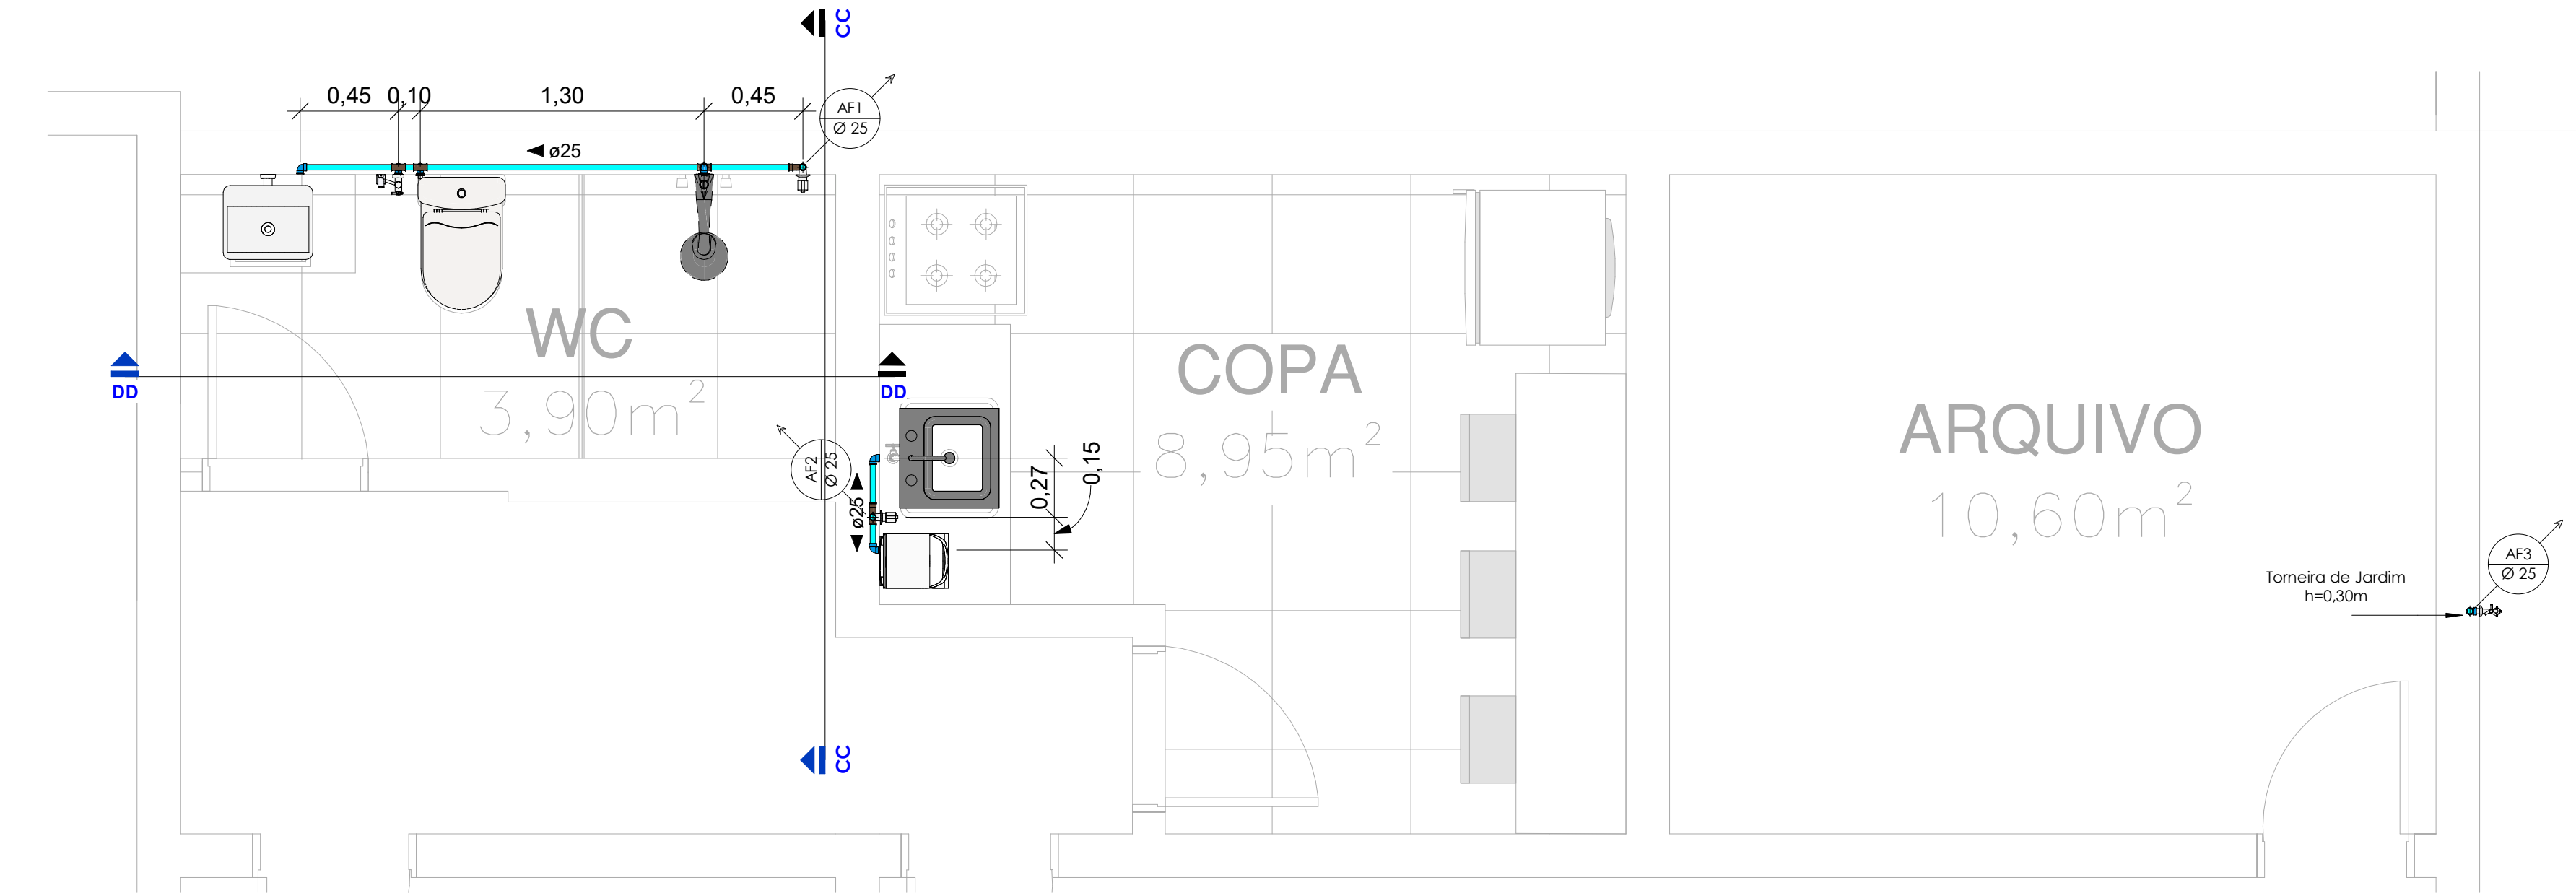


PLANTA BAIXA_REFORMA_GARAGEM_COREMAS_TÉRREO_COPA_WC_ARQUIVO - ESC 1/25

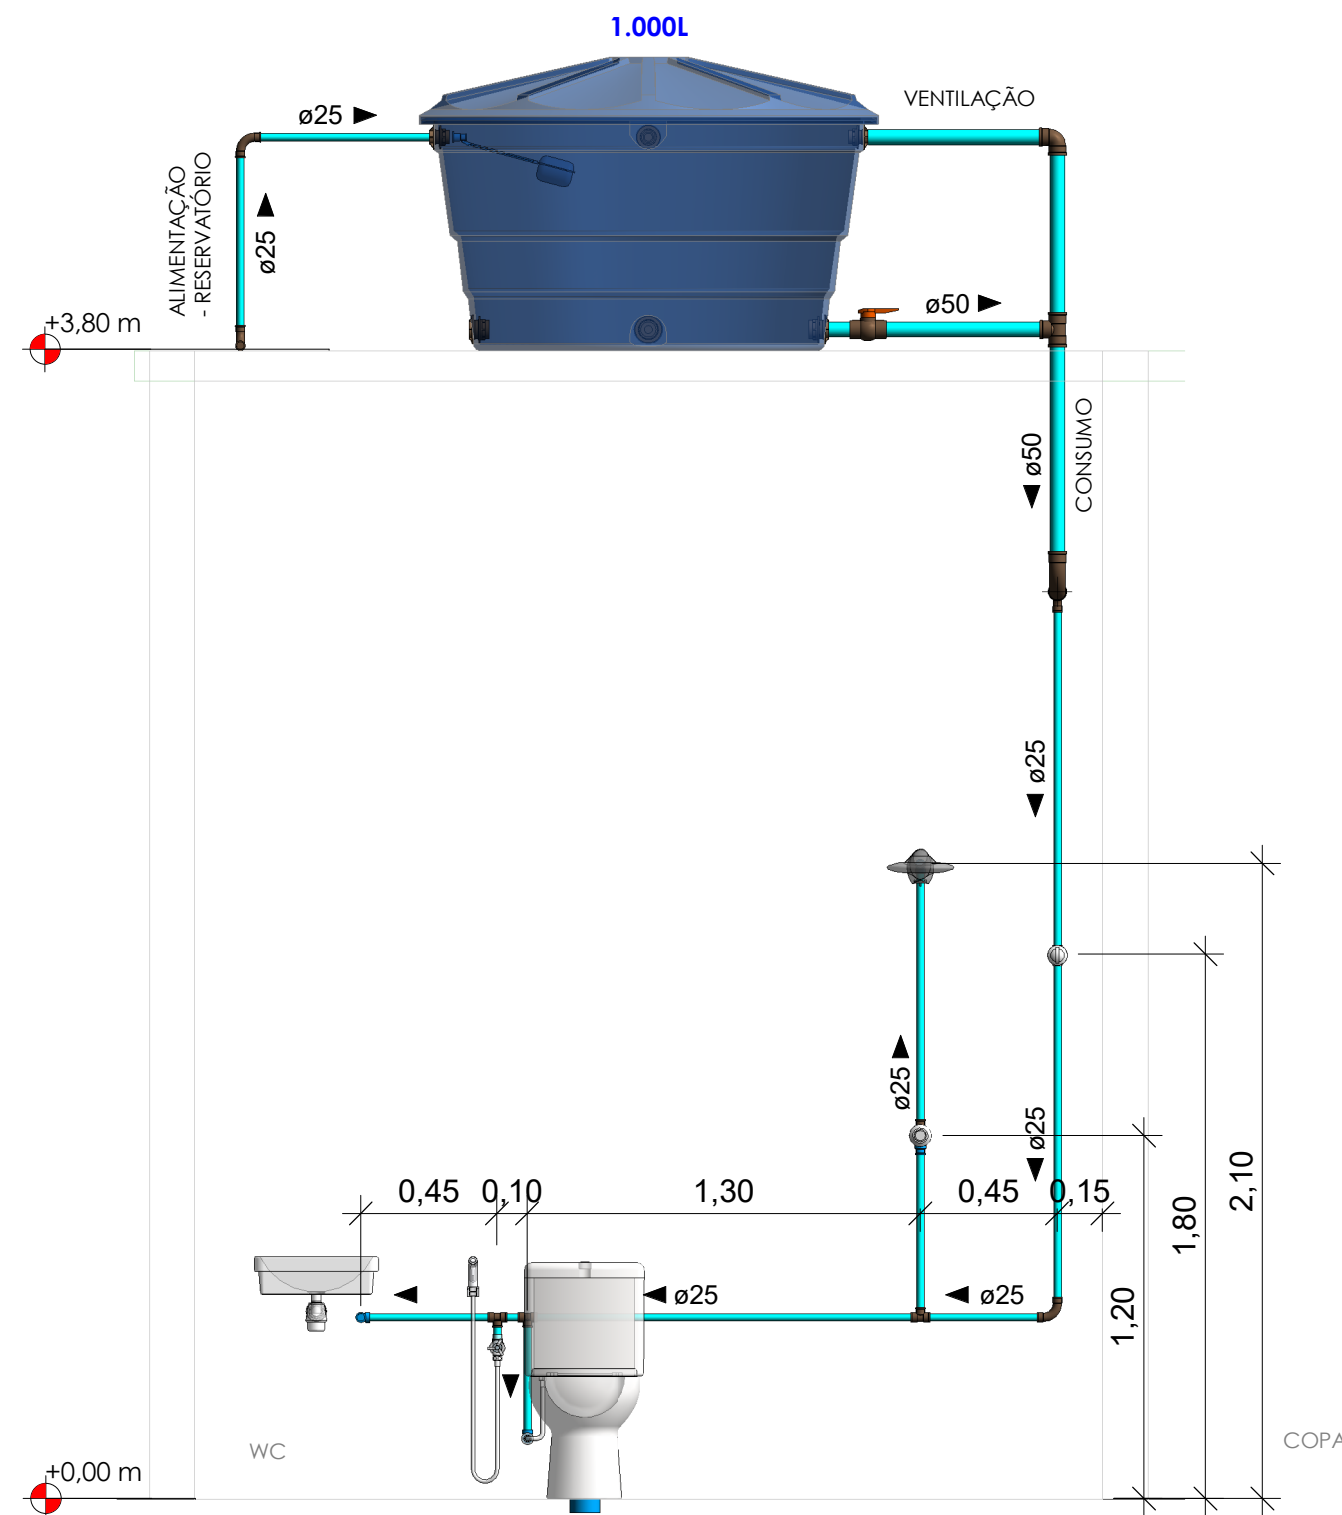


CORTE DD ESC 1/25

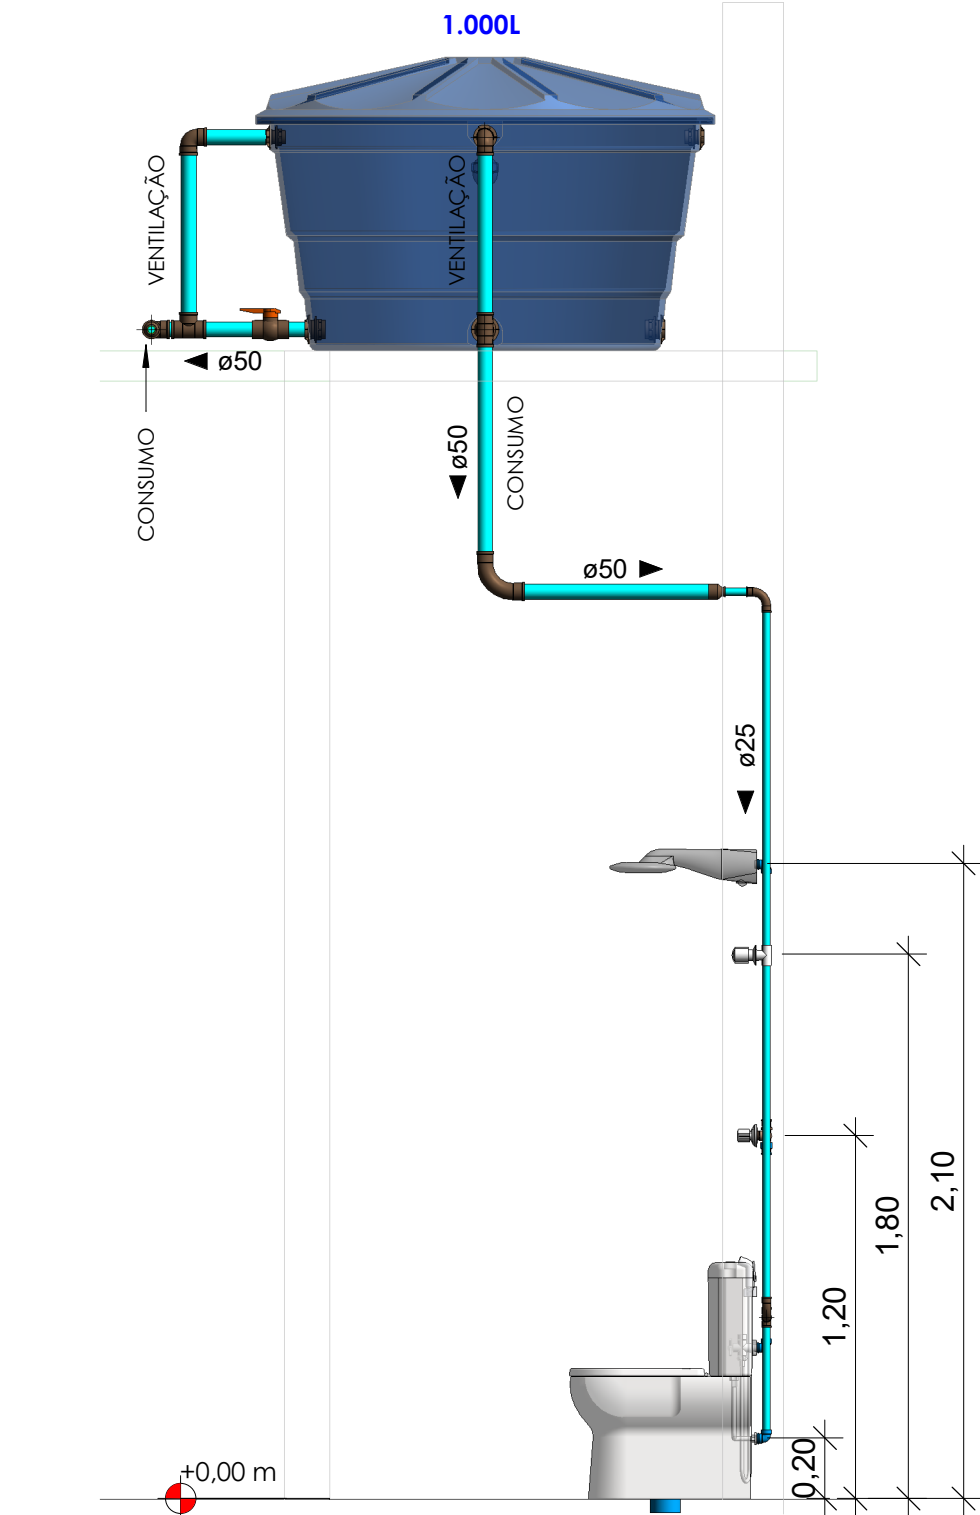


CORTE CC ESC 1/25

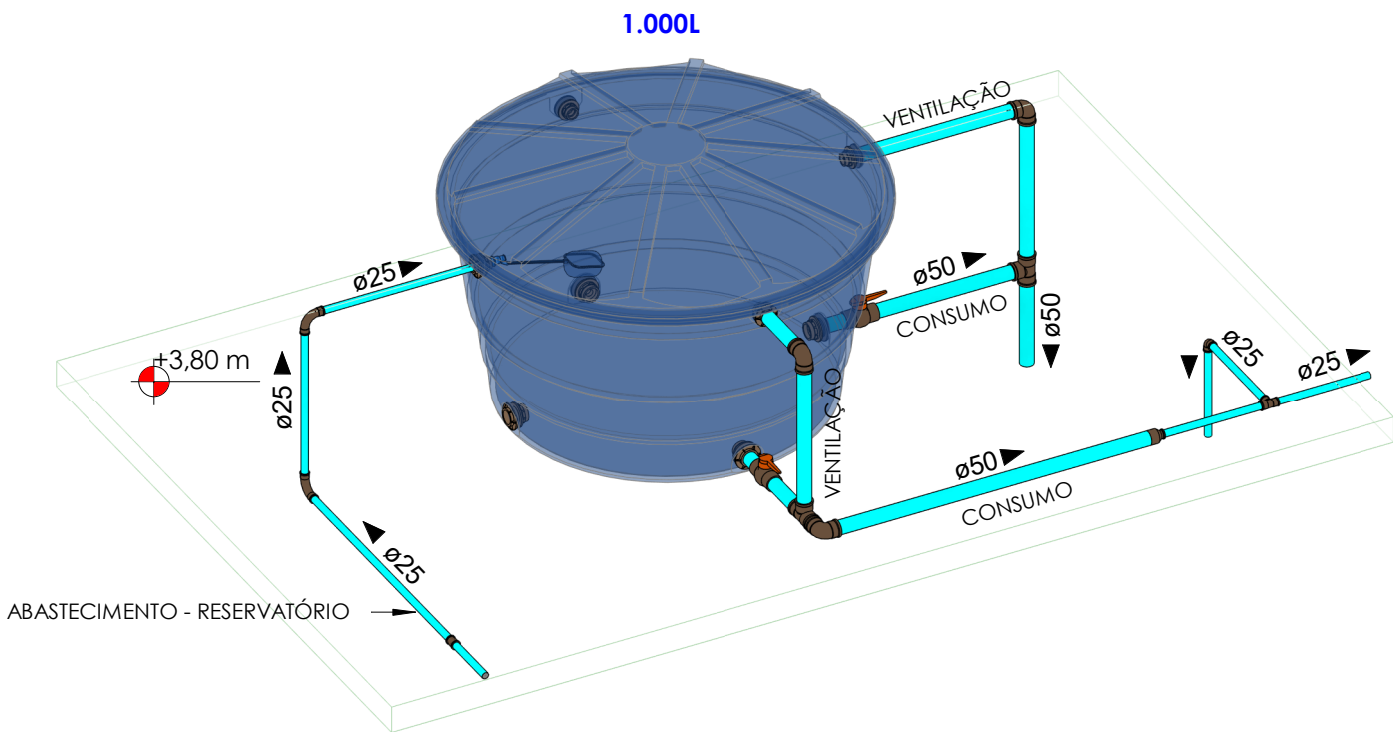

ISOMÉTRICA 05 - CAIXA D'ÁGUA - ESC 1/25

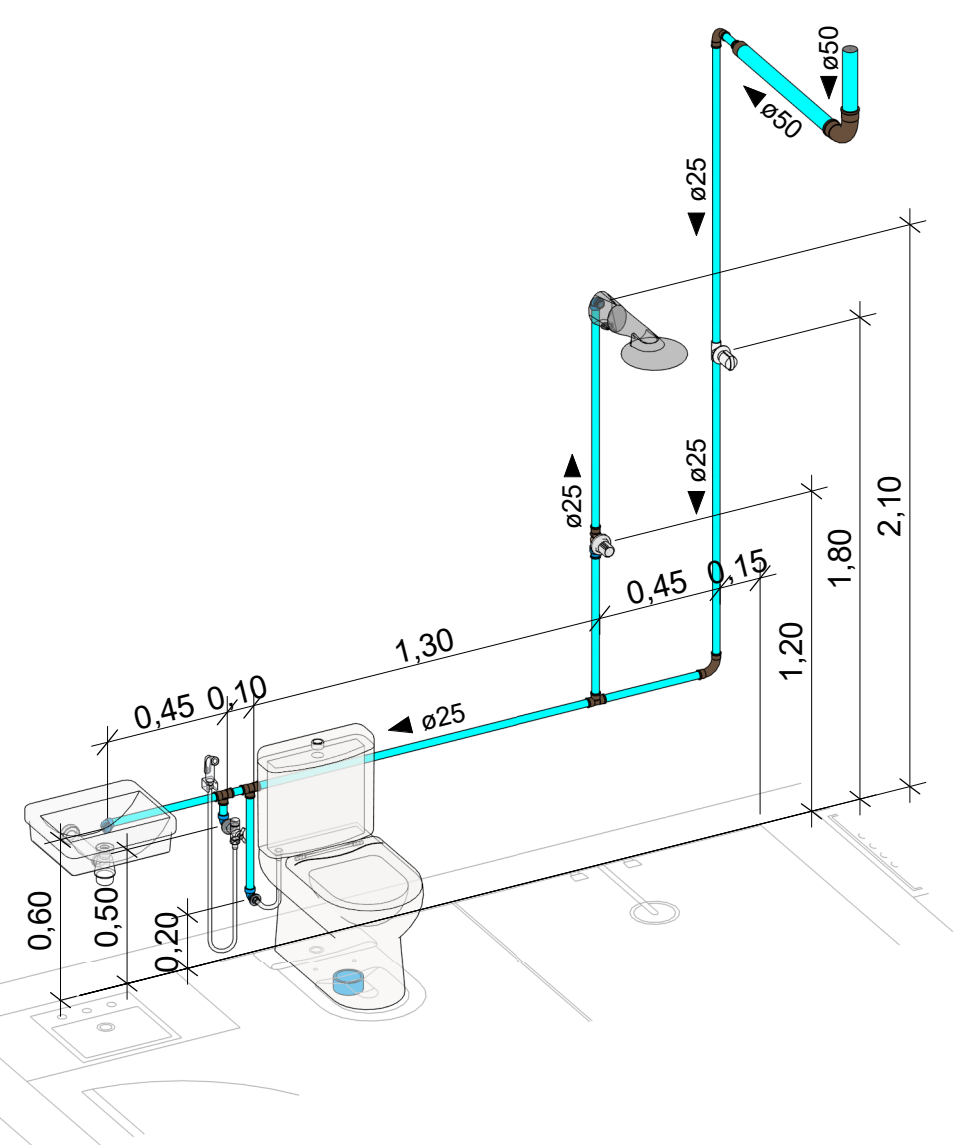

ISOMÉTRICA 03 - WC - ESC 1/25

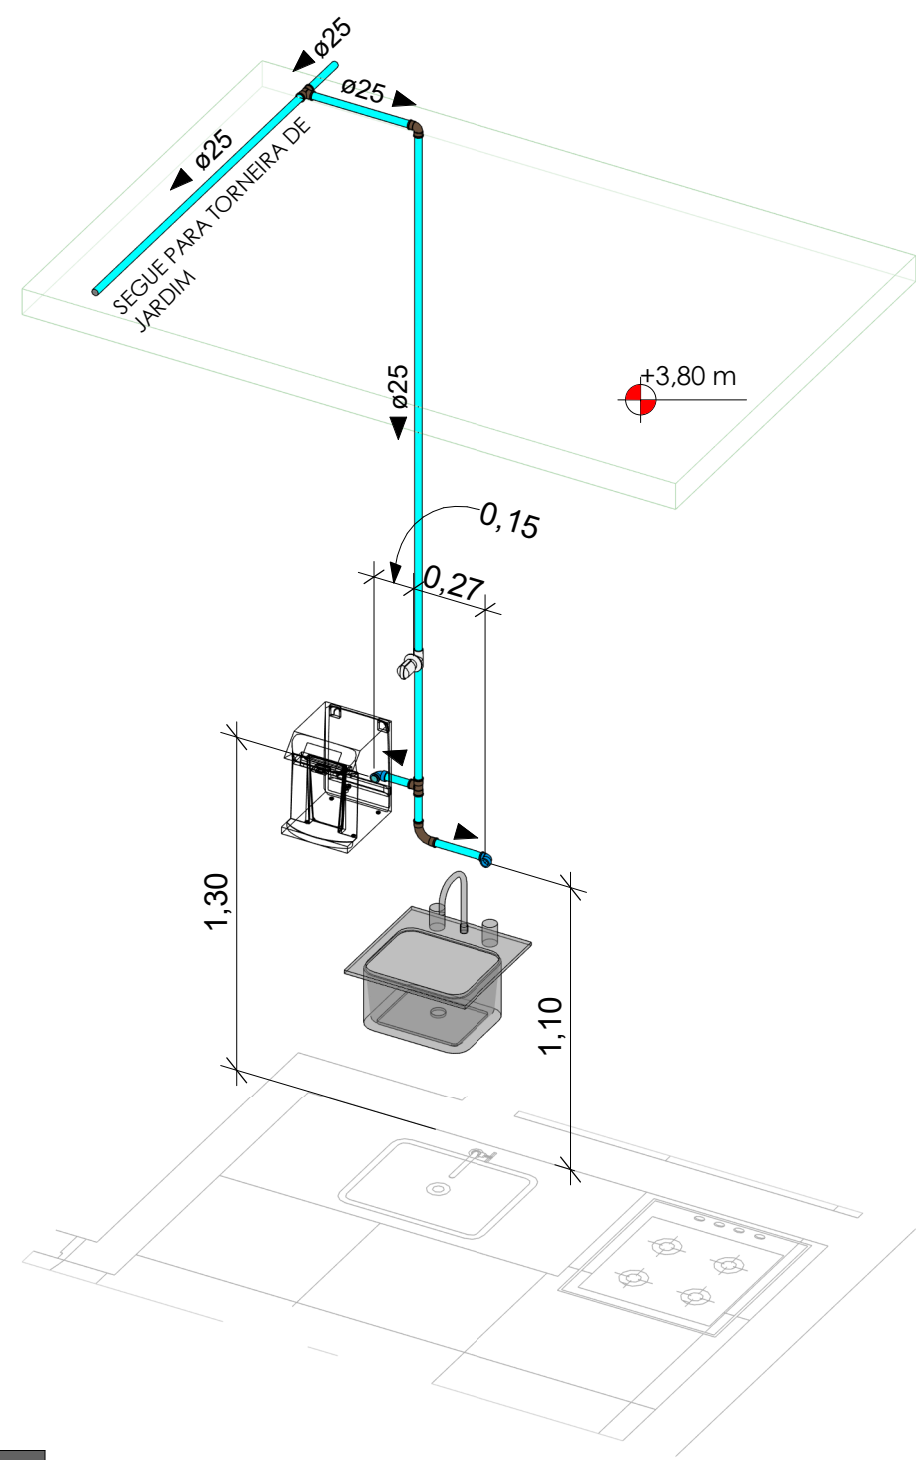


ISOMÉTRICA 04 - COPA - ESC 1/25


PROPRIETÁRIO: PREFEITURA MUNICIPAL DE COREMAS - PB LINCOLN CARTAXO DE LIRA JUNIOR:06897861405			
Assinado de forma digital por LINCOLN CARTAXO DE LIRA JUNIOR:06897861405 Dados: 2025.08.11 14:45:15 -03'00'			
PROJETO: LINCOLN CARTAXO DE LIRA JÚNIOR		CREA 160.814.689-8	
PROJETO: INSTALAÇÕES HIDRÁULICAS DA REFORMA DA GARAGEM			
CONCEDENTE: PREFEITURA MUNICIPAL DE COREMAS - PB			
CONVENIENTE: MUNICÍPIO DE COREMAS - PB			
LOCAL: COREMAS - PB			
RESPONSÁVEL TÉCNICO		RUBRICA	DADOS
DATA	17/06/2025	LINCOLN CARTAXO	CREA 160.814.689-8
CÓPIA			
VISTO			
PRANCHA: 01 / 03		DESCRIÇÃO: PLANTA BAIXA - CAIXA D'ÁGUA, TÉRREO CORTES E ISOMÉTRICAS	
		ESCALA: INDICADA	




Av. Gov. Flavio R. Coutinho, 500, sl. 601
Jd. Oceania, 58037-005 - João Pessoa (PB)
Tel +55 99924.4447
e-mail: contato@lclprojetos.com

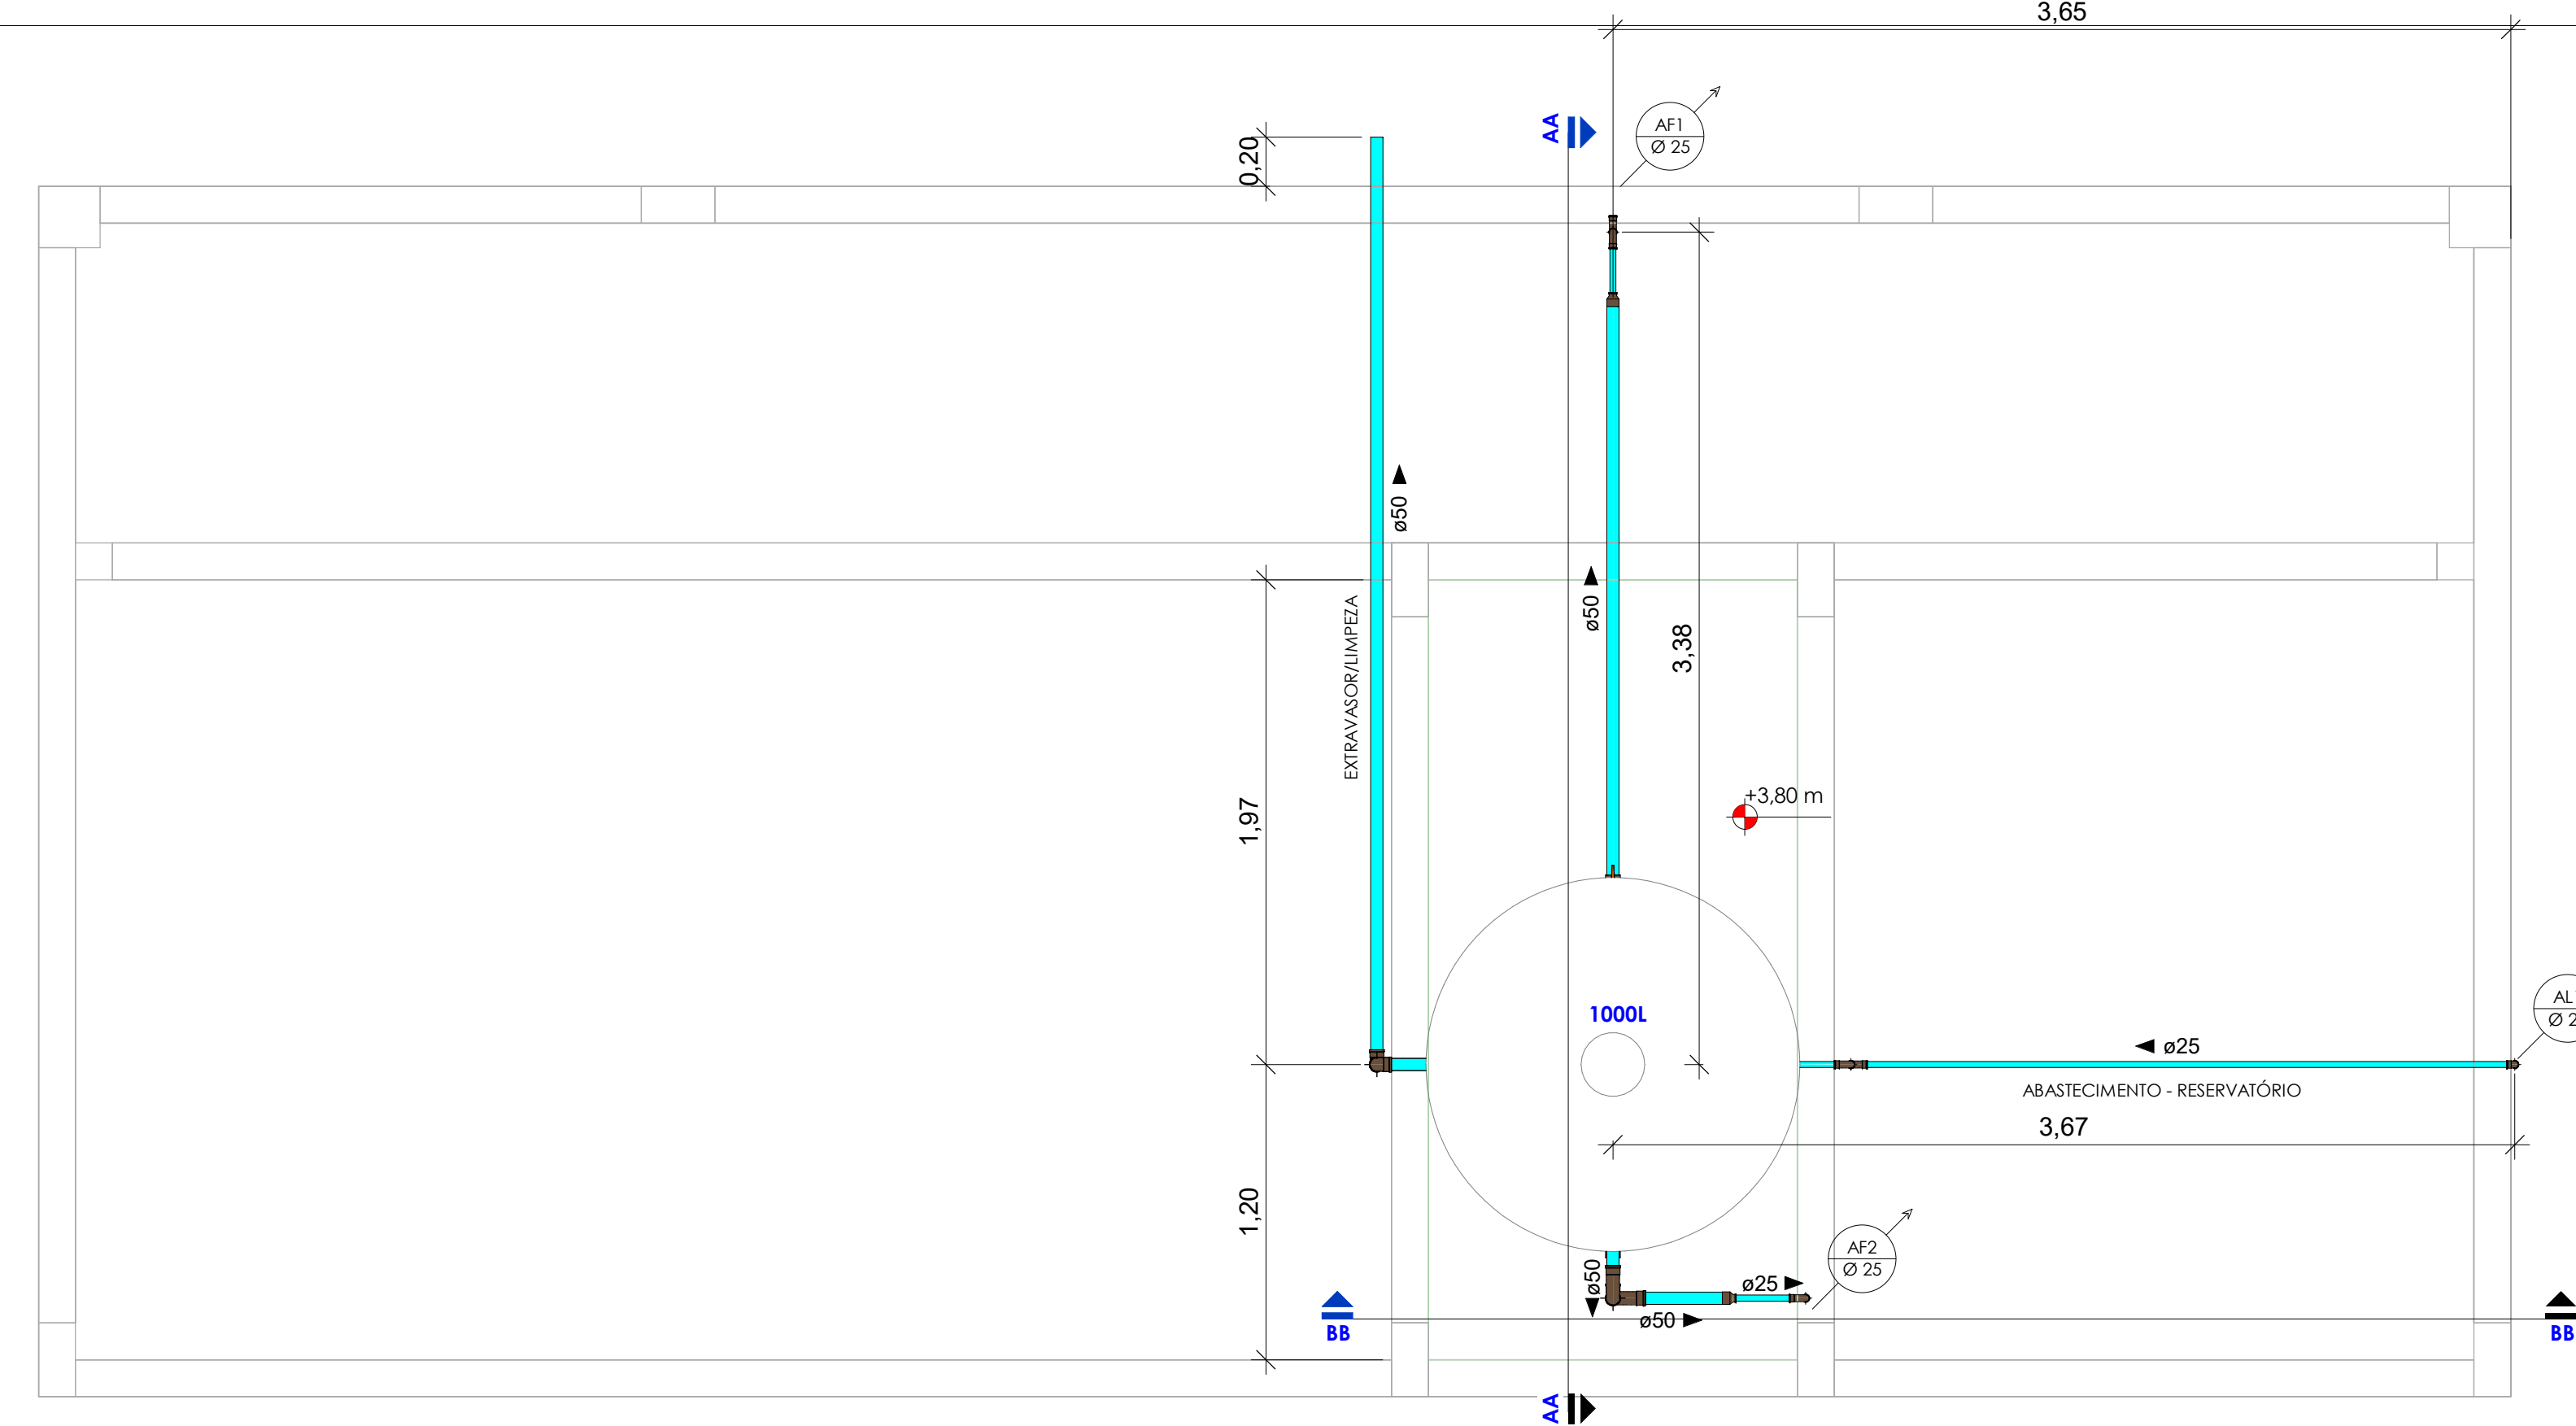


PLANTA BAIXA_ COBERTA - CAIXA_ D'ÁGUA_01 - ESC 1/25

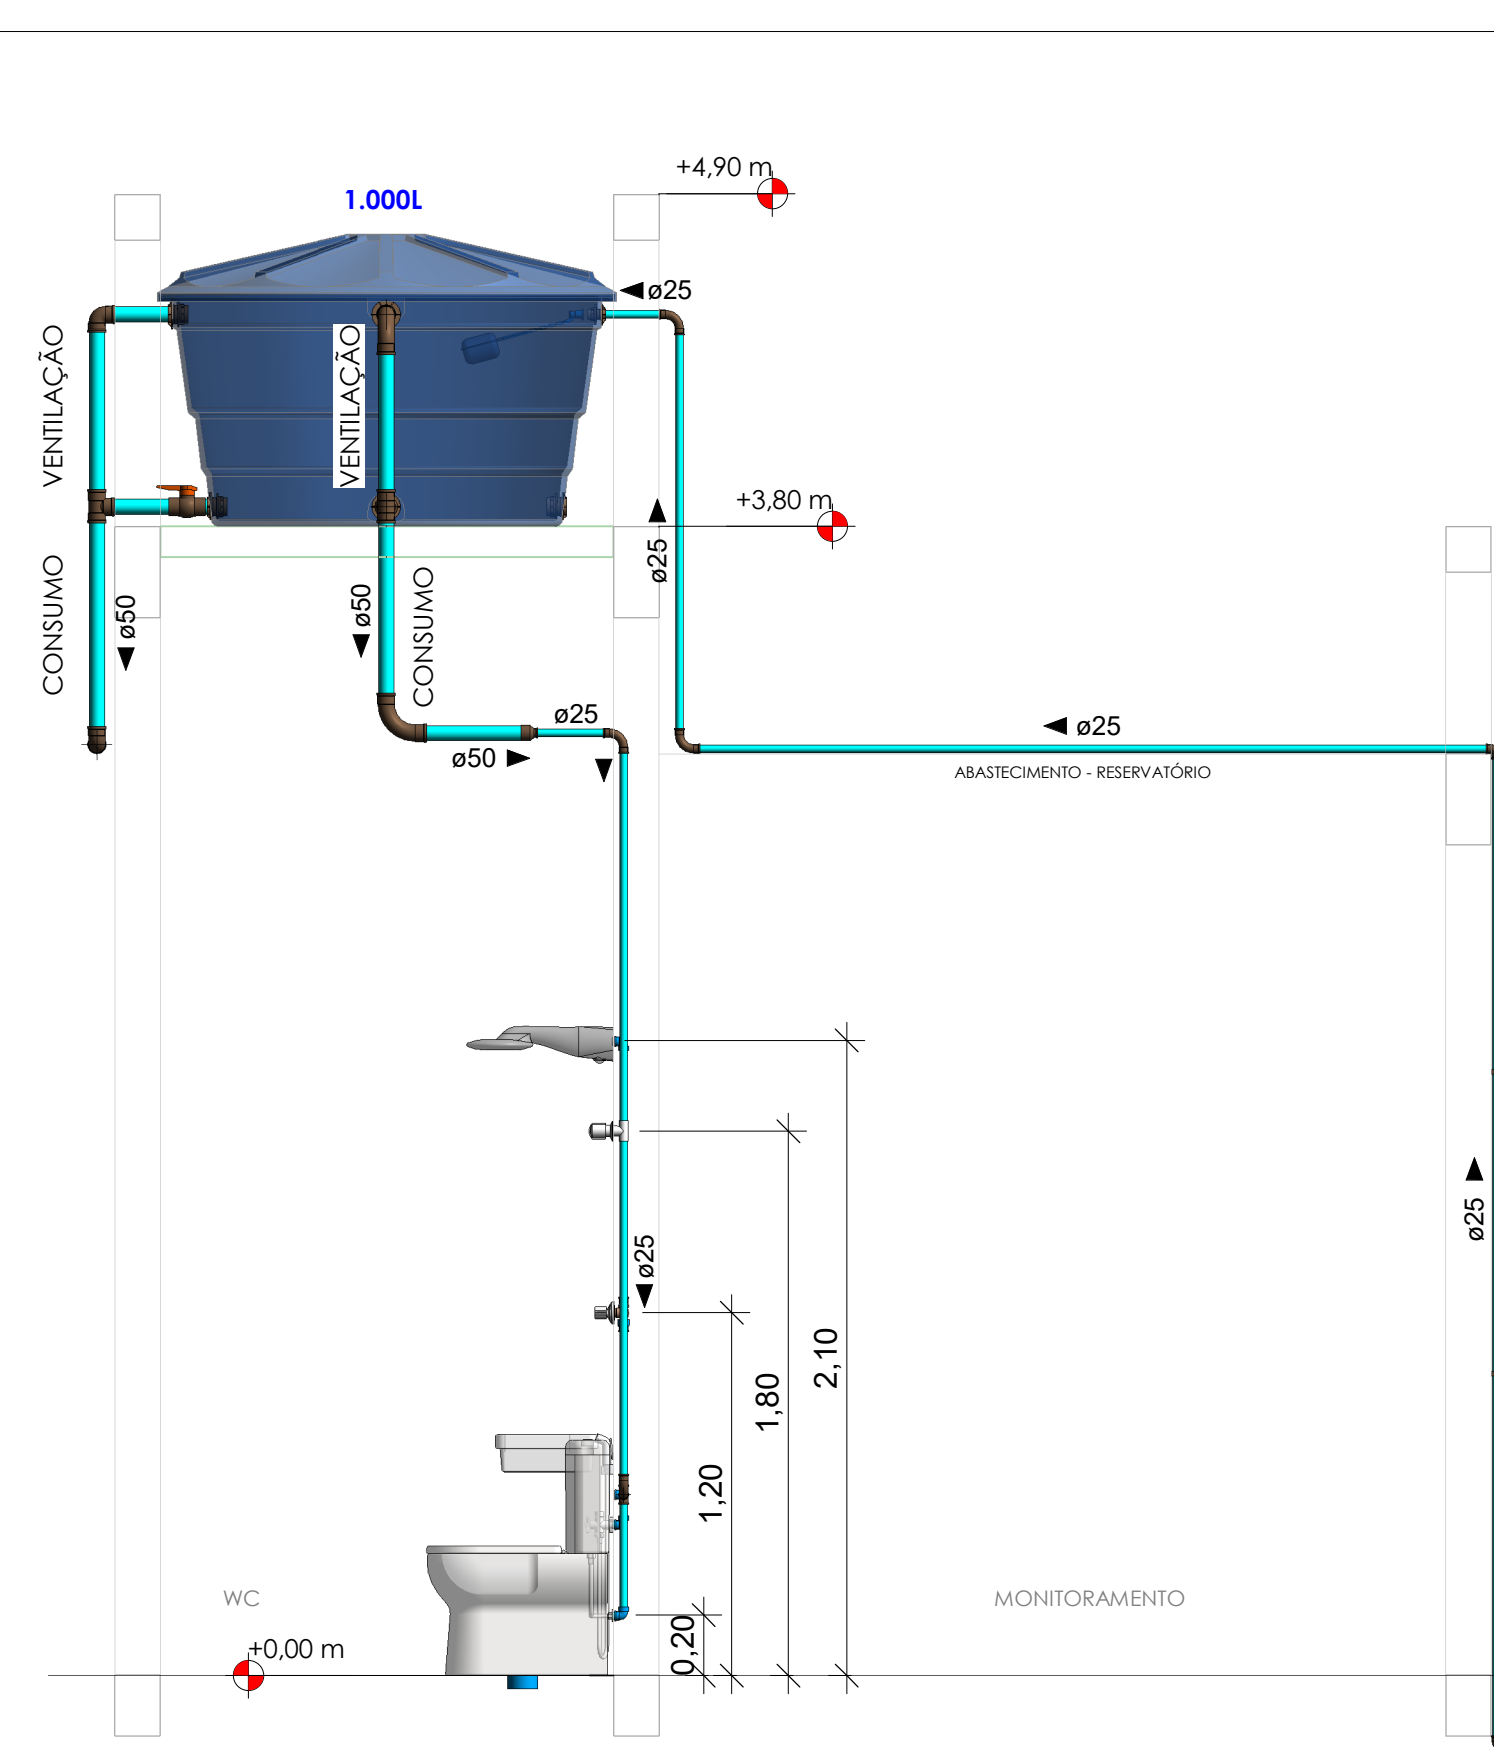


CORTE BB ESC 1/25

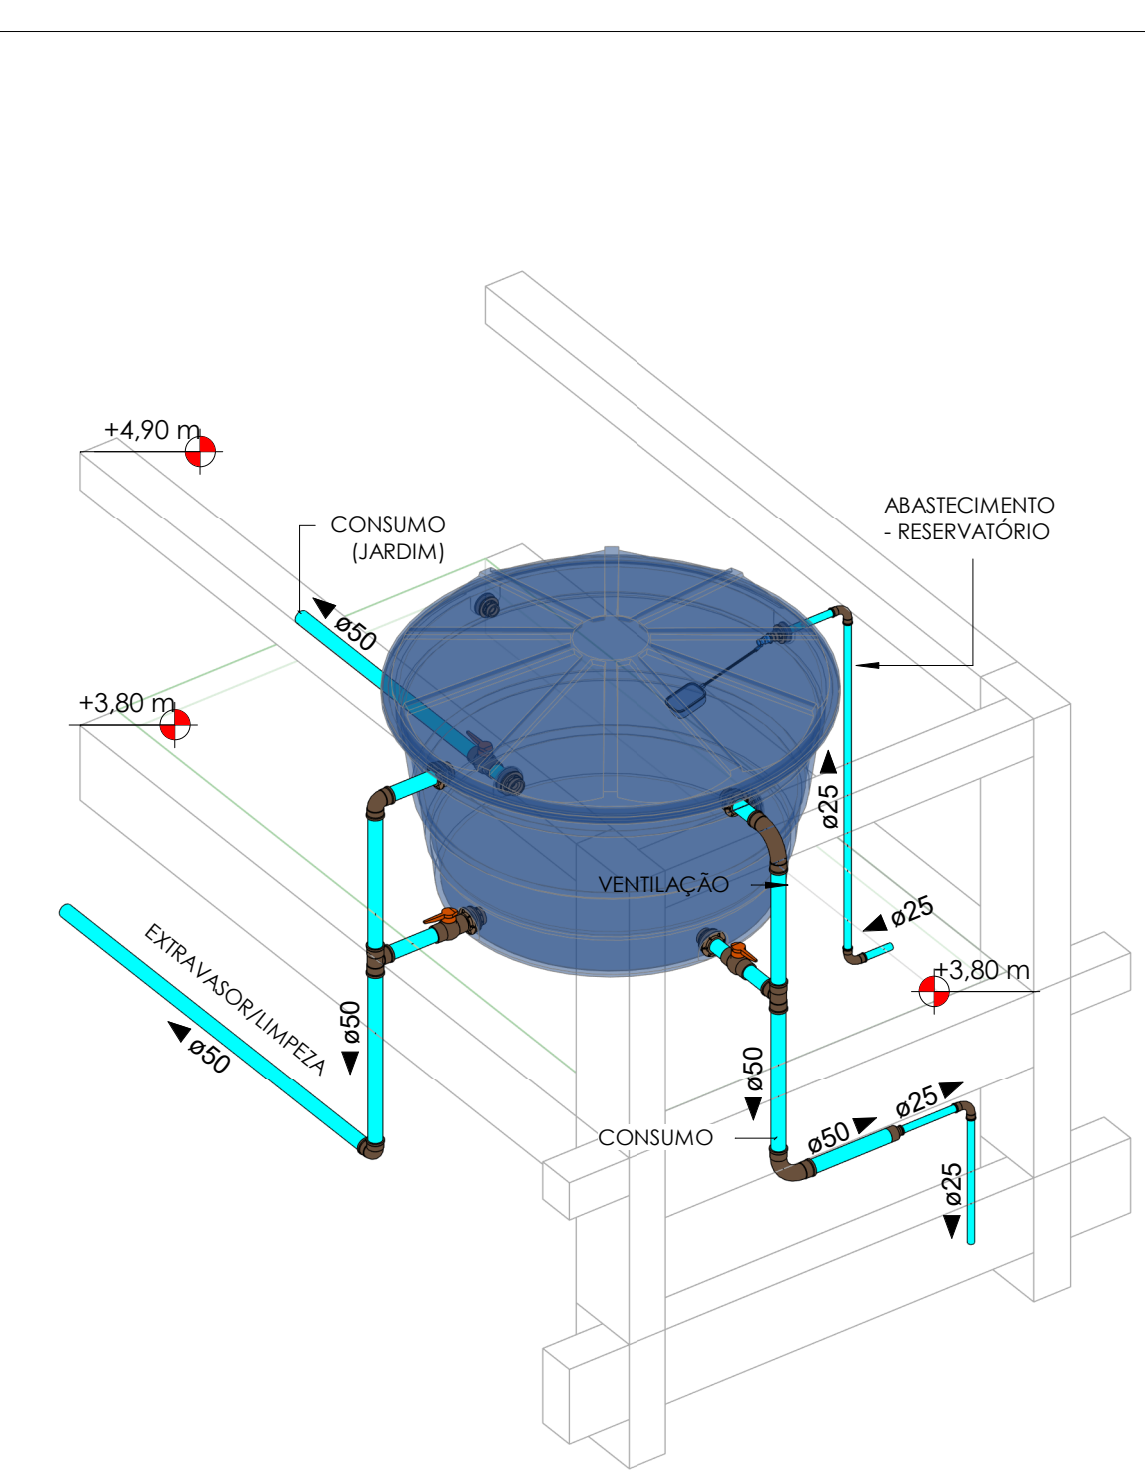


ISOMÉTRICA 02 - WC 2 - ESC 1/25

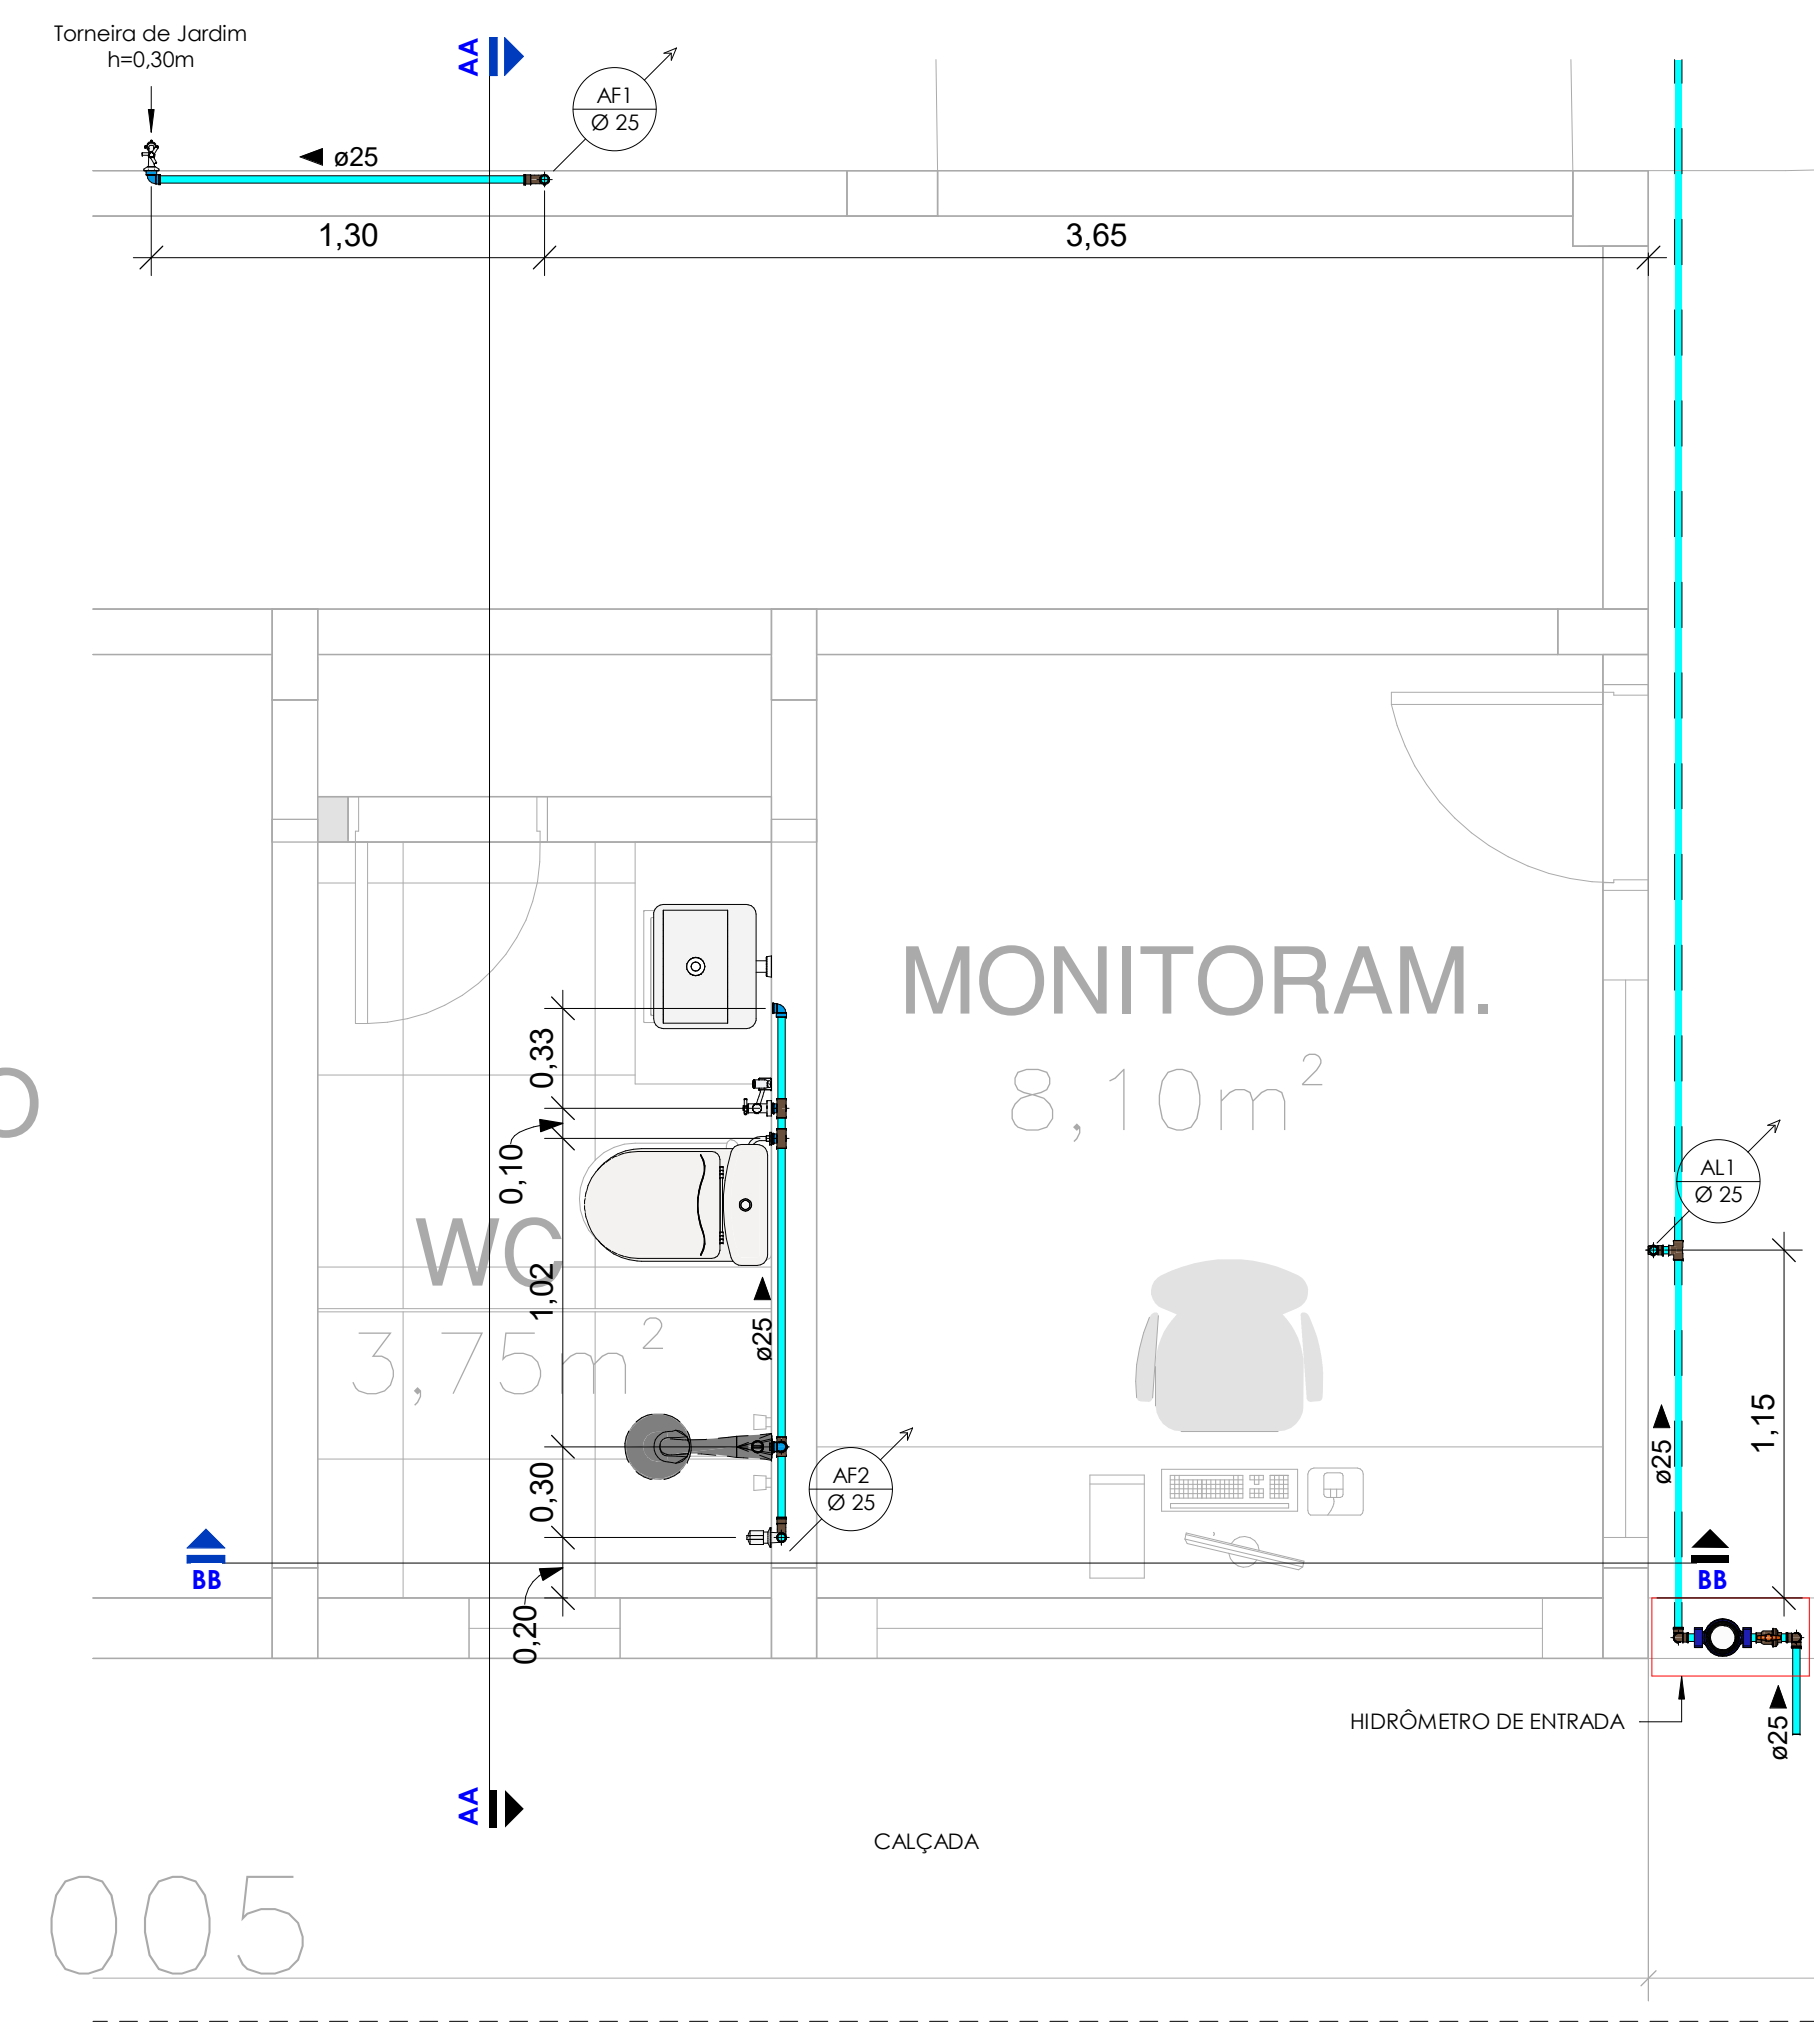

PLANTA BAIXA_ REFORMA_GARAGEM_TÉRREO_DORMITÓRIO_WC_MONITORAMENTO - ESC 1/25

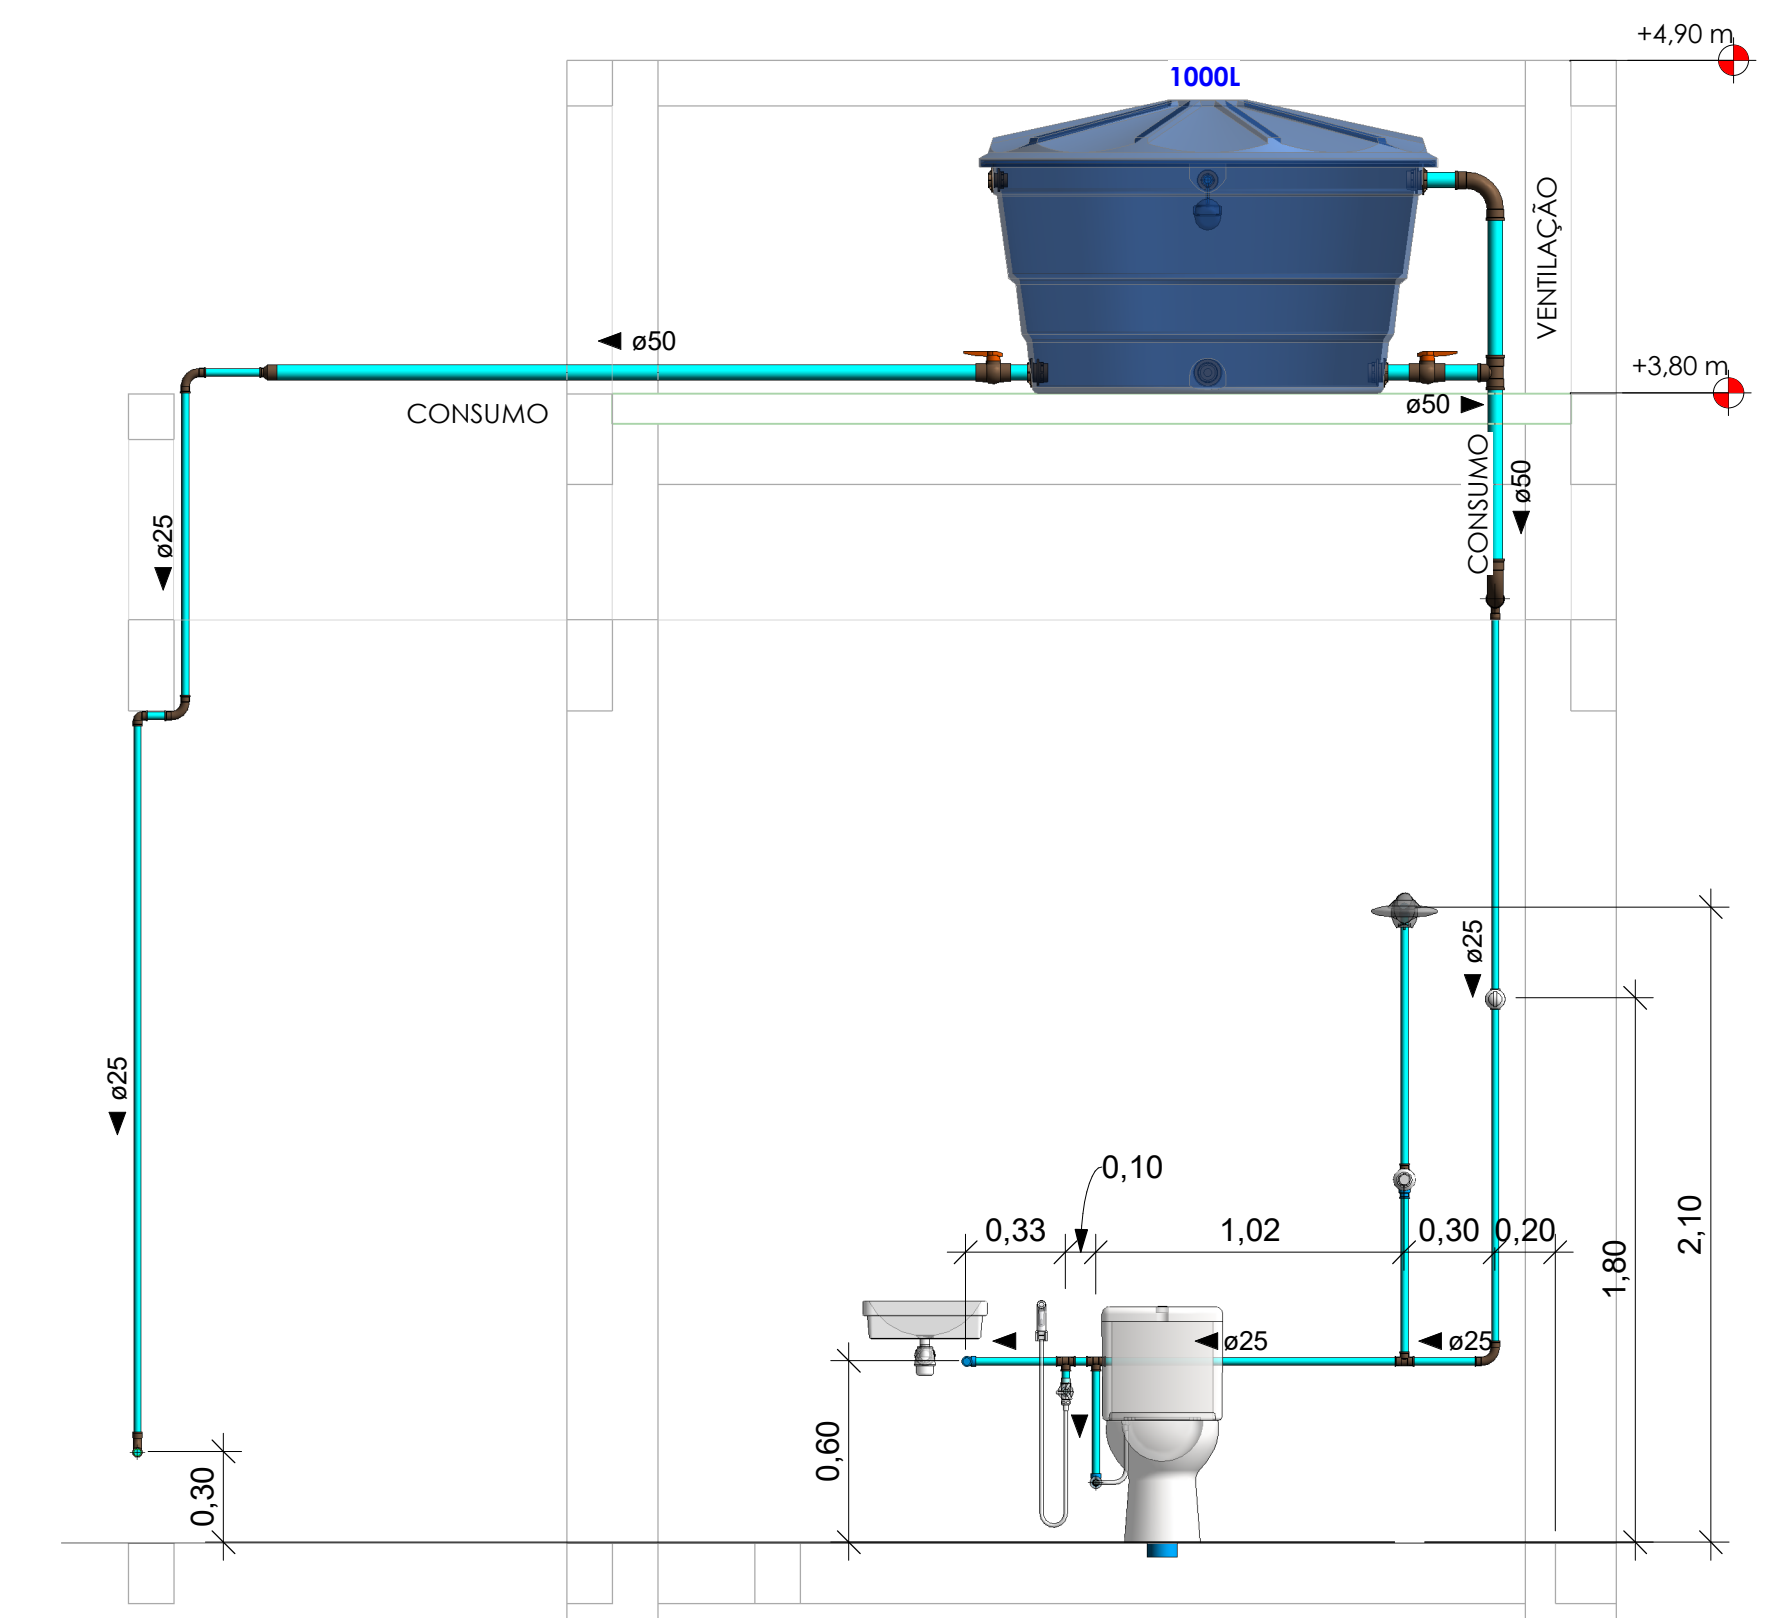

CORTE AA ESC 1/25

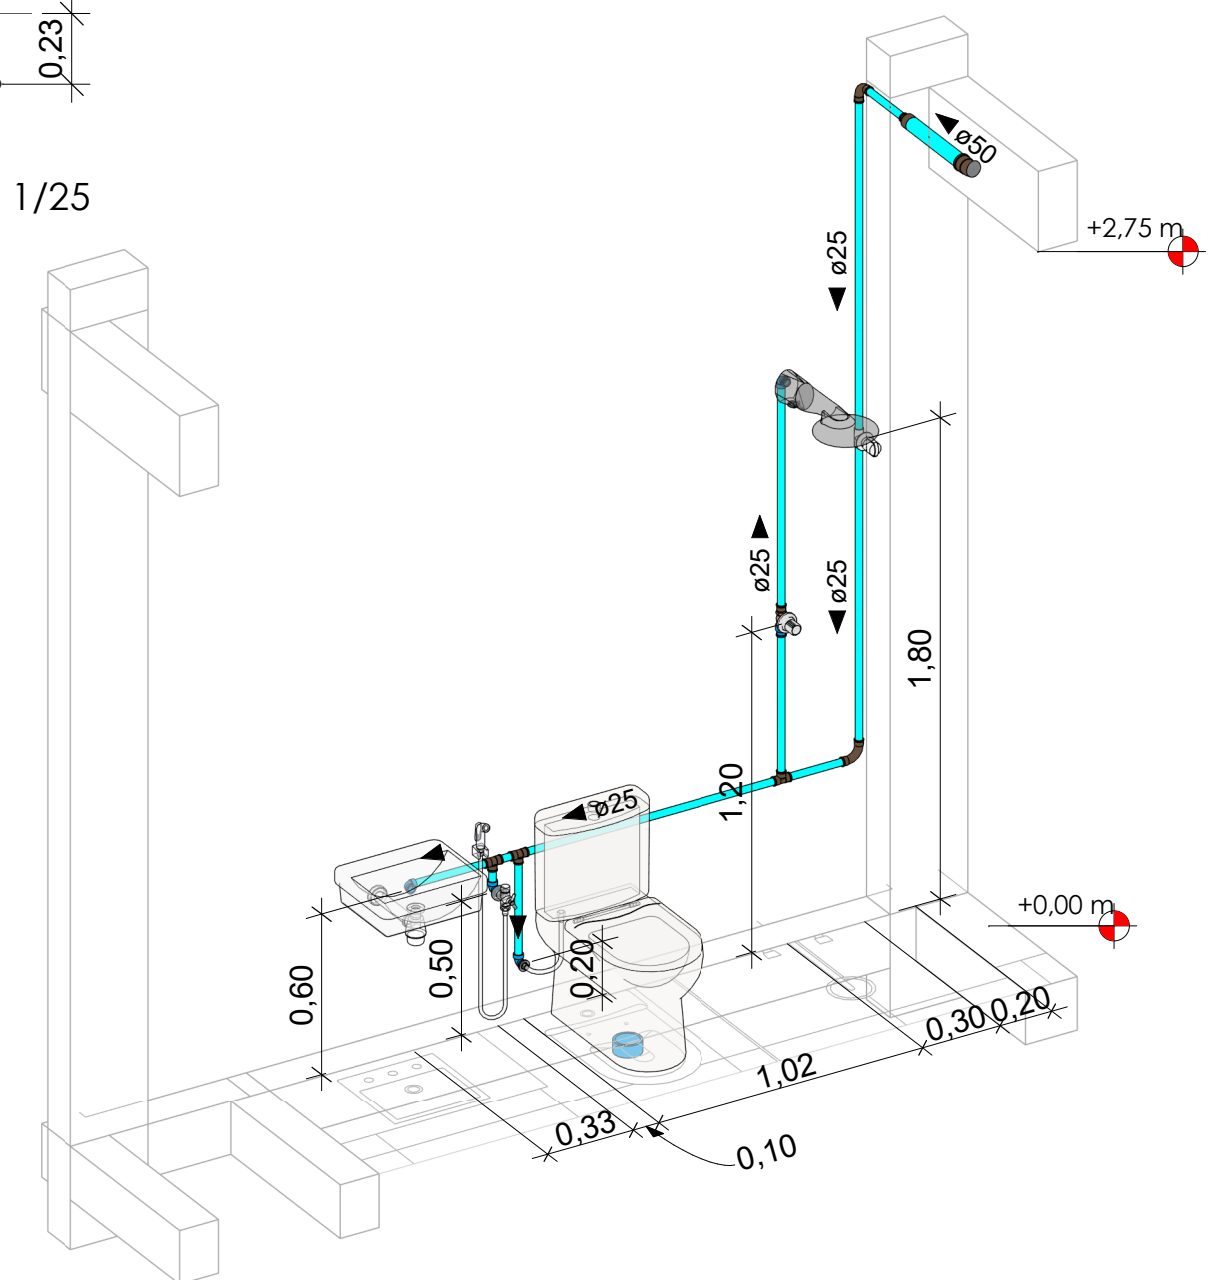

ISOMÉTRICA 01 - WC 1 - ESC 1/25

LEGENDA:

- TUBULAÇÃO PVC BRANCO - ESGOTO
- TUBULAÇÃO PVC BRANCO SN - VENTILAÇÃO ESGOTO
- TUBULAÇÃO PVC MARROM - ÁGUA FRIA
- AL-nn -ALIMENTAÇÃO DO RESERV. SUPERIOR
- CV-nn -COLUNA DE VENTILAÇÃO
- AF-nn -COLUNA DE ÁGUA FRIA (BARRILETE)

TABELA DE ALTURAS		
SIGLA	PONTO	ALTURA
CH	CHUVEIRO	2,10 m
LV	LAVATÓRIO	0,95 m
VS	VASO SANITÁRIO	0,20 m
RG	REGISTRO DE GAVETA	1,80 m
RP	REGISTRO DE PRESSÃO	1,20 m
PIA	PIA DE COZINHA	0,90 m
TQ	TANQUE	1,10 m

PROPRIETÁRIO: PRAÇA MUNICIPAL DE COREMAS - PB

LINCOLN CARTAXO DE LIRA

JUNIOR:06897861405

PROJETO: LINCOLN CARTAXO DE LIRA JÚNIOR

CREA 160.814.689-8

CONCEDENTE: PREFEITURA MUNICIPAL DE COREMAS - PB

CONVENIENTE: MUNICÍPIO DE COREMAS - PB

LOCAL: COREMAS - PB

RESPONSÁVEL TÉCNICO

RUBRICA

DADOS

DATA

17/06/2025

LINCOLN CARTAXO

CREA 160.814.689-8

CÓPIA

VISTO

PRANCHA: 02

DESCRIÇÃO: PLANTA BAIXA - CAIXA D'ÁGUA, TÉRREO

ESCALA: INDICADA

03

CORTES E ISOMÉTRICAS

Av. Gov. Flavio R. Coutinho, 500, sl. 601

Jd. Oceania, 58037-005 - João Pessoa (PB)

Tel +55 99924.4447

e-mail: contato@lclprojetos.com


Peças hidráulicas e sanitárias			
Quantidade	Descrição	Abreviatura	Tipo de sistema
1			
2	Caixa d'água de polietileno, 1000 litros - Fortlev		
2	Torneira de Boia haste ABS Fortlev 1/2"		
2	Torneira de parede para tanque e jardim com bico união plástico (B5007CKCR3), linha Celite One - Metais Celite		
2	Bacia Sanitária com Caixa Acoplada	BS (CD)	Utilização
2	Chuveiro	CH	Utilização
2	Ducha higiênica	DH	Utilização
1	Purificador de água	FI	Utilização
2	Cuba de sobrepor	Cuba de sobrepor	Utilização/Esgoto
2	Sifão para lavatório 1"x1.1/2" com tubo de 300 mm	Sifão lavatório 1x1.1/2"	Utilização/Esgoto
2	Flexível 300mm aço inox	Flexível 300mm	Água Fria

Tabela de acessório de tubo			
Descrição	Família e tipo	Contagem	/Descrição/
	Hidrometro 7m³: 7 m³/h - 1"	1	1/
Registro de Gaveta PVC Cromado 25mm - TIGRE	Registro de Gaveta - Agua Fria - MEP - Tigre: PVC Cromado - 25 mm	3	3/Registro de Gaveta PVC Cromado 25mm - TIGRE/
Registro de pressão DocolBase 3/4" - DocolBásicos	AF_Registro de Pressão: Ø3/4" (25mm)	2	2/Registro de pressão DocolBase 3/4" - DocolBásicos/
Registro Esfera VS Compacto Soldável 50mm - TIGRE	AF_Registro Esfera VS Compacto: Soldável - 50 mm	5	5/Registro Esfera VS Compacto Soldável 50mm - TIGRE/
Registro Esfera VS Soldável 25mm - TIGRE	Registro Esfera VS - Agua Fria - MEP - Tigre: Soldável - 25 mm	1	1/Registro Esfera VS Soldável 25mm - TIGRE/
Total geral: 12		12	

Tabela de conexão de tubo					
Contagem	Tigre: Descrição	Tigre: Fabricante	Tigre: Linha	Tigre: Produto	Tigre: Sistema
22					
2	Adaptador Soldável Curto com Bolsa e Rosca para Registro 25 x 3/4", PVC Marrom, Água Fria - TIGRE	© Tigre S/A	Soldável	Adaptador	Água Fria
2	Bucha de Redução Soldável Longa 50x25mm, PVC Marrom, Água Fria - TIGRE	© Tigre S/A	Soldável	Bucha de Redução	Água Fria
1	Curva 45° Soldável 25mm, PVC Marrom, Água Fria - TIGRE	© Tigre S/A	Soldável	Curva	Água Fria
16	Curva 90° Soldável 25mm, PVC Marrom, Água Fria - TIGRE	© Tigre S/A	Soldável	Curva	Água Fria
3	Curva 90° Soldável 50mm, PVC Marrom, Água Fria - TIGRE	© Tigre S/A	Soldável	Curva	Água Fria
8	Joelho 90° Soldável 25mm, PVC Marrom, Água Fria - TIGRE	© Tigre S/A	Soldável	Joelho	Água Fria
5	Joelho 90° Soldável 50mm, PVC Marrom, Água Fria - TIGRE	© Tigre S/A	Soldável	Joelho	Água Fria
12	Joelho 90° Soldável com Bucha de Latão 25 x 3/4", PVC Marrom, Água Fria - TIGRE	© Tigre S/A	Soldável	Joelho	Água Fria
10	Luva Soldável 25mm, PVC Marrom, Água Fria - TIGRE	© Tigre S/A	Soldável	Luva	Água Fria
2	Luva Soldável e com Bucha de Latão 25 x 3/4", PVC Marrom, Água Fria - TIGRE	© Tigre S/A	Soldável	Luva	Água Fria
9	Tê Soldável 25mm, PVC Marrom, Água Fria - TIGRE	© Tigre S/A	Soldável	Tê	Água Fria
4	Tê Soldável 50mm, PVC Marrom, Água Fria - TIGRE	© Tigre S/A	Soldável	Tê	Água Fria
96					

Tubos Rígidos		
Descrição	Diâmetro	Comprimento (m)
Tubo PVC Marrom - Água Fria Soldável	25 mm	105,31
Tubo PVC Marrom - Água Fria Soldável	50 mm	15,46

TABELA DE ALTURAS		
SIGLA	PONTO	ALTURA
CH	CHUVEIRO	2,10 m
LV	LAVATÓRIO	0,95 m
VS	VASO SANITÁRIO	0,20 m
RG	REGISTRO DE GAVETA	1,80 m
RP	REGISTRO DE PRESSÃO	1,20 m
PIA	PIA DE COZINHA	0,90 m
TQ	TANQUE	1,10 m

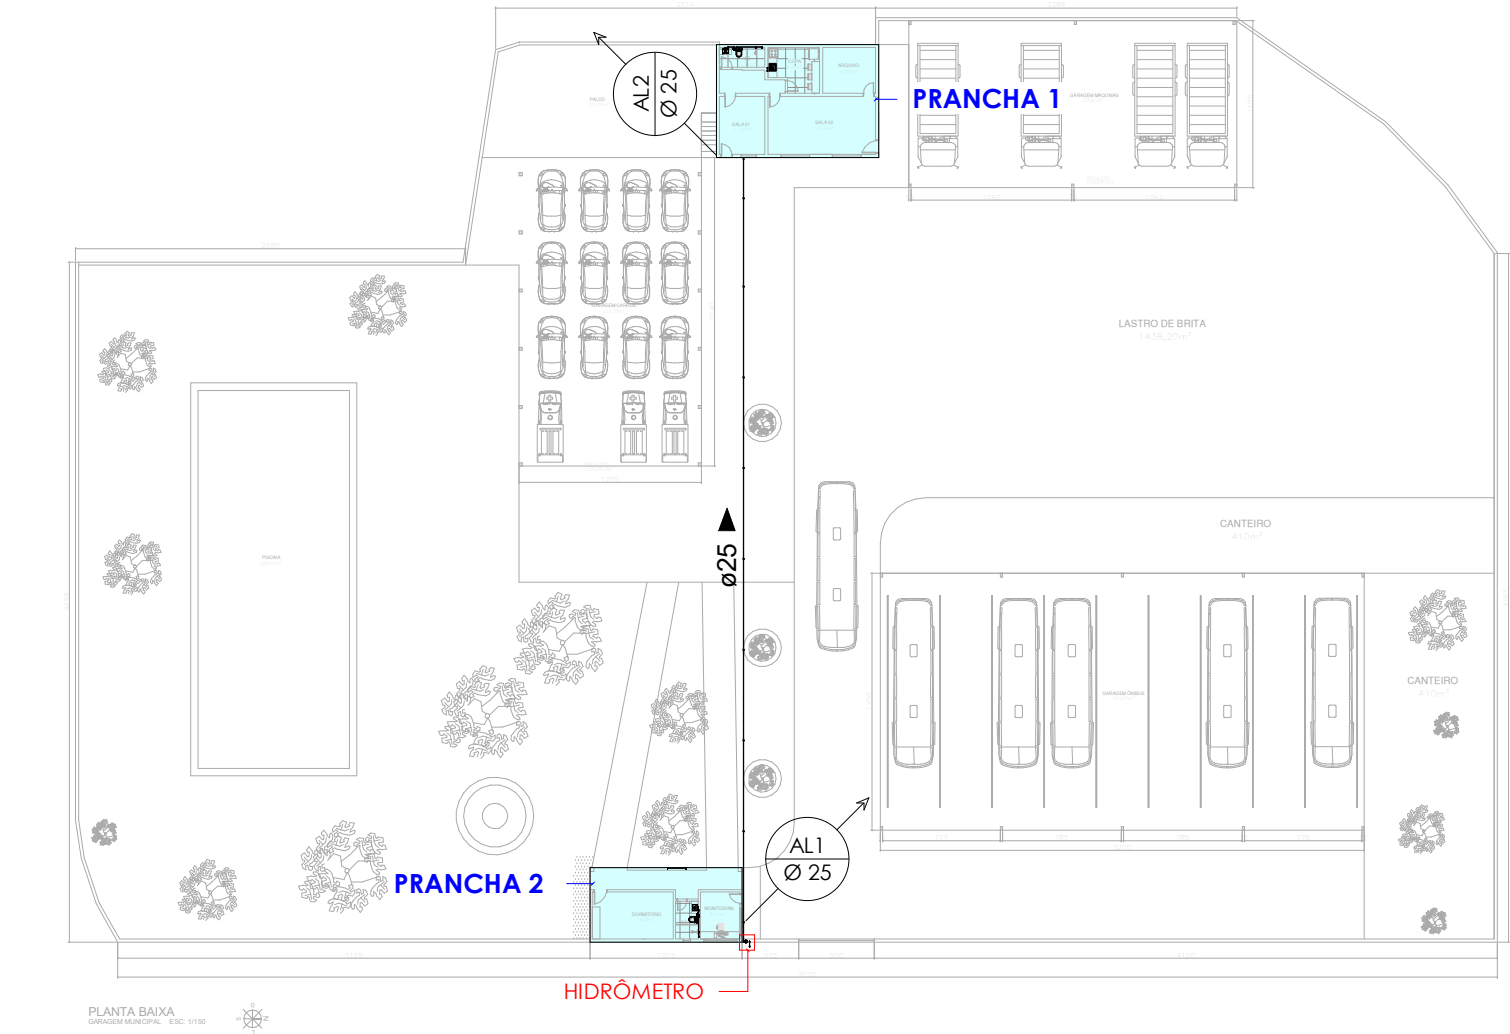

PLANTA BAIXA _REFORMA_GARAGEM_GERAL - ESC 1/500

LEGENDA:

- TUBULAÇÃO PVC BRANCO - ESGOTO
- TUBULAÇÃO PVC BRANCO SN - VENTILAÇÃO ESGOTO
- TUBULAÇÃO PVC MARROM - ÁGUA FRIA
- ALIMENTAÇÃO DO RESERV. SUPERIOR
- COLUNA DE VENTILAÇÃO
- COLUNA DE ÁGUA FRIA (BARRILETE)

PROPRIETÁRIO: PREFEITURA MUNICIPAL DE COREMAS - PB
LINCOLN CARTAXO DE LIRA JUNIOR:06897861405
Assinado de forma digital por LINCOLN CARTAXO DE LIRA JUNIOR:06897861405
Dados: 2025.08.11 14:47:18 -03'00'

PROJETO: LINCOLN CARTAXO DE LIRA JÚNIOR CREA 160.814.689-8

PROJETO: INSTALAÇÕES HIDRÁULICAS DA REFORMA DA GARAGEM DE COREMAS

CONCEDENTE: PREFEITURA MUNICIPAL DE COREMAS - PB

CONVENIENTE: MUNICÍPIO DE COREMAS - PB

LOCAL: COREMAS - PB

		RESPONSÁVEL TÉCNICO	RUBRICA	DADOS
DATA	17/06/2025	LINCOLN CARTAXO		CREA 160.814.689-8
CÓPIA				
VISTO				

PRANCHA:	DESCRIÇÃO:	ESCALA:
03 / 03	QUANTITATIVOS , PLANTA BAIXA GERAL E MAPEAMENTO DAS PRANCHAS	INDICADA



Av. Gov. Flavio R. Coutinho, 500, sl. 601
Jd. Oceania, 58037-005 - João Pessoa (PB)
Tel +55 99924.4447
e-mail: contato@lclprojetos.com