


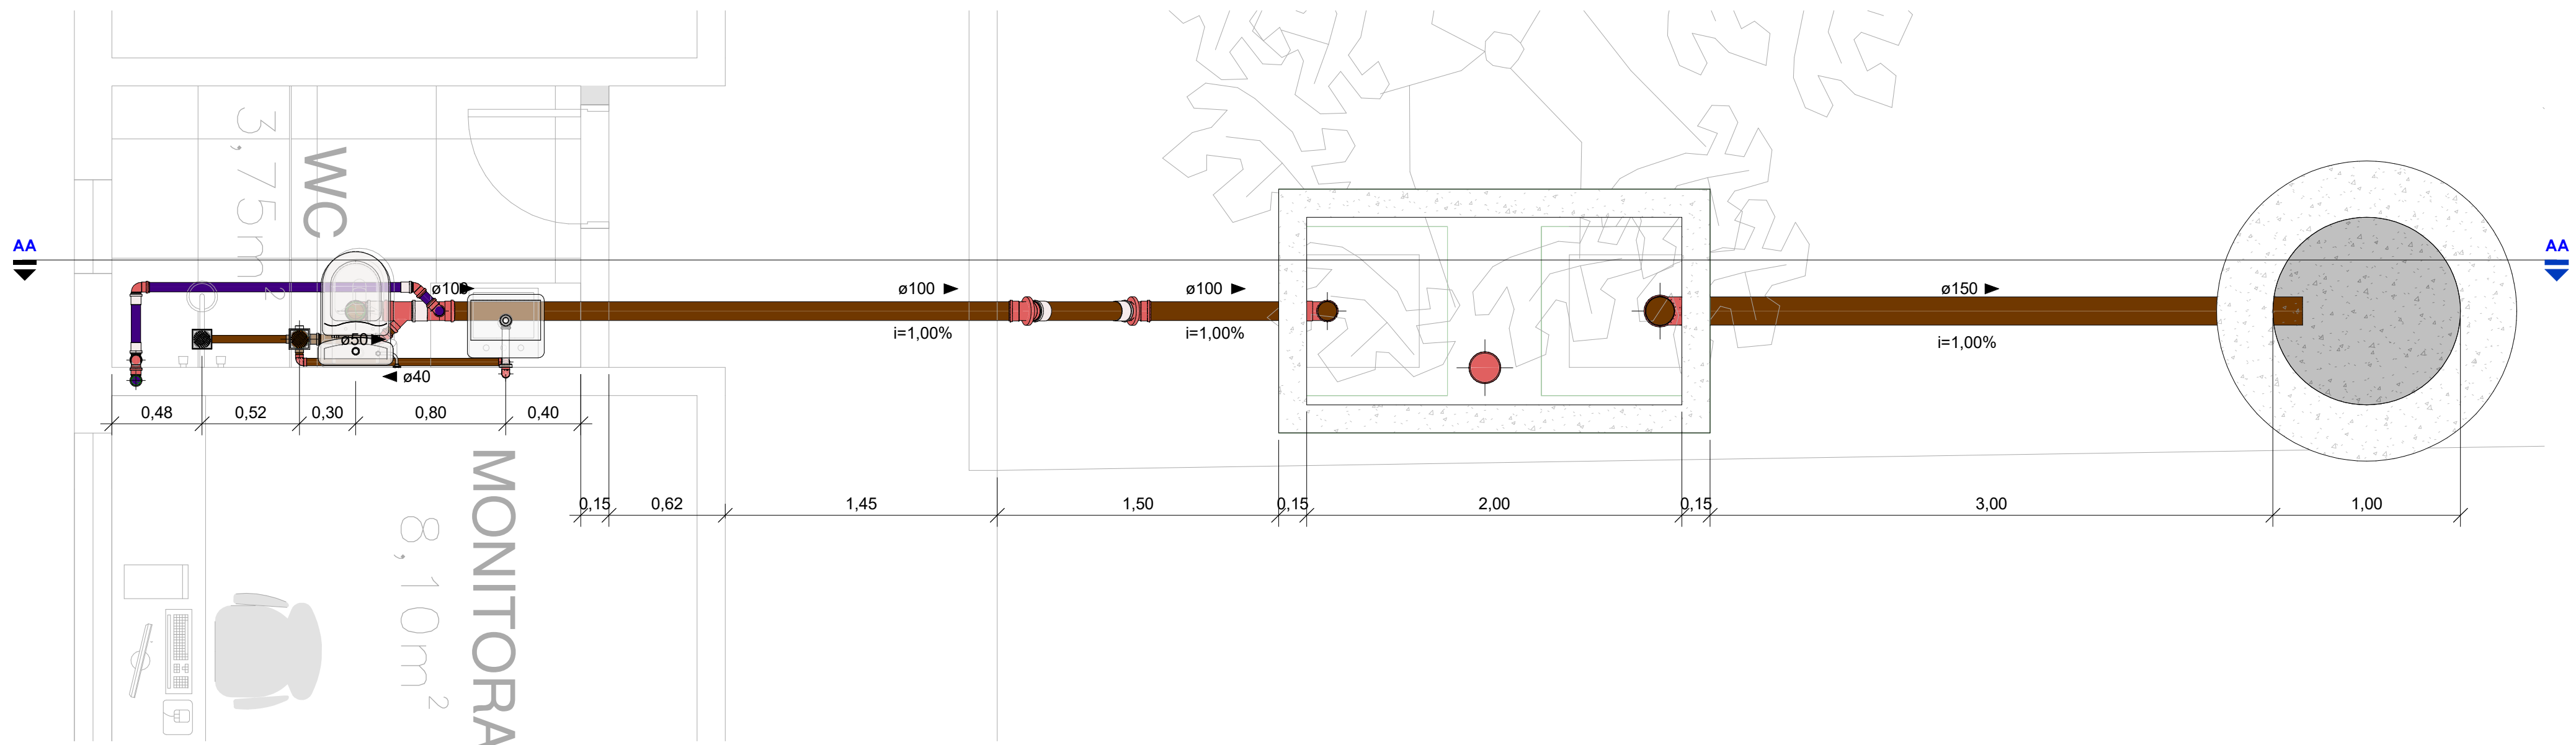

PLANTA BAIXA _DORMITÓRIO_WC_MONITORAMENTO_ - ESC

1/25

MEMORIAL TÉCNICO F.S 01

NORMAS SEGUIDAS

NBR: 13969 - Unidades de Tratamento Complementar e Disposição Final dos Efluentes Líquidos - Projeto, Construção e Operação;

NBR 17076 - Projeto de sistema de tratamento de esgoto de menor porte. Requisitos;

NBR: 7229 - Projeto, Construção e Operação de Sistemas de Tanques Sépticos

DADOS PARA ELABORAÇÃO

Número de Contribuintes (N): 5 Pessoas
Contribuição de Despejos (a): 80
Período de Detenção (T): 1,00
Intervalo de Limpeza (Anos): 1 anos
Temperatura Ambiente > 20 °C
Taxa de Acumulação de Lodo Fresco (LF): 97
Volume Mínimo (L): 1.449 L ou 1,449 m³

DIMENSÕES TANQUE SÉPTICO


B (Base): 1,00 m
L (Largura): 2,00 m
H (Altura): 1,00 m
Volume Real (L): 2.000 L ou 2,0 m³

ÁREA DE INFILTRAÇÃO SUMIDOURO

Volume de Contribuição (V): 400 L/pessoa.dia
Coeficiente de Infiltração (C1): 105,00 (Área bem selecionada e limpa, variando a areia grossa com cascalho).
Área de Infiltração Mínima (m²): 3,81 m²


DIMENSÕES SUMIDOURO

Diâmetro (m): 1,00 m
Profundidade Útil (m): 2,00 m
Dimensões: Informadas em Planta Baixa
Área de Infiltração Lateral (m²): 6,30 m²
Área de Infiltração Fundo (m²): 0,80 m²
Área de Infiltração Total (m²): 7,1 m²

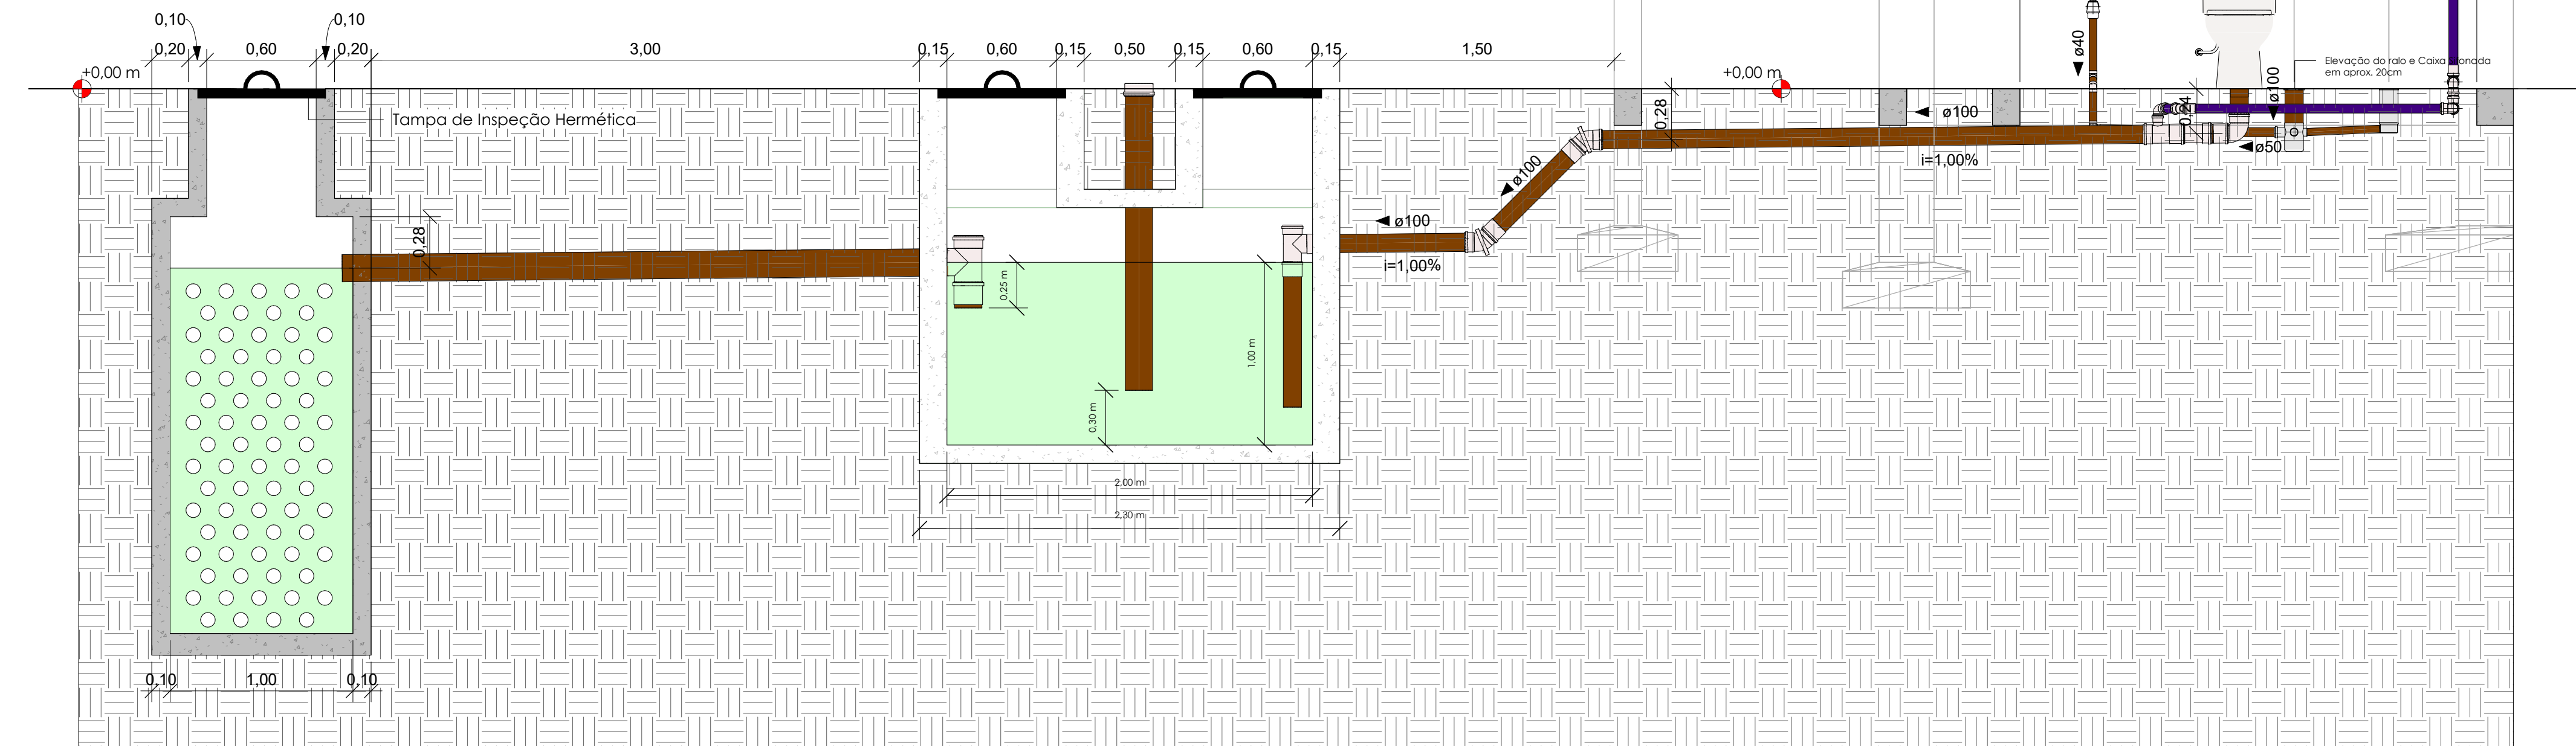

CORTE AA

ESC 1/25

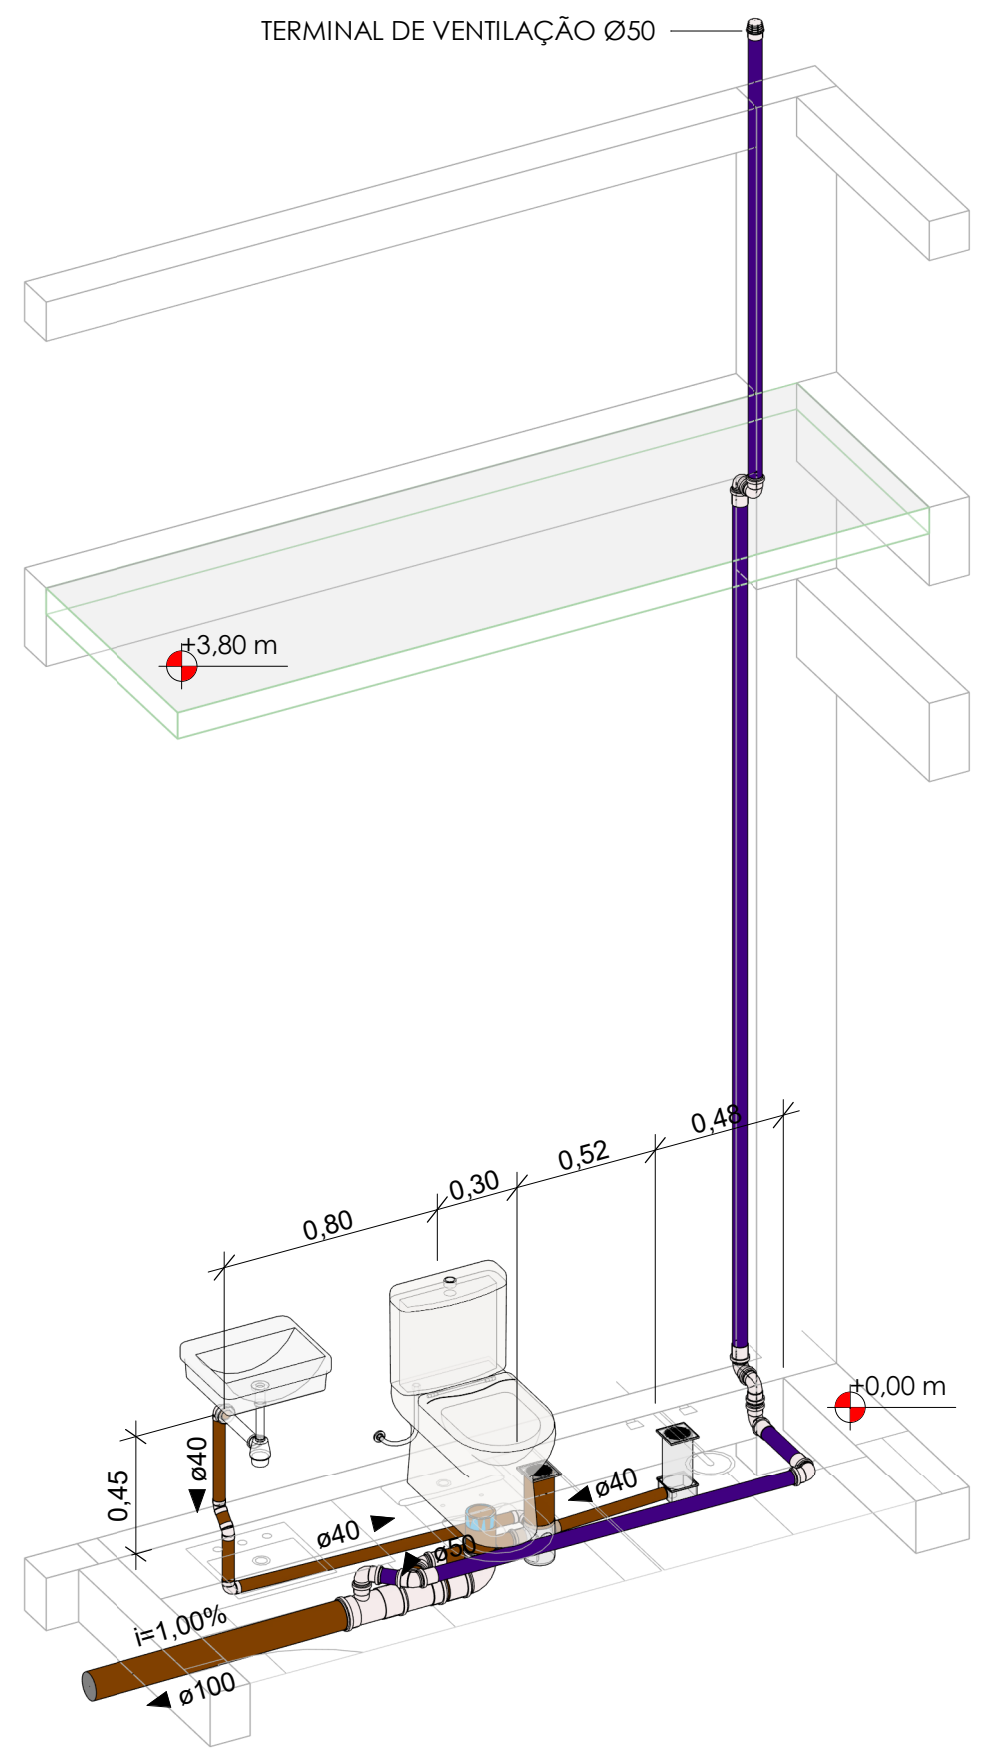

ISOMÉTRICA 02 - WC_MONITORAMENTO - ESC

1/25

LEGENDA:

- TUBULAÇÃO PVC BRANCO - ESGOTO
- TUBULAÇÃO PVC BRANCO SN - VENTILAÇÃO ESGOTO
- TUBULAÇÃO PVC MARROM - ÁGUA FRIA
- TUBO DE QUEDA DE ESGOTO
nn: número da coluna
xx: diâmetro nominal da coluna
- COLUNA DE VENTILAÇÃO
nn: número da coluna
xx: diâmetro nominal da coluna
- COLUNA DE ÁGUA FRIA (BARRILETE)
nn: número da coluna
xx: diâmetro nominal da coluna

CONFORME SUGERIDO PELA ABNT NBR 17076, É NECESSÁRIO UM ESTUDO TÉCNICO DO SOLO PARA VERIFICAÇÃO DA ABSORÇÃO DO SOLO EXISTENTE. O PRESENTE PROJETO NÃO CONTEMPLA OS DADOS DO SOLO LOCAL DESTA EMPREENDIMENTO. VISTO QUE NÃO FOI ENCAMINHADO PELA PREFEITURA, TALS CÁLCULOS AQUI DESCRITOS SÃO INTERPRETADOS COMO MODELO PADRÃO E QUE NÃO CARACTERIZAM A SITUAÇÃO REAL.

PROPRIETÁRIO: PREFEITURA MUNICIPAL DE COREMAS - PB
LINCOLN CARTAXO DE LIRA JÚNIOR
06897861405
Dados: 2025.06.19 17:30:04 -03'00'

PROJETO: LINCOLN CARTAXO DE LIRA JÚNIOR CREA 160.814.689-8


PROJETO: INSTALAÇÕES SANITÁRIAS DA REFORMA DA GARAGEM DE COREMAS
CONCEDENTE: PREFEITURA MUNICIPAL DE COREMAS - PB
CONVENIENTE: MUNICÍPIO DE COREMAS - PB
LOCAL: COREMAS - PB

DATA	19/06/2025	RESPONSÁVEL TÉCNICO	LINCOLN CARTAXO	RUBRICA	DADOS	CREA 160.814.689-8
CÓPIA						
VISTO						

PRANCHA: 01 / 03
DESCRIÇÃO: PLANTA BAIXA - DORMITÓRIO, WC, MONITOR, FOSSA E SUMIDOURO, CORTE, MEMORIAL TÉCNICO E ISOMÉTRICA
ESCALA: INDICADA




Av. Gov. Flavio R. Coutinho, 500, sl. 601
Jd. Oceania, 58037-005 - João Pessoa (PB)
Tel +55 99924.4447
e-mail: contato@lclprojetos.com

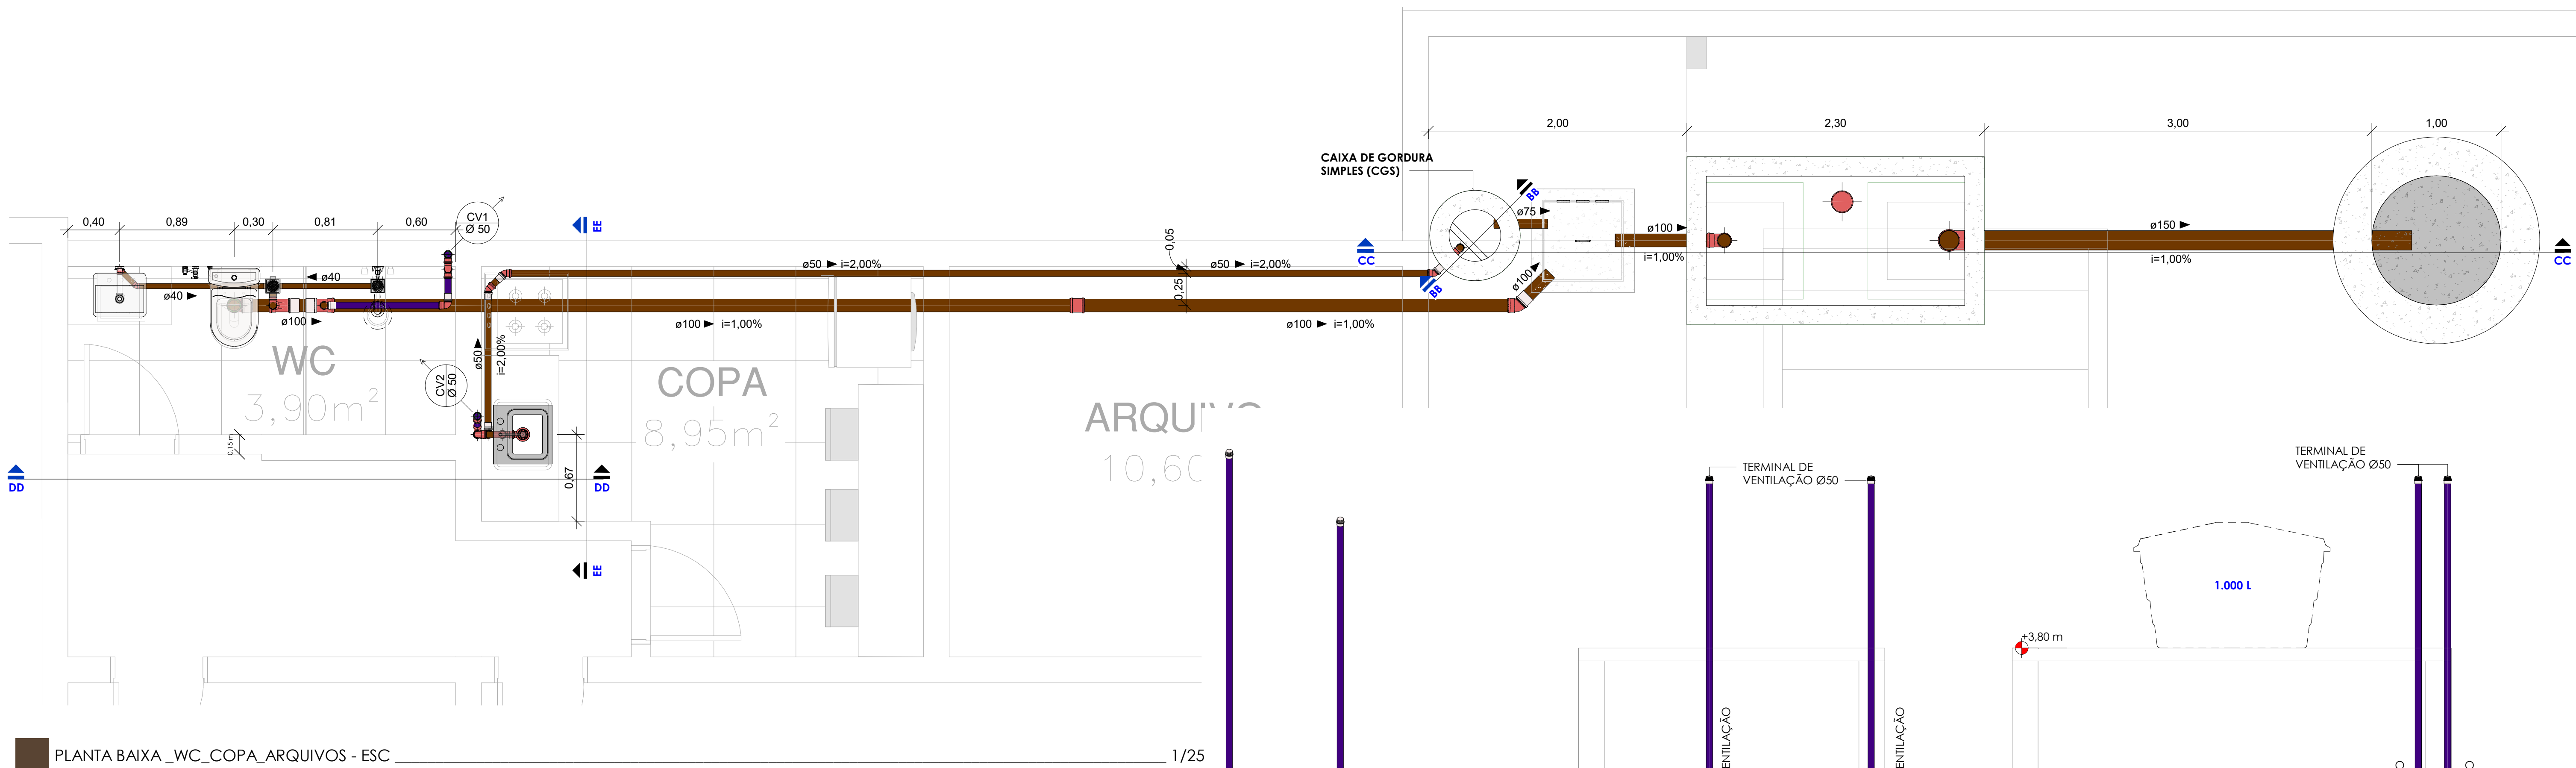


PLANTA BAIXA _WC_COPA_ARQUIVOS - ESC.

1/25

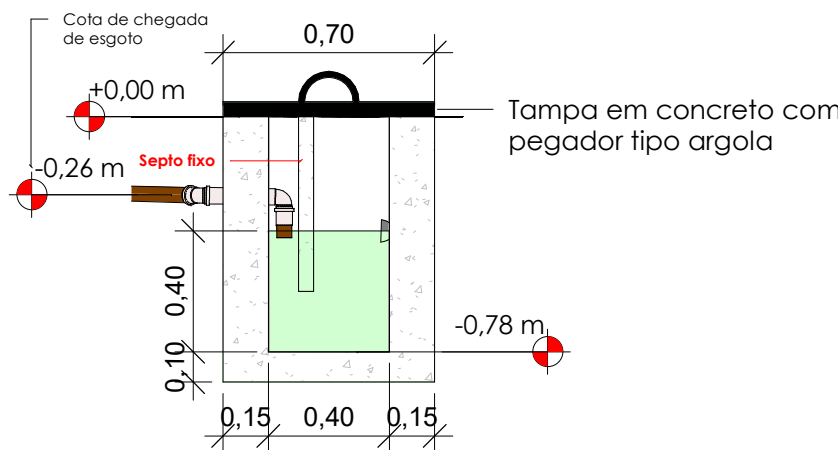


CORTE BB

ESC 1/25

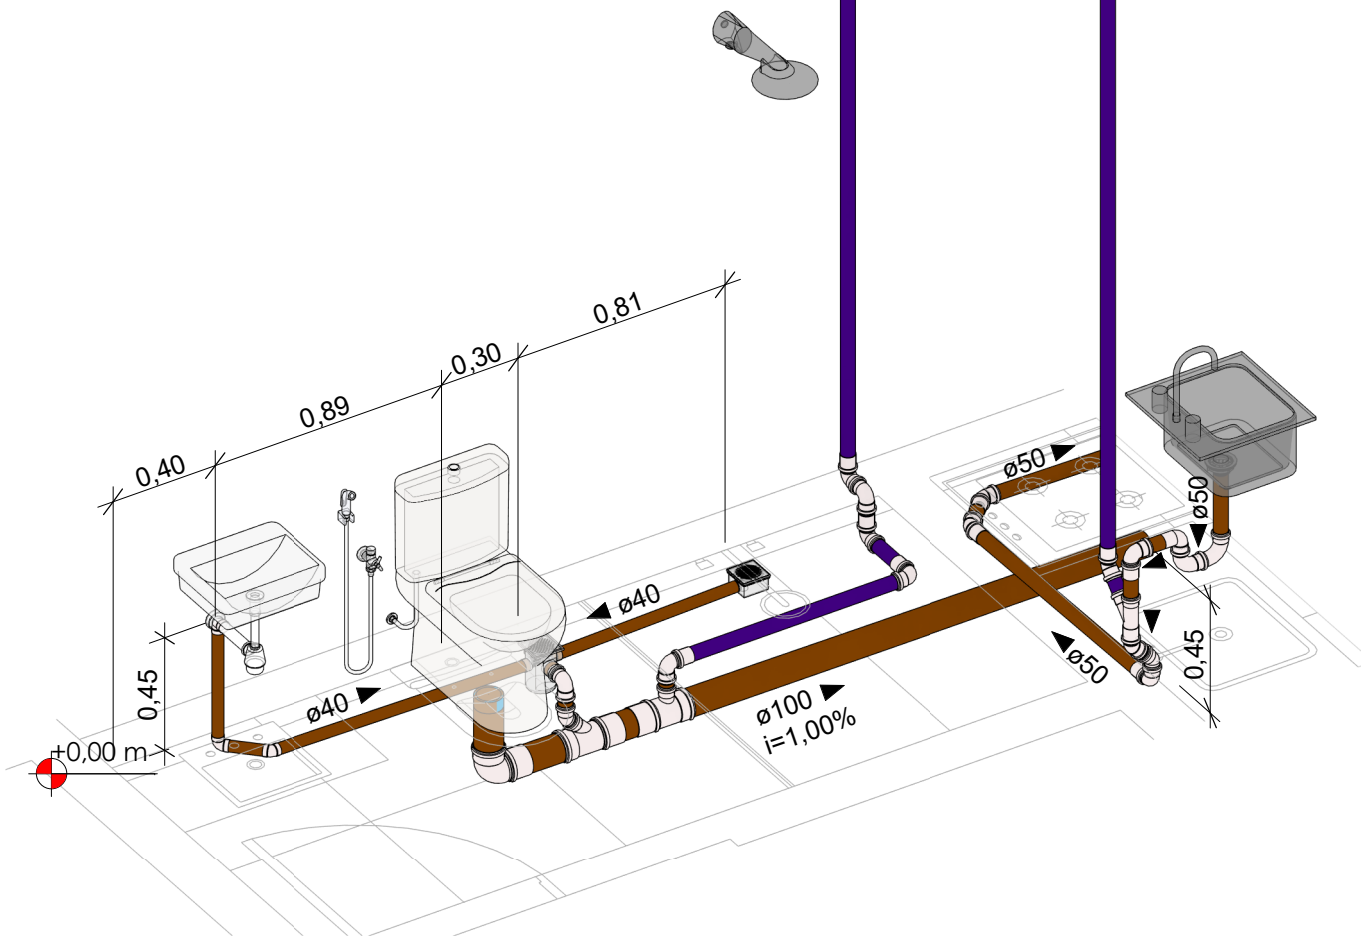


ISOMÉTRICAS 01 - WC_COPA - ESC

1/25

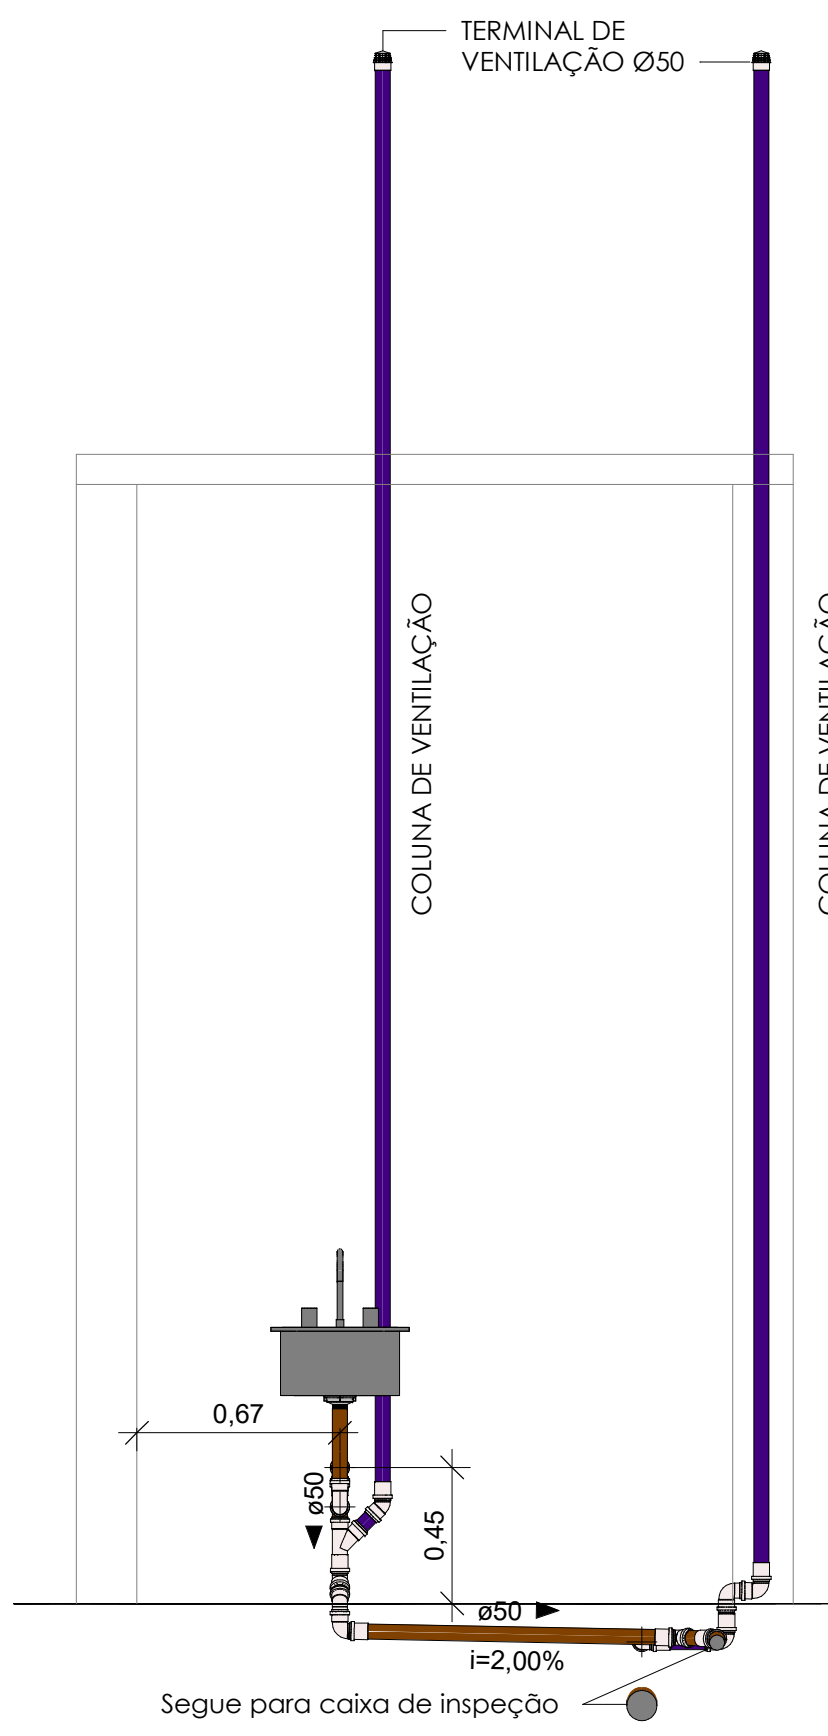

CORTE EE

ESC 1/25

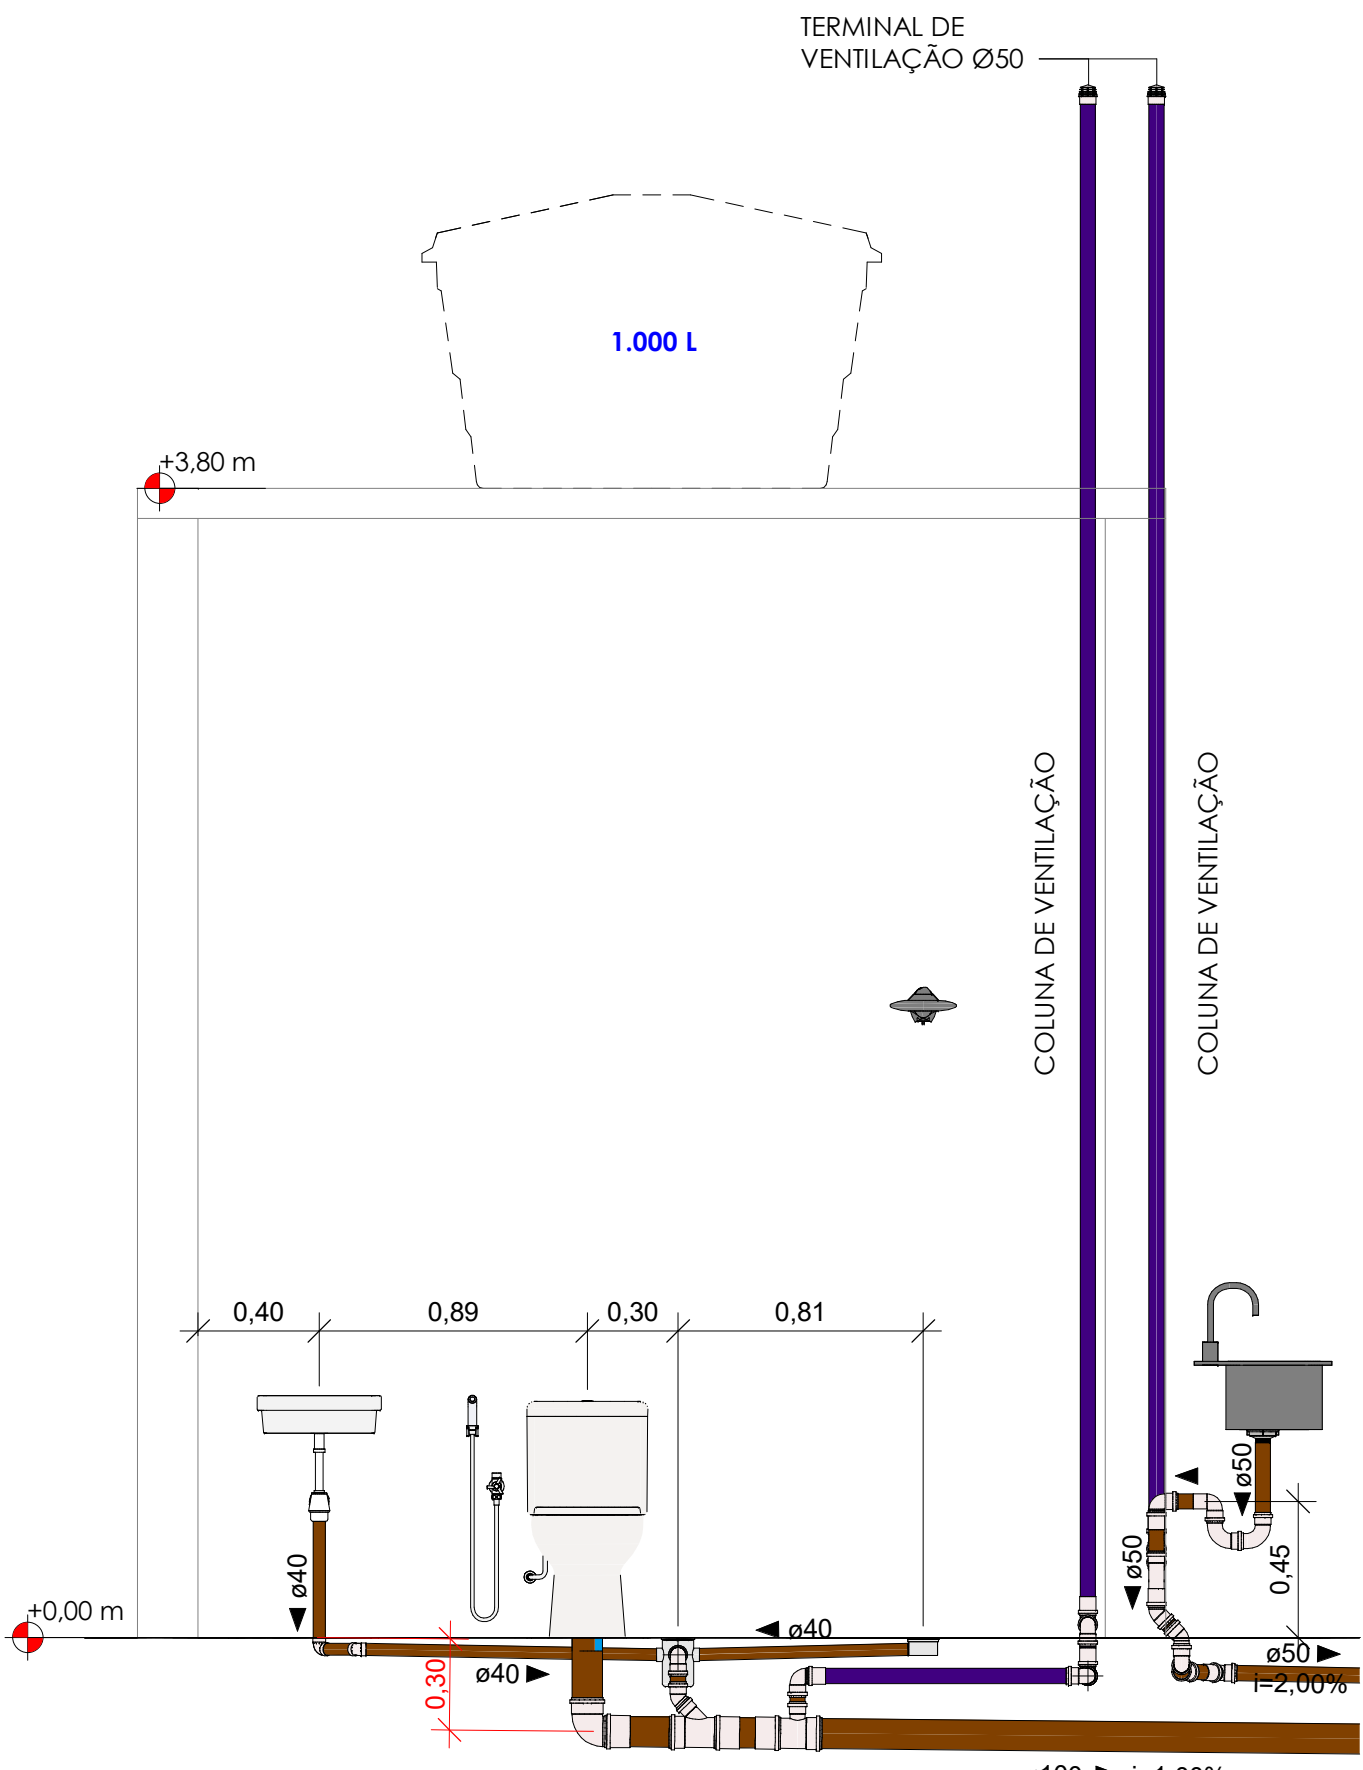

CORTE DD

ESC 1/25

MEMORIAL TÉCNICO F.S 02

NORMAS SEGUIDAS

NBR: 13969 - Unidades de Tratamento Complementar e Disposição Final dos Efluentes Líquidos - Projeto, Construção e Operação;

NBR 17076 - Projeto de sistema de tratamento de esgoto de menor porte. Requisitos;

NBR: 7229 - Projeto, Construção e Operação de Sistemas de Tanques Sépticos

DADOS PARA ELABORAÇÃO

Número de Contribuintes (N): 5 Pessoas
Contribuição de Despejos (q): 80
Período de Detenção (T): 1,00
Intervalo de Limpeza (Anos): 1 anos
Temperatura Ambiente > 20 °C
Taxa de Acumulação de Lodo Fresco (Lf): 97
Volume Mínimo (L): 1.449 L ou 1,449 m³

DIMENSÕES TANQUE SÉPTICO


B (Base): 1,00 m
L (Largura): 2,00 m
H (Altura): 1,00 m
Volume Real (L): 2.000 L ou 2,0 m³

ÁREA DE INFILTRAÇÃO SUMIDOURO

Volume de Contribuição (V): 400 L/pessoa.dia
Coeficiente de Infiltração (C1): 105,00 (Areia bem selecionada e limpa, variando a areia grossa com cascalho).
Área de Infiltração Mínima (m²): 3,81 m²

DIMENSÕES SUMIDOURO

Diâmetro (m): 1,00 m
Profundidade Útil (m): 2,00 m
Dimensões: Informadas em Planta Baixa
Área de Infiltração Lateral (m²): 6,30 m²
Área de Infiltração Fundo (m²): 0,80 m²
Área de Infiltração Total (m²): 7,1 m²

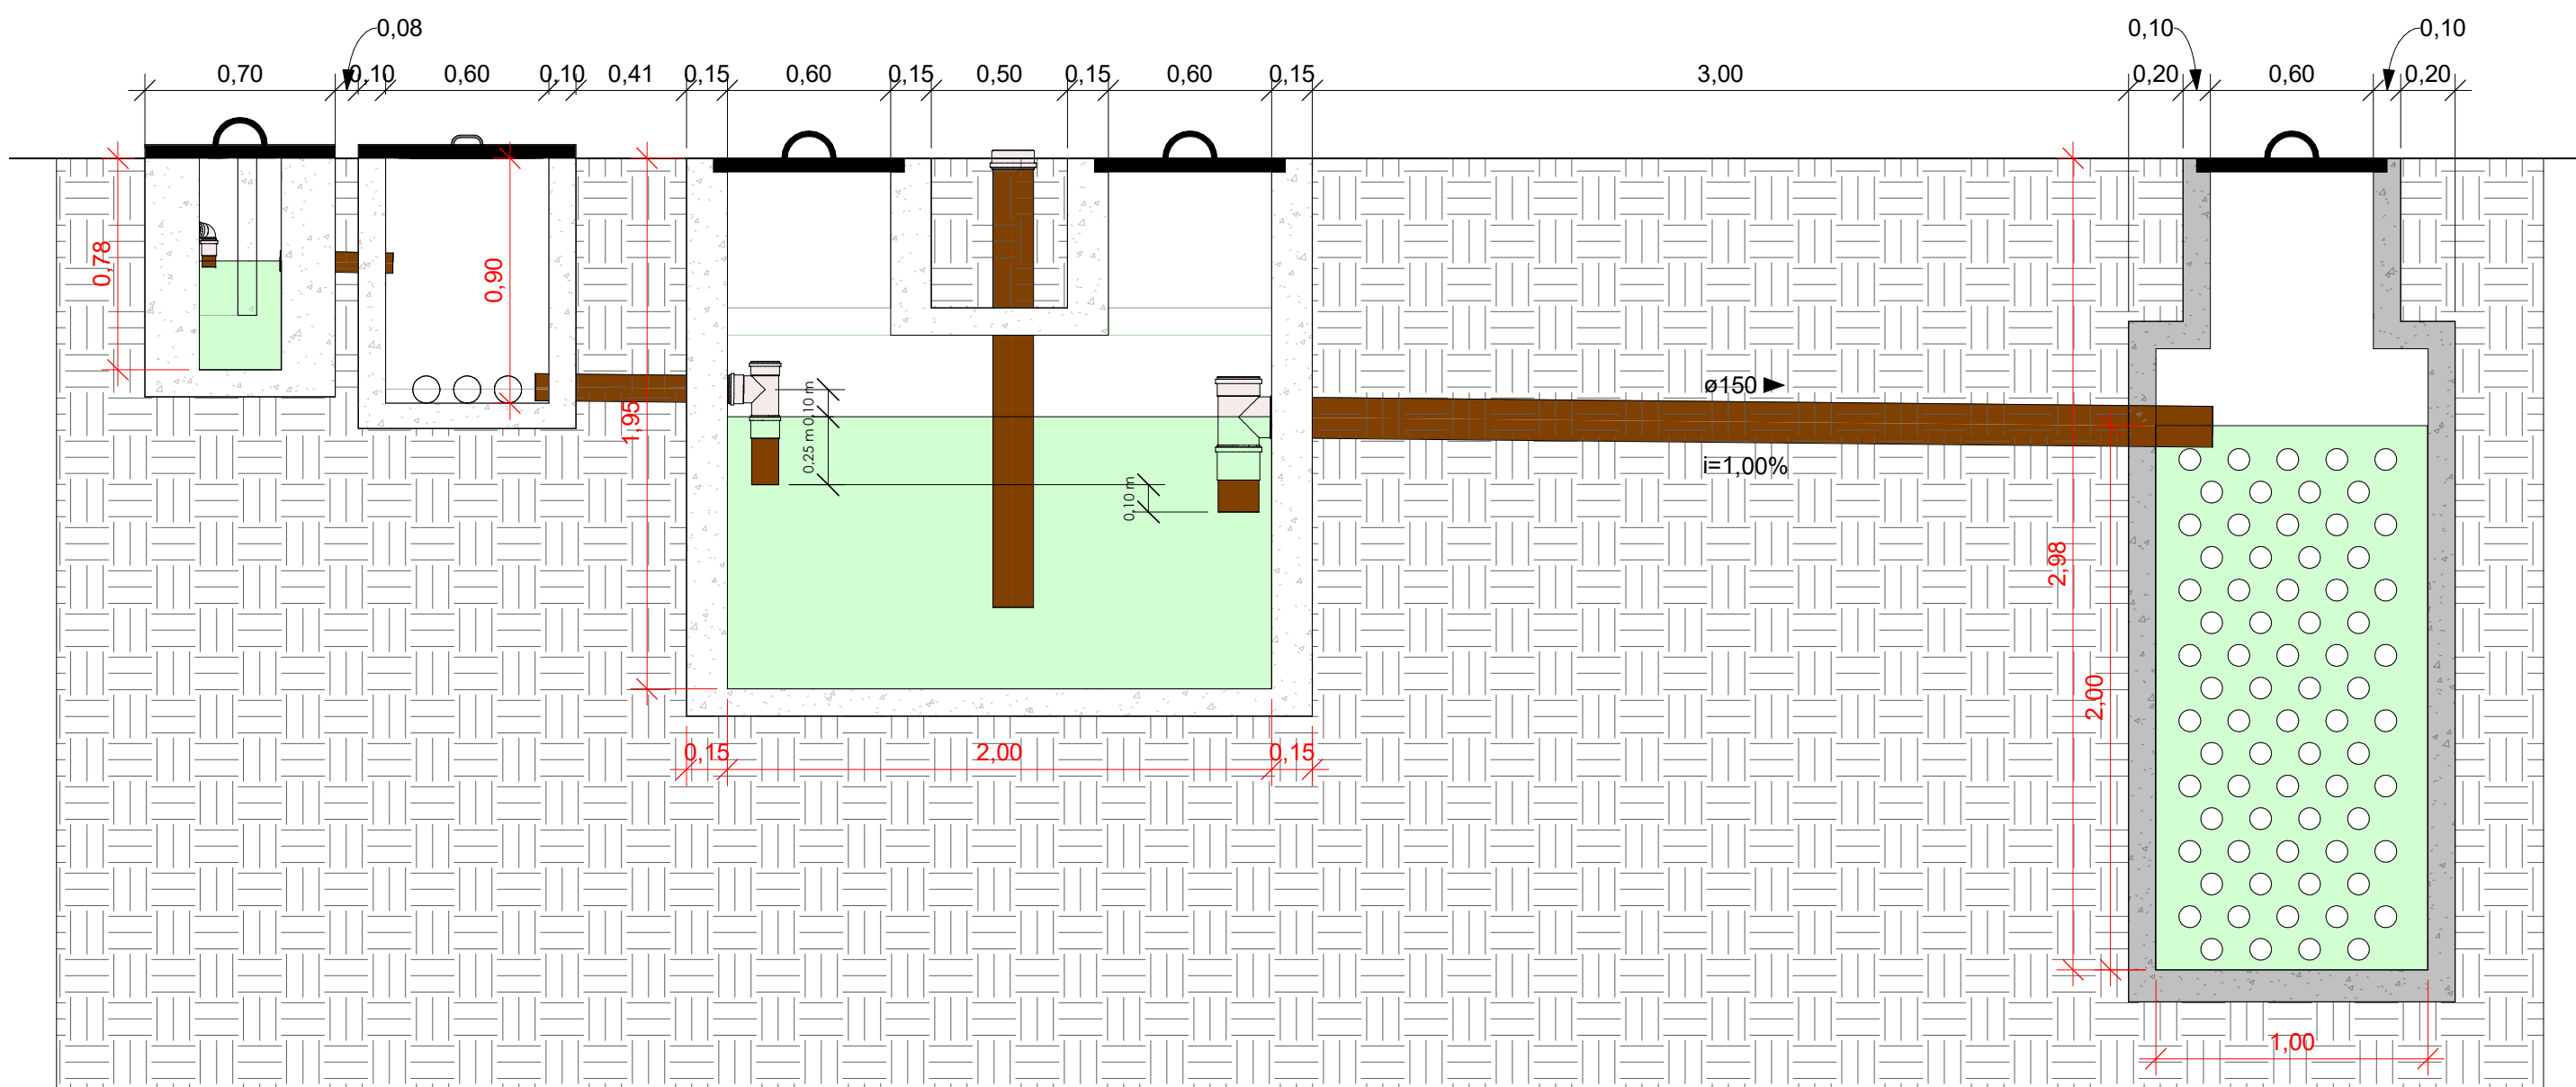

CORTE CC

ESC 1/25

CONFORME SUGERIDO PELA ABNT NBR 17076, É NECESSÁRIO UM ESTUDO TÉCNICO DO SOLO PARA VERIFICAÇÃO DA ABSORÇÃO DO SOLO EXISTENTE. O PRESENTE PROJETO NÃO CONTEMPLA OS DADOS DO SOLO LOCAL DESTA EMPREENDIMENTO. VISTO QUE NÃO FOI ENCAMINHADO PELA PREFEITURA, TALS CÁLCULOS AQUI DESCRITOS SÃO INTERPRETADOS COMO MODELO PADRÃO E QUE NÃO CARACTERIZAM A SITUAÇÃO REAL.

PROPRIETÁRIO: PREFEITURA MUNICIPAL DE COREMAS - PB
LINCOLN CARTAXO DE LIRA JÚNIOR:06897861405
Assinado de forma digital por LINCOLN CARTAXO DE LIRA JÚNIOR:06897861405
Dados: 2025.06.19 17:29:33 -03'00'

PROJETO: LINCOLN CARTAXO DE LIRA JÚNIOR CREA 160.814.689-8

PROJETO: INSTALAÇÕES SANITÁRIAS DA REFORMA DA GARAGEM DE COREMAS

CONCEDENTE: PREFEITURA MUNICIPAL DE COREMAS - PB

CONVENIENTE: MUNICÍPIO DE COREMAS - PB

LOCAL: COREMAS - PB

DATA	RESPONSÁVEL TÉCNICO	RUBRICA	DADOS
19/06/2025	LINCOLN CARTAXO		CREA 160.814.689-8
CÓPIA	CONVÊNIO	SICOMV	

PRANCHA:	DESCRIÇÃO:	ESCALA:
02 /03	PLANTA BAIXA - WC, COPA E ARQUIVO FOSSA E SUMIDOURO, CORTES, MEMORIAL TÉCNICO E ISOMÉTRICA	INDICADA



Av. Gov. Flavio R. Coutinho, 500, sl. 601
Jd. Oceania, 58037-005 - João Pessoa (PB)
Tel +55 99924.4447
e-mail: contato@lclprojetos.com

Peças hidráulicas e sanitárias	
Quantidade	Descrição
1	
2	Antiespuma 100 mm, Esgoto - TIGRE
2	Caixa Sifonada Montada com Grelha e Porta Grelha Quadrados Brancos 100 x 150 x 50mm, Esgoto - TIGRE
2	Porta Grelha Quadrado p/ Grelha Quadrada Branca 100mm, Esgoto - TIGRE
2	Prolongamento p/ Caixa Sifonada 100 x 100mm, Esgoto - TIGRE
2	Ralo Quadrado Montado - Branco c/ grelha branca 100x53x40mm, Esgoto - TIGRE
1	Caixa de Inspeção de Alvenaria - Dimensões internas de 60x60cm
2	Bacia Sanitária com Caixa Acoplada
1	Chuveiro
1	Ducha higiênica
2	Cuba de sobrepor
2	Sifão para lavatório 1"x1.1/2" com tubo de 300 mm
2	Flexível 300mm aço inox

Tabela de conexão de tubo GUARITA					
Contagem	Tigre: Descrição	Tigre: Fabricante	Tigre: Linha	Tigre: Produto	Tigre: Sistema

2					
2	Cap 150mm, Esgoto Série Normal - TIGRE	© Tigre S/A	Série Normal	Cap	Esgoto
2	Curva 90° Curta 50mm, Esgoto Série Normal - TIGRE	© Tigre S/A	Série Normal	Curva 90°	Esgoto
2	Curvar 45° 100mm, Esgoto Série Normal - TIGRE	© Tigre S/A	Série Normal	Curvar	Esgoto
3	Joelho 45° 40mm, Esgoto Série Normal - TIGRE	© Tigre S/A	Série Normal	Joelho	Esgoto
9	Joelho 45° 50mm, Esgoto Série Normal - TIGRE	© Tigre S/A	Série Normal	Joelho	Esgoto
1	Joelho 45° 100mm, Esgoto Série Normal - TIGRE	© Tigre S/A	Série Normal	Joelho	Esgoto
5	Joelho 90° 40mm, Esgoto Série Normal - TIGRE	© Tigre S/A	Série Normal	Joelho	Esgoto
17	Joelho 90° 50mm, Esgoto Série Normal - TIGRE	© Tigre S/A	Série Normal	Joelho	Esgoto
2	Joelho 90° 100mm, Esgoto Série Normal - TIGRE	© Tigre S/A	Série Normal	Joelho	Esgoto
1	Junção Simples 50 x 50mm, Esgoto Série Normal - TIGRE	© Tigre S/A	Série Normal	Tê/Junção	Esgoto
2	Junção Simples 100 x 50mm, Esgoto Série Normal - TIGRE	© Tigre S/A	Série Normal	<varia>	Esgoto
1	Luva de Correr 100mm, Esgoto Série Normal - TIGRE	© Tigre S/A	Série Normal	Luva	Esgoto
18	Luva Simples 50mm, Esgoto Série Normal - TIGRE	© Tigre S/A	Série Normal	Luva	Esgoto
10	Luva Simples 100mm, Esgoto Série Normal - TIGRE	© Tigre S/A	Série Normal	Luva	Esgoto
2	Luva Simples 150mm, Esgoto Série Normal - TIGRE	© Tigre S/A	Série Normal	Luva	Esgoto
3	Terminal de Ventilação 50mm, Esgoto Série Normal - TIGRE	© Tigre S/A	Série Normal	Terminal	Esgoto
2	Tê 100 x 50mm, Esgoto Série Normal - TIGRE	© Tigre S/A	Série Normal	Tê/Junção	Esgoto
2	Tê 100 x 100mm, Esgoto Série Normal - TIGRE	© Tigre S/A	Série Normal	Tê/Junção	Esgoto
2	Tê 150 x 150mm, Esgoto Série Normal - TIGRE	© Tigre S/A	Série Normal	Tê/Junção	Esgoto

Caixas - Ralos - Complementos			
Quantidade	Descrição	Tipo de sistema	Fabricante
1	Caixa de Inspeção de Alvenaria - Dimensões internas de 60x60cm	Inspeção/ Esgoto	Moldada In Loco

Tubos de PVC Rígidos para Esgoto - Guarita	
Diâmetro	Comprimento (m)

40 mm	4,36
50 mm	28,17
75 mm	0,42
100 mm	17,08
150 mm	10,39

Conexões - Esgoto	
Quantidade	Descrição
2	Anel de vedação para Vaso Sanitário


LEGENDA:

- TUBULAÇÃO PVC BRANCO - ESGOTO
- TUBULAÇÃO PVC BRANCO SN - VENTILAÇÃO ESGOTO
- TUBULAÇÃO PVC MARROM - ÁGUA FRIA
- TQ-nn
Øxx


-TUBO DE QUEDA DE ESGOTO
nn: número da coluna
xx: diâmetro nominal da coluna
- CV-nn
Øxx

-COLUNA DE VENTILAÇÃO
nn: número da coluna
xx: diâmetro nominal da coluna
- AF-nn
Øxx


-COLUNA DE ÁGUA FRIA (BARRILETE)
nn: número da coluna
xx: diâmetro nominal da coluna

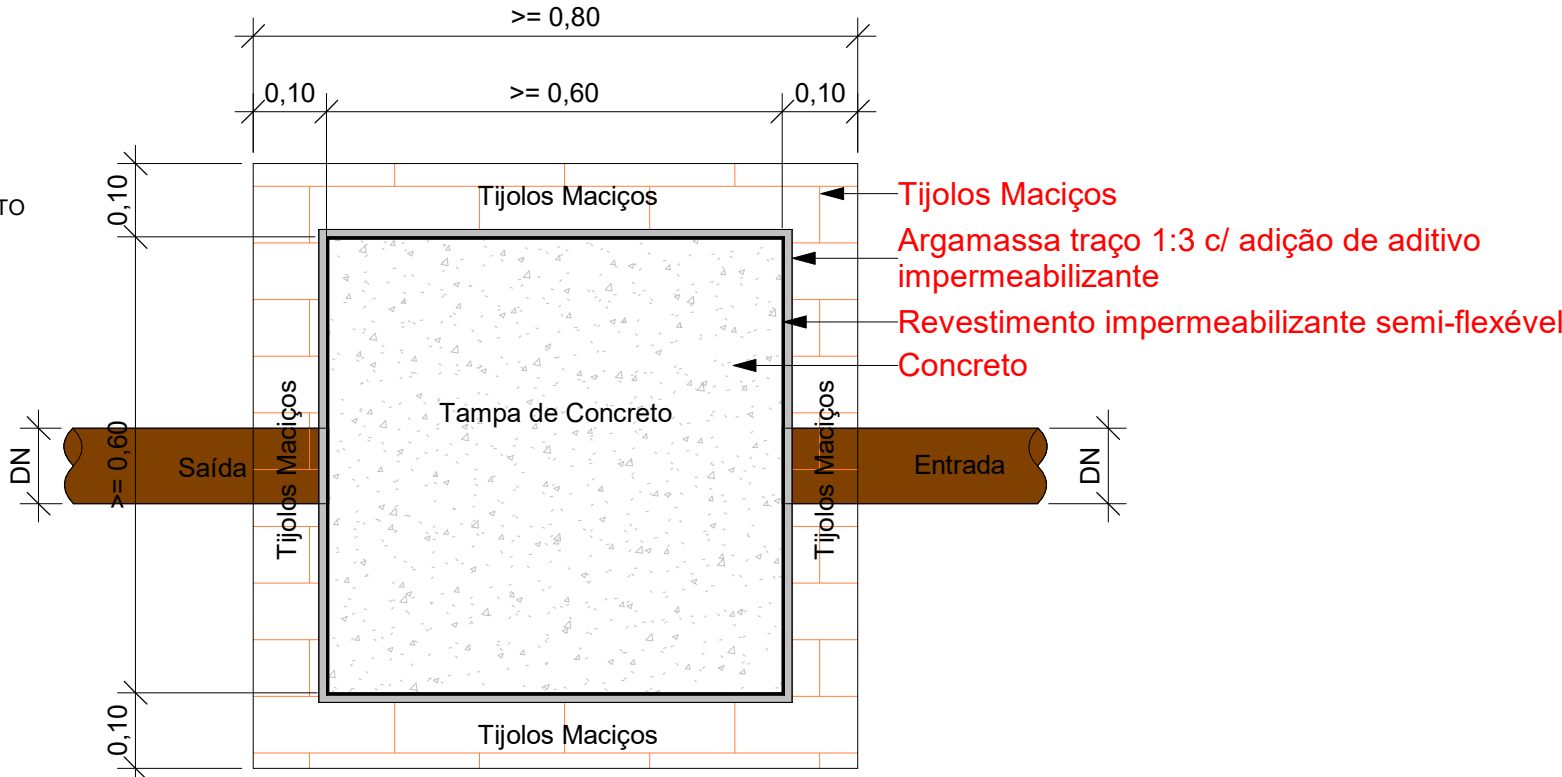

Planta Baixa - Caixa de inspeção
1 : 10

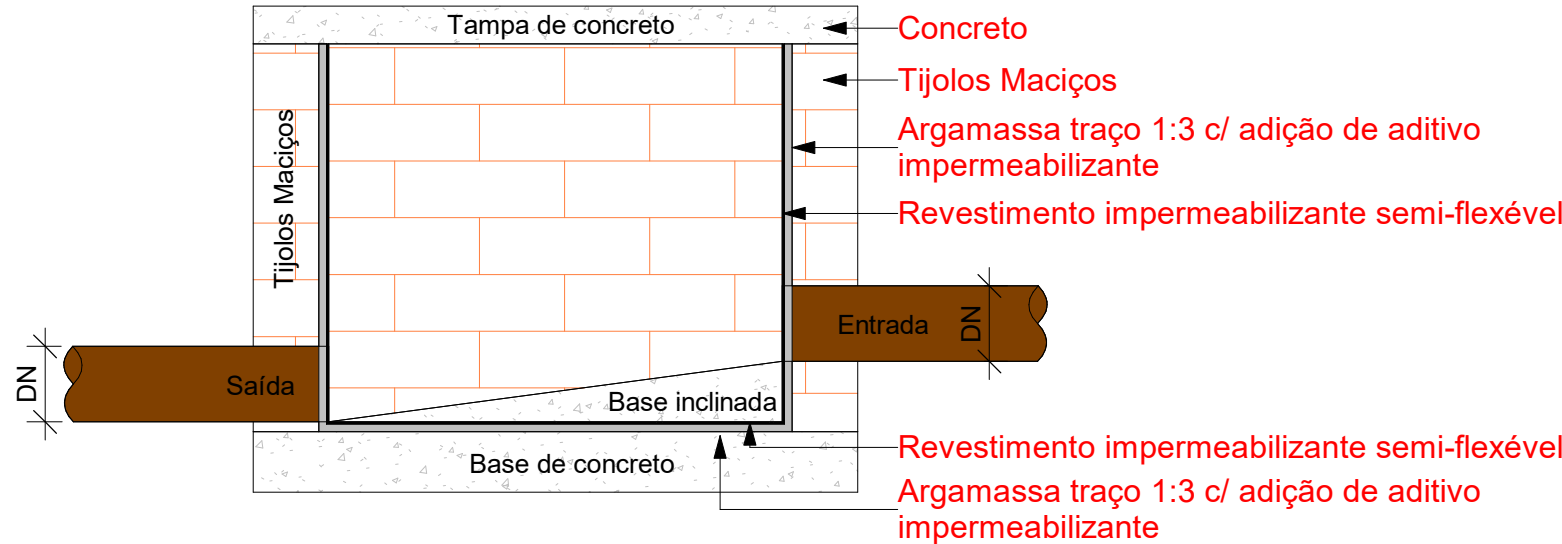

Corte lateral - Caixa de inspeção
1 : 10

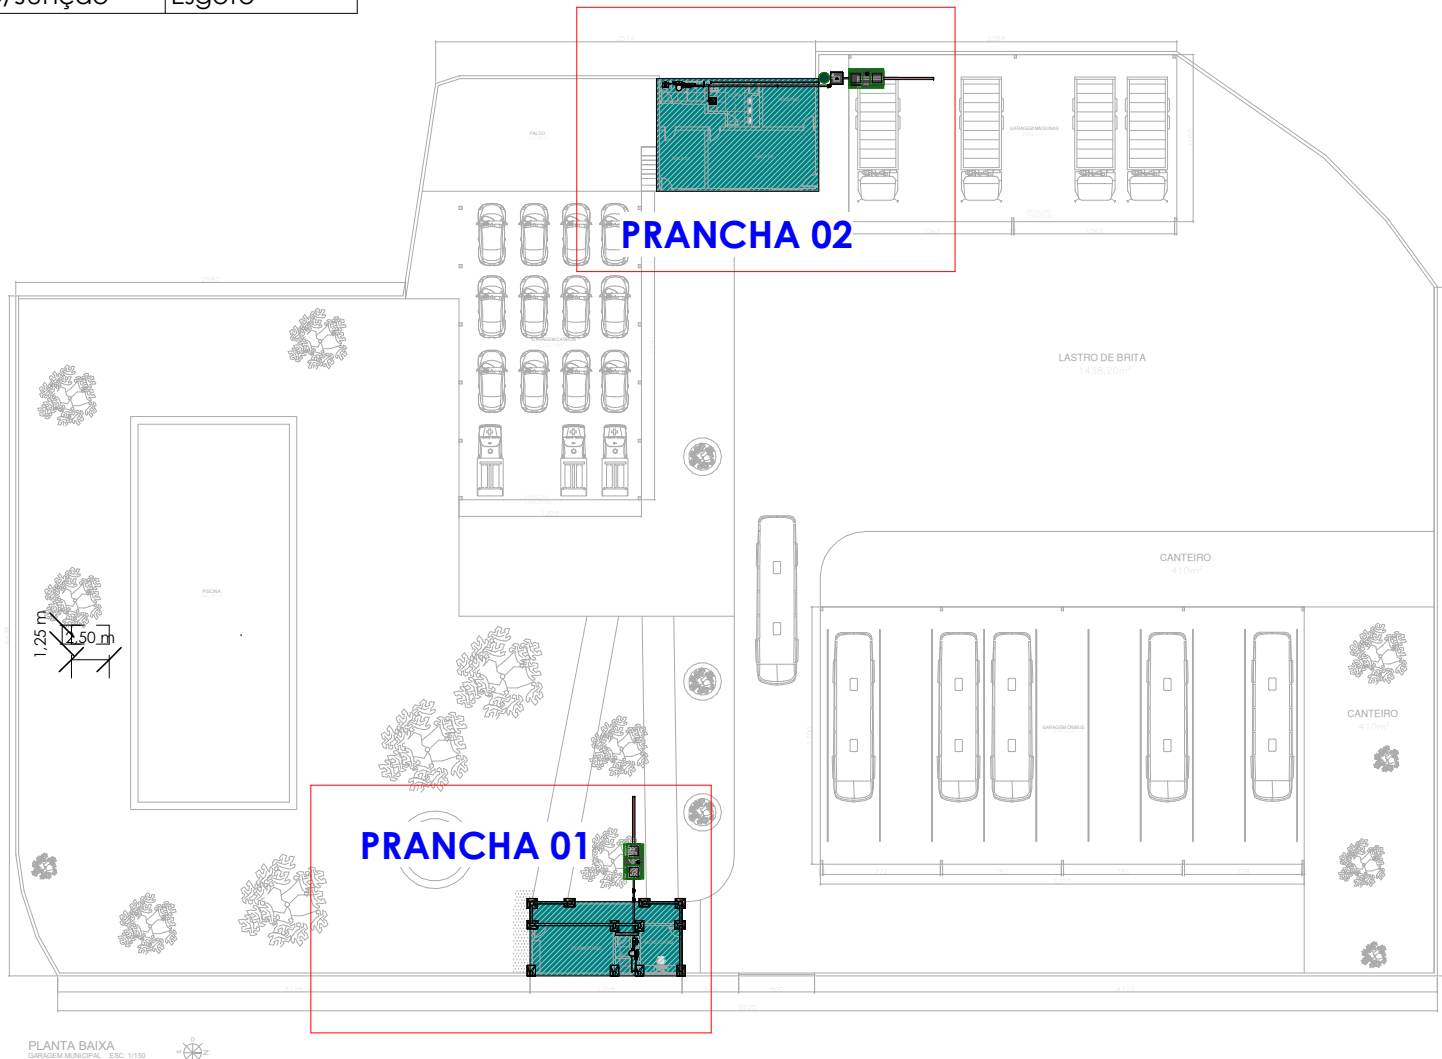

PLANTA BAIXA _GARAGEM_TÉRREO_GERAL_ - ESC 1/500

LINCOLN CARTAXO DE LIRA JUNIOR:06897861405
Assinado de forma digital por LINCOLN CARTAXO DE LIRA JUNIOR:06897861405
Dados: 2025.06.19 17:28:32 -03'00'

PROPRIETÁRIO: PREFEITURA MUNICIPAL DE COREMAS - PB

PROJETO: LINCOLN CARTAXO DE LIRA JÚNIOR CREA 160.814.689-8

PROJETO: INSTALAÇÕES SANITÁRIAS DA REFORMA DA GARAGEM DE COREMAS
CONCEDENTE: PREFEITURA MUNICIPAL DE COREMAS - PB
CONVENIENTE: MUNICÍPIO DE COREMAS - PB
LOCAL: COREMAS - PB

		RESPONSÁVEL TÉCNICO	RUBRICA	DADOS
DATA	19/06/2025	LINCOLN CARTAXO		CREA 160.814.689-8
CÓPIA				
VISTO				

PRANCHA: 03 / 03
DESCRIÇÃO: PLANTA BAIXA - GERAL TÉRREO MAPEAMENTO DAS PRANCHAS QUANTITATIVOS E CORTE
ESCALA: INDICADA



Av. Gov. Flavio R. Coutinho, 500, sl. 601
Jd. Oceania, 58037-005 - João Pessoa (PB)
Tel +55 99924.4447
e-mail: contato@lclprojetos.com