RUA OFICIAL DE JUSTIÇA VICENTE GREGORIO ANTÃO

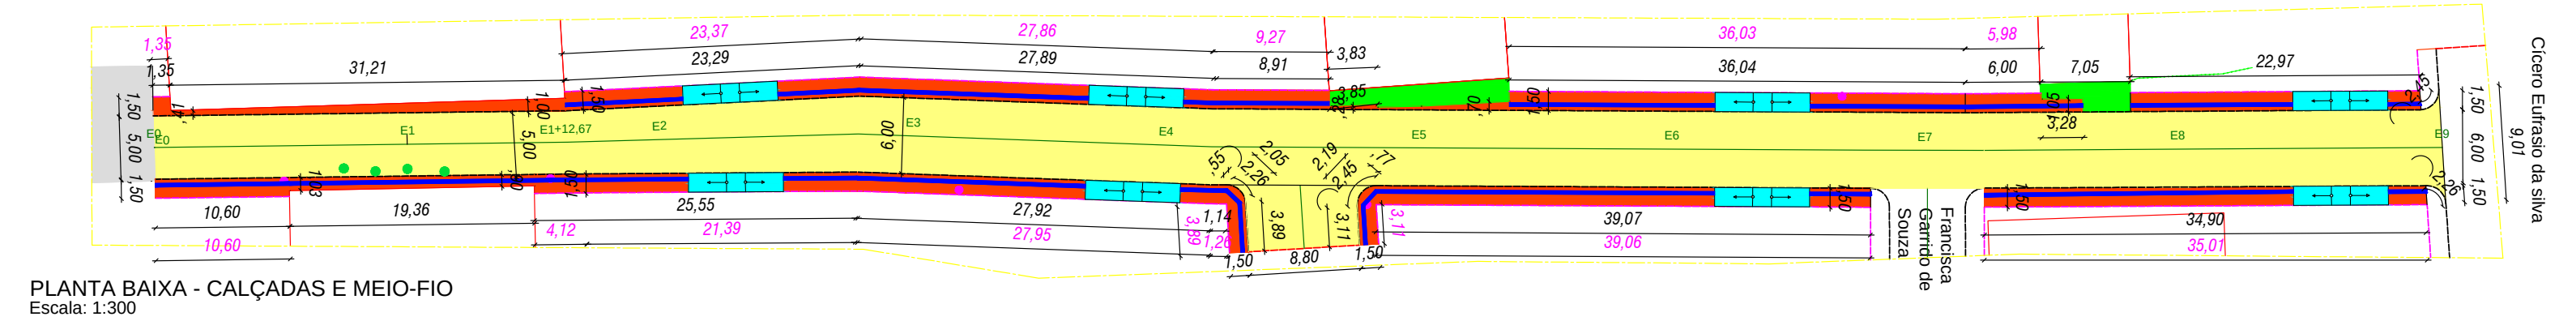
1,35
1,35
31,21
23,37
23,29
27,86
27,89
9,27
8,91
3,83
36,03
36,04
5,98
6,00
7,05
22,97
Cícero Eufrásio da silva
9,01
1,50 6,00 1,50
E0
E1
E1+12,67
E2
E3
E4
E5
E6
E7
E8
E9
10,60
10,60
19,36
4,12
25,55
21,39
27,92
27,95
1,14
3,89
8,80
1,50
39,07
39,06
Francisca Garrido de Souza
34,90
35,01

PLANTA BAIXA - CALÇADAS E MEIO-FIO
Escala: 1:300

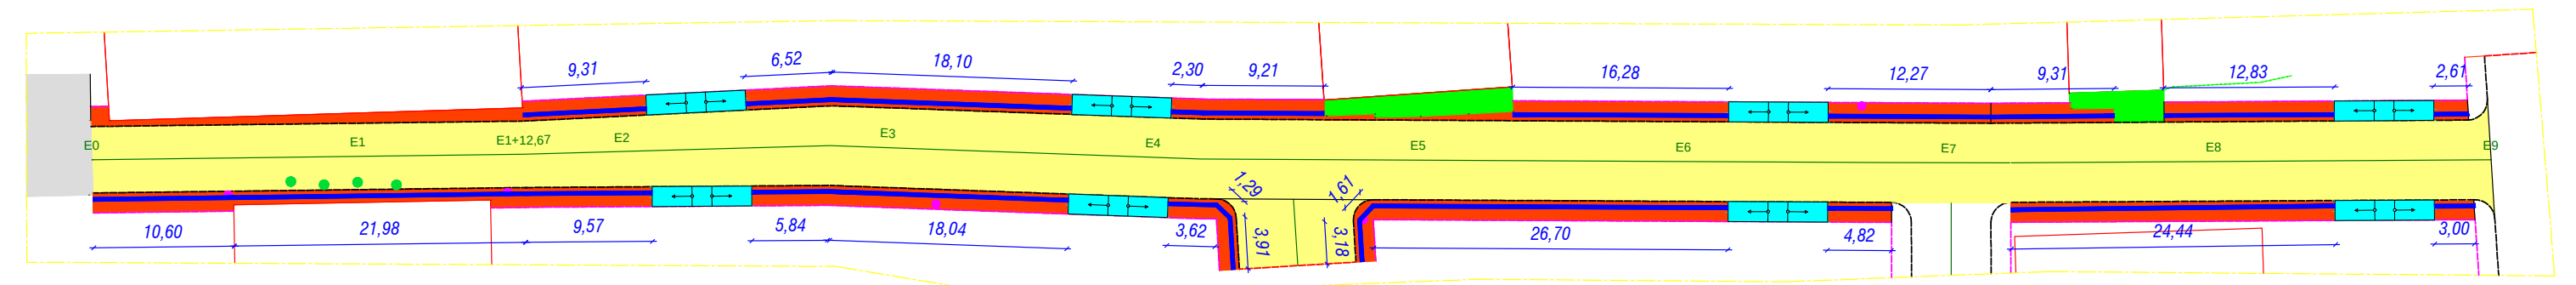
9,31
6,52
18,10
2,30
9,21
16,28
12,27
9,31
12,83
2,61
E0
E1
E1+12,67
E2
E3
E4
E5
E6
E7
E8
E9
10,60
21,98
9,57
5,84
18,04
3,62
3,91
3,18
26,70
4,82
24,44
3,00

PLANTA BAIXA - ROTAS ACESSIVEIS E SINALIZAÇÃO
Escala: 1:300

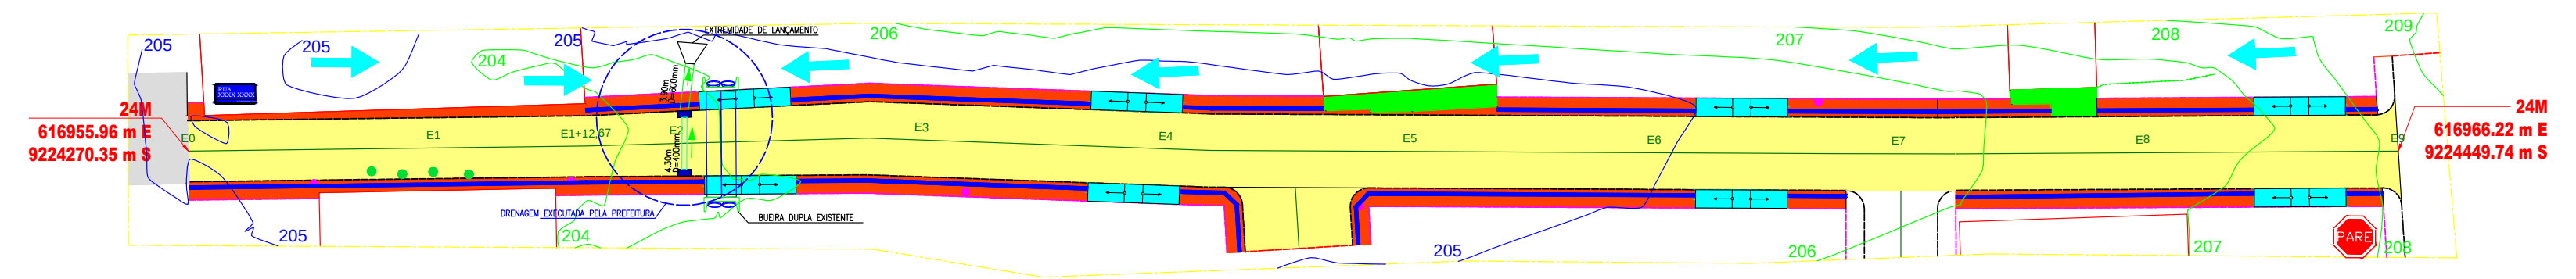
205
205
205
204
206
207
208
209
EXTREMIDADE DE LANÇAMENTO
24M
616955.96 m E
9224270.35 m S
24M
616966.22 m E
9224449.74 m S
DRENAGEM EXECUTADA PELA PREFEITURA
BUEIRO DUPLA EXISTENTE
205
204
206
207
PARE

PLANTA BAIXA - ROTAS ACESSIVEIS E SINALIZAÇÃO
Escala: 1:300

RUA OFICIAL DE JUSTIÇA VICENTE GREGORIO ANTÃO - SEÇÕES
ESC.: 1:200

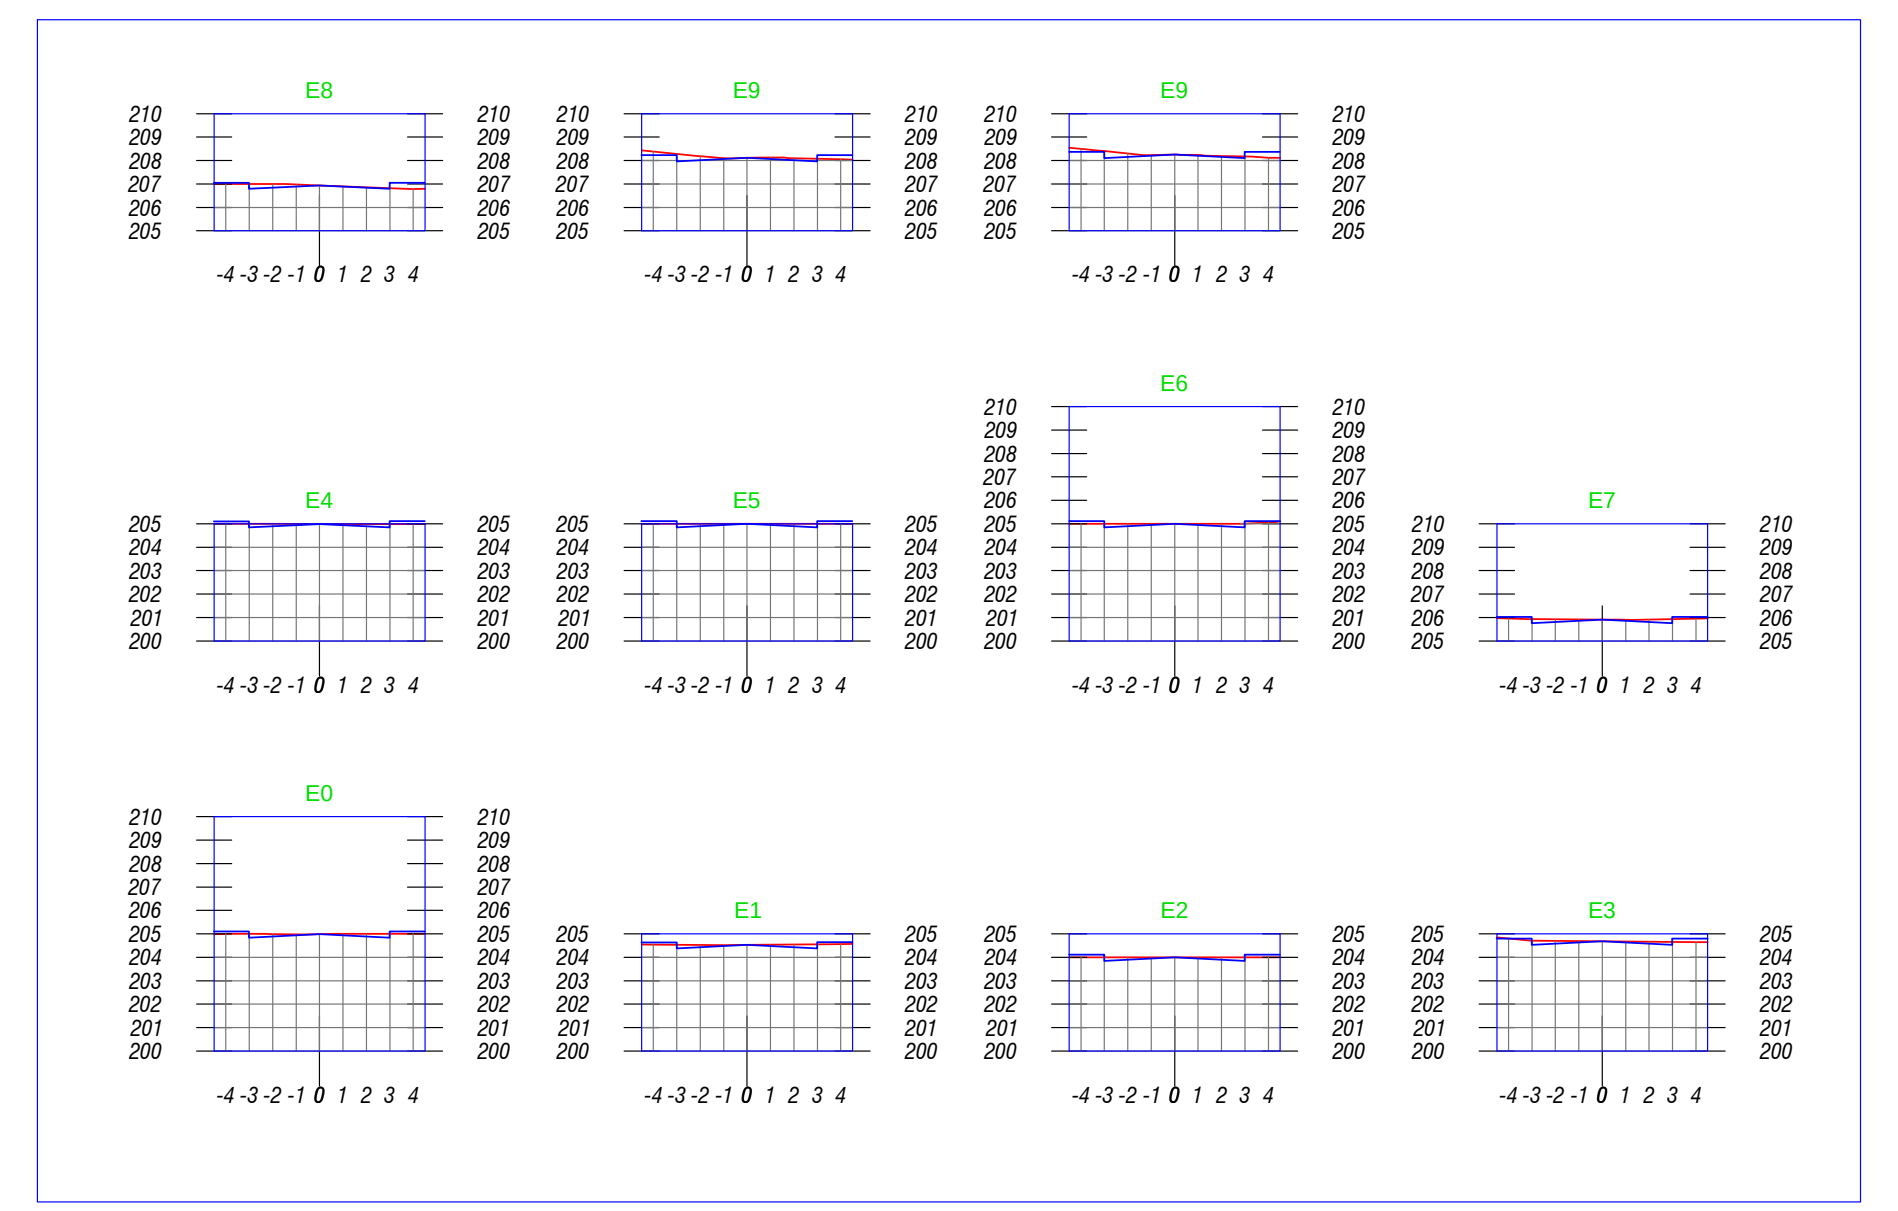

RUA OFICIAL DE JUSTIÇA VICENTE GREGORIO ANTÃO - PERFIL
ESC.: 1:300

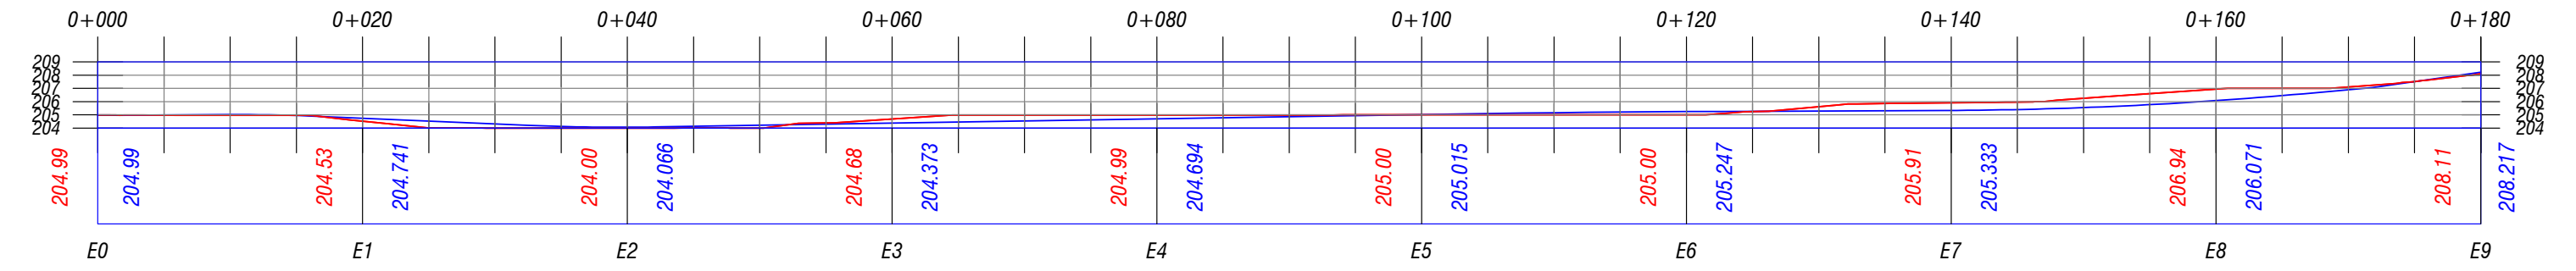

Legenda

Pavimentação

- 🟨 Pavimentação à Construir
- ▨ Pavimento Existente
- — Meio-fio Existente
- - - Meio-fio Projetado
- - - Cordão em Granito
- - - Alvenaria de 1 vez
- — Cerca
- ➡ Sentido do Caimento da água

Passeio

- 🟥 Calçadas à Construir
- 🟩 Calçadas Existentes
- 🟦 Piso Tátil
- ▭ Rampa de Acesso
- ● Poste Existente
- ● Poço de Visita (PV)
- ● Árvore
- — Edificação Existente
- — Lote Projetado

Sinalização

- PARE Placa de Parada Obrigatória
- ▬ Placa com Nome da rua

Boca de Lobo (BLS01)
ESCALA : 1/25

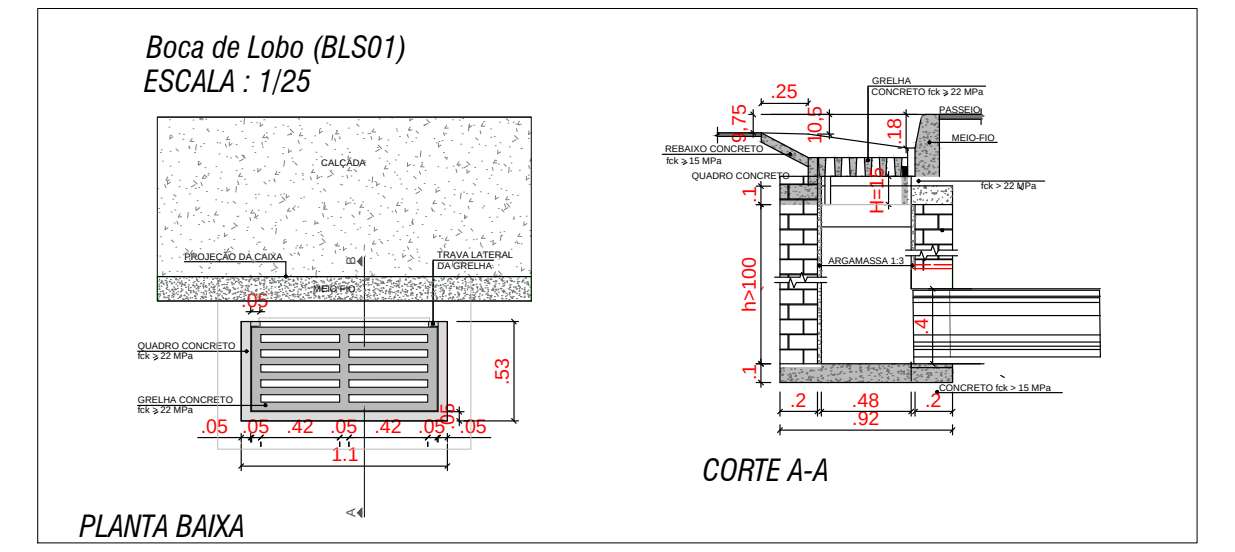
PLANTA BAIXA
CORTE A-A
CALÇADA
GRELHA CONCRETO
25
1,75
48
.92
53
1.1
.05 .05 .42 .05 .42 .05 .05
h=100

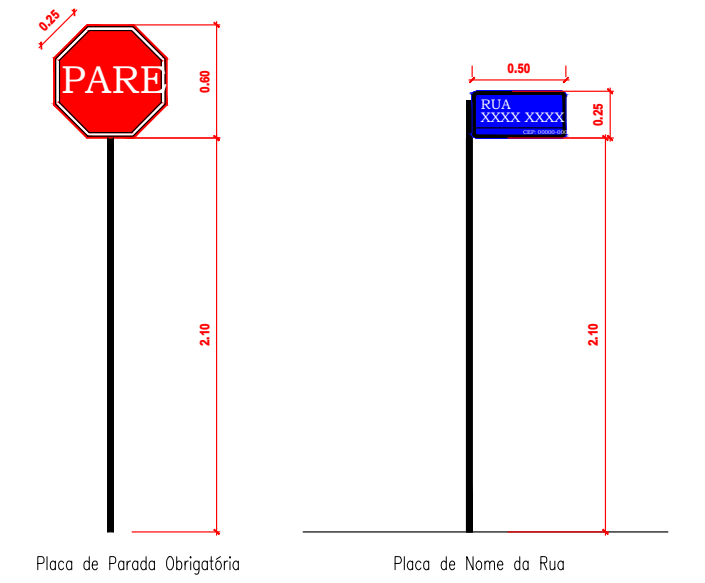
PARE
0.25
0.60
2.10
0.50
0.25
RUA XXXX XXXX
2.10
Placa de Parada Obrigatória
Placa de Nome da Rua

Detalhe – Sinalização Vertical
1:25

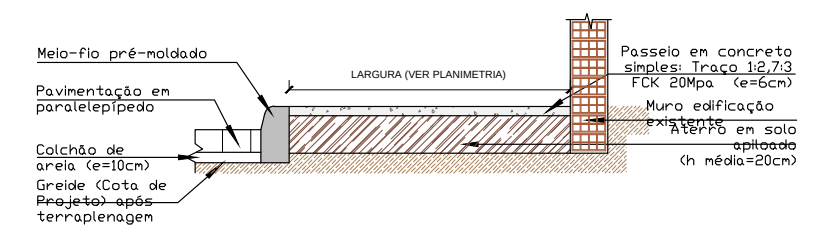
Meio-fio pré-moldado
Pavimentação em paralelepípedo
Colchão de areia (e=10cm)
Greide (Cota de Projeto) após terraplenagem
LARGURA (VER PLANIMETRIA)
Passeio em concreto simples: Traço 1:2:7:3 FCK 20Mpa (e=6cm)
Muro edificação existente
Aterro em solo apiloado (h média=20cm)

Detalhe 01 – Passeio Para Trechos s/ Alvenaria de 1 Vez

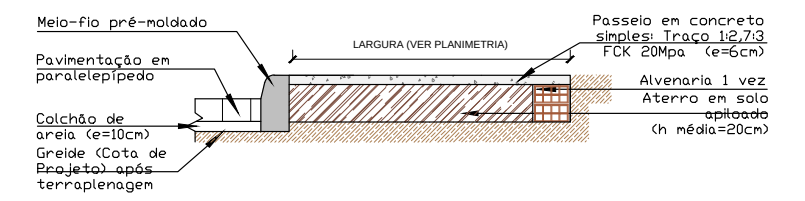
Meio-fio pré-moldado
Pavimentação em paralelepípedo
Colchão de areia (e=10cm)
Greide (Cota de Projeto) após terraplenagem
LARGURA (VER PLANIMETRIA)
Passeio em concreto simples: Traço 1:2:7:3 FCK 20Mpa (e=6cm)
Alvenaria 1 vez
Aterro em solo apiloado (h média=20cm)

Detalhe 02 – Passeio Para Trechos c/ Alvenaria de 1 Vez

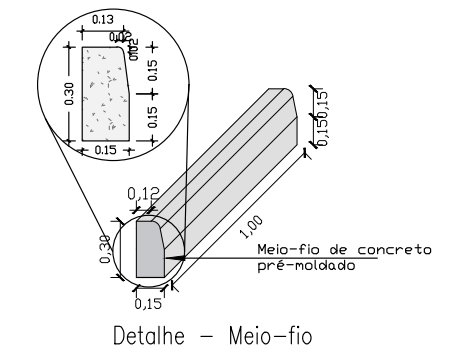
0.13
0.30
0.15
0.12
0.15
1.00
Meio-fio de concreto pré-moldado

Detalhe – Meio-fio

Nota: Para o cálculo do quantitativo de concreto do passeio público, considera-se a dimensão da largura conforme indicado nos detalhe dos passeios.

Seção-Tipo de Pavimentação

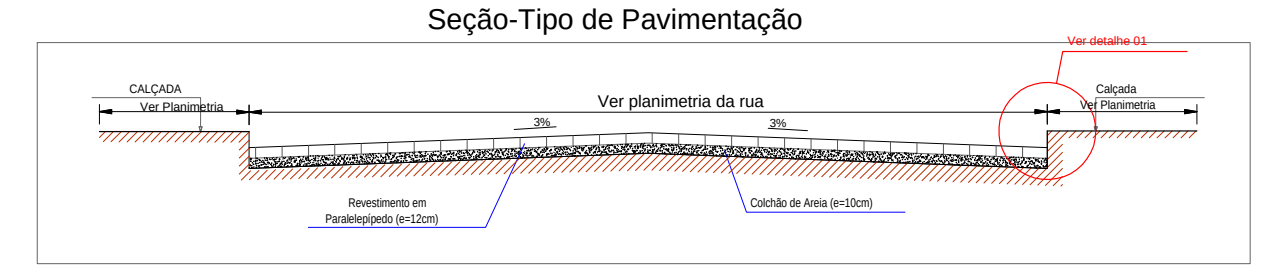
CALÇADA
Ver Planimetria
Ver planimetria da rua
2%
2%
Ver detalhe 01
Calçada
Ver Planimetria
Revestimento em Paralelepípedo (e=12cm)
Colchão de Areia (e=10cm)

Sem Escala

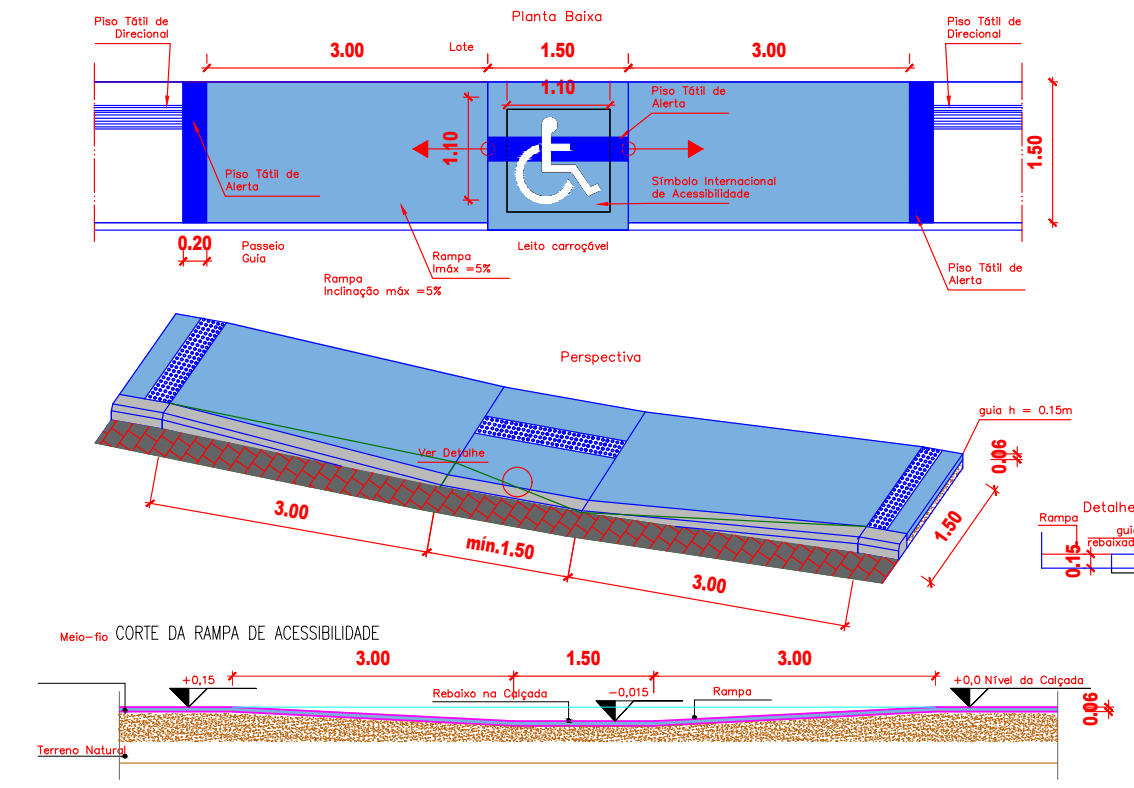
Planta Baixa
Piso Tátil de Direcional
3.00
Lote
1.50
3.00
1.10
Piso Tátil de Alerta
1.50
Símbolo internacional de Acessibilidade
0.20
Passeio Guia
Rampa imáx =5%
Leito carroçável
Rampa inclinação máx =5%
Perspectiva
guia h = 0.15m
3.00
min.1.50
3.00
1.50
0.06
Detalhe
Meio-fio CORTE DA RAMPA DE ACESSIBILIDADE
3.00
1.50
3.00
+0.15
Rebaixo na Calçada
+0.015
Rampa
±0.0 Nível da Calçada
Terreno Natural

Detalhe – Rampa de Acessibilidade
1:50

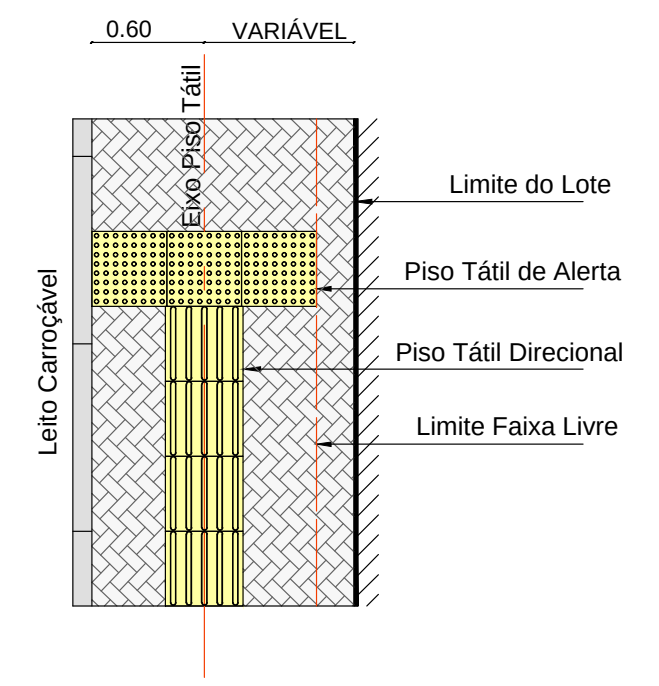
0.60
VARIÁVEL
Eixo Piso Tátil
Limite do Lote
Piso Tátil de Alerta
Piso Tátil Direcional
Limite Faixa Livre
Leito Carroçável

Detalhe 01 – Início/Fim Piso Tátil (D01-IFPT)

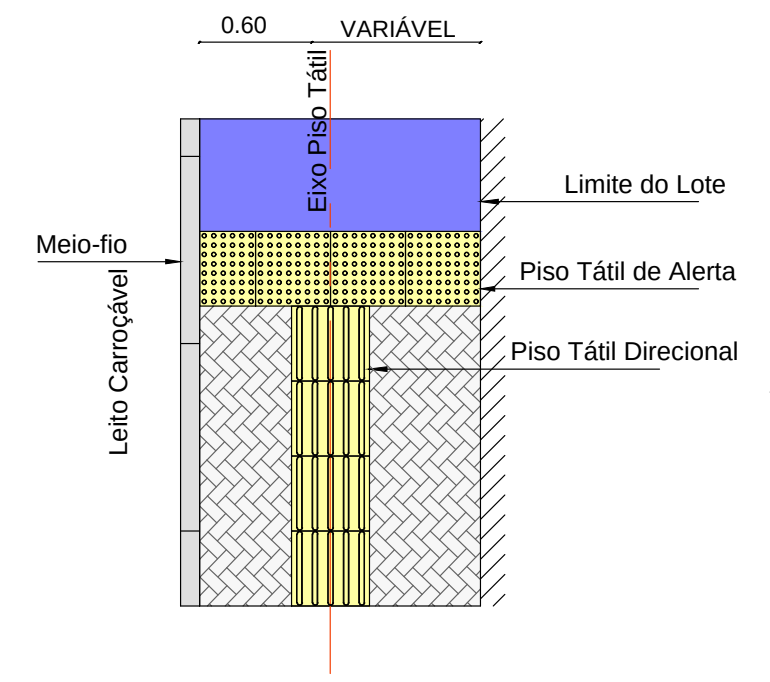
0.60
VARIÁVEL
Eixo Piso Tátil
Meio-fio
Limite do Lote
Piso Tátil de Alerta
Piso Tátil Direcional
Leito Carroçável

Detalhe 02 – Encontro Piso Tátil com Rampa (D02-EPTR)

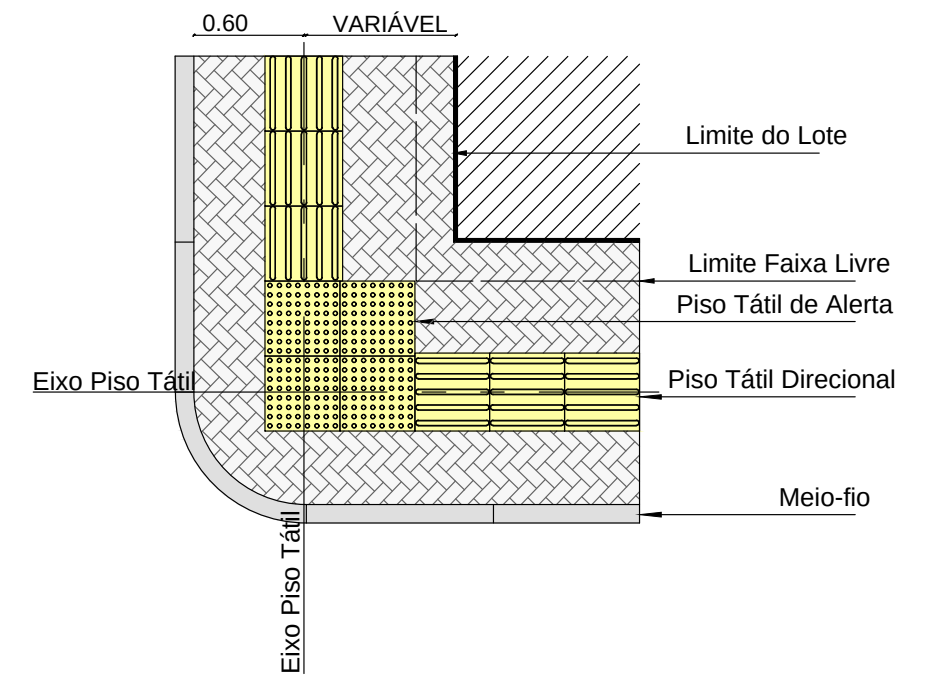
0.60
VARIÁVEL
Limite do Lote
Limite Faixa Livre
Piso Tátil de Alerta
Piso Tátil Direcional
Eixo Piso Tátil
Meio-fio
Eixo Piso Tátil

Detalhe 03 – Mudança de direção – Entre 90° e 150° (D03-MD)

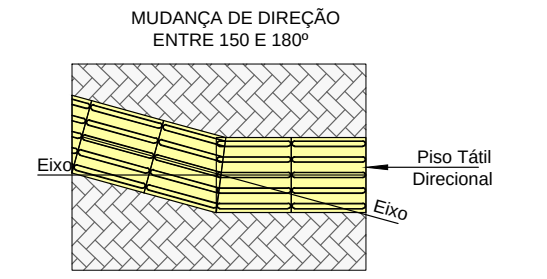
MUDANÇA DE DIREÇÃO ENTRE 150 E 180°
Eixo
Piso Tátil Direcional
Eixo

Detalhe 04 – Mudança de direção entre 150° e 180° (D04-MD)

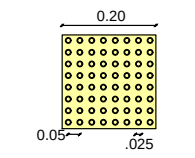

Detalhe 05 – Piso Tátil de Alerta

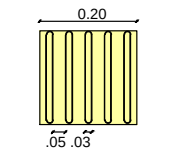

Detalhe 06 – Piso Tátil Direcional

PROPRIETÁRIO Prefeitura Municipal de Coremas- PB
PROJETISTA Kleber Sá de Oliveira
Kleber Sá de Oliveira
Engenheiro Civil
CREA 1602582780

EPE
EMPRESA PARAIBA DE ENGENHARIA
PROJETO: PAVIMENTAÇÃO DE RUAS E VIAS
LOCAL: MUNICÍPIO DE COREMAS - PB
PROPRIETÁRIO: PREFEITURA MUNICIPAL DE COREMAS - PB
FOLHA: 01/07
ESCALA: Indicadas
DESENHOS: Indicados
RESPONSÁVEL TÉCNICO: Kleber Sá de Oliveira Crea: 160391676-8
ANOTAÇÕES:
ARQUIVO: PAV_COREMAS_FINAL P+B_2022.dwg
DESENHO: Diego Medeiros
DATA: SET - 2022

Francisca Garrido de Souza

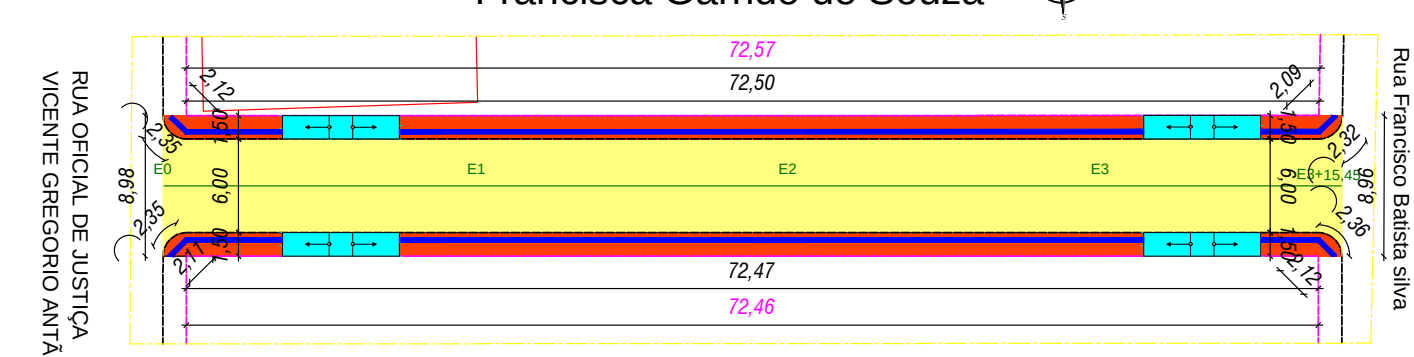
RUA OFICIAL DE JUSTIÇA VICENTE GREGORIO ANTÃO
Rua Francisco Batista silva
72,57
72,50
9,00
6,00
E0
E1
E2
E3
E3+15,45
72,47
72,46

PLANTA BAIXA - CALÇADAS E MEIO-FIO
Escala: 1:300

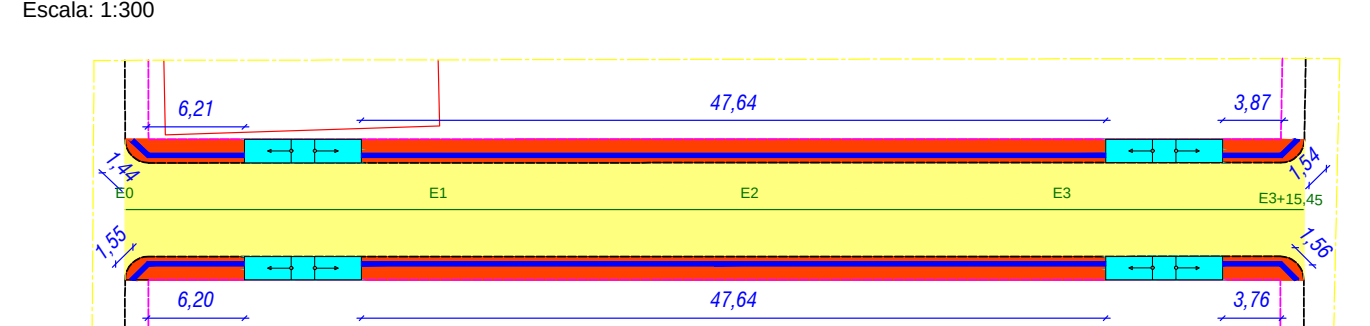
6,21
47,64
3,87
1,44
1,50
1,54
1,56
E0
E1
E2
E3
E3+15,45
6,20
47,64
3,76

PLANTA BAIXA - ROTAS ACESSIVEIS E SINALIZAÇÃO
Escala: 1:300

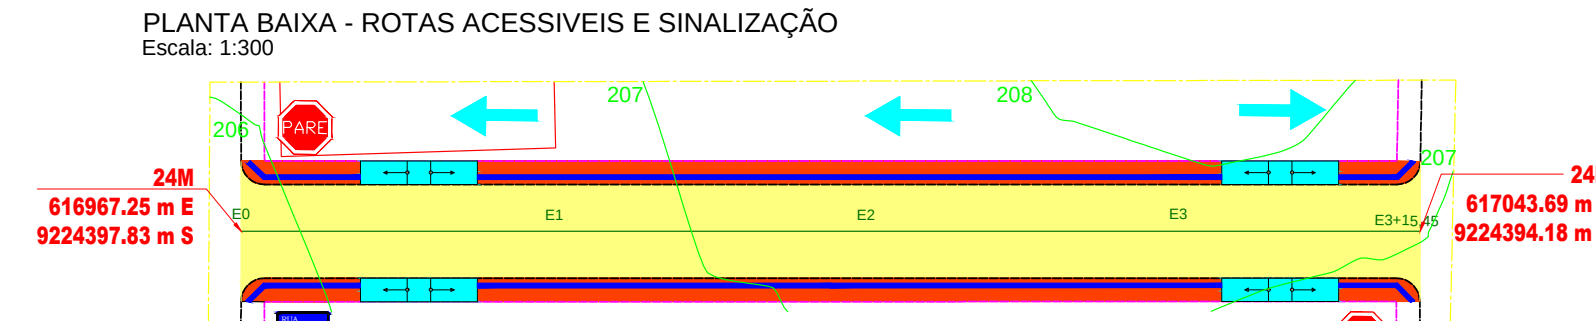
206
207
208
207
PARE
24M
616967.25 m E
9224397.83 m S
24M
617043.69 m E
9224394.18 m S
PARE

PLANTA BAIXA - ROTAS ACESSIVEIS E SINALIZAÇÃO
Escala: 1:300

FRANCISCA GARRIDO DE SOUZA - PERFIL
ESC.: 1:300

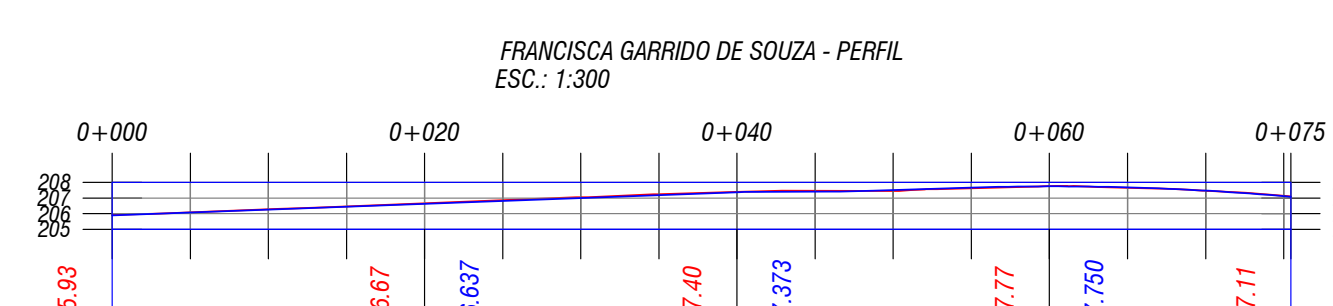

RUA OFICIAL DE JUSTIÇA VICENTE GREGORIO ANTÃO - SEÇÕES
ESC.: 1:200

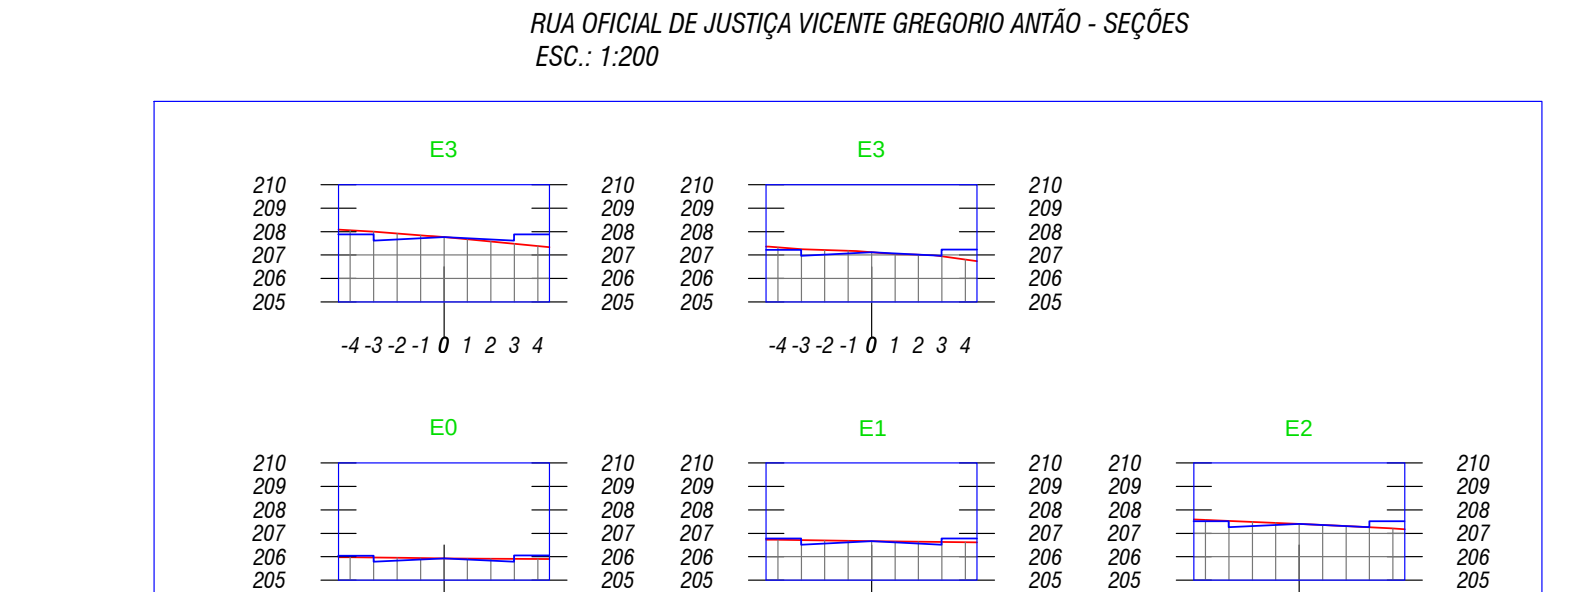

Legenda

Pavimentação

- 🟨 Pavimentação à Construir
- ▨ Pavimento Existente
- — Meio-fio Existente
- - - Meio-fio Projetado
- - - Cordão em Granito
- - - Alvenaria de 1 vez
- — Cerca
- ➡ Sentido do Caimento da água

Passeio

- 🟥 Calçadas à Construir
- 🟩 Calçadas Existentes
- 🟦 Piso Tátil
- ▭ Rampa de Acesso
- ● Poste Existente
- ● Poço de Visita (PV)
- ● Árvore
- — Edificação Existente
- — Lote Projetado

Sinalização

- PARE Placa de Parada Obrigatória
- ▬ Placa com Nome da rua

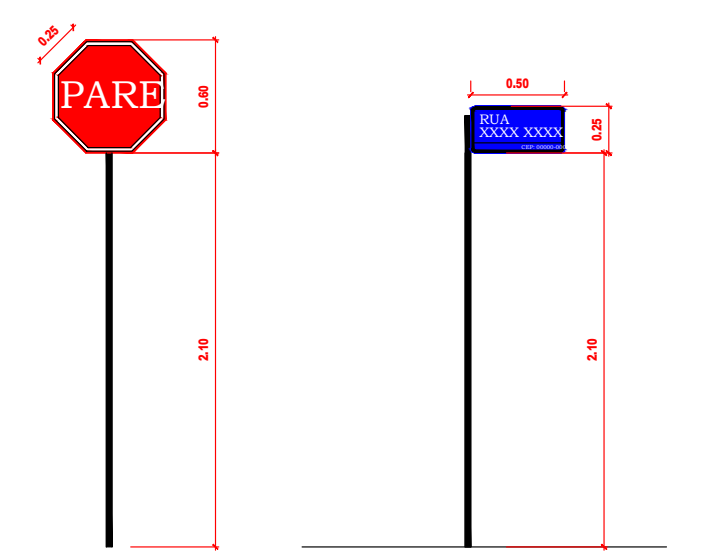
PARE
0.25
0.60
2.10
0.50
0.25
RUA XXXX XXXX
2.10
Placa de Parada Obrigatória
Placa de Nome da Rua

Detalhe – Sinalização Vertical
1:25

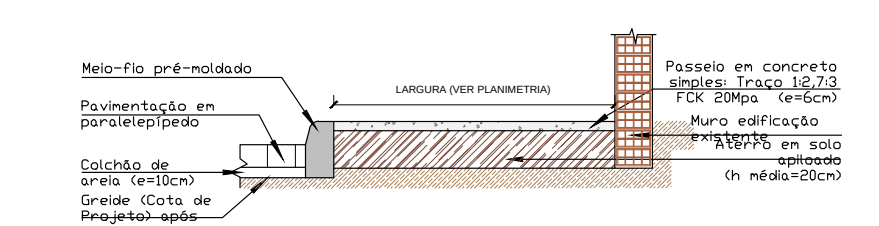
Meio-fio pré-moldado
Pavimentação em paralelepípedo
Colchão de areia (e=10cm)
Greide (Cota de Projeto) após terraplenagem
LARGURA (VER PLANIMETRIA)
Passeio em concreto simples: Traço 1:2:7:3 FCK 20Mpa (e=6cm)
Muro edificação existente
Aterro em solo apiloado (h média=20cm)

Detalhe 01 – Passeio Para Trechos s/ Alvenaria de 1 Vez

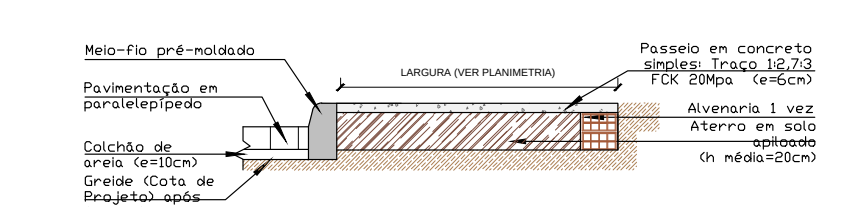
Meio-fio pré-moldado
Pavimentação em paralelepípedo
Colchão de areia (e=10cm)
Greide (Cota de Projeto) após terraplenagem
LARGURA (VER PLANIMETRIA)
Passeio em concreto simples: Traço 1:2:7:3 FCK 20Mpa (e=6cm)
Alvenaria 1 vez
Aterro em solo apiloado (h média=20cm)

Detalhe 02 – Passeio Para Trechos c/ Alvenaria de 1 Vez

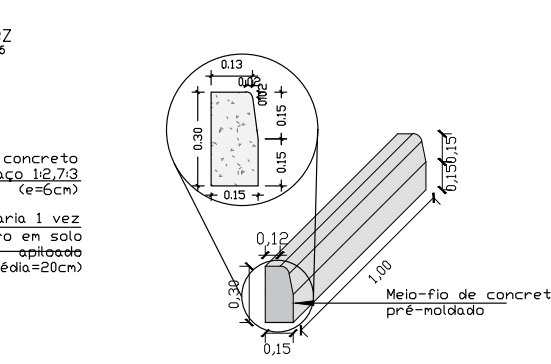
0.13
0.30
0.15
0.12
0.15
1.00
Meio-fio de concreto pré-moldado

Detalhe – Meio-fio

Nota: Para o cálculo do quantitativo de concreto do passeio público, considera-se a dimensão da largura conforme indicado nos detalhe dos passeios.

Seção-Tipo de Pavimentação

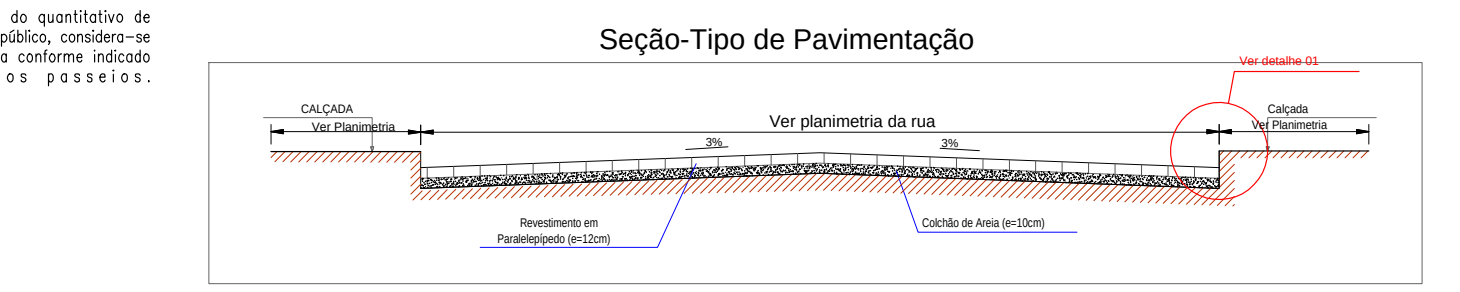
CALÇADA
Ver Planimetria
Ver planimetria da rua
2%
2%
Ver detalhe 01
Calçada
Ver Planimetria
Revestimento em Paralelepípedo (e=12cm)
Colchão de Areia (e=10cm)

Sem Escala

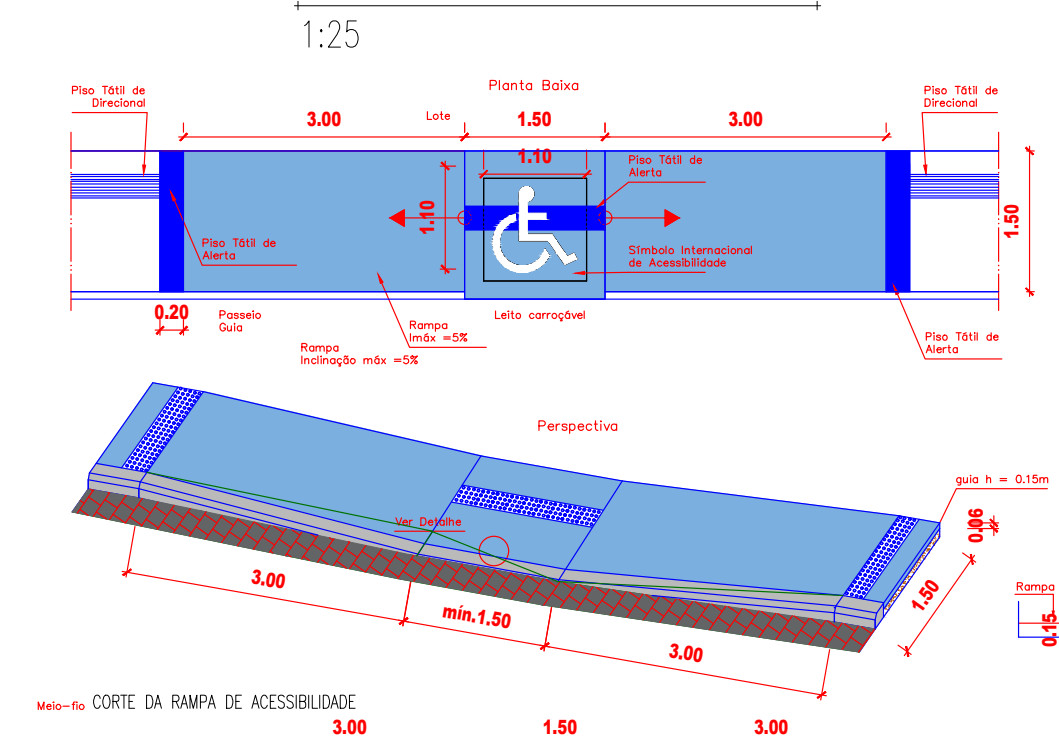
Planta Baixa
Piso Tátil de Direcional
3.00
Lote
1.50
3.00
1.10
Piso Tátil de Alerta
1.50
Símbolo internacional de Acessibilidade
0.20
Passeio Guia
Rampa imáx =5%
Leito carroçável
Rampa inclinação máx =5%
Perspectiva
guia h = 0.15m
3.00
min.1.50
3.00
1.50
0.06
Detalhe
Meio-fio CORTE DA RAMPA DE ACESSIBILIDADE
3.00
1.50
3.00
+0.15
Rebaixo na Calçada
+0.015
Rampa
±0.0 Nível da Calçada
Terreno Natural

Detalhe – Rampa de Acessibilidade
1:50

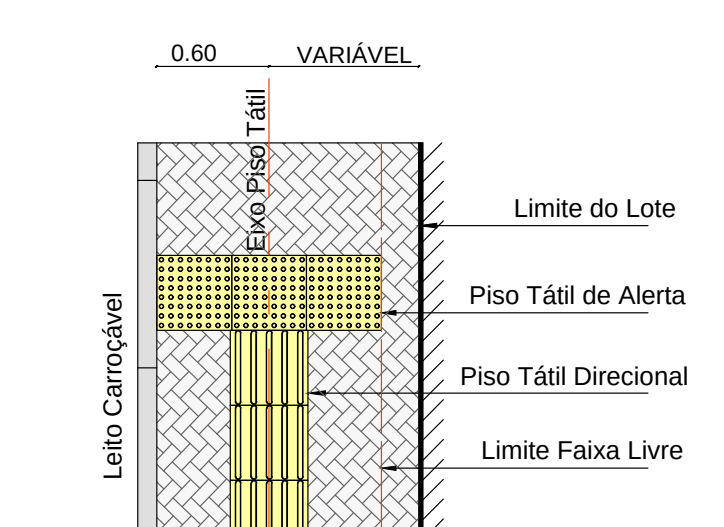
0.60
VARIÁVEL
Eixo Piso Tátil
Limite do Lote
Piso Tátil de Alerta
Piso Tátil Direcional
Limite Faixa Livre
Leito Carroçável

Detalhe 01 – Início/Fim Piso Tátil (D01-IFPT)

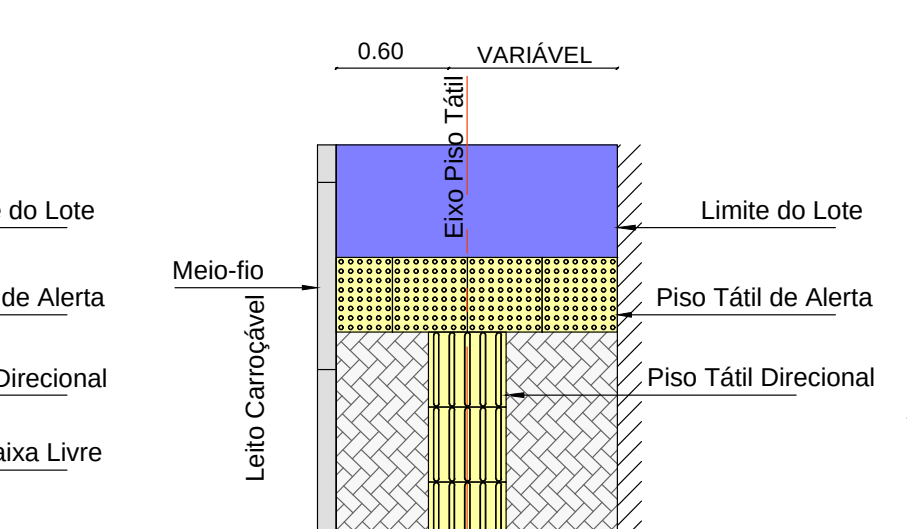
0.60
VARIÁVEL
Eixo Piso Tátil
Meio-fio
Limite do Lote
Piso Tátil de Alerta
Piso Tátil Direcional
Leito Carroçável

Detalhe 02 – Encontro Piso Tátil com Rampa (D02-EPTR)

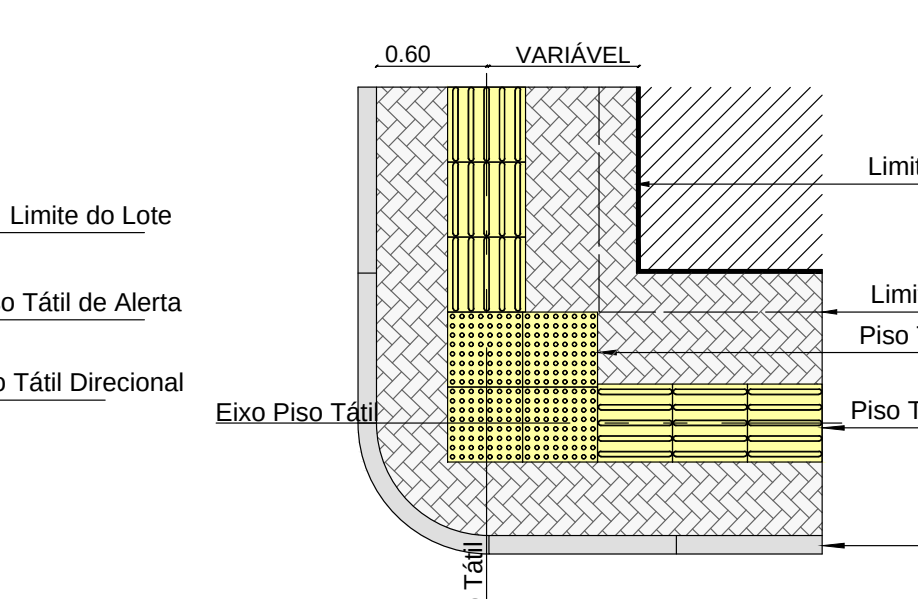
0.60
VARIÁVEL
Limite do Lote
Limite Faixa Livre
Piso Tátil de Alerta
Piso Tátil Direcional
Eixo Piso Tátil
Meio-fio
Eixo Piso Tátil

Detalhe 03 – Mudança de direção – Entre 90° e 150° (D03-MD)

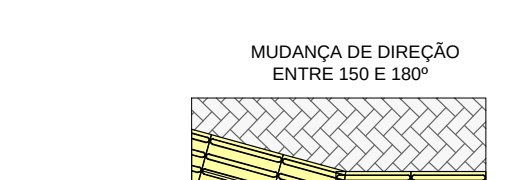
MUDANÇA DE DIREÇÃO ENTRE 150 E 180°
Eixo
Piso Tátil Direcional
Eixo

Detalhe 04 – Mudança de direção entre 150° e 180° (D04-MD)

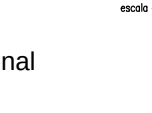

Detalhe 05 – Piso Tátil de Alerta

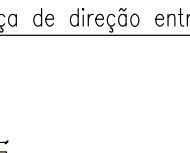

Detalhe 06 – Piso Tátil Direcional

PROPRIETÁRIO Prefeitura Municipal de Coremas- PB
PROJETISTA Kleber Sá de Oliveira
Kleber Sá de Oliveira
Engenheiro Civil
CREA 1602582780

EPE
EMPRESA PARAIBA DE ENGENHARIA
PROJETO: PAVIMENTAÇÃO DE RUAS E VIAS
LOCAL: MUNICÍPIO DE COREMAS - PB
PROPRIETÁRIO: PREFEITURA MUNICIPAL DE COREMAS - PB
FOLHA: 02/07
ESCALA: Indicadas
DESENHOS: Indicados
RESPONSÁVEL TÉCNICO: Kleber Sá de Oliveira Crea: 160391676-8
ANOTAÇÕES:
ARQUIVO: PAV_COREMAS_FINAL P+B_2022.dwg
DESENHO: Diego Medeiros
DATA: SET - 2022

Rua Francisco Batista Silva

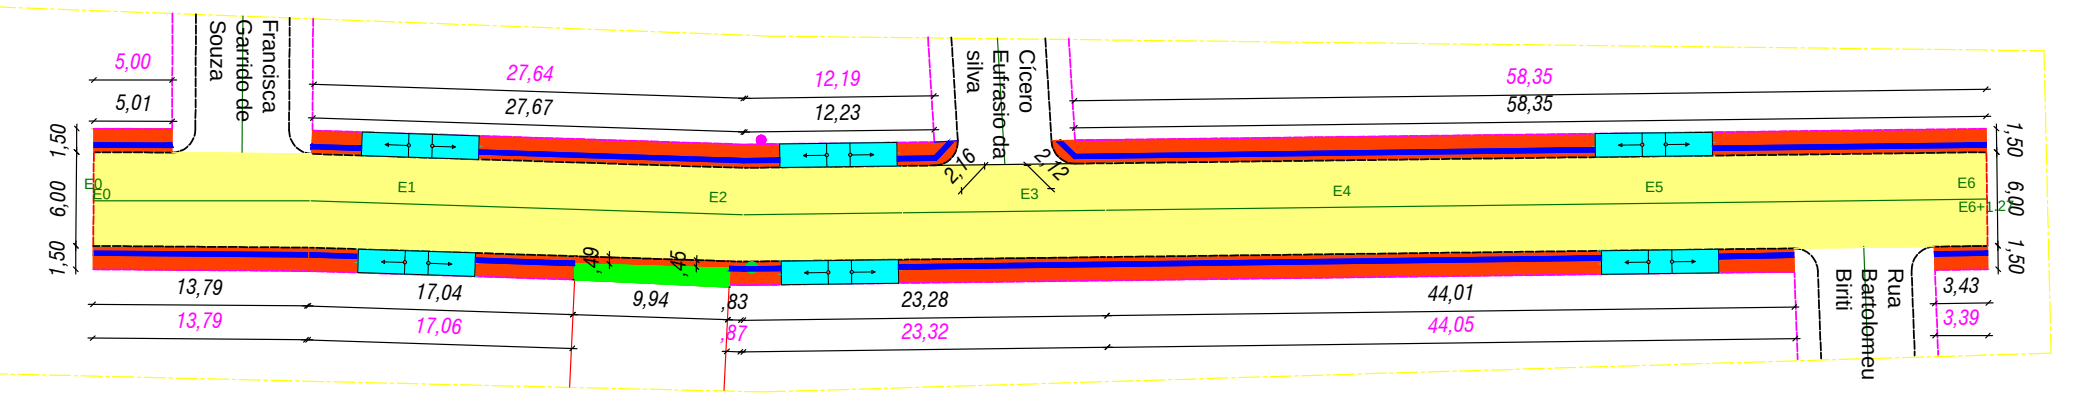
Francisca Garrido de Souza
Cícero Eufrásio da Silva
Rua Bartolomeu Brito
5,00
5,01
27,64
27,67
12,19
12,23
58,35
58,35
1,50
6,00
1,50
E0
E1
E2
E3
E4
E5
E6
E6+1,27
13,79
13,79
17,04
17,06
9,94
23,28
23,32
44,01
44,05
3,43
3,39

PLANTA BAIXA - CALÇADAS E MEIO-FIO
Escala: 1:300

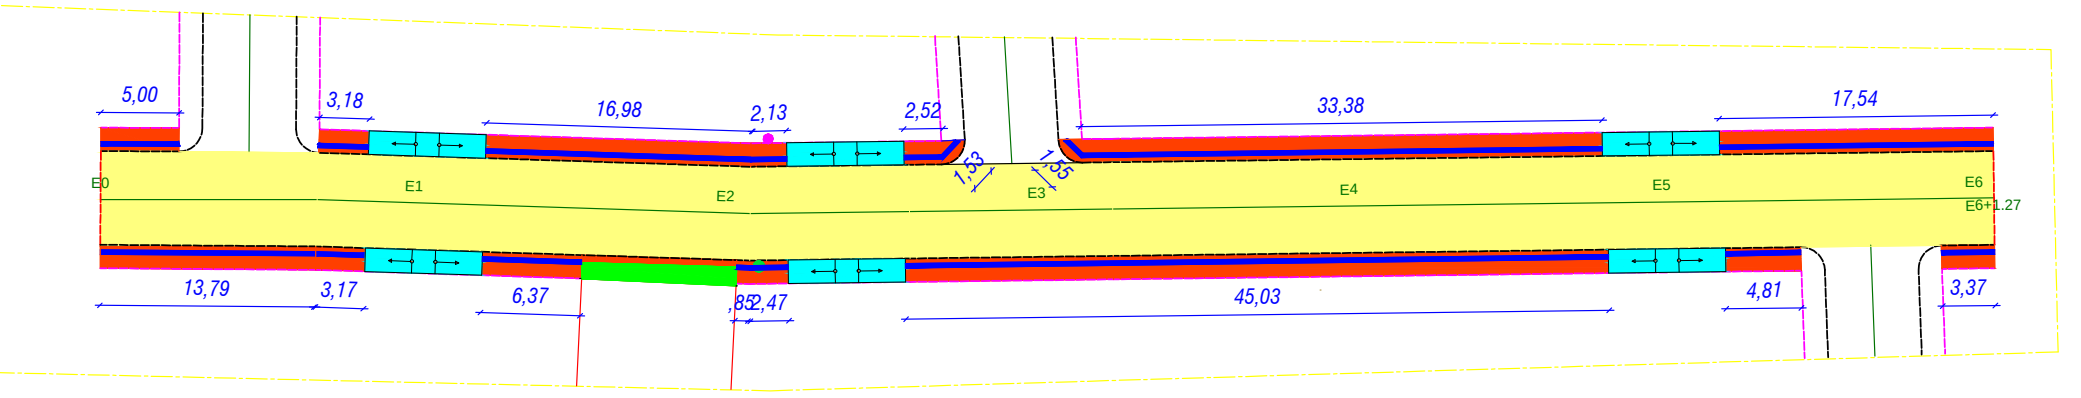
5,00
3,18
16,98
2,13
2,52
33,38
17,54
E0
E1
E2
E3
E4
E5
E6
E6+1,27
13,79
3,17
6,37
2,47
45,03
4,81
3,37

PLANTA BAIXA - ROTAS ACESSIVEIS E SINALIZAÇÃO
Escala: 1:300

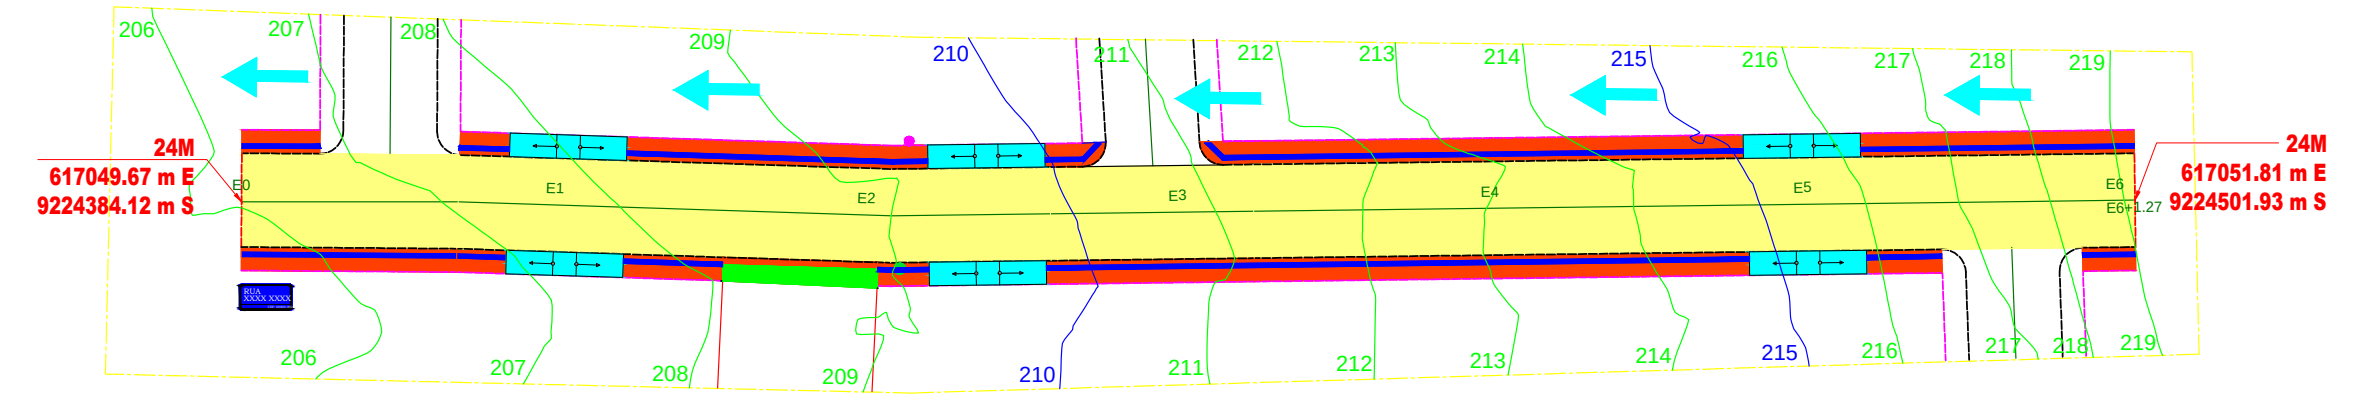
206
207
208
209
210
211
212
213
214
215
216
217
218
219
24M
617049.67 m E
9224384.12 m S
24M
617051.81 m E
9224501.93 m S
E0
E1
E2
E3
E4
E5
E6

PLANTA BAIXA - ROTAS ACESSIVEIS E SINALIZAÇÃO
Escala: 1:300

RUA FRANCISCO BATISTA SILVA - SEÇÕES
ESC.: 1:200

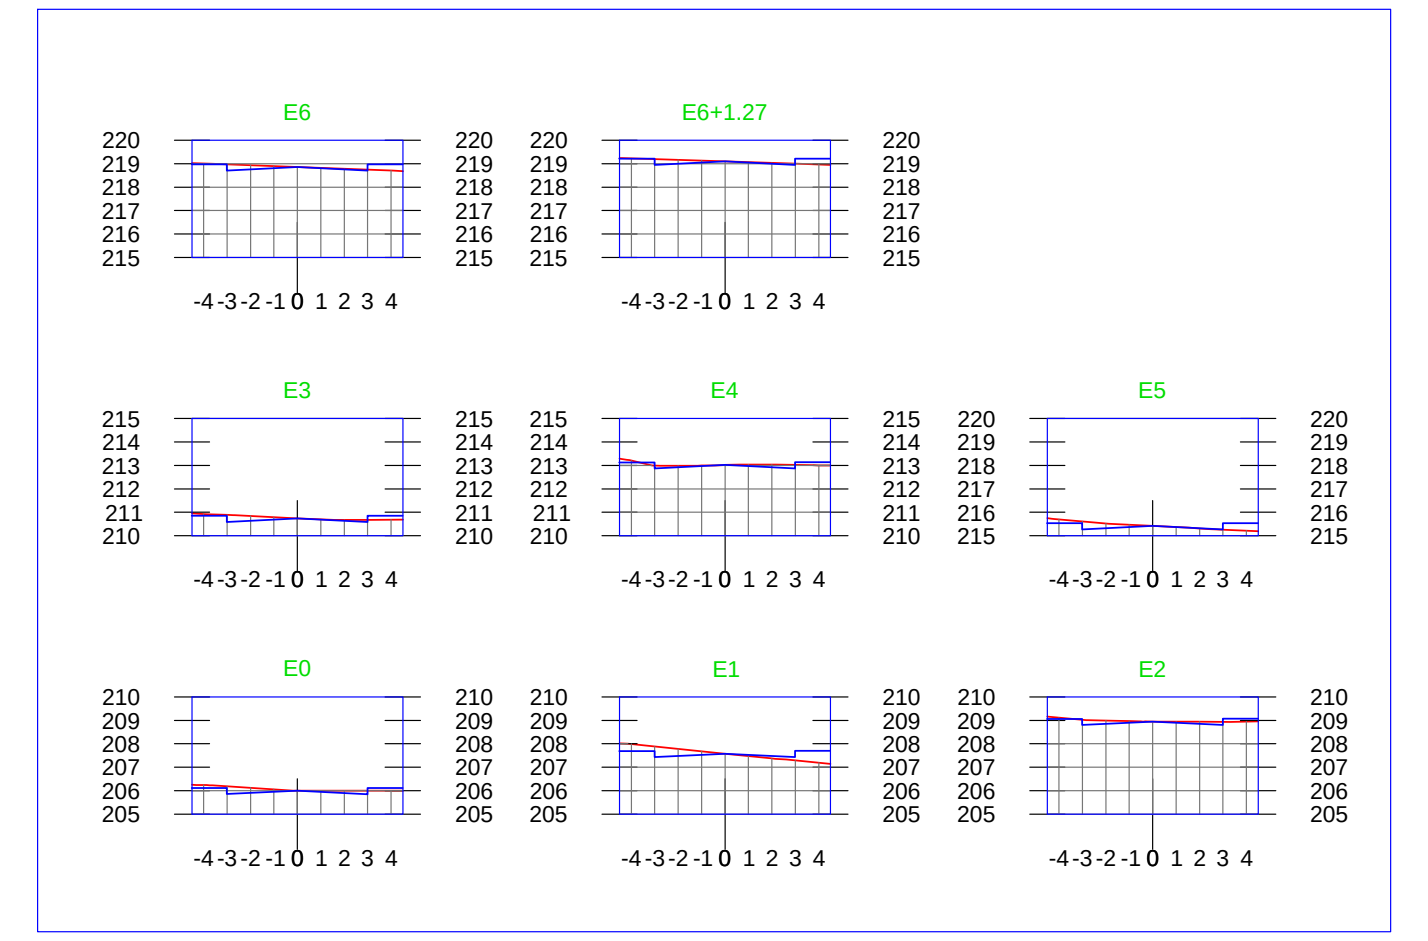

RUA FRANCISCO BATISTA SILVA - PERFIL
ESC.: 1:300

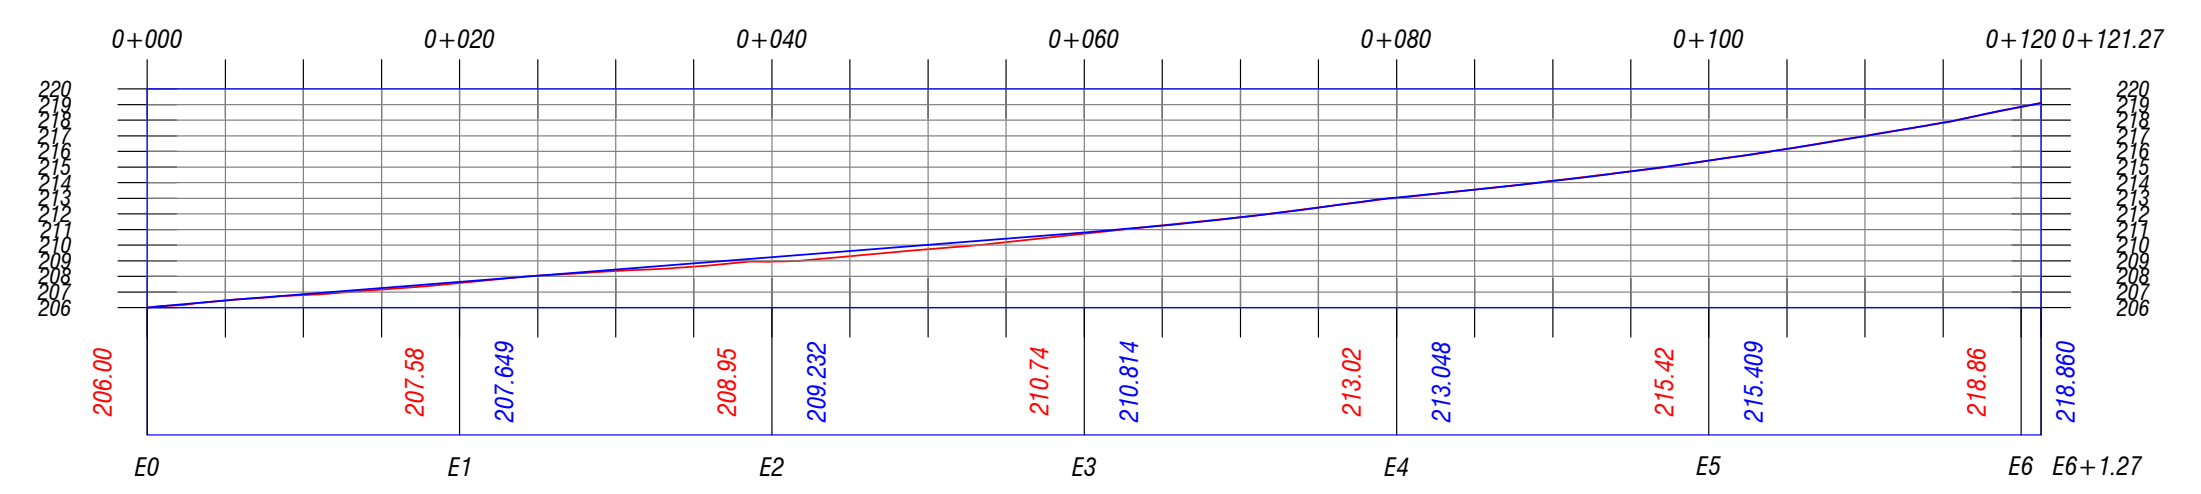

Legenda

Pavimentação

- 🟨 Pavimentação à Construir
- ▨ Pavimento Existente
- — Meio-fio Existente
- - - Meio-fio Projetado
- - - Cordão em Granito
- - - Alvenaria de 1 vez
- — Cerca
- ➡ Sentido do Caimento da água

Passeio

- 🟥 Calçadas à Construir
- 🟩 Calçadas Existentes
- 🟦 Piso Tátil
- ▭ Rampa de Acesso
- ● Poste Existente
- ● Poço de Visita (PV)
- ● Árvore
- — Edificação Existente
- — Lote Projetado

Sinalização

- PARE Placa de Parada Obrigatória
- ▬ Placa com Nome da rua

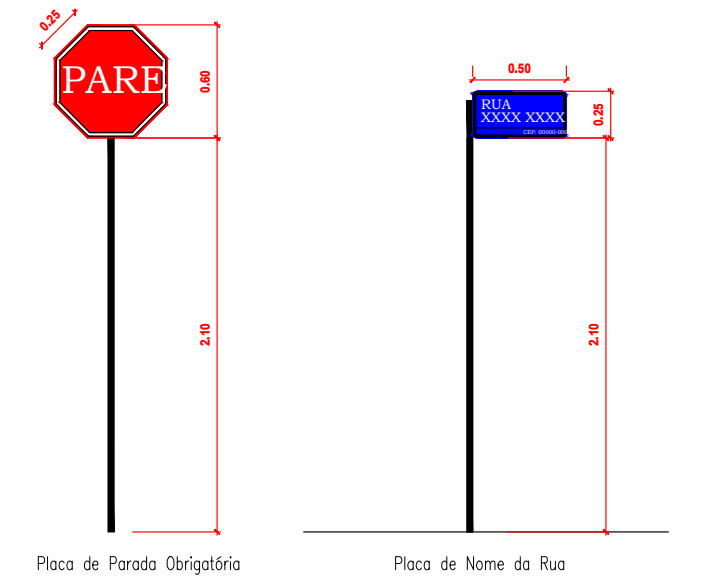
PARE
0.25
0.60
2.10
0.50
0.25
RUA XXXX XXXX
2.10
Placa de Parada Obrigatória
Placa de Nome da Rua

Detalhe – Sinalização Vertical
1:25

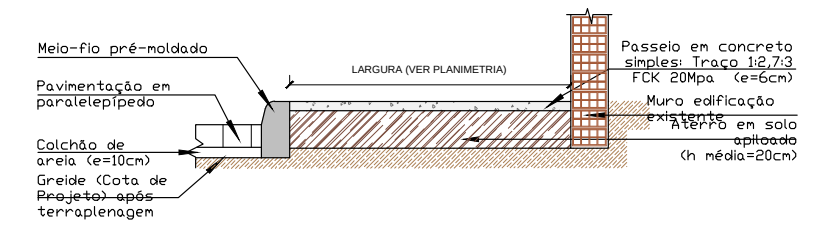
Meio-fio pré-moldado
Pavimentação em paralelepípedo
Colchão de areia (e=10cm)
Greide (Cota de Projeto) após terraplenagem
LARGURA (VER PLANIMETRIA)
Passeio em concreto simples: Traço 1:2:7:3 FCK 20Mpa (e=6cm)
Muro edificação existente
Aterro em solo apiloado (h média=20cm)

Detalhe 01 – Passeio Para Trechos s/ Alvenaria de 1 Vez

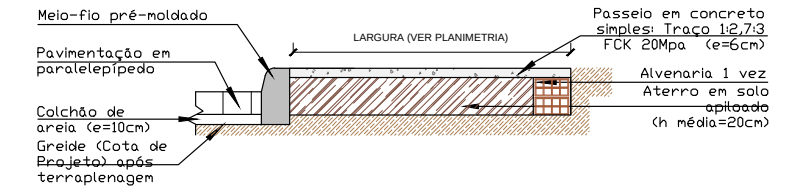
Meio-fio pré-moldado
Pavimentação em paralelepípedo
Colchão de areia (e=10cm)
Greide (Cota de Projeto) após terraplenagem
LARGURA (VER PLANIMETRIA)
Passeio em concreto simples: Traço 1:2:7:3 FCK 20Mpa (e=6cm)
Alvenaria 1 vez
Aterro em solo apiloado (h média=20cm)

Detalhe 02 – Passeio Para Trechos c/ Alvenaria de 1 Vez

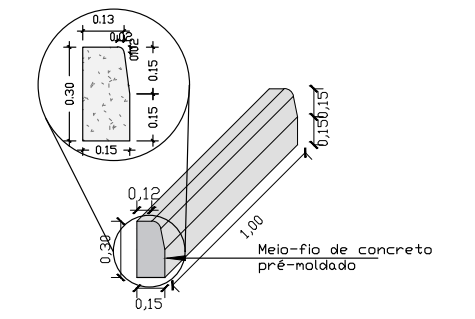
0.13
0.30
0.15
0.12
0.15
1.00
Meio-fio de concreto pré-moldado

Detalhe – Meio-fio

Nota: Para o cálculo do quantitativo de concreto do passeio público, considera-se a dimensão da largura conforme indicado nos detalhe dos passeios.

Seção-Tipo de Pavimentação

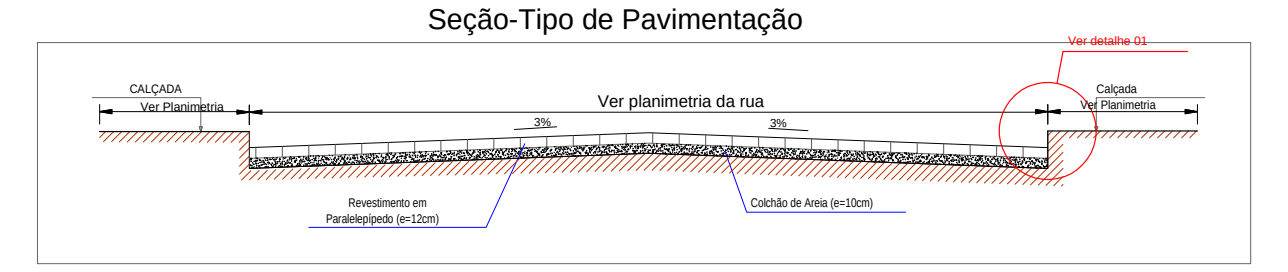
CALÇADA
Ver Planimetria
Ver planimetria da rua
2%
2%
Ver detalhe 01
Calçada
Ver Planimetria
Revestimento em Paralelepípedo (e=12cm)
Colchão de Areia (e=10cm)

Sem Escala

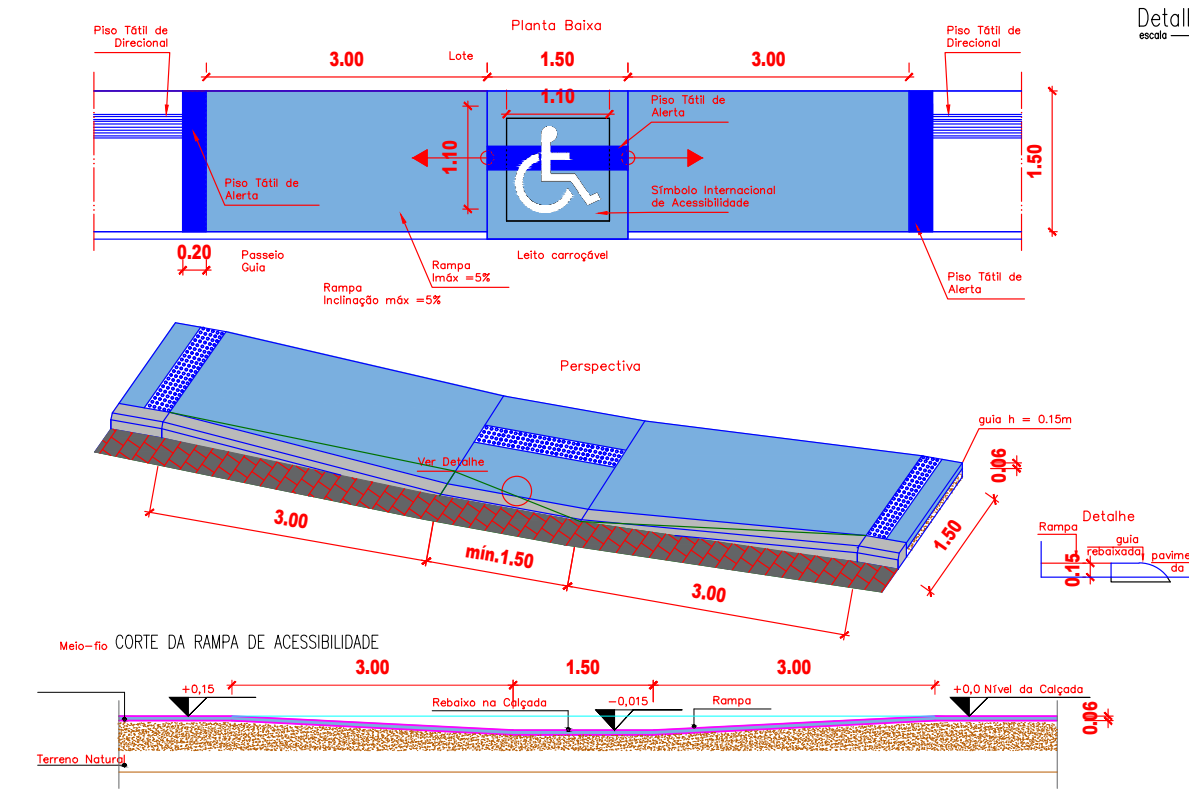
Planta Baixa
Piso Tátil de Direcional
3.00
Lote
1.50
3.00
1.10
Piso Tátil de Alerta
1.50
Símbolo internacional de Acessibilidade
0.20
Passeio Guia
Rampa imáx =5%
Leito carroçável
Rampa inclinação máx =5%
Perspectiva
guia h = 0.15m
3.00
min.1.50
3.00
1.50
0.06
Detalhe
Meio-fio CORTE DA RAMPA DE ACESSIBILIDADE
3.00
1.50
3.00
+0.15
Rebaixo na Calçada
+0.015
Rampa
±0.0 Nível da Calçada
Terreno Natural

Detalhe – Rampa de Acessibilidade
1:50

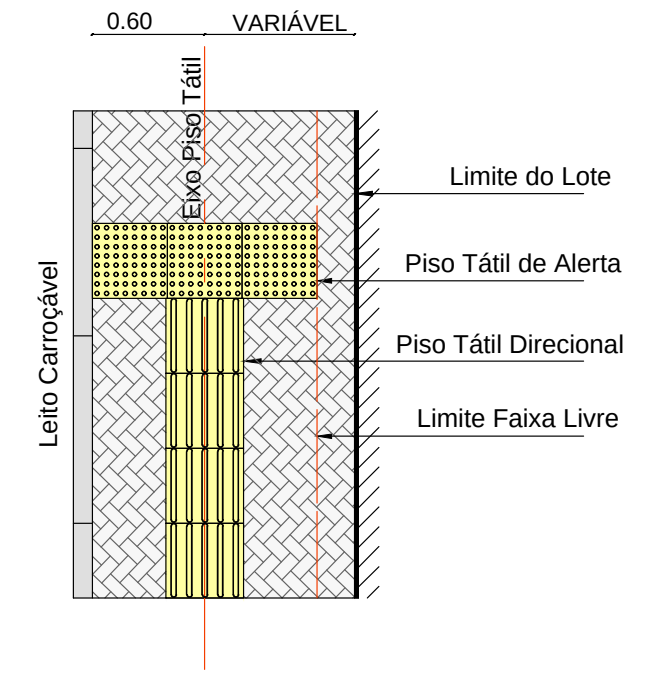
0.60
VARIÁVEL
Eixo Piso Tátil
Limite do Lote
Piso Tátil de Alerta
Piso Tátil Direcional
Limite Faixa Livre
Leito Carroçável

Detalhe 01 – Início/Fim Piso Tátil (D01-IFPT)

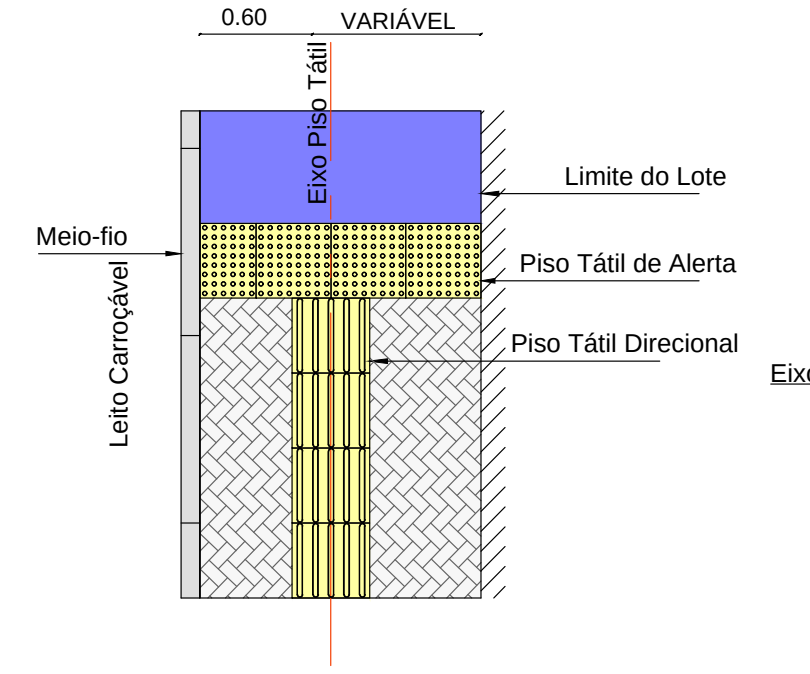
0.60
VARIÁVEL
Eixo Piso Tátil
Meio-fio
Limite do Lote
Piso Tátil de Alerta
Piso Tátil Direcional
Leito Carroçável

Detalhe 02 – Encontro Piso Tátil com Rampa (D02-EPTR)

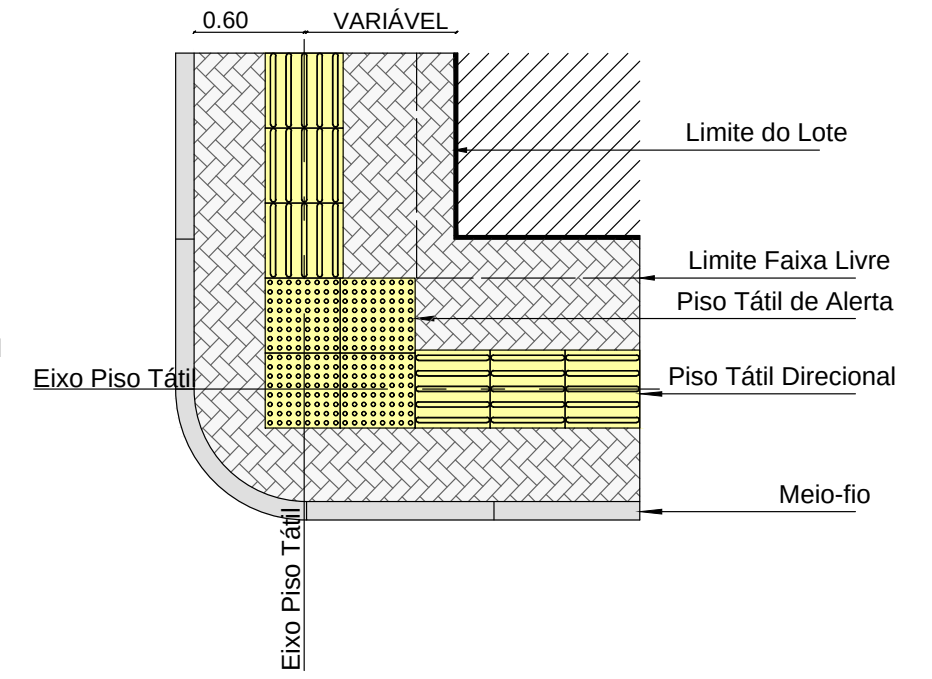
0.60
VARIÁVEL
Limite do Lote
Limite Faixa Livre
Piso Tátil de Alerta
Piso Tátil Direcional
Eixo Piso Tátil
Meio-fio
Eixo Piso Tátil

Detalhe 03 – Mudança de direção – Entre 90° e 150° (D03-MD)

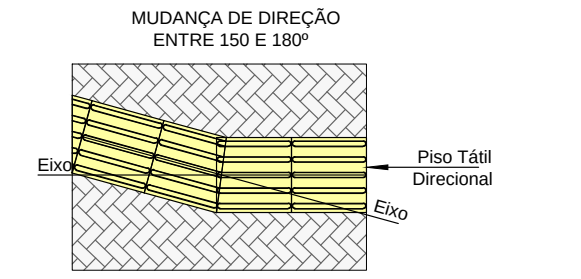
MUDANÇA DE DIREÇÃO ENTRE 150 E 180°
Eixo
Piso Tátil Direcional
Eixo

Detalhe 04 – Mudança de direção entre 150° e 180° (D04-MD)

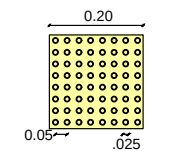

Detalhe 05 – Piso Tátil de Alerta

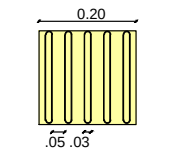

Detalhe 06 – Piso Tátil Direcional

PROPRIETÁRIO Prefeitura Municipal de Coremas- PB
PROJETISTA Kleber Sá de Oliveira
Kleber Sá de Oliveira
Engenheiro Civil
CREA 1602582780

EPE
EMPRESA PARAIBA DE ENGENHARIA
PROJETO: PAVIMENTAÇÃO DE RUAS E VIAS
LOCAL: MUNICÍPIO DE COREMAS - PB
PROPRIETÁRIO: PREFEITURA MUNICIPAL DE COREMAS - PB
FOLHA: 03/07
ESCALA: Indicadas
DESENHOS: Indicados
RESPONSÁVEL TÉCNICO: Kleber Sá de Oliveira Crea: 160391676-8
ANOTAÇÕES:
ARQUIVO: PAV_COREMAS_FINAL P+B_2022.dwg
DESENHO: Diego Medeiros
DATA: SET - 2022