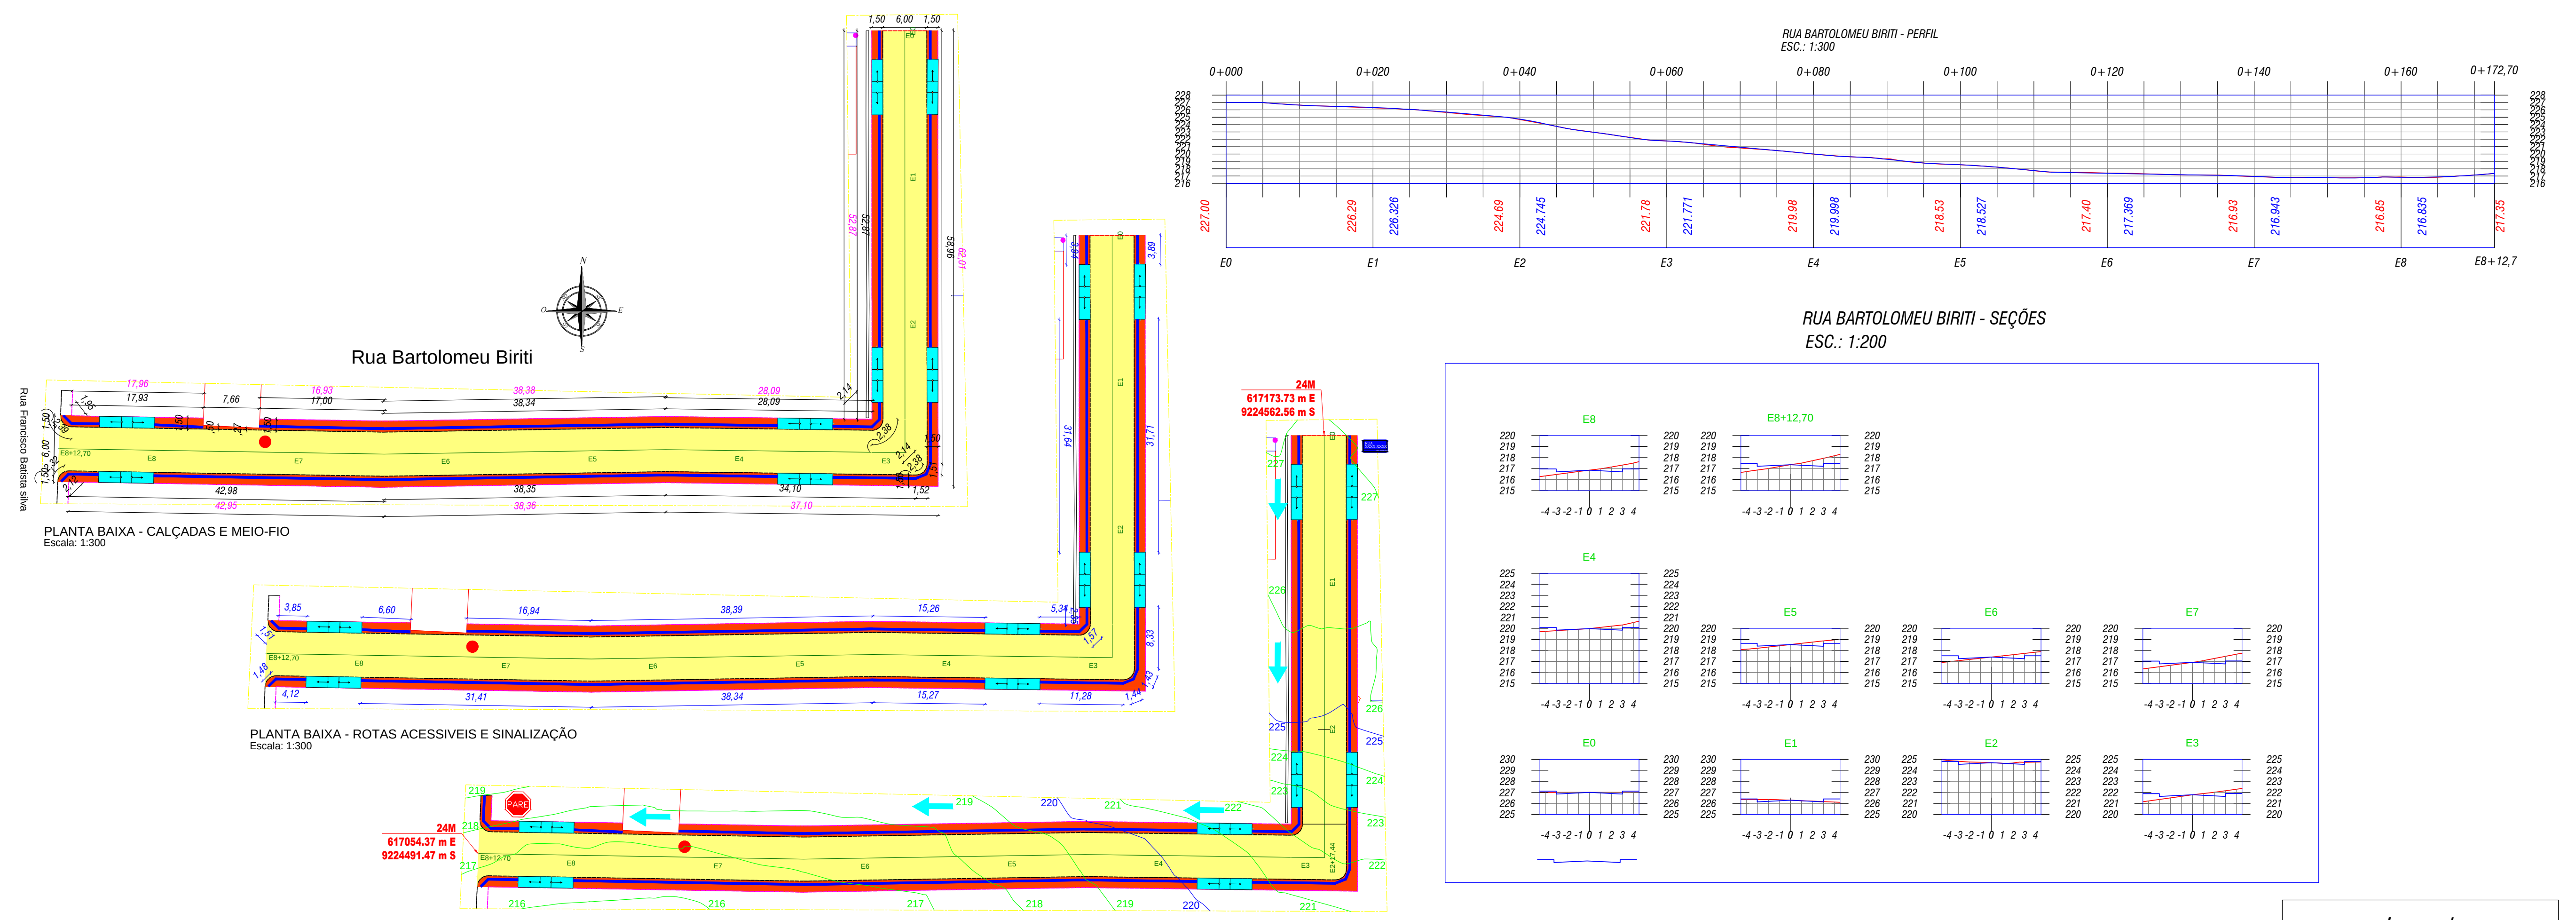
Rua Bartolomeu Biriti
Rua Francisco Batista silva
N
O
E
S
1,50 6,00 1,50
17,96
17,93
7,66
16,93
17,00
38,38
38,34
28,09
28,09
2,14
2,38
52,87
52,87
58,96
60,07
42,98
42,95
38,35
38,36
34,10
37,10
1,52
E8+12,70
E8
E7
E6
E5
E4
E3
E2
E1
E0
PLANTA BAIXA - CALÇADAS E MEIO-FIO
Escala: 1:300
3,85
6,60
16,94
38,39
15,26
5,34
3,69
31,64
31,71
8,33
4,12
31,41
38,34
15,27
11,28
1,44
PLANTA BAIXA - ROTAS ACESSIVEIS E SINALIZAÇÃO
Escala: 1:300
24M
617173.73 m E
9224562.56 m S
227
226
225
224
223
222
221
220
219
218
217
216
24M
617054.37 m E
9224491.47 m S
PARE
E2+17,44
PLANTA BAIXA - ROTAS ACESSIVEIS E SINALIZAÇÃO
Escala: 1:300
RUA BARTOLOMEU BIRITI - PERFIL
ESC.: 1:300
0+000
0+020
0+040
0+060
0+080
0+100
0+120
0+140
0+160
0+172,70
227,00
226,29
226,326
224,69
224,745
221,78
221,771
219,98
219,998
218,53
218,527
217,40
217,369
216,93
216,943
216,85
216,835
217,35
E0
E1
E2
E3
E4
E5
E6
E7
E8
E8+12,7
RUA BARTOLOMEU BIRITI - SEÇÕES
ESC.: 1:200
E8
E8+12,70
E4
E5
E6
E7
E0
E1
E2
E3
-4 -3 -2 -1 0 1 2 3 4

Legenda

Pavimentação

- 🟨 Pavimentação à Construir
- ▨ Pavimento Existente
- — Meio-fio Existente
- - - Meio-fio Projetado
- - - Cordão em Granito
- - - Alvenaria de 1 vez
- — Cerca
- ➡ Sentido do Caimento da água

Passeio

- 🟥 Calçadas à Construir
- 🟩 Calçadas Existentes
- 🟦 Piso Tátil
- ▭ Rampa de Acesso
- ● Poste Existente
- ● Poço de Visita (PV)
- ● Árvore
- — Edificação Existente
- — Lote Projetado

Sinalização

- PARE Placa de Parada Obrigatória
- RUA XXXX XXXX Placa com Nome da rua

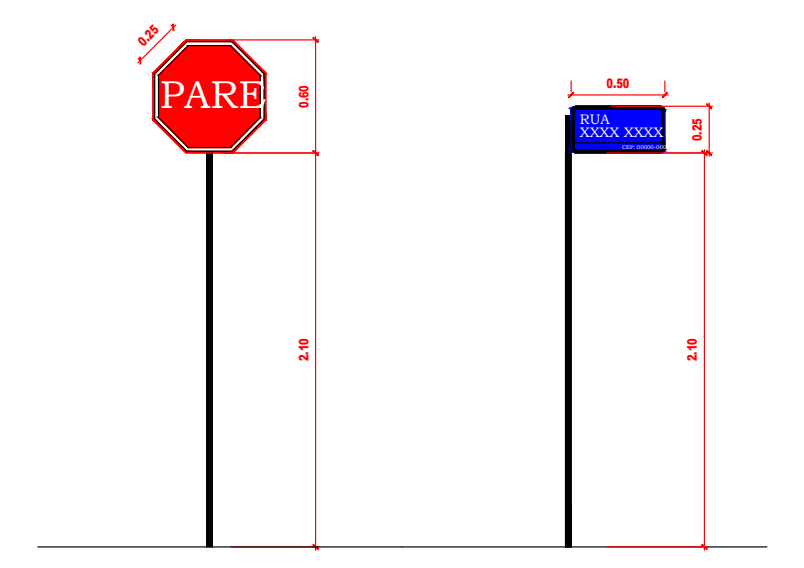
PARE
0.25
0.60
2.10
RUA
XXXX XXXX
0.50
0.25
Placa de Parada Obrigatória
Placa de Nome da Rua

Detalhe – Sinalização Vertical
1:25

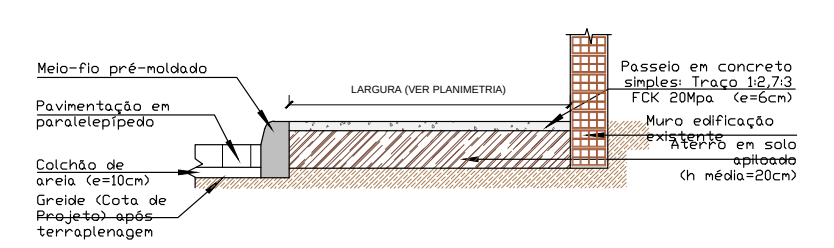
Meio-fio pré-moldado
Pavimentação em paralelepípedo
Colchão de areia (e=10cm)
Greide (Cota de Projeto) após terraplenagem
LARGURA (VER PLANIMETRIA)
Passeio em concreto simples: Traço 1:2,7:3 FCK 20Mpa (e=6cm)
Muro edificação existente
Aterro em solo apiloado (h média=20cm)

Detalhe 01 – Passeio Para Trechos s/ Alvenaria de 1 Vez

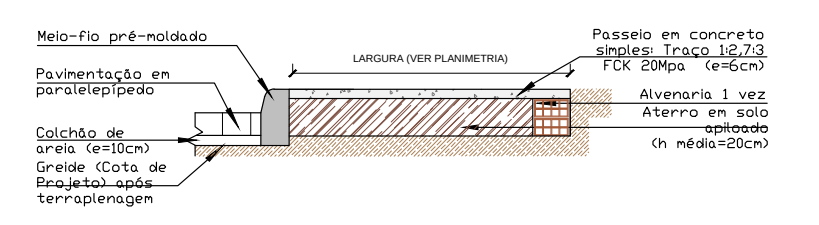
Meio-fio pré-moldado
Pavimentação em paralelepípedo
Colchão de areia (e=10cm)
Greide (Cota de Projeto) após terraplenagem
LARGURA (VER PLANIMETRIA)
Passeio em concreto simples: Traço 1:2,7:3 FCK 20Mpa (e=6cm)
Alvenaria 1 vez
Aterro em solo apiloado (h média=20cm)

Detalhe 02 – Passeio Para Trechos c/ Alvenaria de 1 Vez

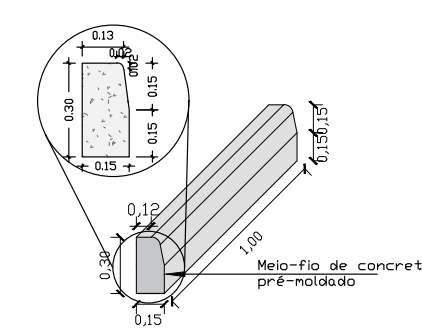
0.13
0.30
0.15
0.15
0.12
0.15
1.00
Meio-fio de concreto pré-moldado

Detalhe – Meio-fio

Nota: Para o cálculo do quantitativo de concreto do passeio público, considera-se a dimensão da largura conforme indicado nos detalhe dos passeios.

Seção-Tipo de Pavimentação

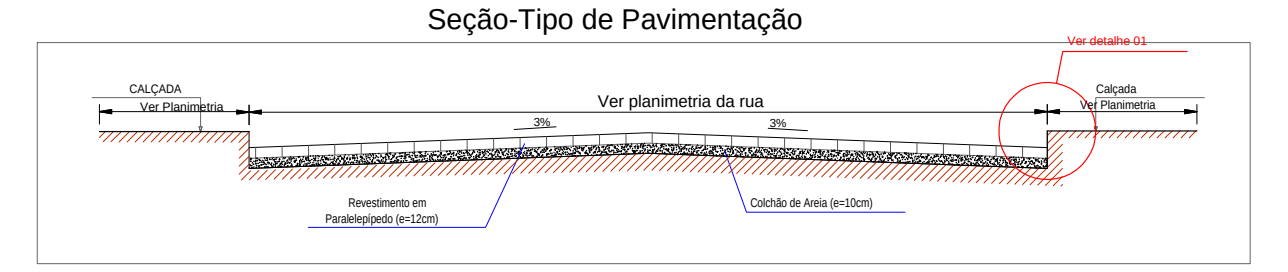
CALÇADA
Ver Planimetria
Ver planimetria da rua
3%
3%
Ver detalhe 01
Calçada
Ver Planimetria
Revestimento em Paralelepípedo (e=12cm)
Colchão de Areia (e=10cm)

Sem Escala

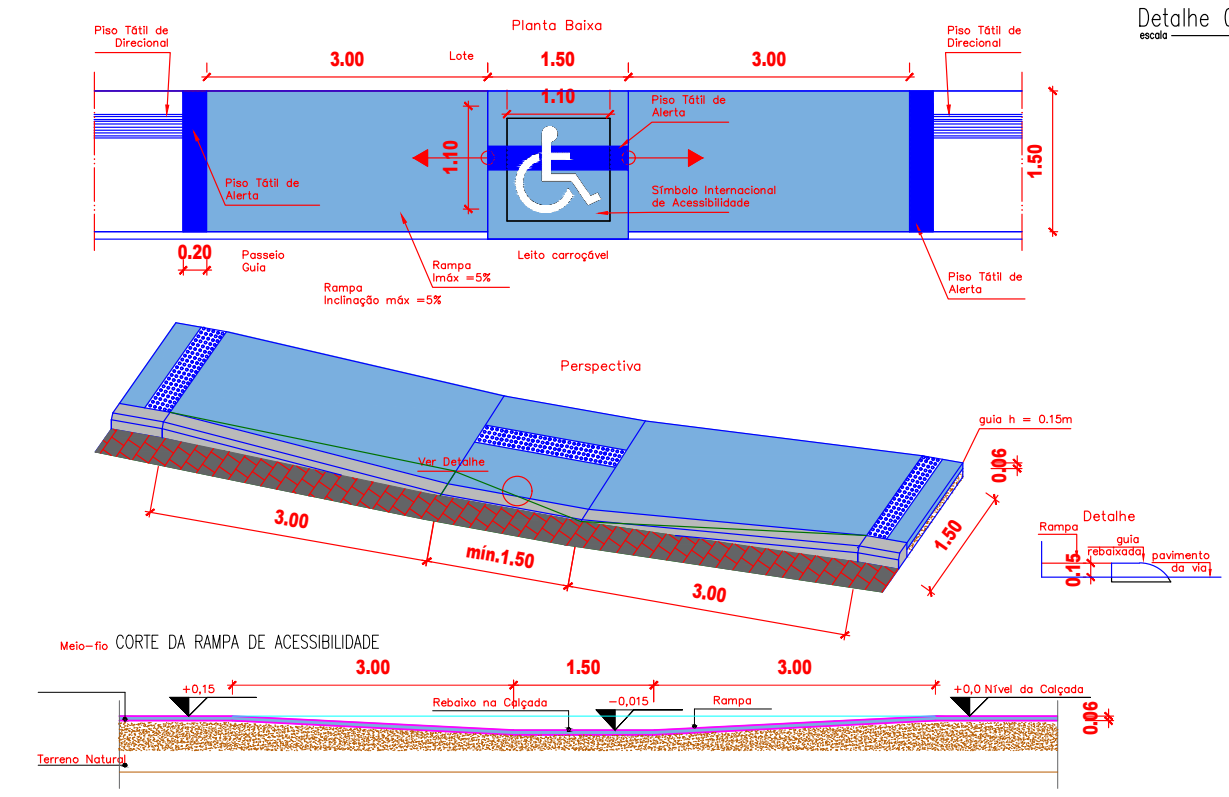
Planta Baixa
Piso Tátil de Direcional
3.00
Lote
1.50
3.00
1.10
1.10
Piso Tátil de Alerta
Símbolo Internacional de Acessibilidade
0.20
Passeio
Guia
Rampa
Inclinação máx =5%
Rampa
máx =5%
Leito carroçável
1.50
Perspectiva
guia h = 0.15m
0.06
Detalhe
Rampa
guia rebaixada
pavimento da via
0.15
3.00
min.1.50
3.00
Meio-fio
CORTE DA RAMPA DE ACESSIBILIDADE
3.00
1.50
3.00
+0.15
Rebaixo na Calçada
-0.015
Rampa
+0.0 Nível da Calçada
Terreno Natural

Detalhe – Rampa de Acessibilidade
1:50

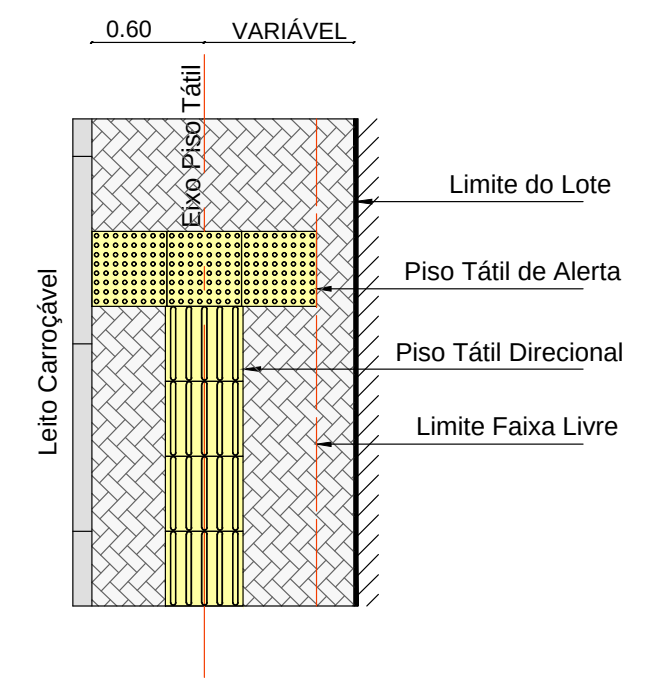
0.60
VARIÁVEL
Eixo Piso Tátil
Leito Carroçável
Limite do Lote
Piso Tátil de Alerta
Piso Tátil Direcional
Limite Faixa Livre

Detalhe 01 – Início/Fim Piso Tátil (D01–IFPT)

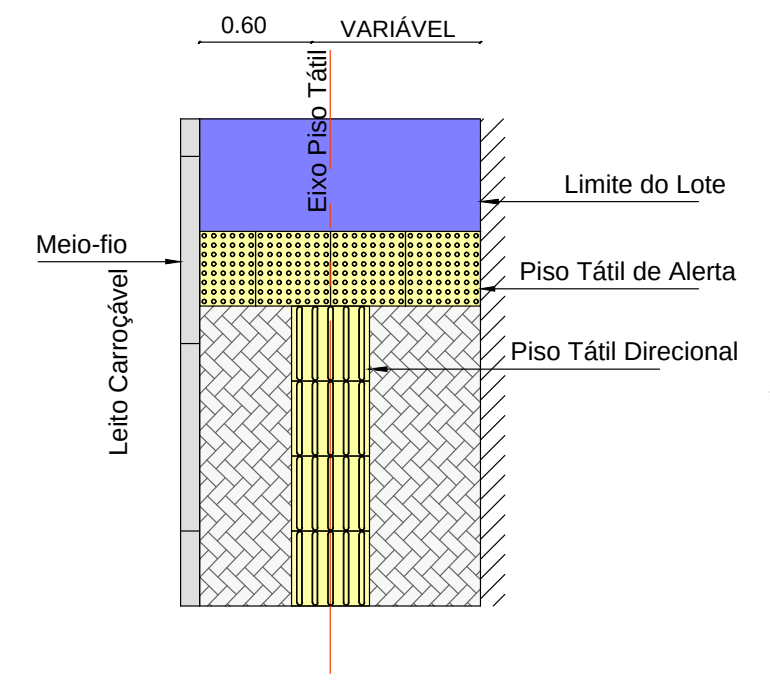
0.60
VARIÁVEL
Eixo Piso Tátil
Meio-fio
Leito Carroçável
Limite do Lote
Piso Tátil de Alerta
Piso Tátil Direcional

Detalhe 02 – Encontro Piso Tátil com Rampa (D02–EPTR)

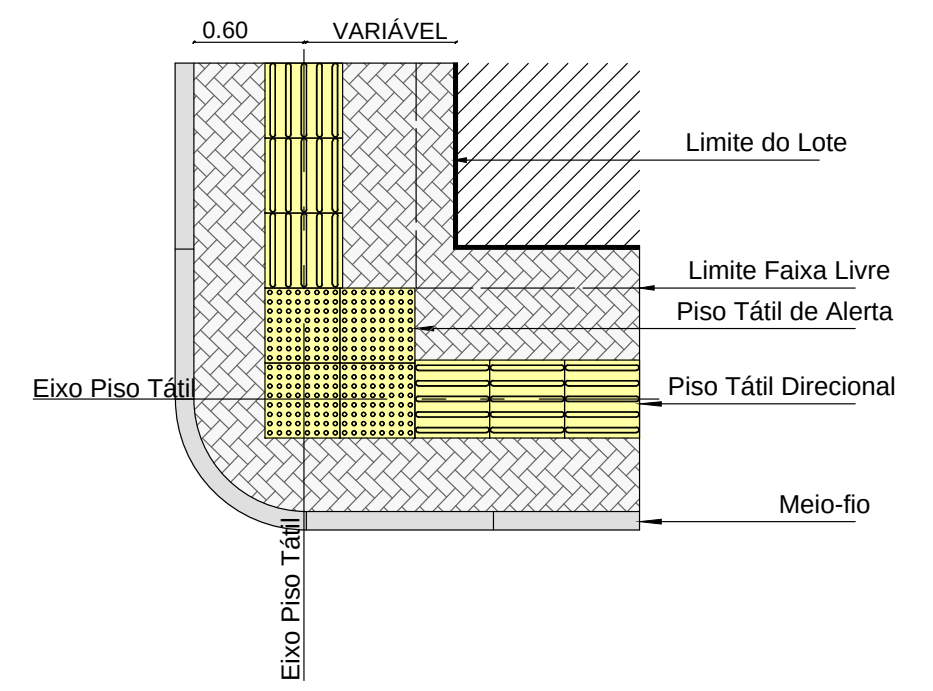
0.60
VARIÁVEL
Limite do Lote
Limite Faixa Livre
Piso Tátil de Alerta
Eixo Piso Tátil
Piso Tátil Direcional
Meio-fio
Eixo Piso Tátil

Detalhe 03 – Mudança de direção – Entre 90° e 150° (D03–MD)

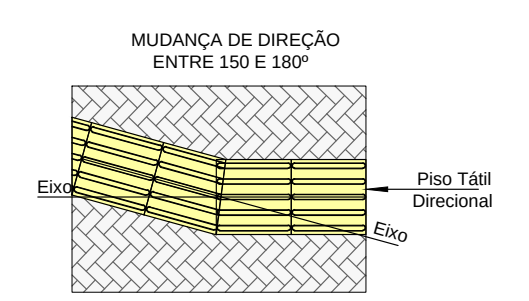
MUDANÇA DE DIREÇÃO
ENTRE 150 E 180º
Eixo
Piso Tátil Direcional
Eixo

Detalhe 04 – Mudança de direção entre 150° e 180° (D04–MD)

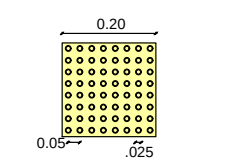

Detalhe 05 – Piso Tátil de Alerta

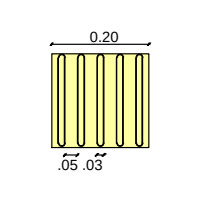

Detalhe 06 – Piso Tátil Direcional

PROPRIETÁRIO Prefeitura Municipal de Coremas- PB

Kleber Sá de Oliveira
Engenheiro Civil
CREA 1602582780

PROJETISTA Kleber Sá de Oliveira

EPE
EMPRESA PARAIBA DE ENGENHARIA

PROJETO:
PAVIMENTAÇÃO DE RUAS E VIAS
LOCAL:
MUNICÍPIO DE COREMAS - PB
PROPRIETÁRIO:
PREFEITURA MUNICIPAL DE COREMAS - PB

FOLHA 04/07
ESCALA: Indicadas
DESENHOS: Indicados
RESPONSÁVEL TÉCNICO:
Kleber Sá de Oliveira
Crea: 160391676-8
ANOTAÇÕES:
ARQUIVO:
PAV_COREMAS_FINAL_2022.dwg
DESENHO: Diego Medeiros
DATA: SET - 2022

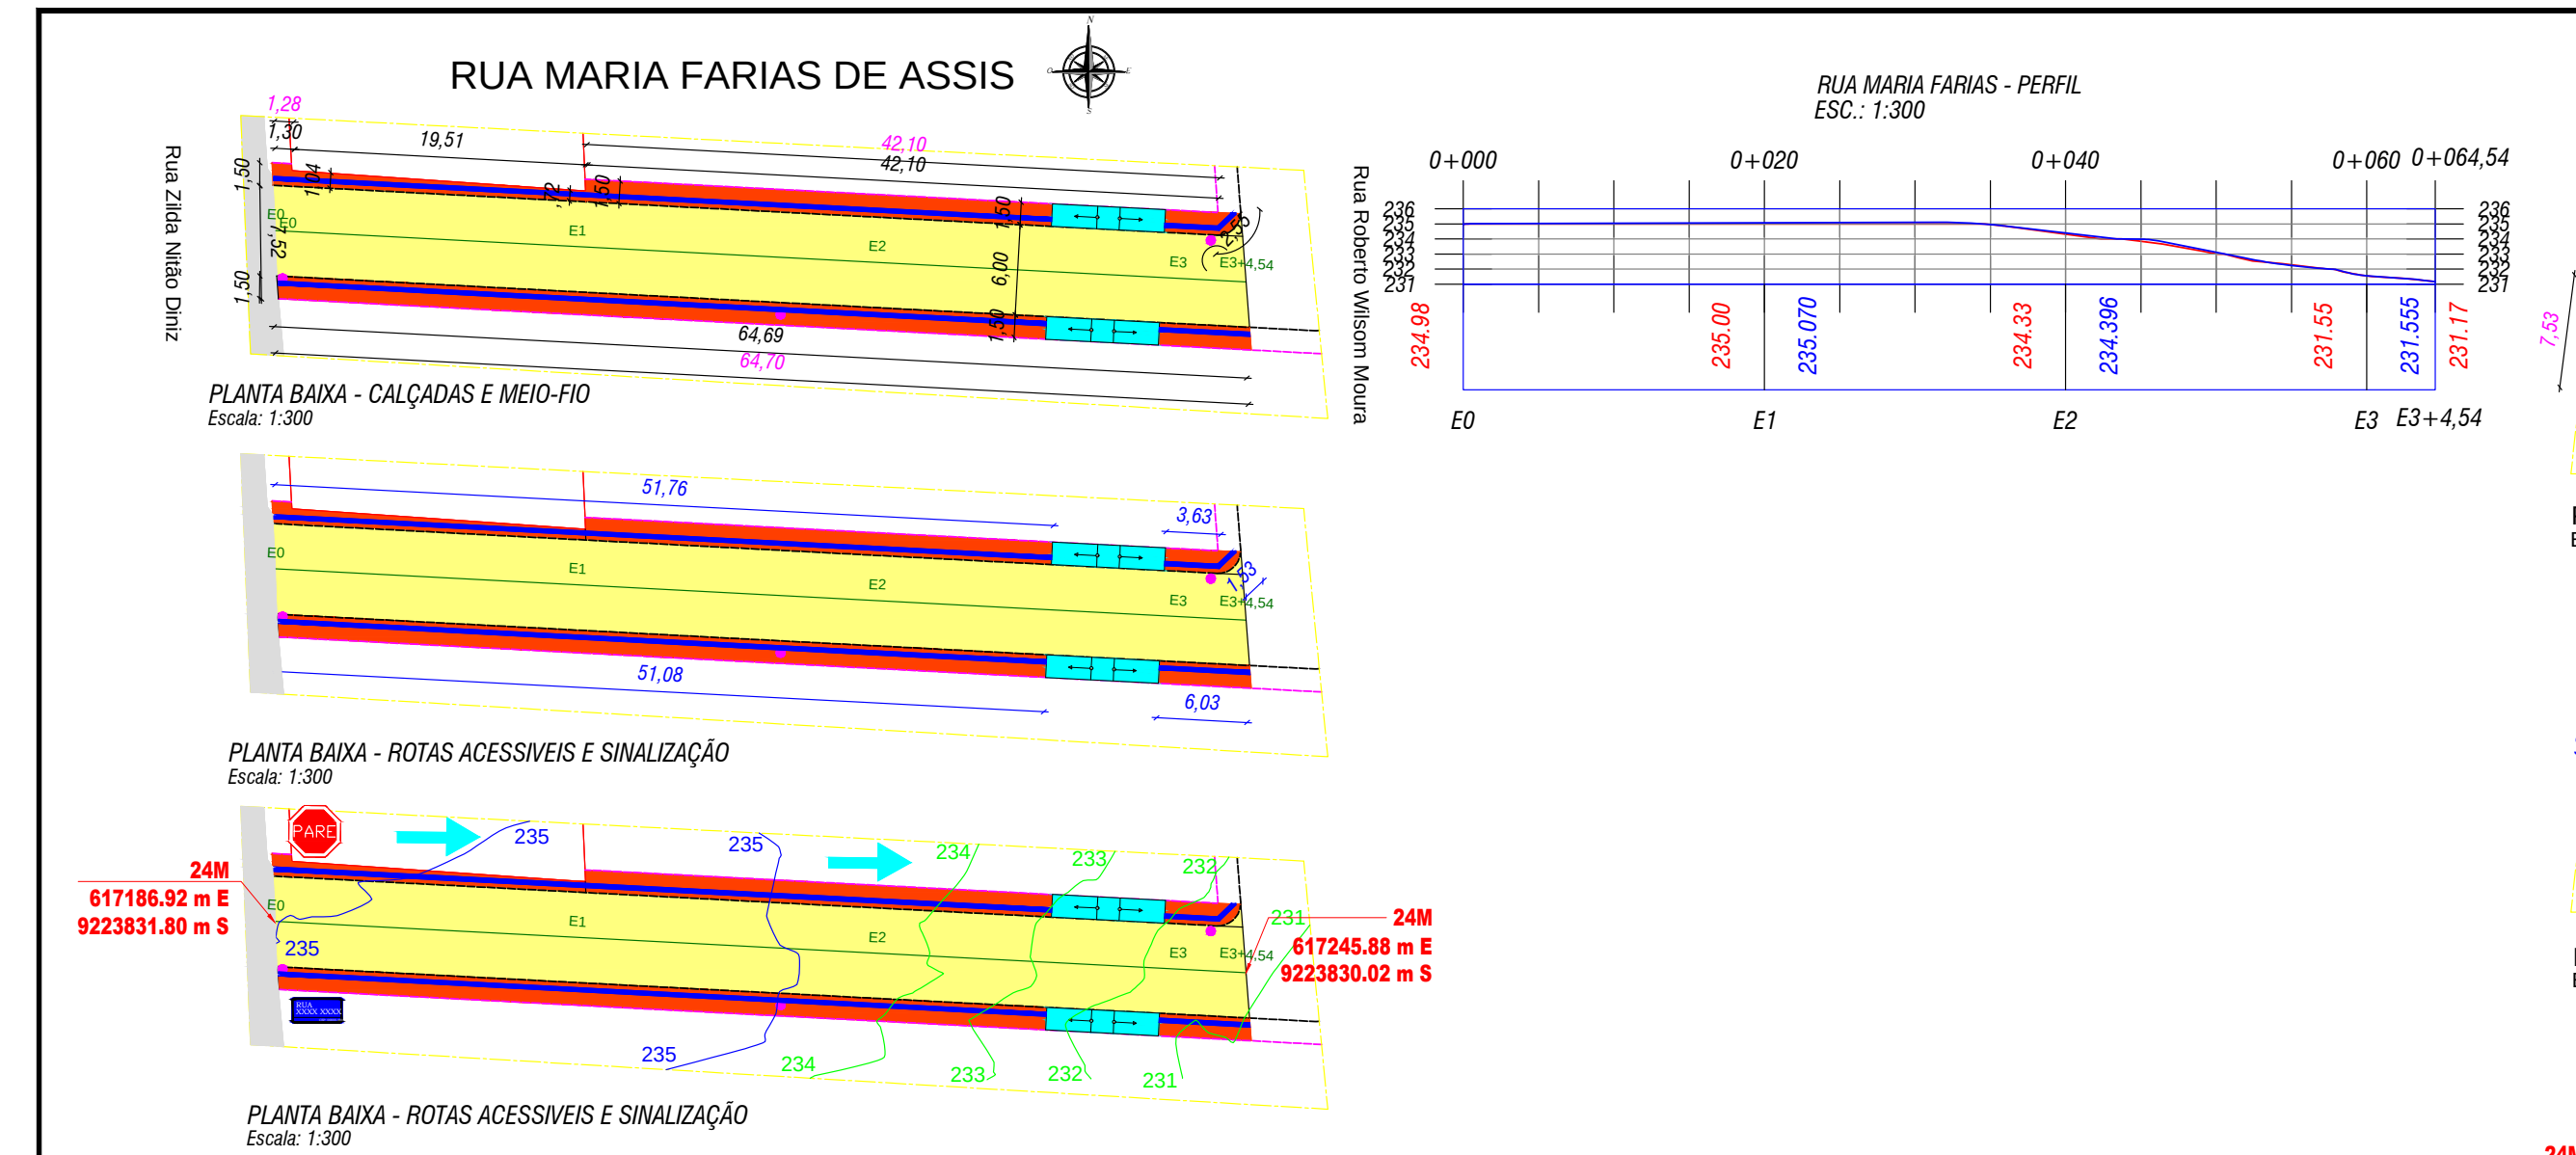
RUA MARIA FARIAS DE ASSIS
Rua Zilda Nitão Diniz
Rua Roberto Wilsom Moura
1,28
1,30
19,51
42,10
42,10
1,50
6,00
1,50
64,69
64,70
E0
E1
E2
E3
E3+4,54
PLANTA BAIXA - CALÇADAS E MEIO-FIO
Escala: 1:300
51,76
3,63
51,08
6,03
PLANTA BAIXA - ROTAS ACESSIVEIS E SINALIZAÇÃO
Escala: 1:300
PARE
235
234
233
232
231
24M
617186.92 m E
9223831.80 m S
24M
617245.88 m E
9223830.02 m S
PLANTA BAIXA - ROTAS ACESSIVEIS E SINALIZAÇÃO
Escala: 1:300
RUA MARIA FARIAS - PERFIL
ESC.: 1:300
0+000
0+020
0+040
0+060
0+064,54
234.98
235.00
235.070
234.33
234.396
231.55
231.555
231.17
E0
E1
E2
E3
E3+4,54

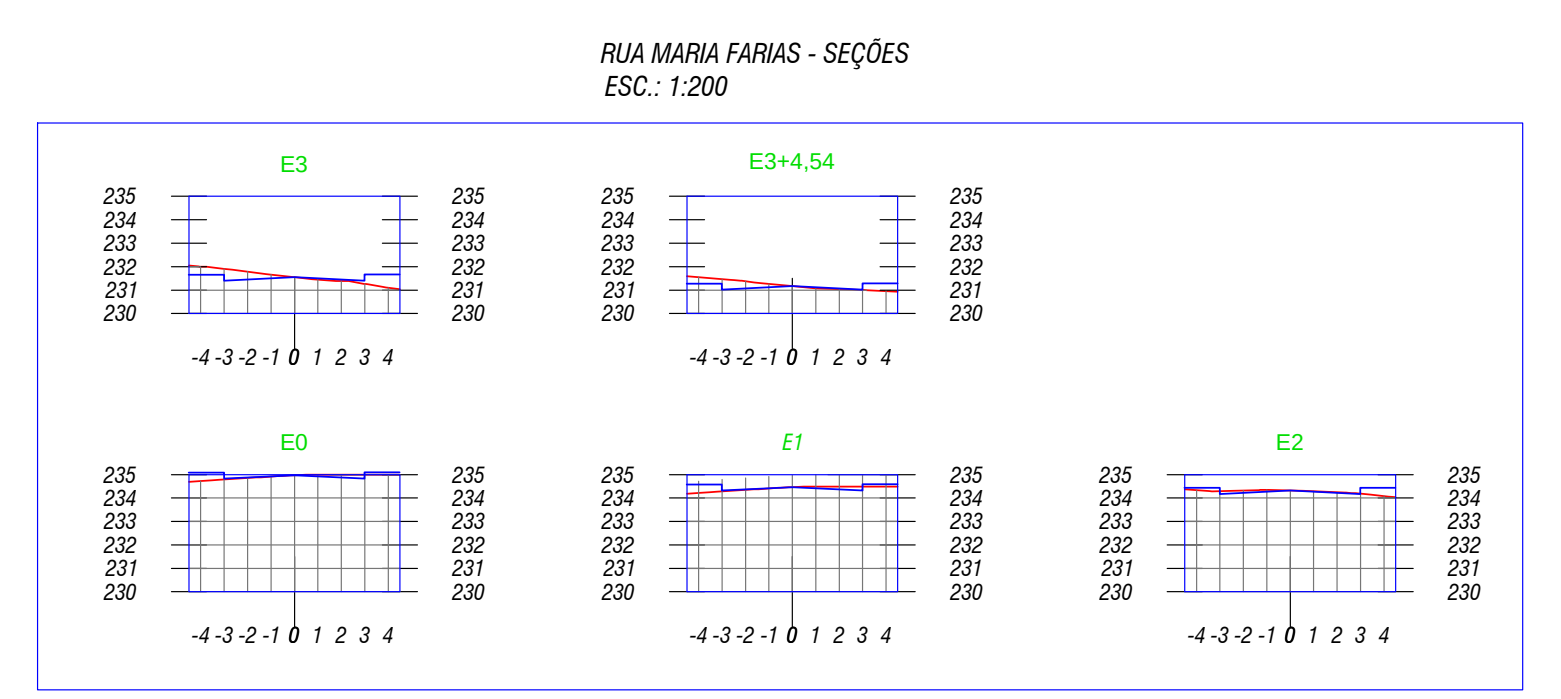
RUA MARIA FARIAS - SEÇÕES
ESC.: 1:200
E3
E3+4,54
E0
E1
E2
235
234
233
232
231
230
-4 -3 -2 -1 0 1 2 3 4

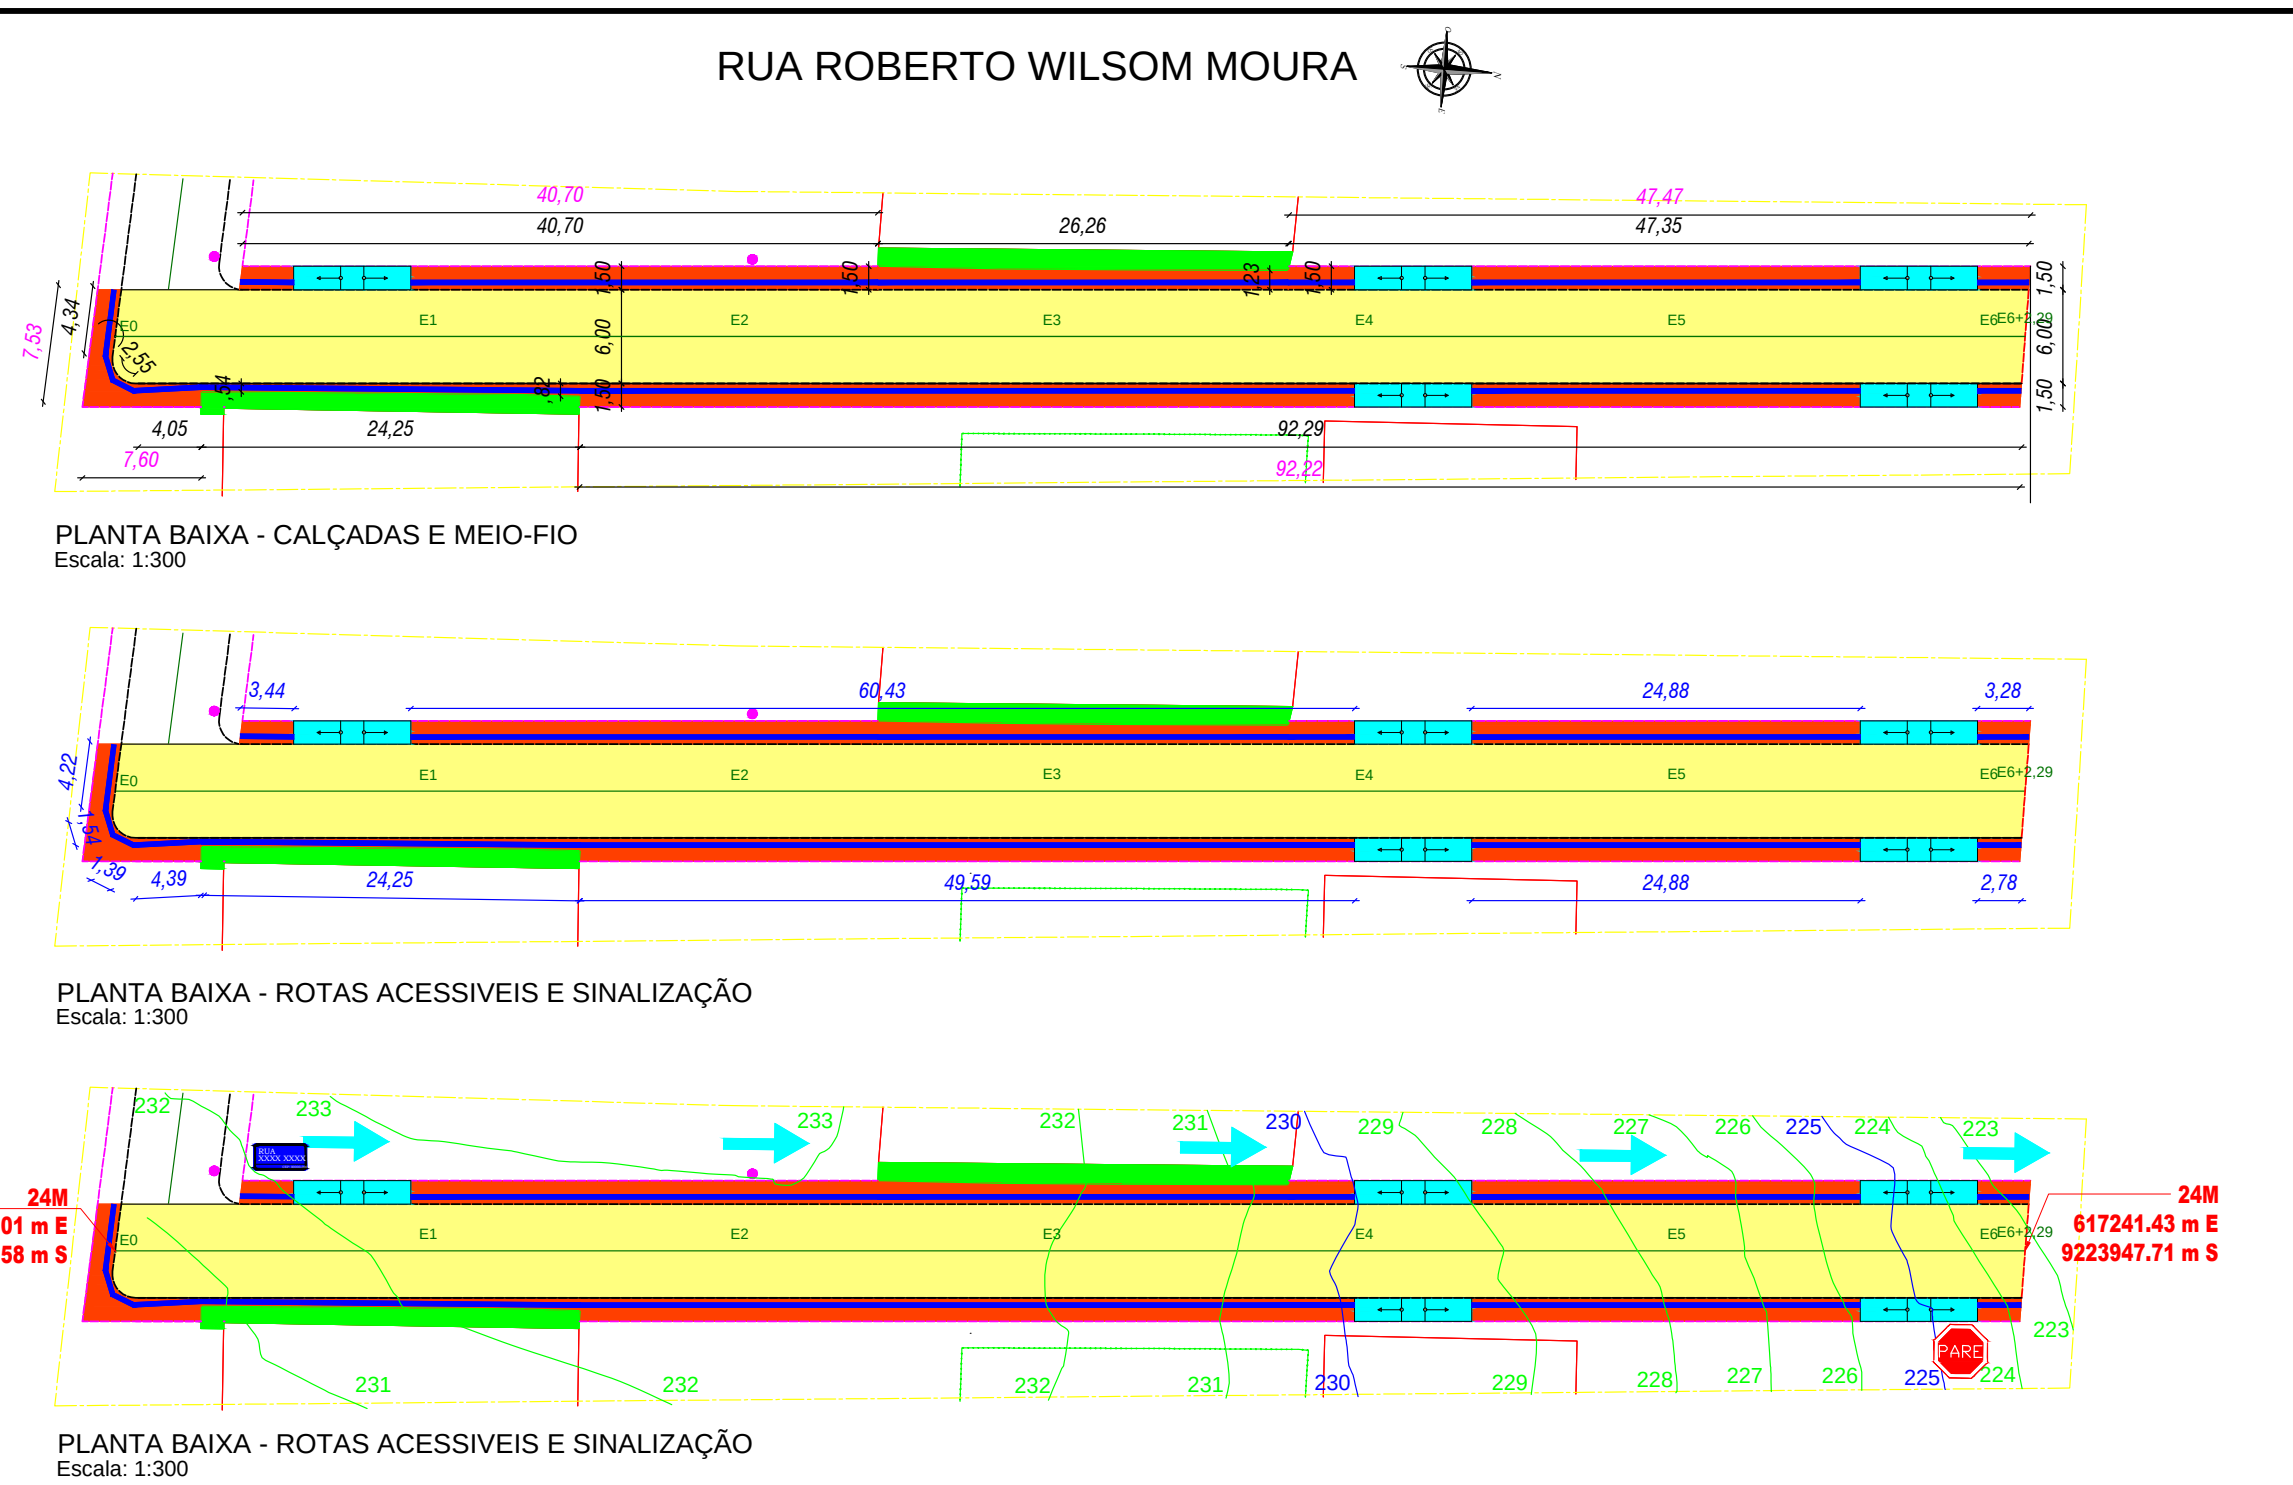
RUA ROBERTO WILSOM MOURA
40,70
40,70
26,26
47,47
47,35
7,53
4,34
1,50
6,00
1,50
4,05
24,25
7,60
92,29
92,22
E0
E1
E2
E3
E4
E5
E6
E6+2,29
PLANTA BAIXA - CALÇADAS E MEIO-FIO
Escala: 1:300
3,44
60,43
24,88
3,28
4,22
4,39
24,25
49,59
24,88
2,78
PLANTA BAIXA - ROTAS ACESSIVEIS E SINALIZAÇÃO
Escala: 1:300
24M
617249.01 m E
9223830.58 m S
233
232
231
230
229
228
227
226
225
224
223
PARE
24M
617241.43 m E
9223947.71 m S
PLANTA BAIXA - ROTAS ACESSIVEIS E SINALIZAÇÃO
Escala: 1:300

Legenda

Pavimentação

- 🟨 Pavimentação à Construir
- ▨ Pavimento Existente
- — Meio-fio Existente
- - - Meio-fio Projetado
- - - Cordão em Granito
- - - Alvenaria de 1 vez
- — Cerca
- ➡ Sentido do Caimento da água

Passeio

- 🟥 Calçadas à Construir
- 🟩 Calçadas Existentes
- 🟦 Piso Tátil
- ▭ Rampa de Acesso
- ● Poste Existente
- ● Poço de Visita (PV)
- ● Árvore
- — Edificação Existente
- — Lote Projetado

Sinalização

- PARE Placa de Parada Obrigatória
- RUA XXXX XXXX Placa com Nome da rua

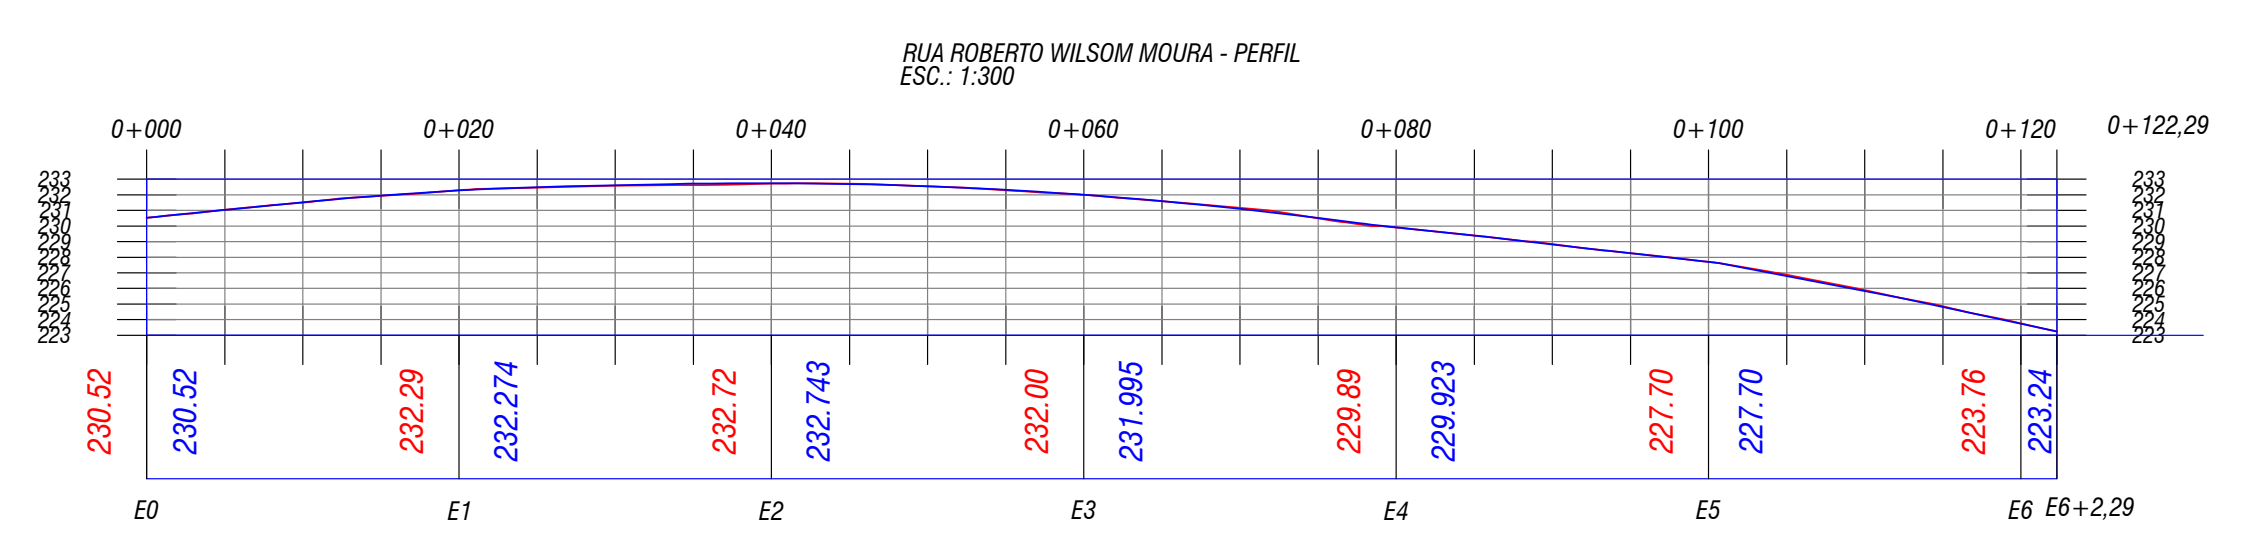

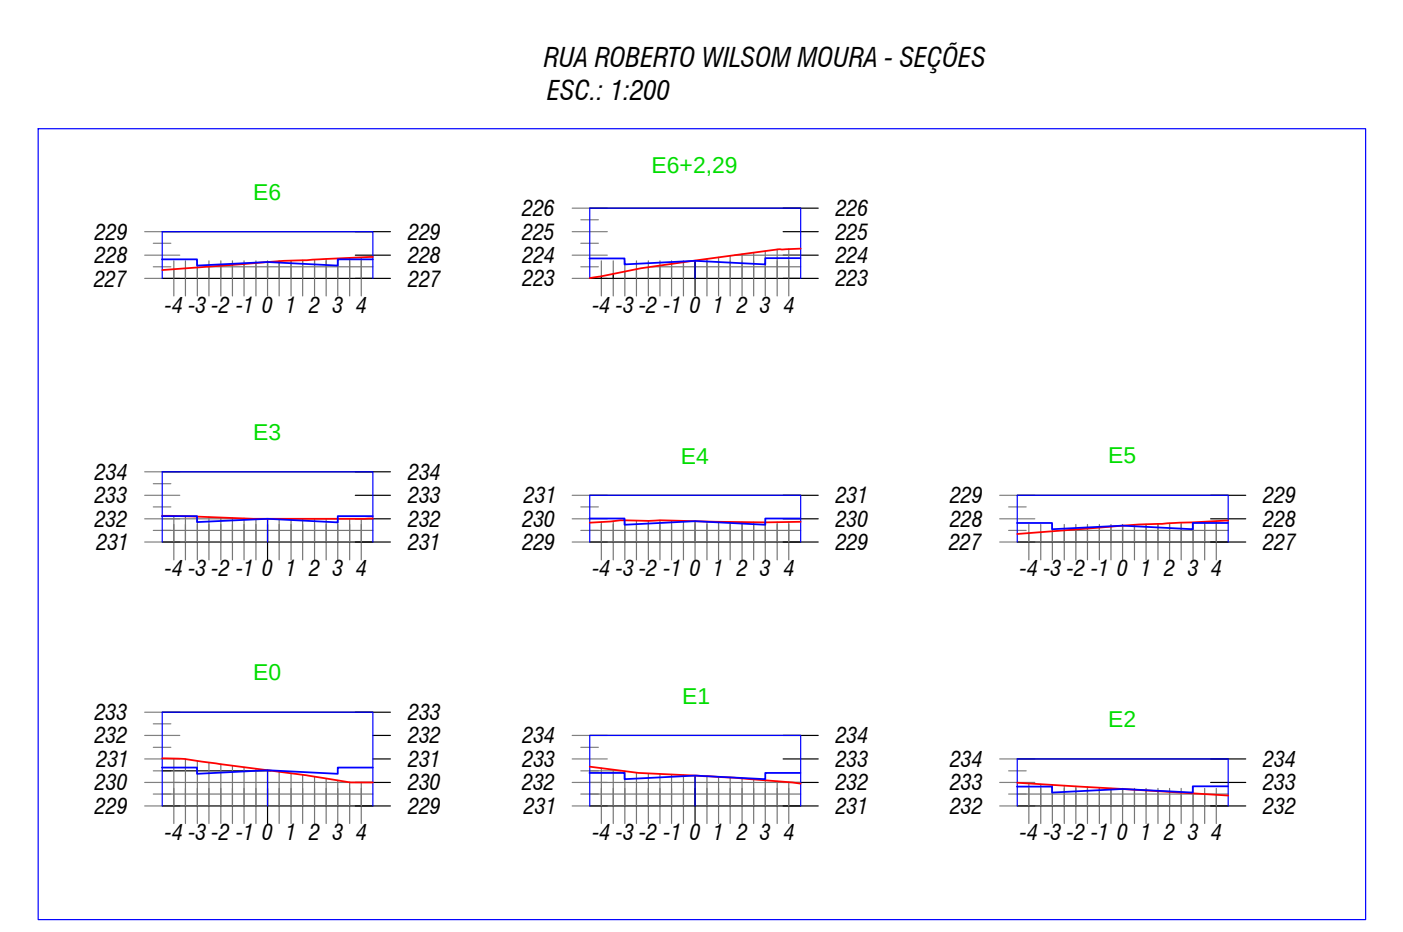
RUA ROBERTO WILSOM MOURA - SEÇÕES
ESC.: 1:200
E6
E6+2,29
E3
E4
E5
E0
E1
E2
-4 -3 -2 -1 0 1 2 3 4

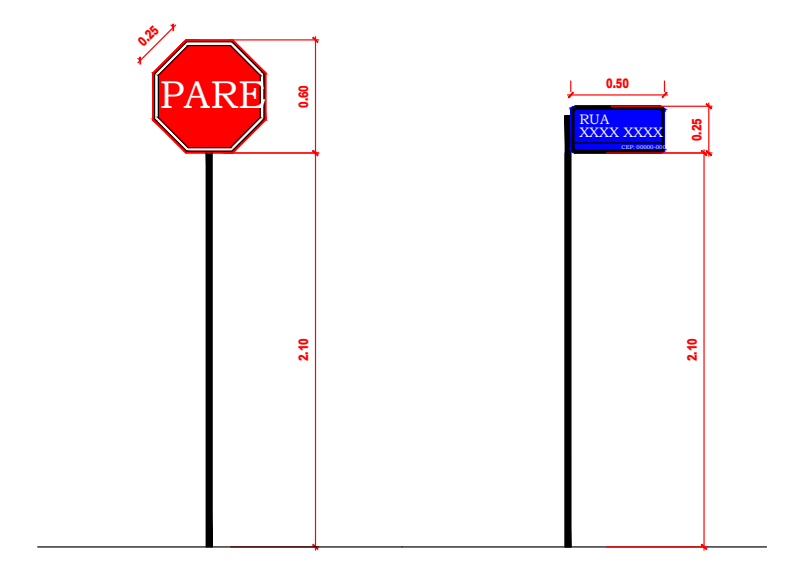
PARE
0.25
0.60
2.10
RUA
XXXX XXXX
0.50
0.25
Placa de Parada Obrigatória
Placa de Nome da Rua

Detalhe – Sinalização Vertical
1:25

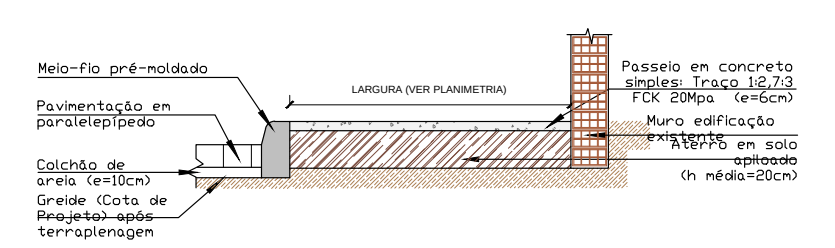
Meio-fio pré-moldado
Pavimentação em paralelepípedo
Colchão de areia (e=10cm)
Greide (Cota de Projeto) após terraplenagem
LARGURA (VER PLANIMETRIA)
Passeio em concreto simples: Traço 1:2,7:3 FCK 20Mpa (e=6cm)
Muro edificação existente
Aterro em solo apiloado (h média=20cm)

Detalhe 01 – Passeio Para Trechos s/ Alvenaria de 1 Vez

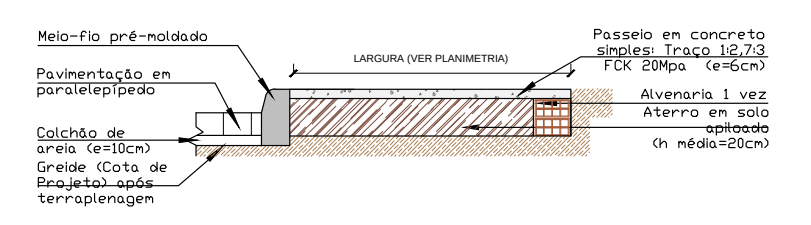
Meio-fio pré-moldado
Pavimentação em paralelepípedo
Colchão de areia (e=10cm)
Greide (Cota de Projeto) após terraplenagem
LARGURA (VER PLANIMETRIA)
Passeio em concreto simples: Traço 1:2,7:3 FCK 20Mpa (e=6cm)
Alvenaria 1 vez
Aterro em solo apiloado (h média=20cm)

Detalhe 02 – Passeio Para Trechos c/ Alvenaria de 1 Vez

Seção-Tipo de Pavimentação

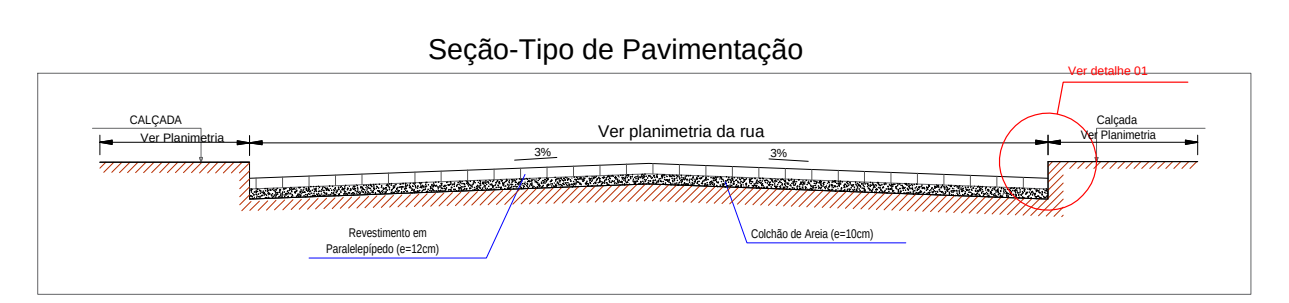
CALÇADA
Ver Planimetria
Ver planimetria da rua
3%
3%
Ver detalhe 01
Calçada
Ver Planimetria
Revestimento em Paralelepípedo (e=12cm)
Colchão de Areia (e=10cm)

Sem Escala

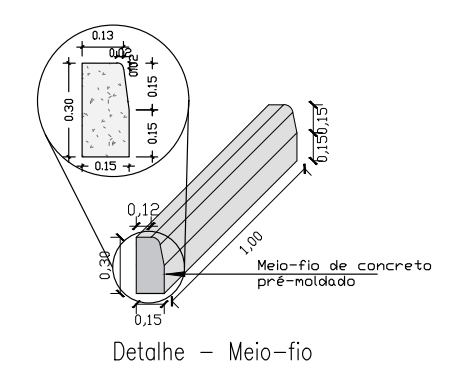
0.13
0.30
0.15
0.15
0.12
0.15
1.00
Meio-fio de concreto pré-moldado

Detalhe – Meio-fio

Nota: Para o cálculo do quantitativo de concreto do passeio público, considera-se a dimensão da largura conforme indicado nos detalhe dos passeios.

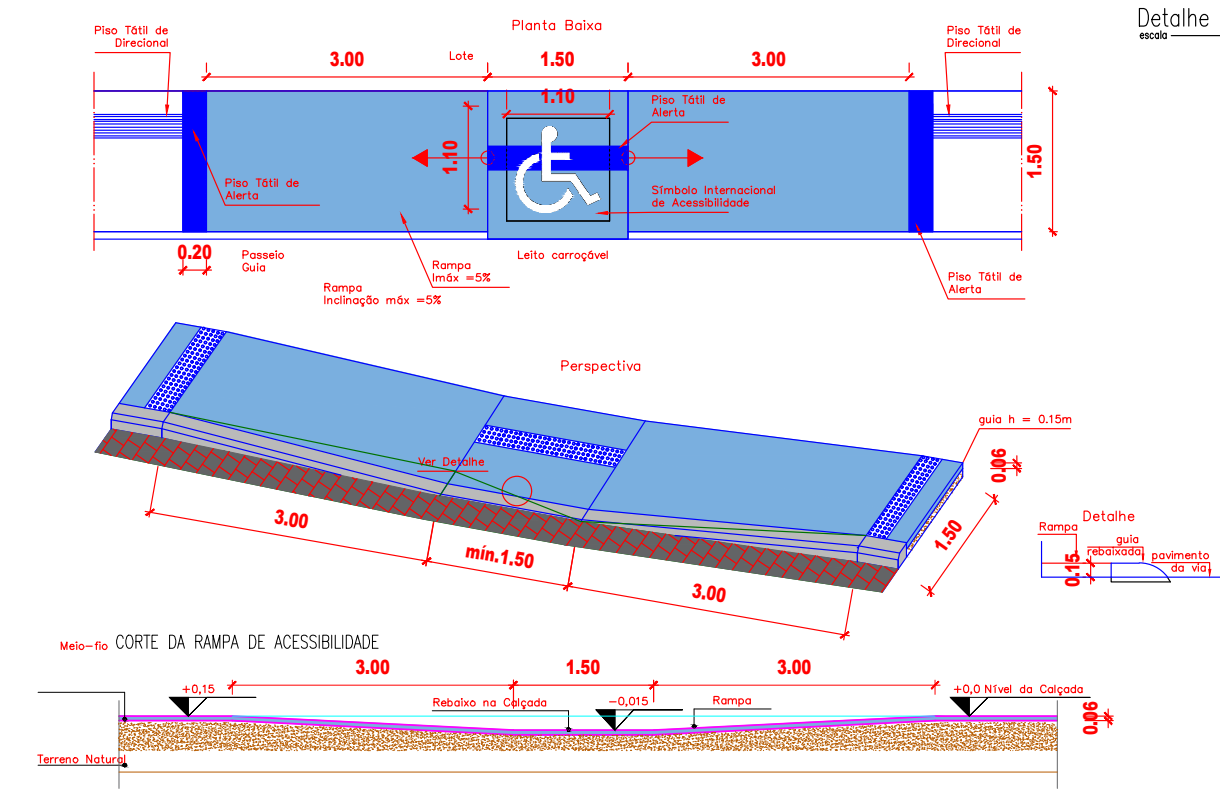
Planta Baixa
Piso Tátil de Direcional
3.00
Lote
1.50
3.00
1.10
1.10
Piso Tátil de Alerta
Símbolo Internacional de Acessibilidade
0.20
Passeio
Guia
Rampa
Inclinação máx =5%
Rampa
máx =5%
Leito carroçável
1.50
Perspectiva
guia h = 0.15m
0.06
Detalhe
Rampa
guia rebaixada
pavimento da via
3.00
min.1.50
3.00
Meio-fio
CORTE DA RAMPA DE ACESSIBILIDADE
3.00
1.50
3.00
+0.15
Rebaixo na Calçada
-0.015
Rampa
+0.0 Nível da Calçada
Terreno Natural

Detalhe – Rampa de Acessibilidade
1:50

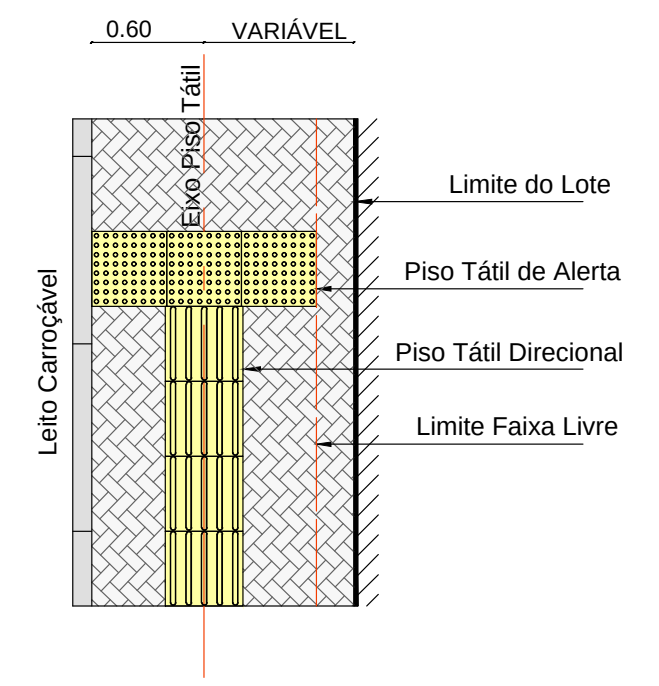
0.60
VARIÁVEL
Eixo Piso Tátil
Leito Carroçável
Limite do Lote
Piso Tátil de Alerta
Piso Tátil Direcional
Limite Faixa Livre

Detalhe 01 – Início/Fim Piso Tátil (D01–IFPT)

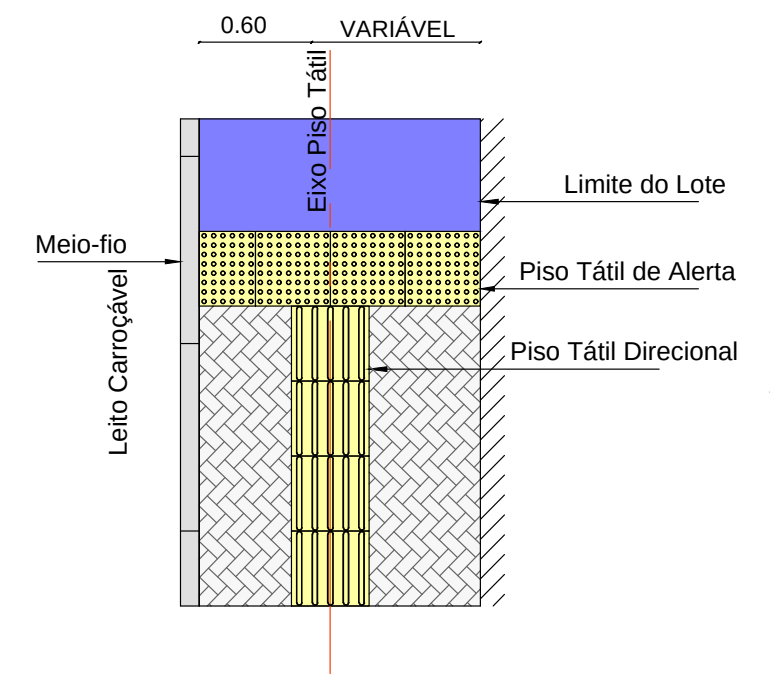
0.60
VARIÁVEL
Eixo Piso Tátil
Meio-fio
Leito Carroçável
Limite do Lote
Piso Tátil de Alerta
Piso Tátil Direcional

Detalhe 02 – Encontro Piso Tátil com Rampa (D02–EPTR)

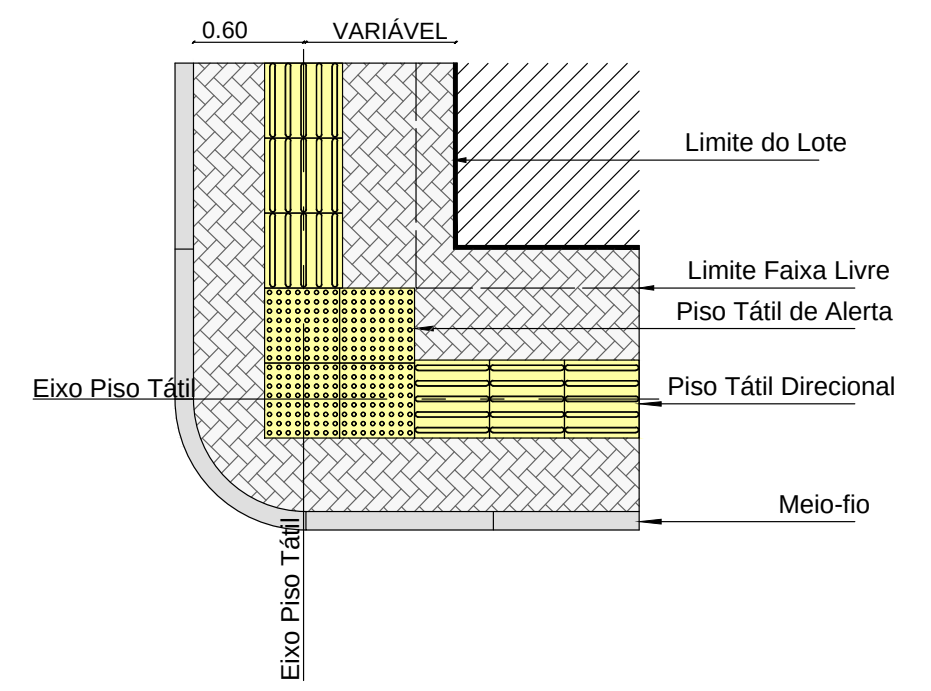
0.60
VARIÁVEL
Limite do Lote
Limite Faixa Livre
Piso Tátil de Alerta
Eixo Piso Tátil
Piso Tátil Direcional
Meio-fio
Eixo Piso Tátil

Detalhe 03 – Mudança de direção – Entre 90° e 150° (D03–MD)

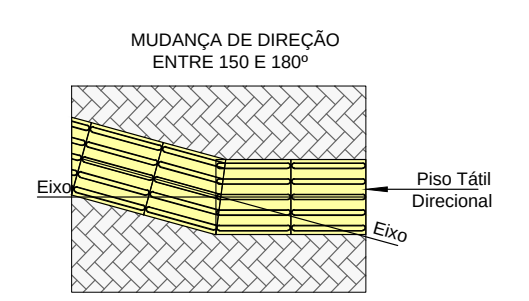
MUDANÇA DE DIREÇÃO
ENTRE 150 E 180º
Eixo
Piso Tátil Direcional
Eixo

Detalhe 04 – Mudança de direção entre 150° e 180° (D04–MD)

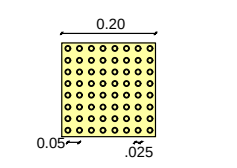

Detalhe 05 – Piso Tátil de Alerta

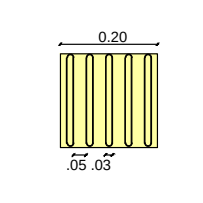

Detalhe 06 – Piso Tátil Direcional

PROPRIETÁRIO Prefeitura Municipal de Coremas- PB

Kleber Sá de Oliveira
Engenheiro Civil
CREA 1602582780

PROJETISTA Kleber Sá de Oliveira

EPE
EMPRESA PARAIBA DE ENGENHARIA

PROJETO:
PAVIMENTAÇÃO DE RUAS E VIAS
LOCAL:
MUNICÍPIO DE COREMAS - PB
PROPRIETÁRIO:
PREFEITURA MUNICIPAL DE COREMAS - PB

FOLHA 05/07
ESCALA: Indicadas
DESENHOS: Indicados
RESPONSÁVEL TÉCNICO:
Kleber Sá de Oliveira
Crea: 160391676-8
ANOTAÇÕES:
ARQUIVO:
PAV_COREMAS_FINAL_2022.dwg
DESENHO: Diego Medeiros
DATA: SET - 2022

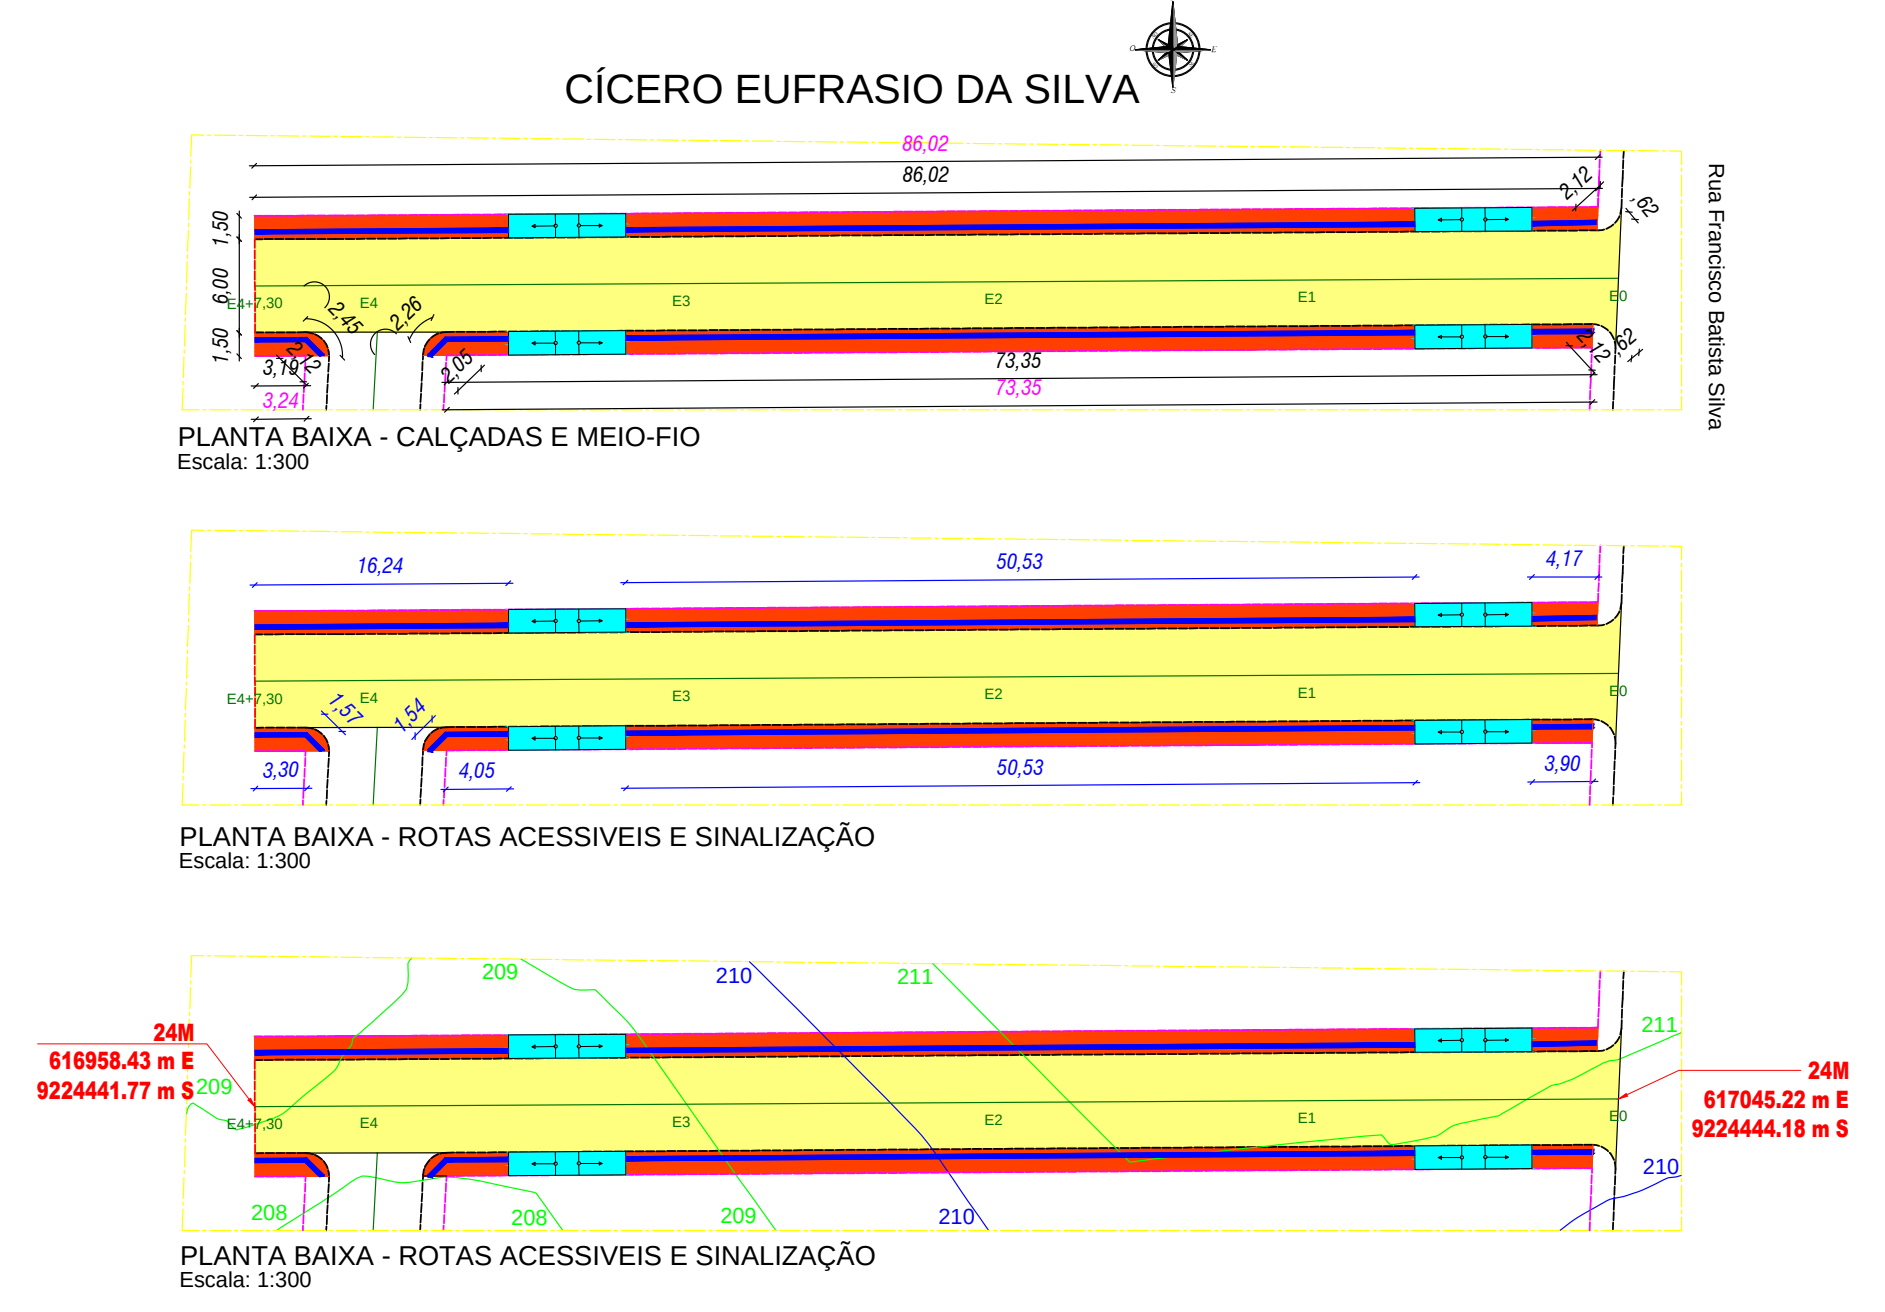
CÍCERO EUFRASIO DA SILVA
Rua Francisco Batista Silva
86,02
86,02
2,12
1,50
6,00
1,50
3,19
3,24
2,26
2,05
73,35
73,35
E4+7,30
E4
E3
E2
E1
E0
PLANTA BAIXA - CALÇADAS E MEIO-FIO
Escala: 1:300
16,24
50,53
4,17
1,57
1,54
3,30
4,05
50,53
3,90
PLANTA BAIXA - ROTAS ACESSIVEIS E SINALIZAÇÃO
Escala: 1:300
24M
616958.43 m E
9224441.77 m S
208
209
210
211
24M
617045.22 m E
9224444.18 m S
PLANTA BAIXA - ROTAS ACESSIVEIS E SINALIZAÇÃO
Escala: 1:300

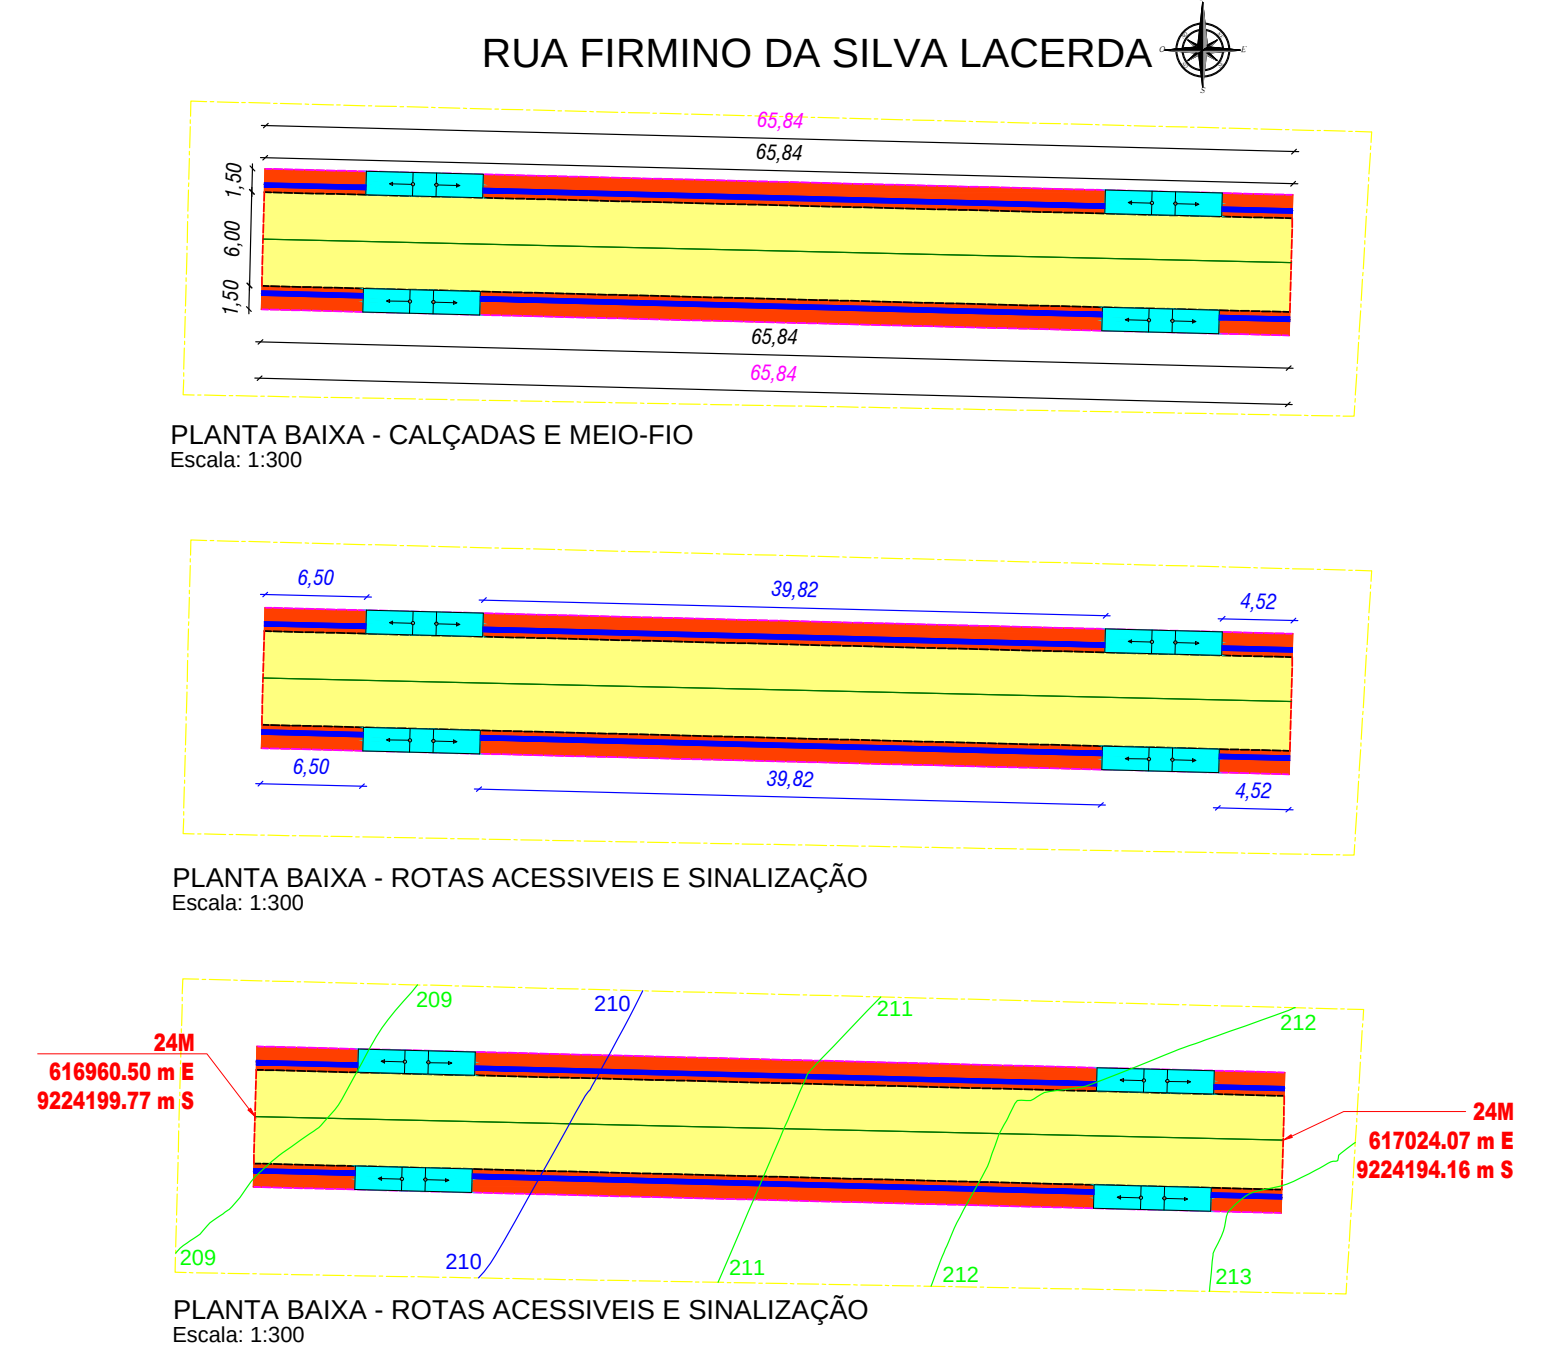
RUA FIRMINO DA SILVA LACERDA
65,84
65,84
1,50
6,00
1,50
65,84
65,84
PLANTA BAIXA - CALÇADAS E MEIO-FIO
Escala: 1:300
6,50
39,82
4,52
6,50
39,82
4,52
PLANTA BAIXA - ROTAS ACESSIVEIS E SINALIZAÇÃO
Escala: 1:300
24M
616960.50 m E
9224199.77 m S
209
210
211
212
213
24M
617024.07 m E
9224194.16 m S
PLANTA BAIXA - ROTAS ACESSIVEIS E SINALIZAÇÃO
Escala: 1:300

Legenda

Pavimentação

- 🟨 Pavimentação à Construir
- ▨ Pavimento Existente
- — Meio-fio Existente
- - - Meio-fio Projetado
- - - Cordão em Granito
- - - Alvenaria de 1 vez
- — Cerca
- ➡ Sentido do Caimento da água

Passeio

- 🟥 Calçadas à Construir
- 🟩 Calçadas Existentes
- 🟦 Piso Tátil
- ▭ Rampa de Acesso
- ● Poste Existente
- ● Poço de Visita (PV)
- ● Árvore
- — Edificação Existente
- — Lote Projetado

Sinalização

- PARE Placa de Parada Obrigatória
- RUA XXXX XXXX Placa com Nome da rua

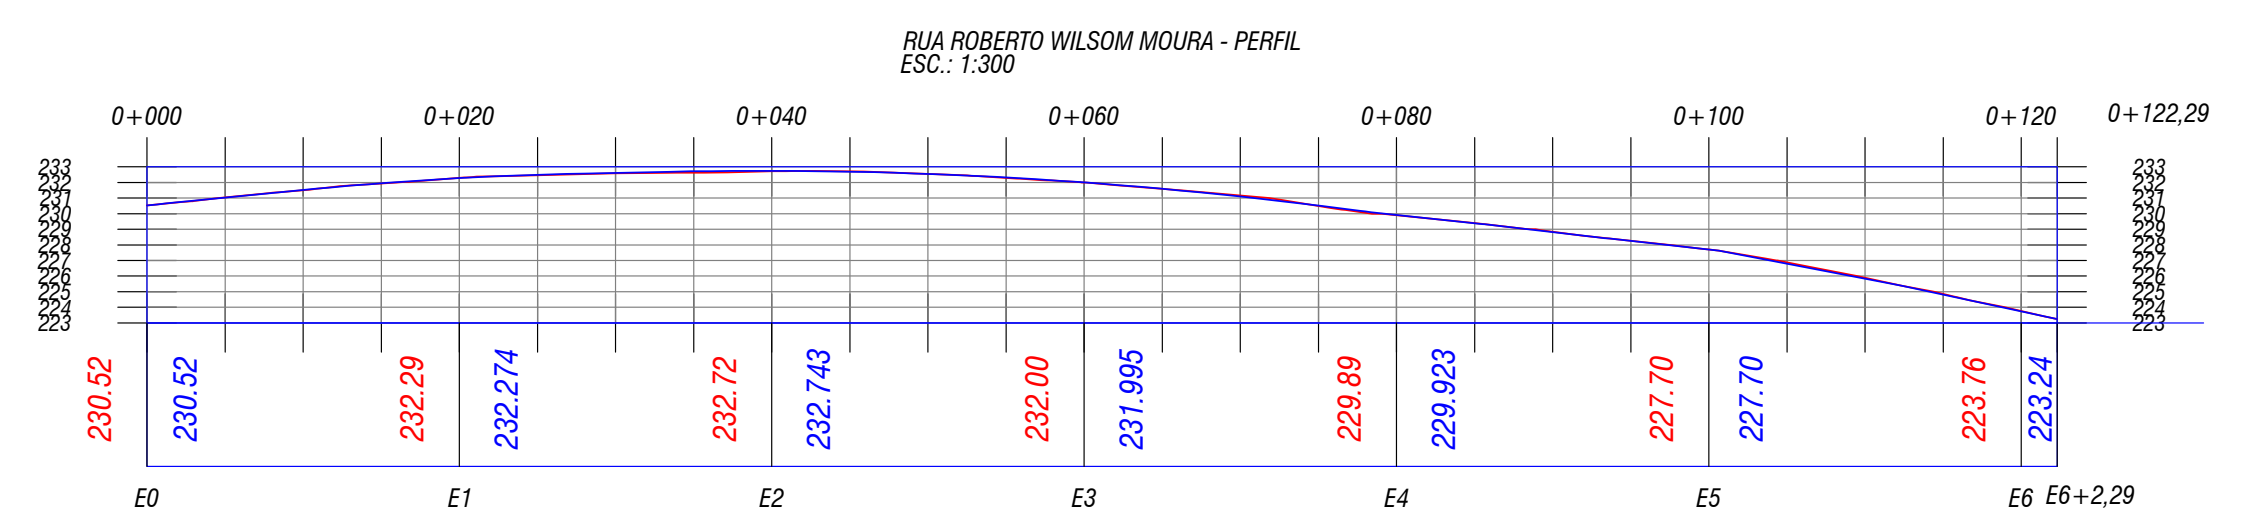

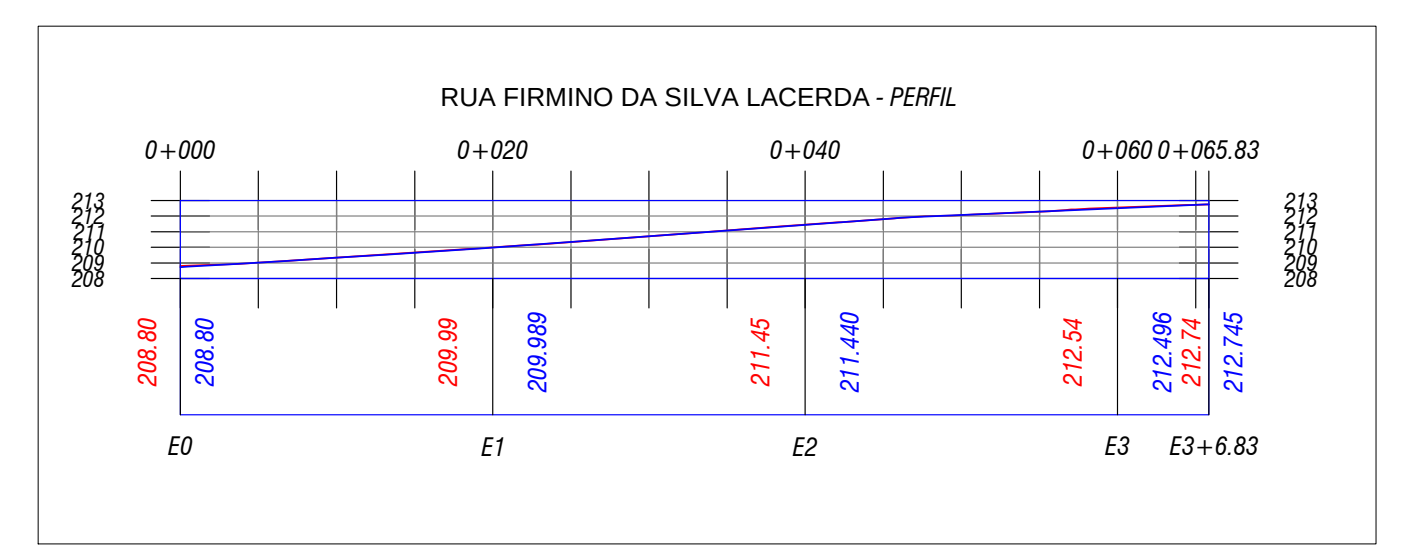

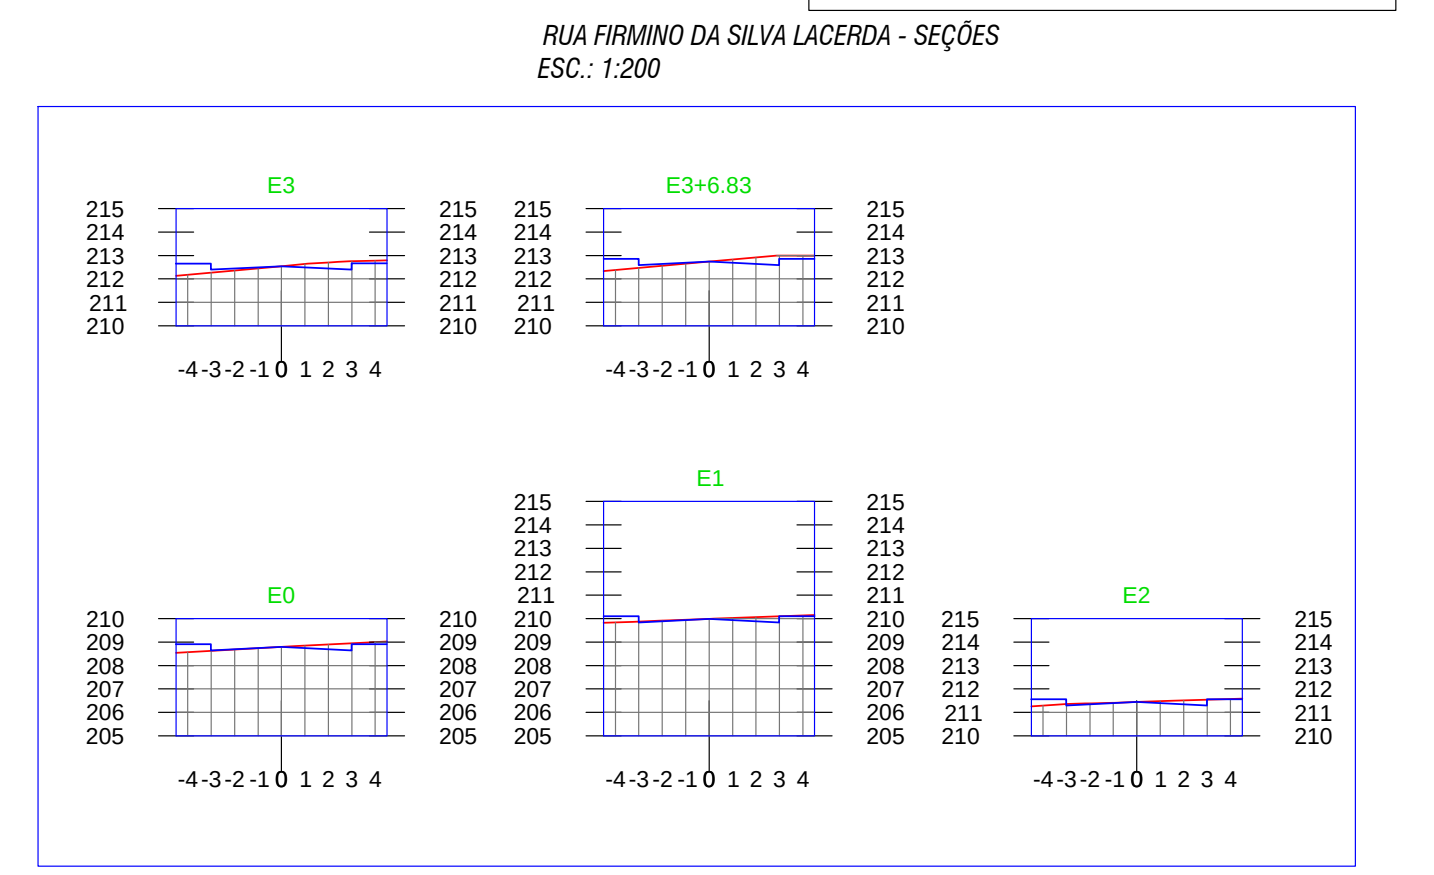
RUA FIRMINO DA SILVA LACERDA - SEÇÕES
ESC.: 1:200
E3
E3+6.83
E0
E1
E2
-4 -3 -2 -1 0 1 2 3 4

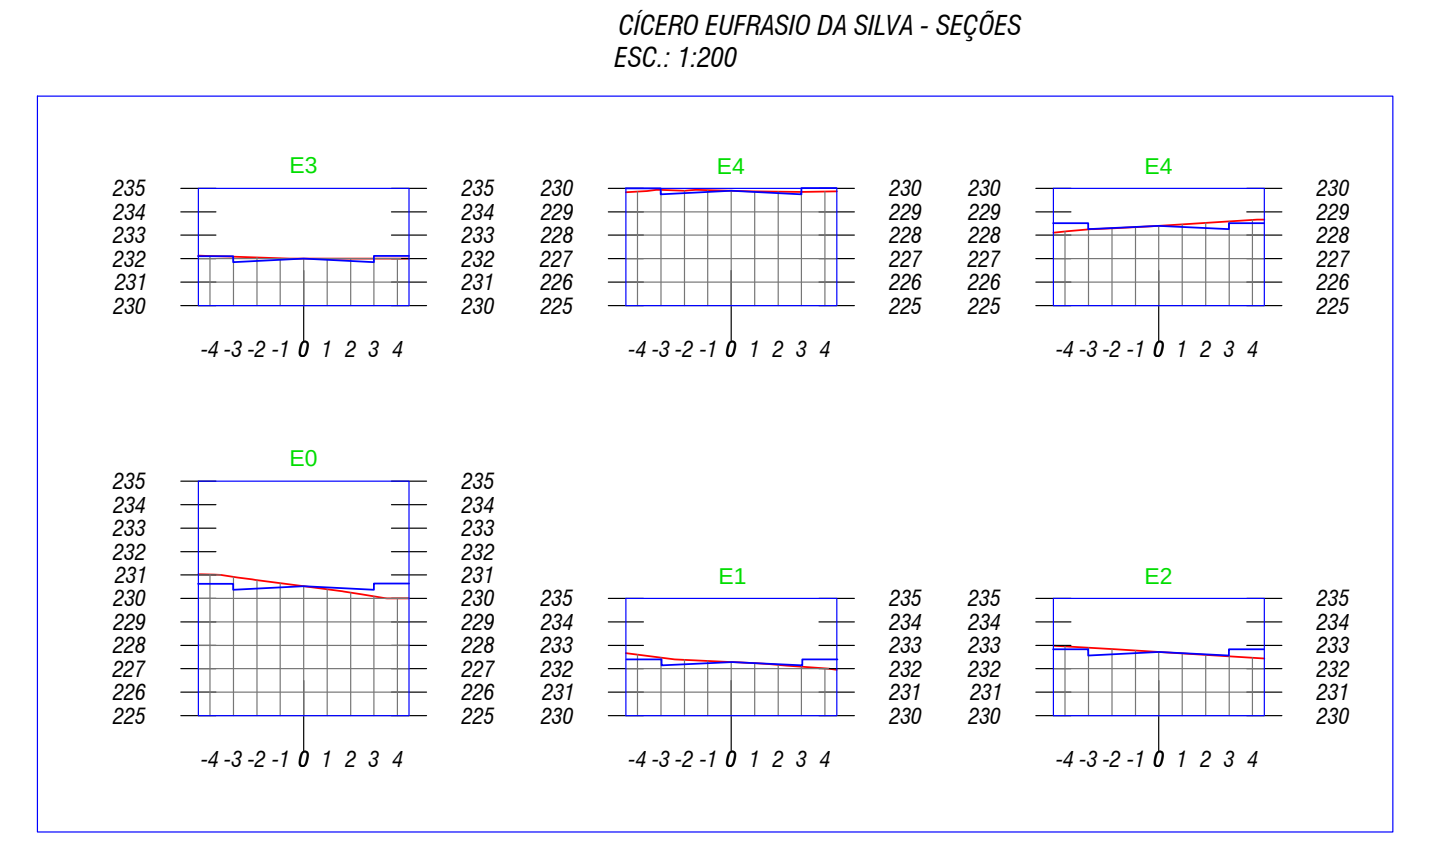
CÍCERO EUFRASIO DA SILVA - SEÇÕES
ESC.: 1:200
E3
E4
E4
E0
E1
E2
-4 -3 -2 -1 0 1 2 3 4

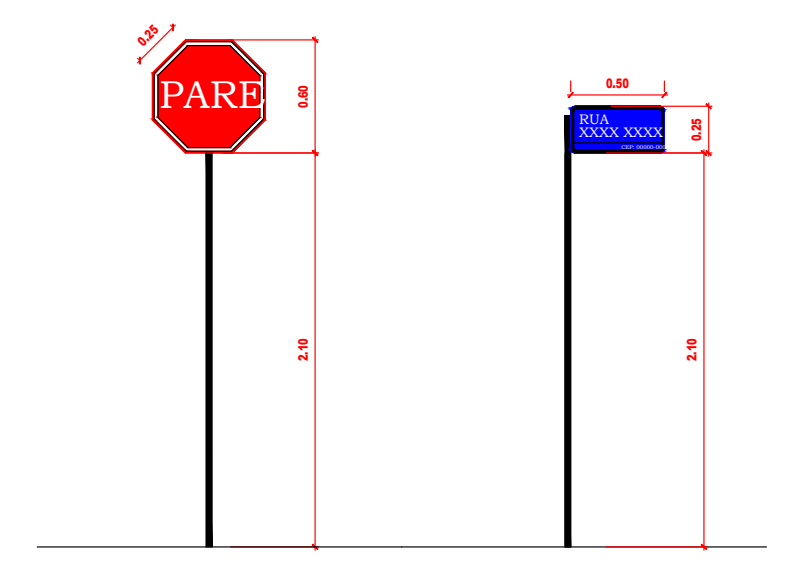
PARE
0.25
0.60
2.10
RUA
XXXX XXXX
0.50
0.25
Placa de Parada Obrigatória
Placa de Nome da Rua

Detalhe – Sinalização Vertical
1:25

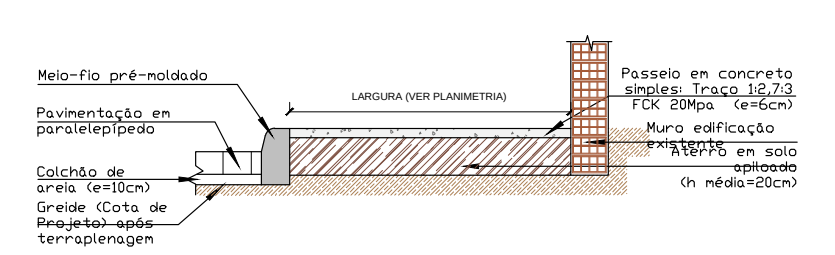
Meio-fio pré-moldado
Pavimentação em paralelepípedo
Colchão de areia (e=10cm)
Greide (Cota de Projeto) após terraplenagem
LARGURA (VER PLANIMETRIA)
Passeio em concreto simples: Traço 1:2,7:3 FCK 20Mpa (e=6cm)
Muro edificação existente
Aterro em solo apiloado (h média=20cm)

Detalhe 01 – Passeio Para Trechos s/ Alvenaria de 1 Vez

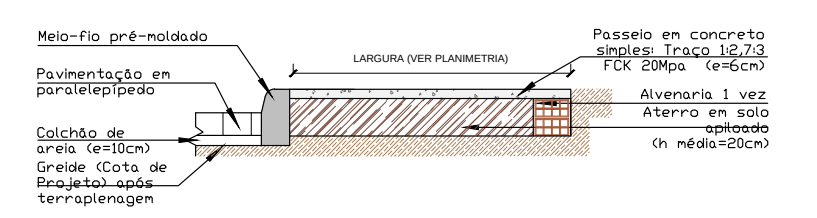
Meio-fio pré-moldado
Pavimentação em paralelepípedo
Colchão de areia (e=10cm)
Greide (Cota de Projeto) após terraplenagem
LARGURA (VER PLANIMETRIA)
Passeio em concreto simples: Traço 1:2,7:3 FCK 20Mpa (e=6cm)
Alvenaria 1 vez
Aterro em solo apiloado (h média=20cm)

Detalhe 02 – Passeio Para Trechos c/ Alvenaria de 1 Vez

Seção-Tipo de Pavimentação

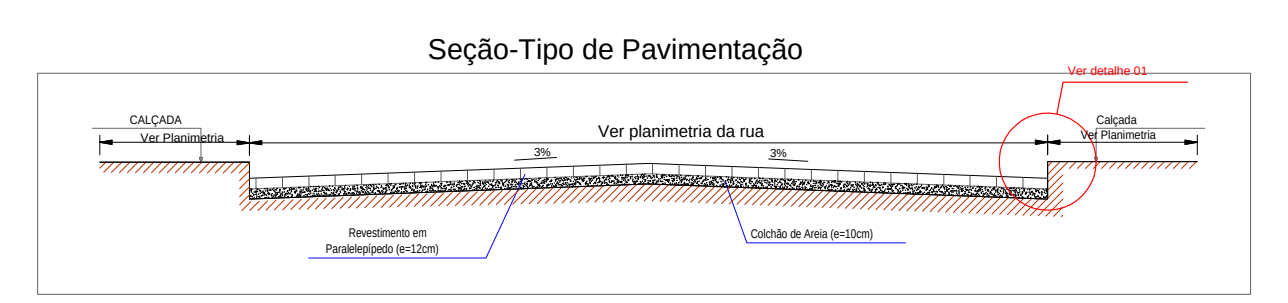
CALÇADA
Ver Planimetria
Ver planimetria da rua
3%
3%
Ver detalhe 01
Calçada
Ver Planimetria
Revestimento em Paralelepípedo (e=12cm)
Colchão de Areia (e=10cm)

Sem Escala

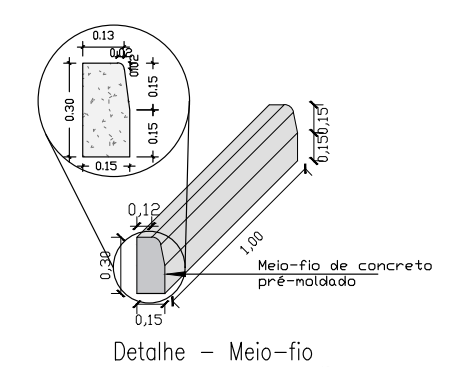
0.13
0.30
0.15
0.15
0.12
0.15
1.00
Meio-fio de concreto pré-moldado

Detalhe – Meio-fio

Nota: Para o cálculo do quantitativo de concreto do passeio público, considera-se a dimensão da largura conforme indicado nos detalhe dos passeios.

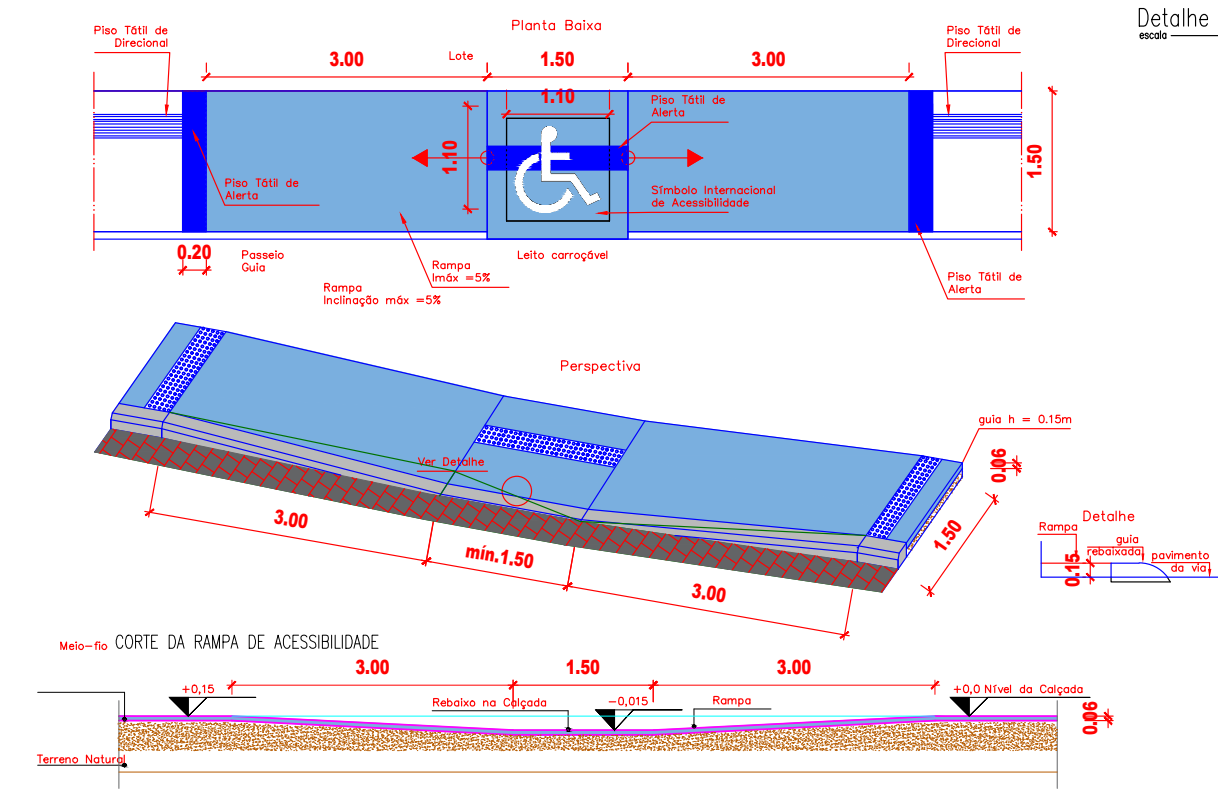
Planta Baixa
Piso Tátil de Direcional
3.00
Lote
1.50
3.00
1.10
1.10
Piso Tátil de Alerta
Símbolo Internacional de Acessibilidade
0.20
Passeio
Guia
Rampa
Inclinação máx =5%
Rampa
máx =5%
Leito carroçável
1.50
Perspectiva
guia h = 0.15m
0.06
Detalhe
Rampa
guia rebaixada
pavimento da via
3.00
min.1.50
3.00
Meio-fio
CORTE DA RAMPA DE ACESSIBILIDADE
3.00
1.50
3.00
+0.15
Rebaixo na Calçada
-0.015
Rampa
+0.0 Nível da Calçada
Terreno Natural

Detalhe – Rampa de Acessibilidade
1:50

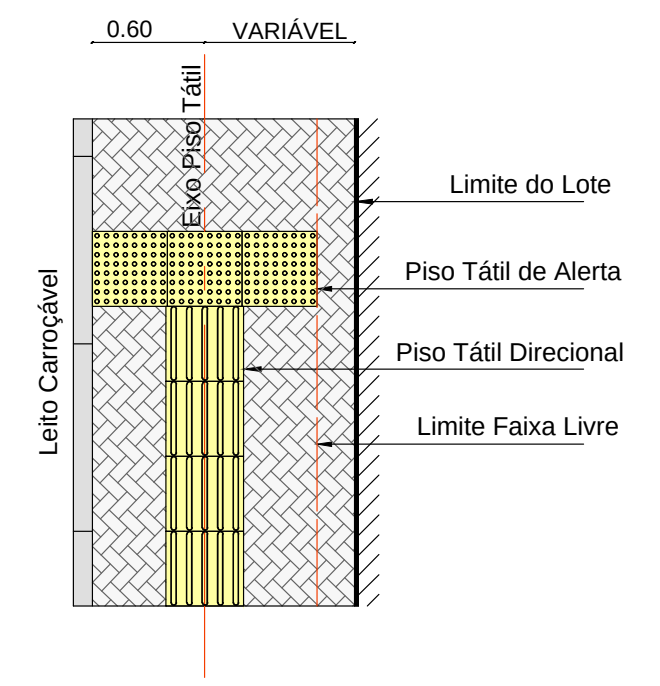
0.60
VARIÁVEL
Eixo Piso Tátil
Leito Carroçável
Limite do Lote
Piso Tátil de Alerta
Piso Tátil Direcional
Limite Faixa Livre

Detalhe 01 – Início/Fim Piso Tátil (D01–IFPT)

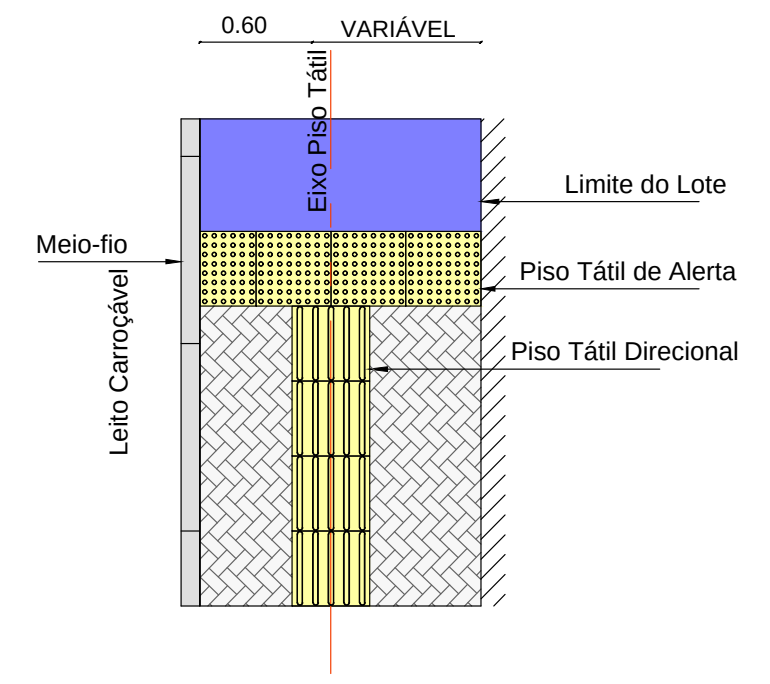
0.60
VARIÁVEL
Eixo Piso Tátil
Meio-fio
Leito Carroçável
Limite do Lote
Piso Tátil de Alerta
Piso Tátil Direcional

Detalhe 02 – Encontro Piso Tátil com Rampa (D02–EPTR)

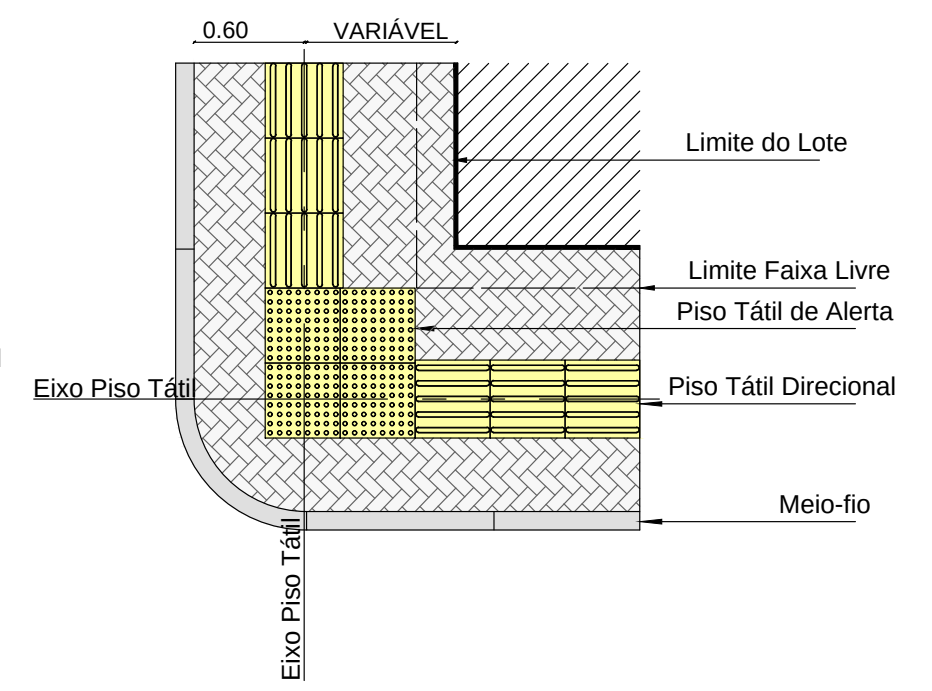
0.60
VARIÁVEL
Limite do Lote
Limite Faixa Livre
Piso Tátil de Alerta
Eixo Piso Tátil
Piso Tátil Direcional
Meio-fio
Eixo Piso Tátil

Detalhe 03 – Mudança de direção – Entre 90° e 150° (D03–MD)

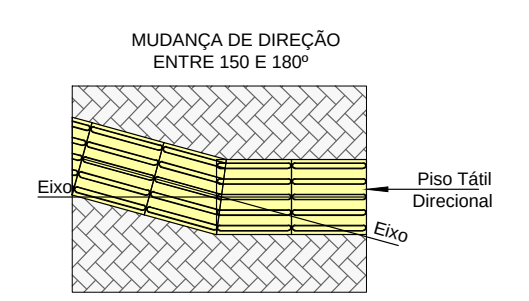
MUDANÇA DE DIREÇÃO
ENTRE 150 E 180º
Eixo
Piso Tátil Direcional
Eixo

Detalhe 04 – Mudança de direção entre 150° e 180° (D04–MD)

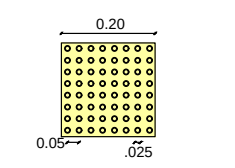

Detalhe 05 – Piso Tátil de Alerta

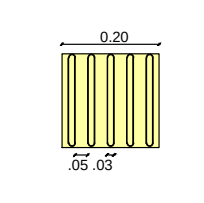

Detalhe 06 – Piso Tátil Direcional

PROPRIETÁRIO Prefeitura Municipal de Coremas- PB

Kleber Sá de Oliveira
Engenheiro Civil
CREA 1602582780

PROJETISTA Kleber Sá de Oliveira

EPE
EMPRESA PARAIBA DE ENGENHARIA

PROJETO:
PAVIMENTAÇÃO DE RUAS E VIAS
LOCAL:
MUNICÍPIO DE COREMAS - PB
PROPRIETÁRIO:
PREFEITURA MUNICIPAL DE COREMAS - PB

FOLHA 06/07
ESCALA: Indicadas
DESENHOS: Indicados
RESPONSÁVEL TÉCNICO:
Kleber Sá de Oliveira
Crea: 160391676-8
ANOTAÇÕES:
ARQUIVO:
PAV_COREMAS_FINAL_2022.dwg
DESENHO: Diego Medeiros
DATA: SET - 2022