
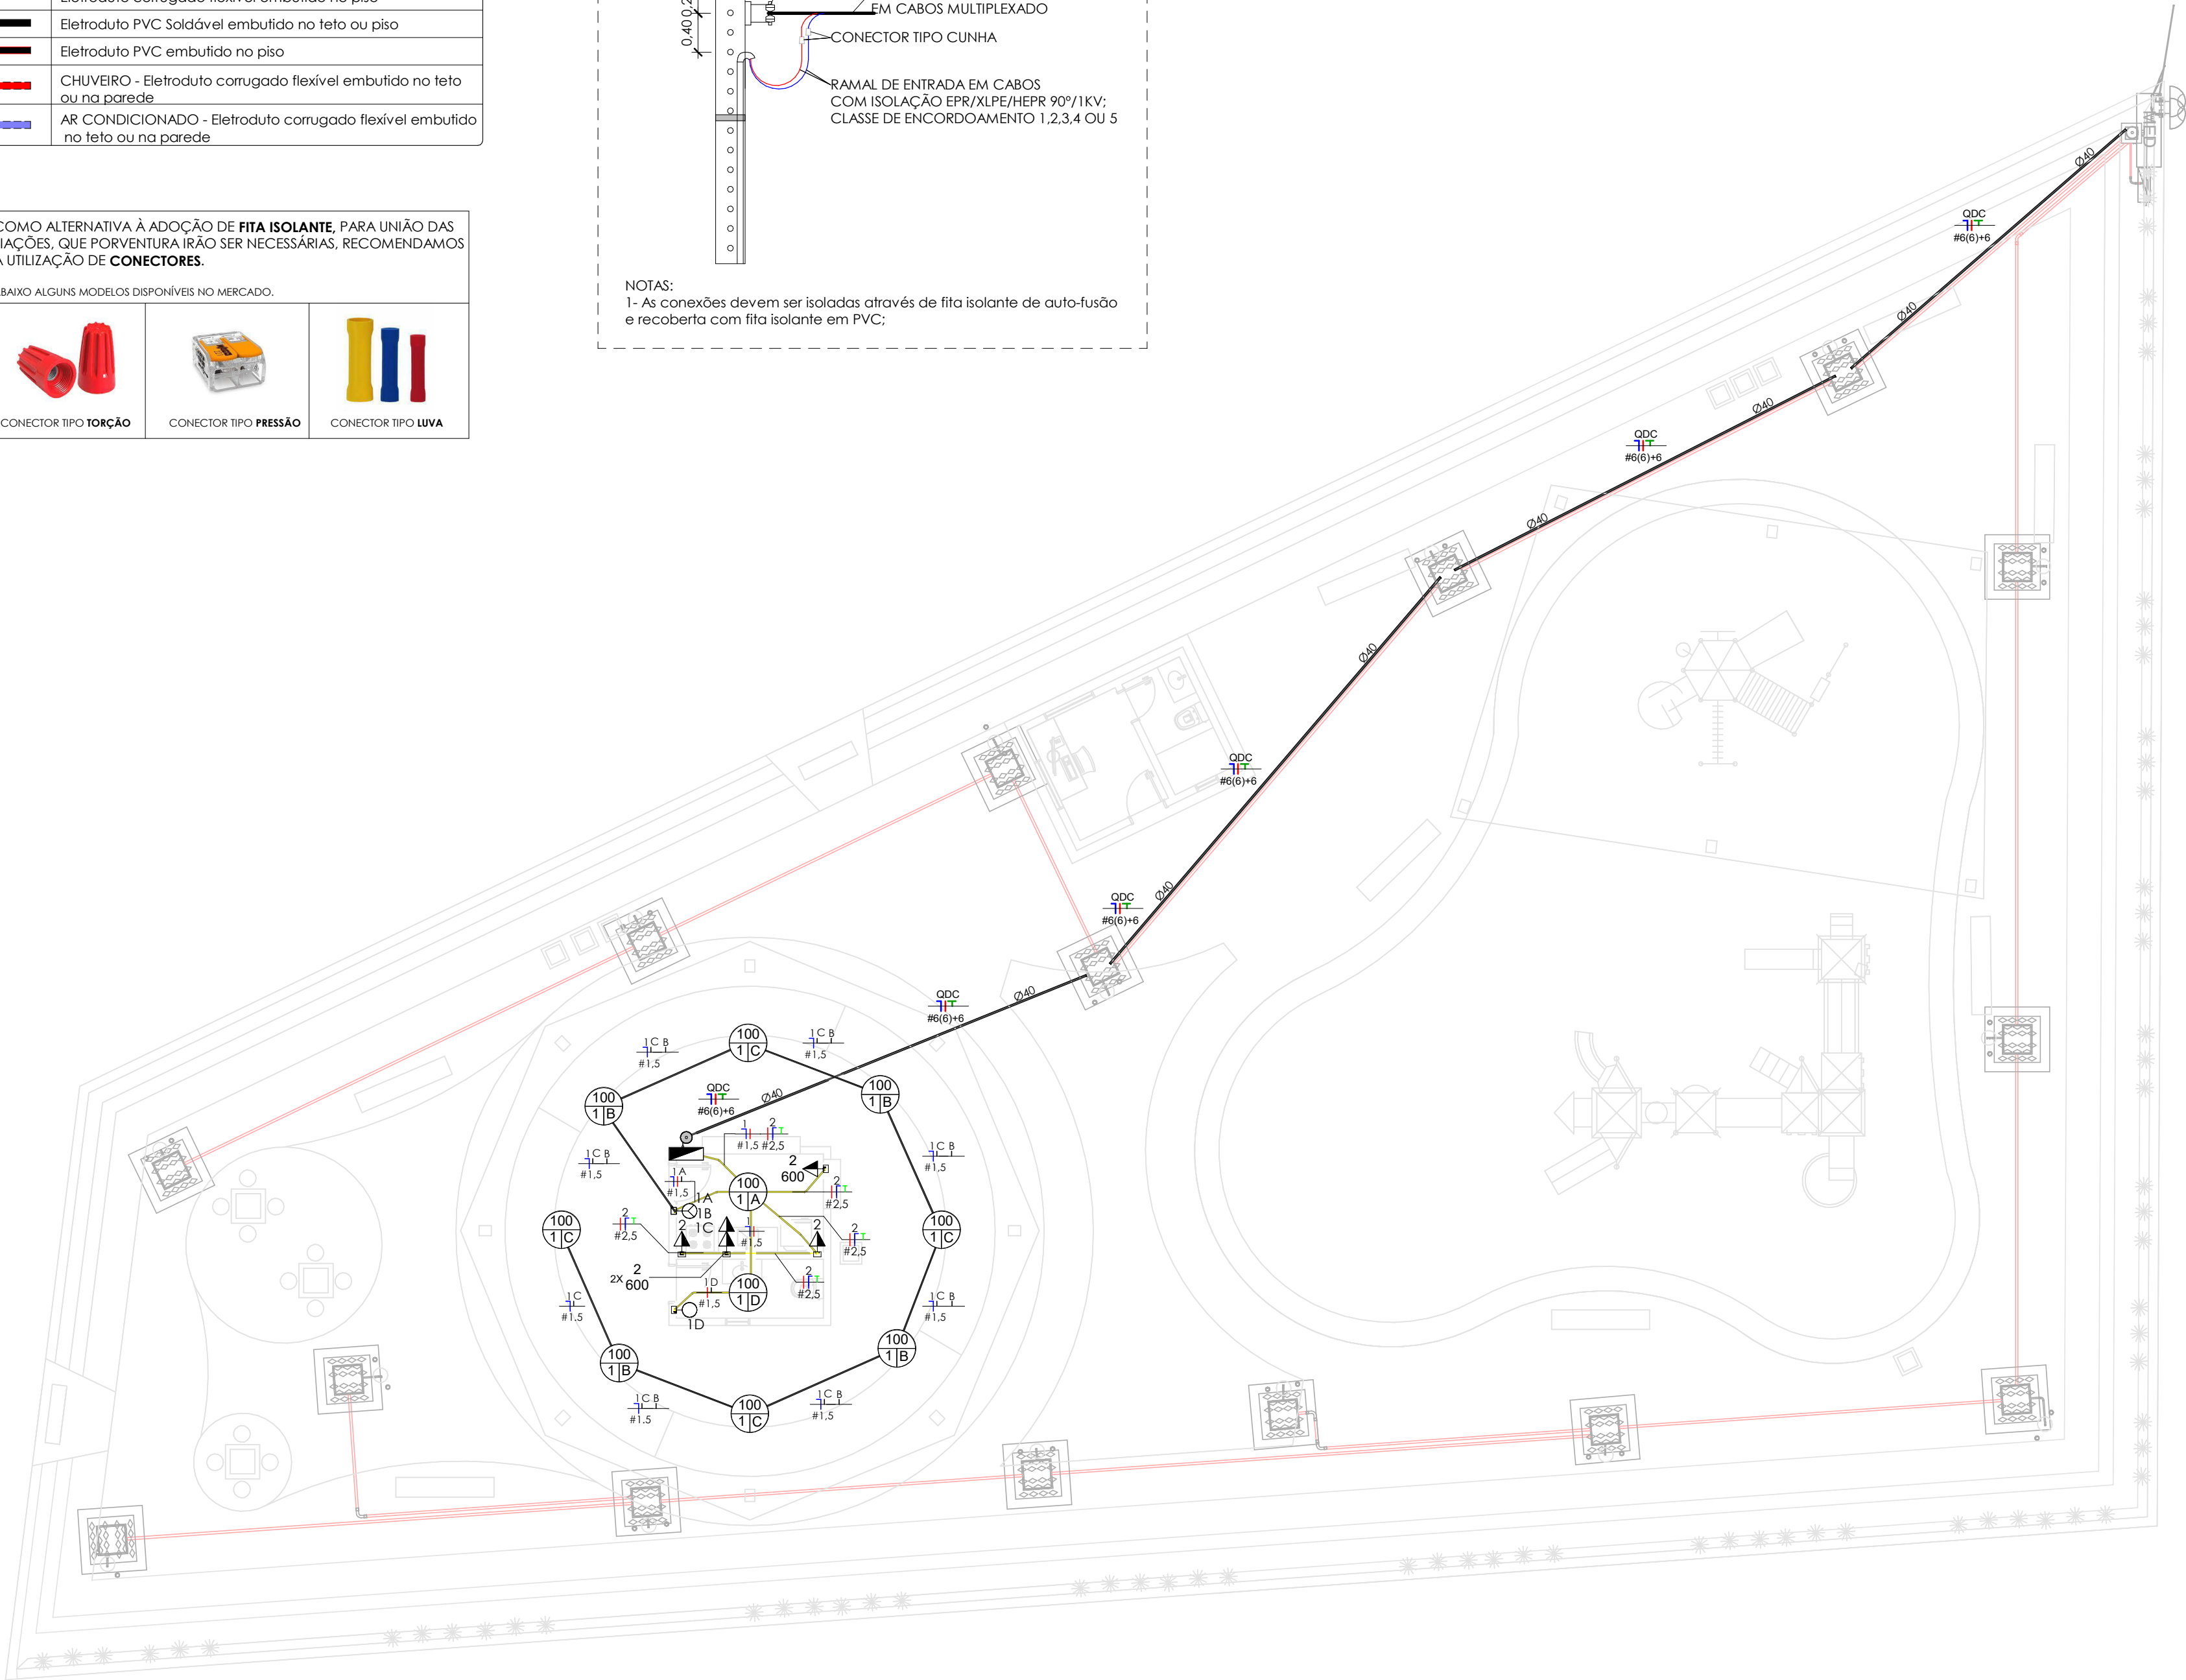


| SIMBOLOGIA - ELETRODUTOS |                                                                               |
|--------------------------|-------------------------------------------------------------------------------|
|                          | Eletroduto corrugado flexível embutido no teto ou na parede                   |
|                          | Eletroduto corrugado flexível embutido no piso                                |
|                          | Eletroduto PVC Soldável embutido no teto ou piso                              |
|                          | Eletroduto PVC embutido no piso                                               |
|                          | CHUVEIRO - Eletroduto corrugado flexível embutido no teto ou na parede        |
|                          | AR CONDICIONADO - Eletroduto corrugado flexível embutido no teto ou na parede |

COMO ALTERNATIVA À ADOÇÃO DE FITA ISOLANTE, PARA UNIÃO DAS FIAÇÕES, QUE PORVENTURA IRÃO SER NECESSÁRIAS, RECOMENDAMOS A UTILIZAÇÃO DE CONECTORES.

ABAIXO ALGUNS MODELOS DISPONÍVEIS NO MERCADO.

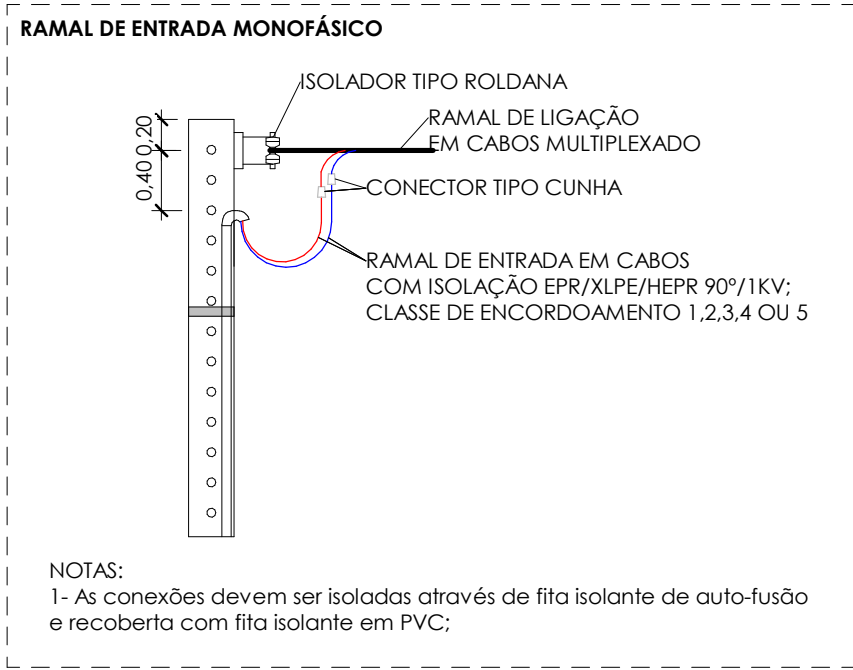

- APROVEITAMENTO DAS CAIXAS DE PASSAGENS QUANTIFICADOS NO PROJETO DE ILUMINAÇÃO GERAL DA PRAÇA

### QUANTITATIVO DE CABOS EM METROS (Cobre/EPR-XLPE/0,6-1kV/90°C)

(F- Condutor Fase), (N - Condutor Neutro), (T - Condutor Terra), (Re - Condutor de Retorno)

Sugestão de Cores para os condutores- F: Vermelho, N: Azul Claro, PE: Verde, Re - Branco

| F-6,0mm² | N-6,0mm² | T-6,0mm² | Tipo de Condutor |
|----------|----------|----------|------------------|
| 42,6     | 42,6     | 42,6     | HEPR             |

### QUANTITATIVO DE CABOS EM METROS (Cobre/Un/Iso. PVC/750V/70°C)

(F- Condutor Fase), (N - Condutor Neutro), (T - Condutor Terra), (Re - Condutor de ...)

Sugestão de Cores para os condutores- F: Vermelho, N: Azul Claro, PE: Verde, Re - ...

| F-1,5mm² | F-2,5mm² | N-1,5mm² | N-2,5mm² | T-2,5mm² | Re-1,5mm² | Tipo de Condutor |
|----------|----------|----------|----------|----------|-----------|------------------|
| 12,6     | 13,6     | 37,7     | 13,6     | 13,6     | 61,3      | PVC              |

### GERAL - LISTA DE MATERIAIS - COMPONENTES



| Descrição do Material   | Dimensões                                                      | Quantidade (peças) |
|---|----------------------------------------------------------------|--------------------|
|   |                                                                | 7                  |
| Derivações para Eletrodutos de PVC Rígido<br>Curva 90° para eletroduto rígido de PVC DN25mm rosca Ø3/4" BSP conforme ABNT NBR 15465   | DN25mm (3/4")                                                  | 2                  |
| Luva para eletroduto de PVC rígido DN25mm rosca Ø3/4" BSP conforme ABNT NBR 15465   | Ø 3/4"                                                         | 4                  |
| Disjuntores e Proteções<br>DPS - Disjuntor de proteção contra surtos, monopolar, tensão nominal de operação UO 220/380V, máxima tensão de operação contínua UC= 275 V, corrente de descarga máxima= 30kA, fixação em trilho DIN 35mm<br>IDR Interruptor Diferencial Residual Bipolar In=40A, 30mA<br>Mini Disjuntor Monopolar 10A Curva C, conforme ABNT NBR NM 60898, encaixe perfil DIN 35mm<br>Mini Disjuntor Monopolar 16A Curva C, conforme ABNT NBR NM 60898, encaixe perfil DIN 35mm<br>Mini Disjuntor Monopolar 32A Curva C, conforme ABNT NBR NM 60898, encaixe perfil DIN 35mm | VCL 275V 30kA Slim<br>In=40 A, 30mA<br>C 10A<br>C 16A<br>C 32A | 2<br>1<br>1<br>1   |
| Interruptores<br>Conjunto montado com 1 Interruptor simples, 10A 250V~, 4"x2"<br>Conjunto montado de Interruptor com 3 teclas simples, 4"x2"   | 1S, 4"x2"<br>3xS, 4"x2"                                        | 1<br>1             |
| Quadros<br>Quadro de Distribuição 6/8 Disjuntores, de embutir, fabricado em PVC antichamas, com barramento de terra e neutro, porta branca, dimensões 245x190x78,7mm.   | 6/8 Disjuntores                                                | 1                  |
| Sistema de Aterramento<br>Conjunto: Caixa de Aterramento [20x20cm] + Conector Tipo Cunha + Haste de aterramento Ø 16mm (5/8")X2400   |                                                                | 1                  |
| Tomadas<br>Conjunto montado de 1 Tomada 2P+T, 10A, posto horizontal, 4"x2"<br>Conjunto montado de 2 Tomadas 2P+T, 10A, postos horizontais, 4"x2"   | 10A, 4"x2"<br>2x10A, 4"x2"                                     | 3<br>1             |

### GERAL - LISTA DE MATERIAIS - ELETRODUTOS

| Descrição do Material             | Diâmetro Nominal | Comprimento (m) |
|-----------------------------------|------------------|-----------------|
| Eletroduto de PVC Rígido Soldável | Ø40              | 38,76 m         |
| Eletroduto de PVC Rígido Soldável | Ø25              | 28,53 m         |
| Eletroduto flexível corrugado     | Ø25              | 21,31 m         |

### SIMBOLOGIA

|  |                                                                      |
|--|----------------------------------------------------------------------|
|  | Tomada Baixa 2P+T, 10A, a 30cm do piso acabado                       |
|  | Tomada Média 2P+T, 10A, a 120cm do piso acabado                      |
|  | Tomada Alta 2P+T, 10A, a 210cm do piso acabado                       |
|  | Tomada Baixa 2P+T, 20A, a 30cm do piso acabado                       |
|  | Tomada Média 2P+T, 20A, a 120cm do piso acabado                      |
|  | Tomada Alta 2P+T, 20A, a 210cm do piso acabado                       |
|  | Tomada de Piso 2P+T, 10A                                             |
|  | Tomada de Piso 2P+T, 20A                                             |
|  | Ponto de Ar Condicionado em caixa Polar                              |
|  | Ponto de Força com placa saída de fio, a 230cm do piso acabado       |
|  | Ponto de Força com placa saída de fio, a "X" cm do piso acabado      |
|  | Interruptor simples de uma seção                                     |
|  | Conjunto de 2 Interruptores simples                                  |
|  | Conjunto de 3 Interruptores simples                                  |
|  | Interruptor paralelo (three-way)                                     |
|  | Ponto para acionamento da campainha                                  |
|  | Ponto para campainha                                                 |
|  | Ponto de Telefone, RJ11, a 30cm do piso acabado                      |
|  | Condutores Neutro, Fase, Terra e Retorno, respectivamente            |
|  | Ponto de luz tipo balizador de piso, circuito e comando              |
|  | Ponto de luz embutido no teto, circuito e comando, respectivamente   |
|  | Luminária tubular de sobrepor - 2x LED                               |
|  | Ponto de luz na parede a 210cm do piso acabado                       |
|  | Sensor de presença no teto                                           |
|  | Eletroduto corrugado flexível embutido no teto ou na parede          |
|  | Eletroduto corrugado flexível embutido no piso                       |
|  | Eletroduto PVC embutido no teto ou na parede                         |
|  | Eletroduto PVC embutido no piso                                      |
|  | Eletroduto Aço Galvanizado                                           |
|  | LUMINÁRIA DE FITA LED                                                |
|  | Eletrocalha perfurada ou perfilado                                   |
|  | Quadro geral de luz e força embutido a 1,50 do piso acabado          |
|  | Eletroduto corrugado PVC flexível reforçado laranja embutido no piso |
|  | Bloco Autônomo                                                       |
|  | Caixa de passagem Elétrica no piso                                   |
|  | Eletroduto que sobe                                                  |
|  | Eletroduto que desce                                                 |
|  | Eletroduto que passa descendo                                        |
|  | Eletroduto que passa subindo                                         |
|  | DE DETALHE ESTRUTURAL                                                |

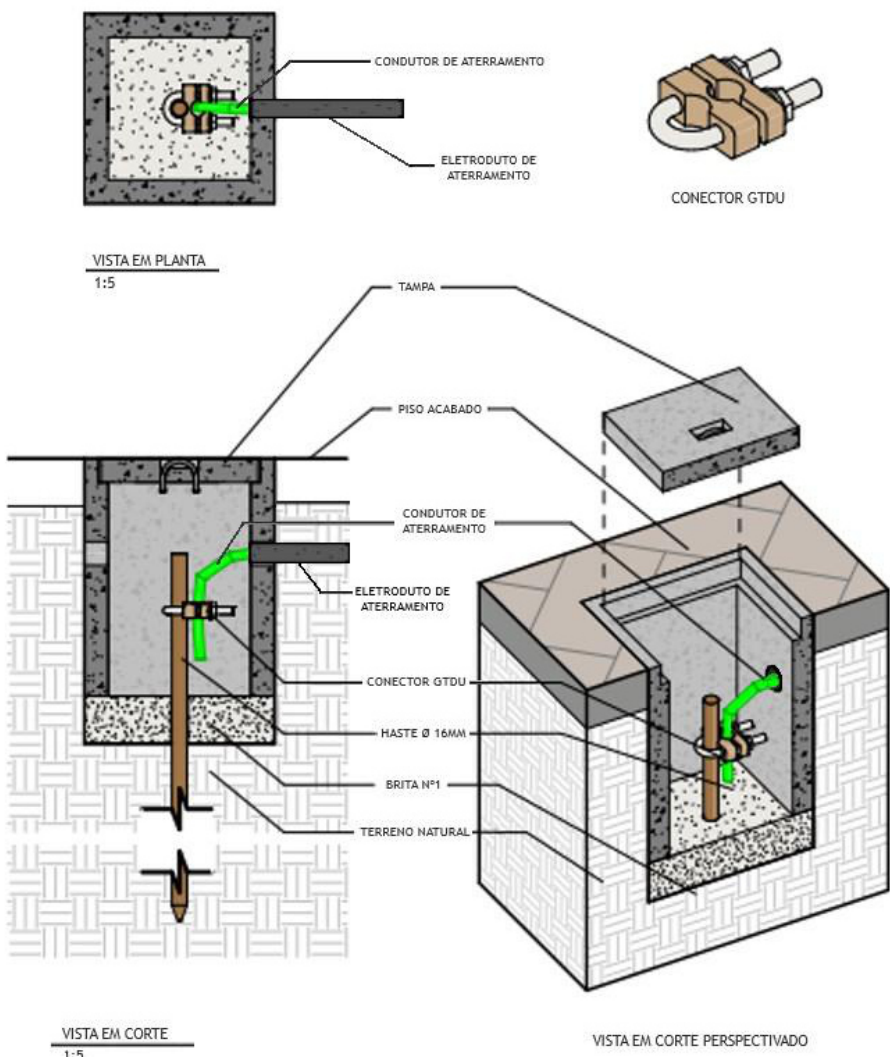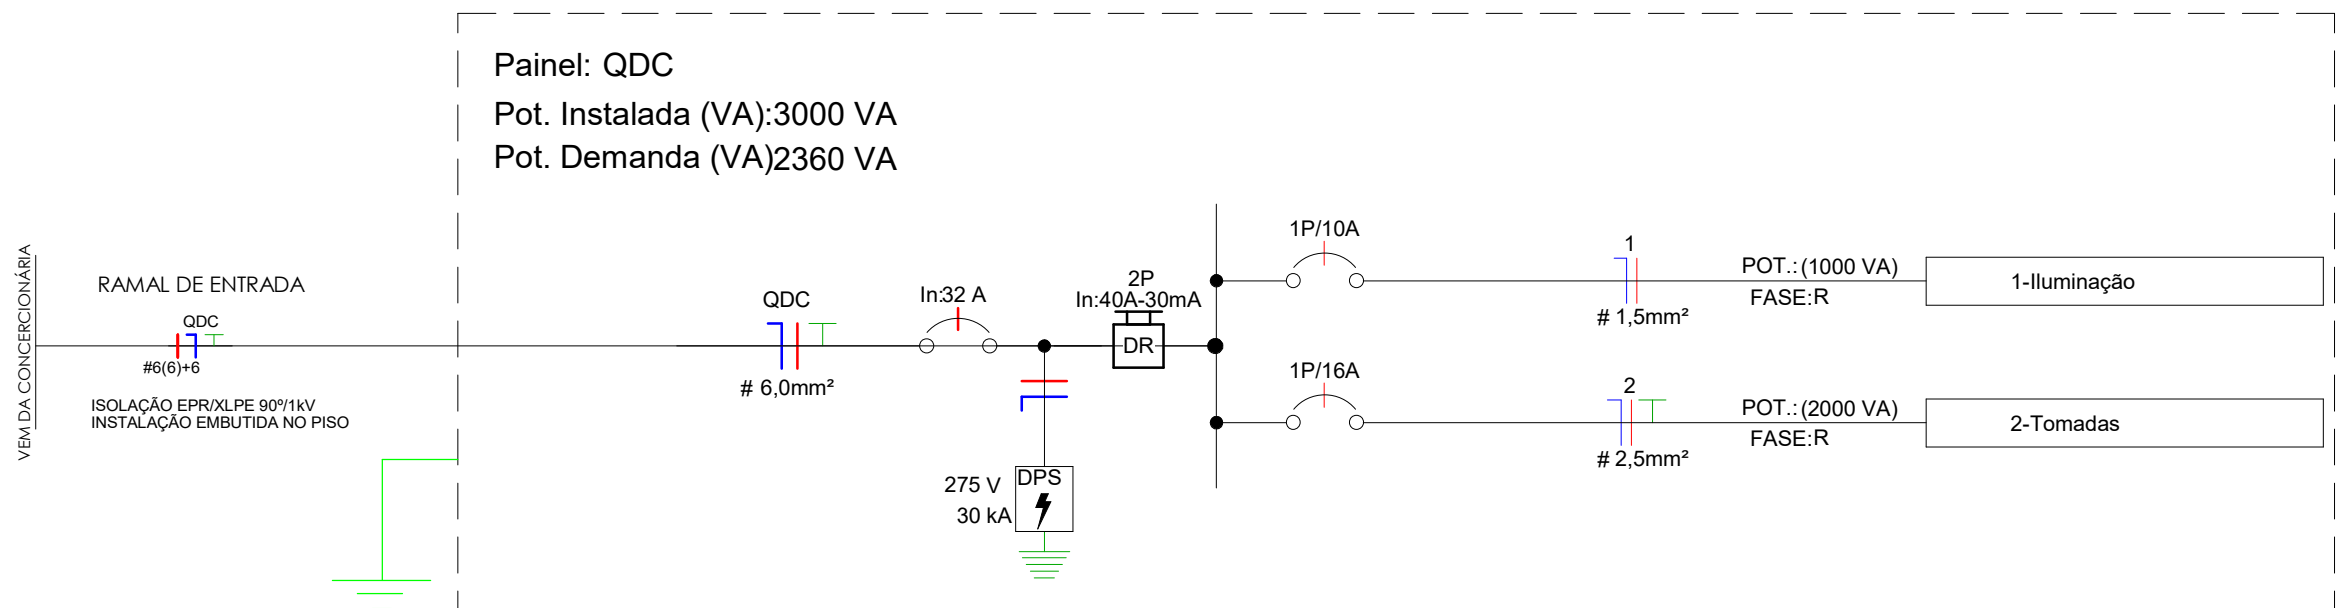

PROPRIETÁRIO: PREFEITURA MUNICIPAL DE COREMAS-PB

PROJETO: LINCOLN CARTAXO DE LIRA JÚNIOR CREA 160.814.689-8

PROJETO: PROJETO ELÉTRICO - QUISSQUE

CONCEDENTE: PREFEITURA MUNICIPAL DE COREMAS - PB

CONVENIENTE: MUNICÍPIO DE COREMAS - PB

LOCAL: COREMAS-PB

| DATA       | RESPONSÁVEL TÉCNICO | RUBRICA | DADOS              |
|------------|---------------------|---------|--------------------|
| ABRIL/2025 | LINCOLN CARTAXO     |         | CREA 160.814.689-8 |
| CÓPIA      |                     |         |                    |
| VISTO      |                     |         |                    |

PRANCHAS: DESCRIÇÃO:

01 /01

PROJETO ELÉTRICO

ESCALA:

INDICADA



Av. Gov. Flavio R. Coutinho, 500, sl. 601  
Jd. Oceania, 58037-005 - João Pessoa (PB)  
Tel +55 99924.4447  
e-mail: contato@lclprojetos.com