



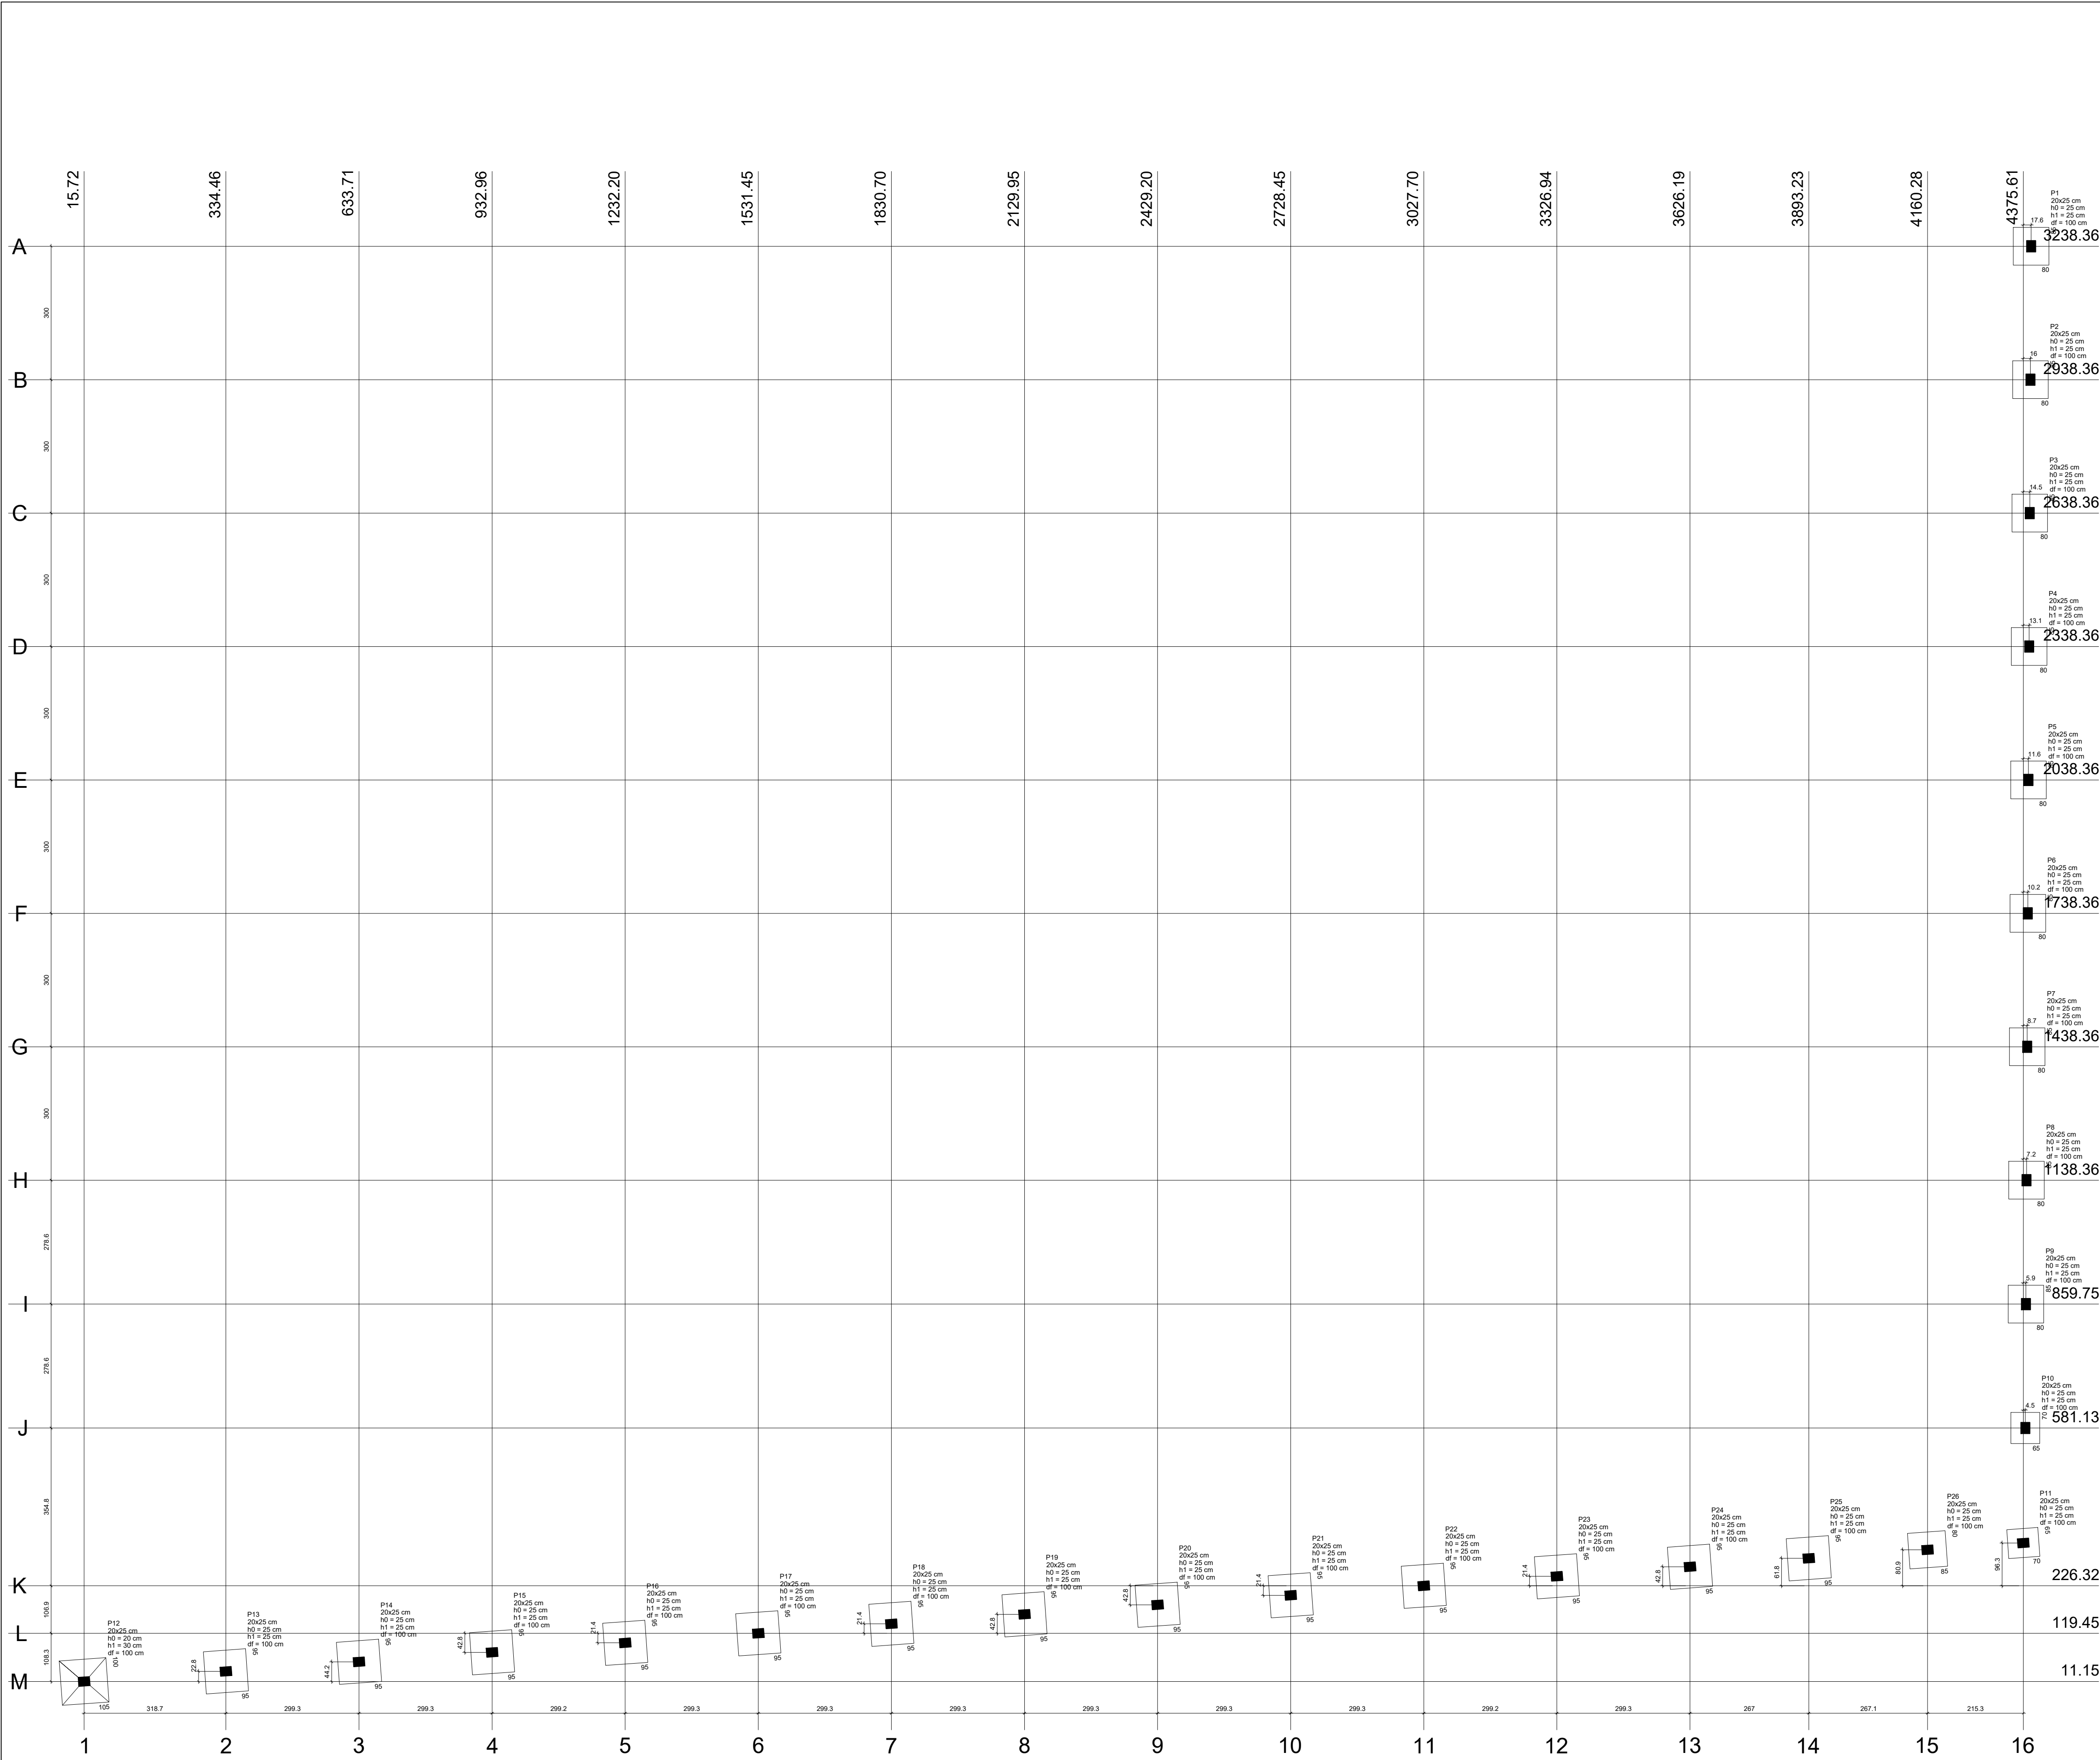

Planta de locação
escala 1:75

Pilar											
Nome	Seção (cm)	X (cm)	Y (cm)	Carga Máx. (kgf)	Carga Min. (kgf)	Mx (kgf.m)	My (kgf.m)	Fx (kgf)	Fy (kgf)		
P1	20x25	4393.20	3238.36	900	500	200	300	100	200		
P2	20x25	4391.63	2938.36	1100	900	200	300	100	200		
P3	20x25	4390.16	2638.36	1100	900	200	300	100	200		
P4	20x25	4388.70	2338.36	1100	900	300	300	100	200		
P5	20x25	4387.23	2038.36	1100	900	300	300	100	200		
P6	20x25	4385.77	1738.36	1100	900	300	300	100	200		
P7	20x25	4384.30	1438.36	1100	900	300	300	100	200		
P8	20x25	4382.84	1138.36	1100	900	300	300	200	200		
P9	20x25	4381.48	859.75	1000	800	300	300	100	200		
P10	20x25	4380.12	581.13	1000	800	300	200	100	200		
P11	20x25	4375.61	322.58	1000	600	200	200	200	200		
P12	20x25	15.72	11.15	800	600	500	200	200	200		
P13	20x25	334.46	33.94	1100	900	500	200	200	200		
P14	20x25	633.71	55.32	1100	900	500	200	200	200		
P15	20x25	932.96	76.69	1100	900	500	200	200	200		
P16	20x25	1232.20	98.07	1100	900	500	200	200	200		
P17	20x25	1531.45	119.45	1100	900	500	200	200	200		
P18	20x25	1830.70	140.82	1100	900	500	200	200	200		
P19	20x25	2129.95	162.20	1100	900	500	200	200	200		
P20	20x25	2429.20	183.57	1100	900	500	200	200	200		
P21	20x25	2728.45	204.95	1100	900	500	200	200	200		
P22	20x25	3027.70	226.32	1100	900	500	200	200	200		
P23	20x25	3326.94	247.70	1100	900	500	200	200	200		
P24	20x25	3626.19	269.08	1000	800	500	200	200	200		
P25	20x25	3893.23	288.15	1000	800	400	200	200	200		
P26	20x25	4160.28	307.23	1000	800	300	200	200	200		

Locação no eixo X		Locação no eixo Y		Fundação			
Coordenadas (cm)	Nome	Coordenadas (cm)	Nome	Lado B (cm)	Lado H (cm)	h0 / ha (cm)	h1 / hb (cm)
15.72	P12	3238.36	P1	80	85	25	25
334.46	P13	2938.36	P2	80	85	25	25
633.71	P14	2638.36	P3	80	85	25	25
932.96	P15	2338.36	P4	80	85	25	25
1232.20	P16	2038.36	P5	80	85	25	25
1531.45	P17	1738.36	P6	80	85	25	25
1830.70	P18	1438.36	P7	80	85	25	25
2129.95	P19	1138.36	P8	80	85	25	25
2429.20	P20	859.75	P9	80	85	25	25
2728.45	P21	581.13	P10	65	70	25	25
3027.70	P22	322.58	P11	65	70	25	25
3326.94	P23	307.23	P26	100	105	20	30
3626.19	P24	288.15	P25	95	95	25	25
3893.23	P25	269.08	P24	95	95	25	25
4160.28	P26	247.70	P23	95	95	25	25
4375.61	P11	226.32	P22	95	95	25	25
4380.12	P10	204.95	P21	95	95	25	25
4381.48	P9	183.57	P20	95	95	25	25
4382.84	P8	162.20	P19	95	95	25	25
4384.30	P7	140.82	P18	95	95	25	25
4385.77	P6	119.45	P17	95	95	25	25
4387.23	P5	98.07	P16	95	95	25	25
4388.70	P4	76.69	P15	95	95	25	25
4390.16	P3	55.32	P14	95	95	25	25
4391.63	P2	33.94	P13	95	95	25	25
4393.20	P1	11.15	P12	80	85	25	25

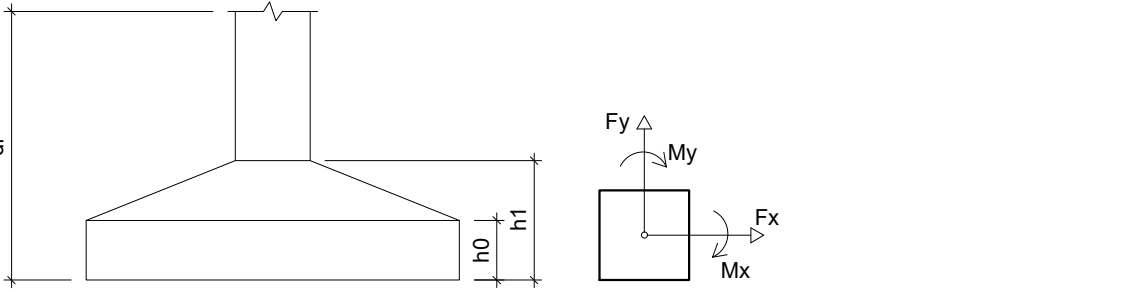

PROPRIETÁRIO: PREFEITURA MUNICIPAL DE COREMAS - PB

PROJETO: LINCOLN CARTAXO DE LIRA JÚNIOR CREA 160.814.689-8

CONSTRUÇÃO:

FOLHA 01/06
PROJETO: PRAÇA NOVA - COREMAS (PROJETO GUARITA)
CONCEDENTE: PREFEITURA MUNICIPAL DE COREMAS - PB
CONVENIENTE: PREFEITURA MUNICIPAL DE COREMAS - PB
LOCALIDADE: COREMAS - PB

DESENHO	DATA	RESPONSÁVEL	RUBRICA	DADOS
DESENHO	ABRIL/2025	LINCOLN CARTAXO		
CÓPIA				
VISTO				
ESCALAS	DESENHOS	CONVÊNIO		
	- VIGAS BALDRAME.			
INDICADA		REVISÃO		
		ARQUIVO		

Aprovações: