


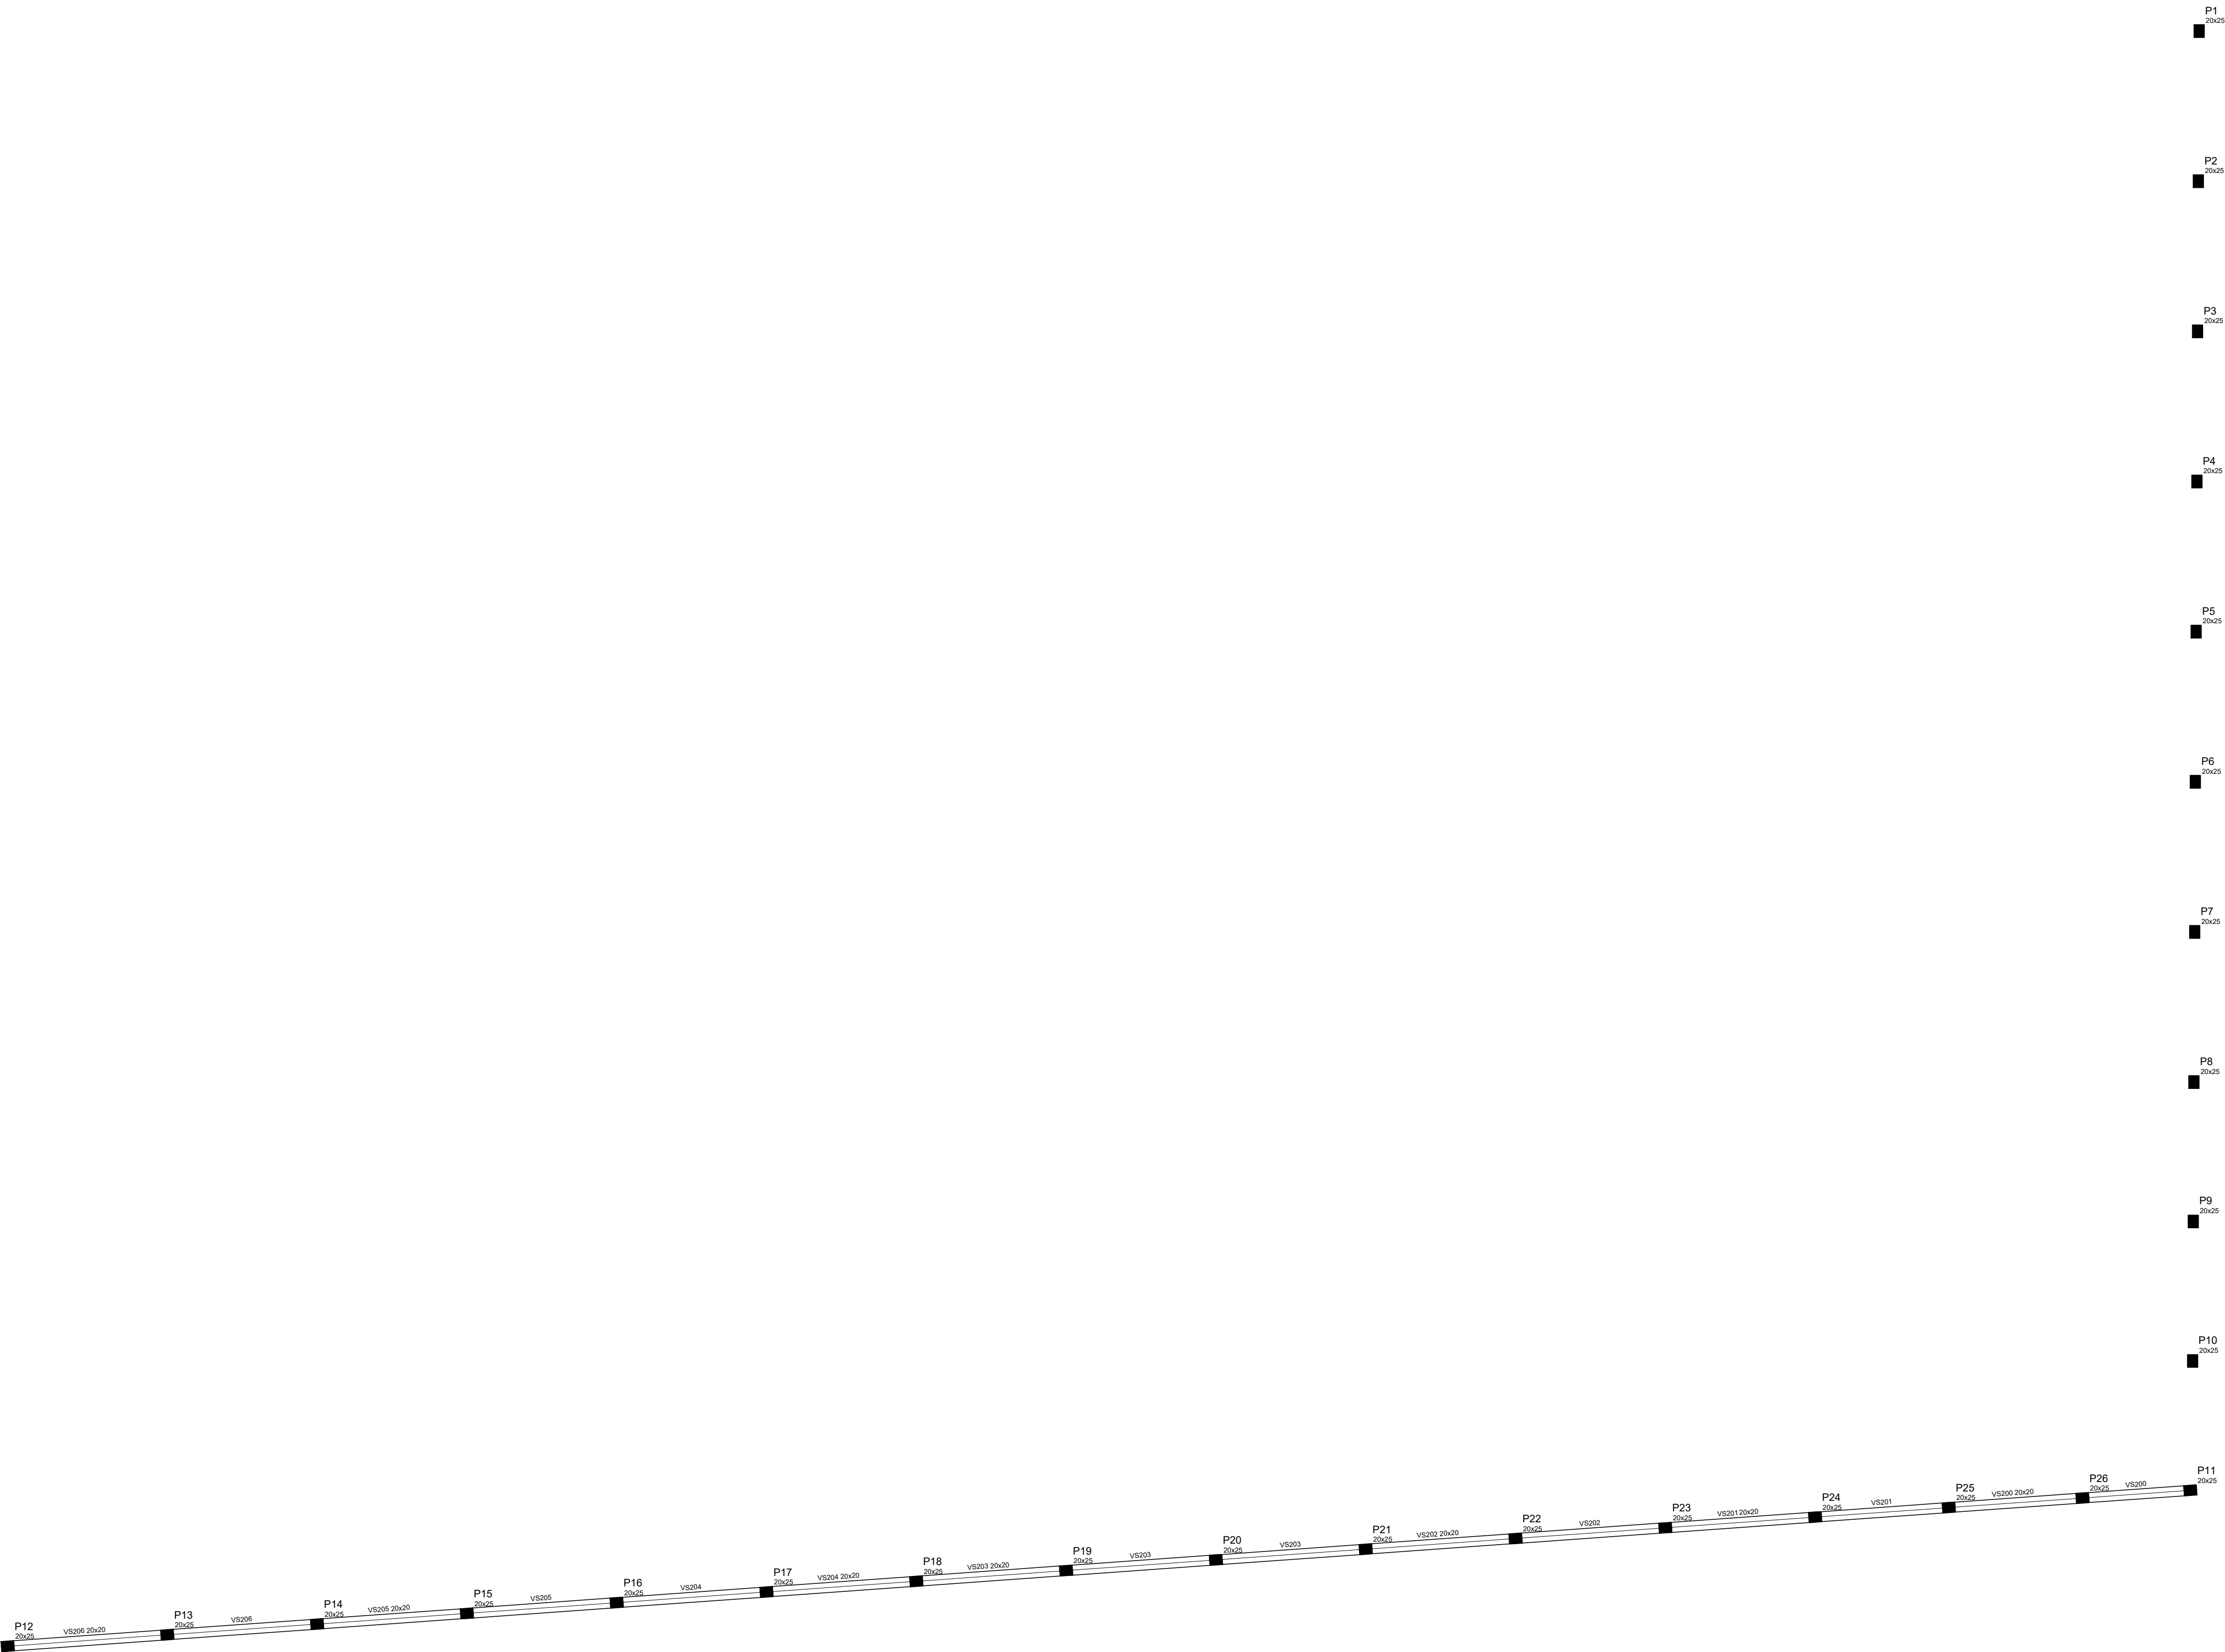

Forma do pavimento +230
escala 1:75

Vigas			
Nome	Seção (cm)	Elevação (cm)	Nível (cm)
VS200	20x20	0	230
VS201	20x20	0	230
VS202	20x20	0	230
VS203	20x20	0	230
VS204	20x20	0	230
VS205	20x20	0	230
VS206	20x20	0	230

Características dos materiais	
fck (kgf/cm²)	Ecs (kgf/cm²)
250	238000

Pilares			
Nome	Seção (cm)	Elevação (cm)	Nível (cm)
P1	20 x 25	0	230
P2	20 x 25	0	230
P3	20 x 25	0	230
P4	20 x 25	0	230
P5	20 x 25	0	230
P6	20 x 25	0	230
P7	20 x 25	0	230
P8	20 x 25	0	230
P9	20 x 25	0	230
P10	20 x 25	0	230
P11	20 x 25	0	230
P12	20 x 25	0	230
P13	20 x 25	0	230
P14	20 x 25	0	230
P15	20 x 25	0	230
P16	20 x 25	0	230
P17	20 x 25	0	230
P18	20 x 25	0	230
P19	20 x 25	0	230
P20	20 x 25	0	230
P21	20 x 25	0	230
P22	20 x 25	0	230
P23	20 x 25	0	230
P24	20 x 25	0	230
P25	20 x 25	0	230
P26	20 x 25	0	230

Legenda dos Pilares	
	Pilar que morre
	Pilar que passa
	Pilar que nasce
	Pilar com mudança de seção

PROPRIETÁRIO: PREFEITURA MUNICIPAL DE COREMAS - PB

PROJETO: LINCOLN CARTAXO DE LIRA JÚNIOR CREA 160.814.689-8

CONSTRUÇÃO:

FOLHA 04/06
PROJETO: PRAÇA NOVA - COREMAS (PROJETO GUARITA)
CONCEDENTE: PREFEITURA MUNICIPAL DE COREMAS - PB
CONVENIENTE: PREFEITURA MUNICIPAL DE COREMAS - PB
LOCALIDADE: COREMAS - PB

	DATA	RESPONSÁVEL	RUBRICA	DADOS
DESENHO	ABRIL/2025	LINCOLN CARTAXO		
CÓPIA				
VISTO				
ESCALAS	DESENHOS			CONVÊNIO
INDICADA	- VIGAS BALDRAME.			REVISÃO
				ARQUIVO

Aprovações: