



VS100

ESC 1:50

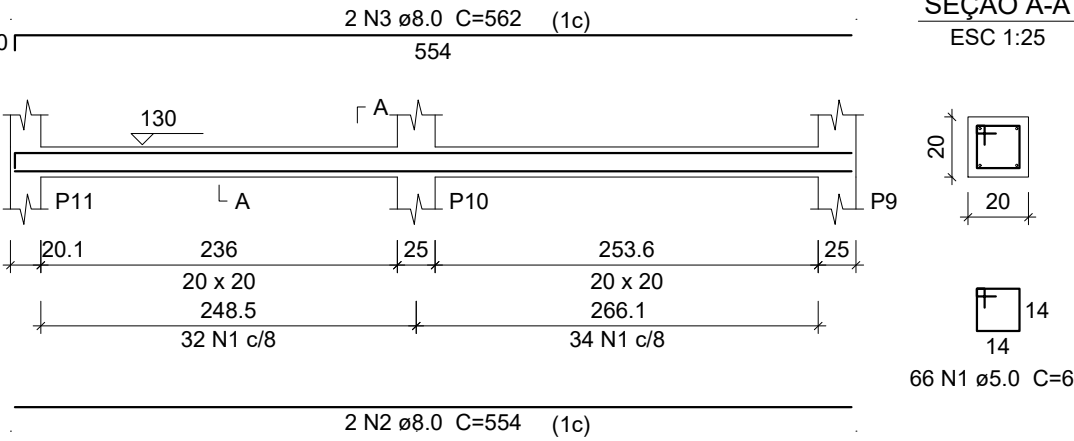


VS101

ESC 1:50

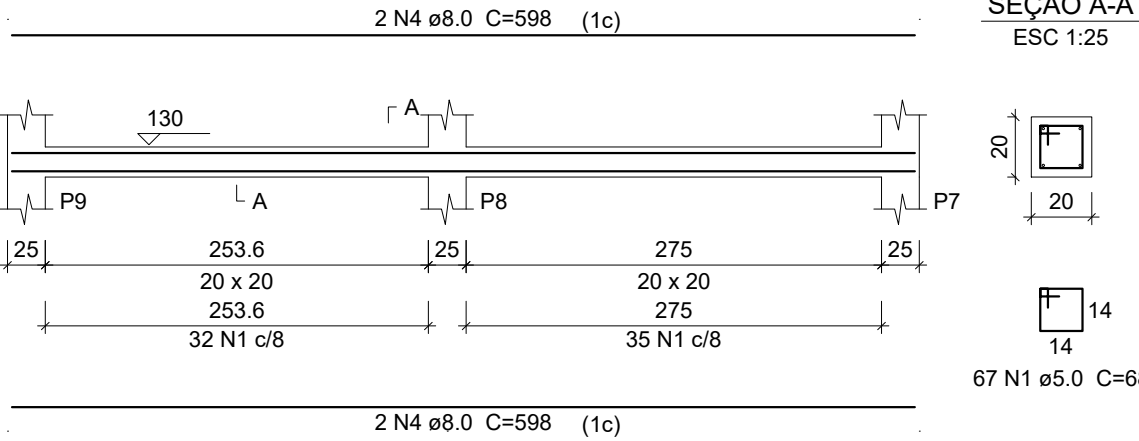


VS102

ESC 1:50

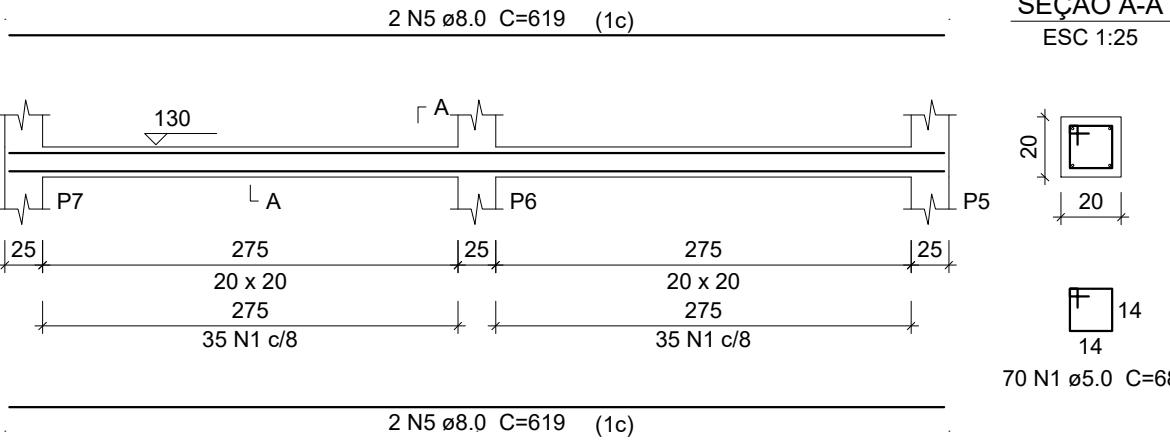


VS103

ESC 1:50

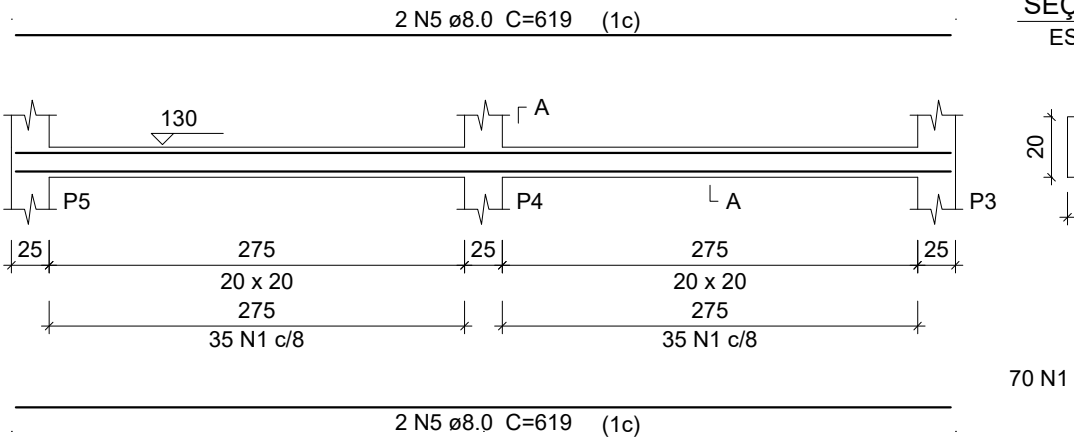

VS104

ESC 1:50

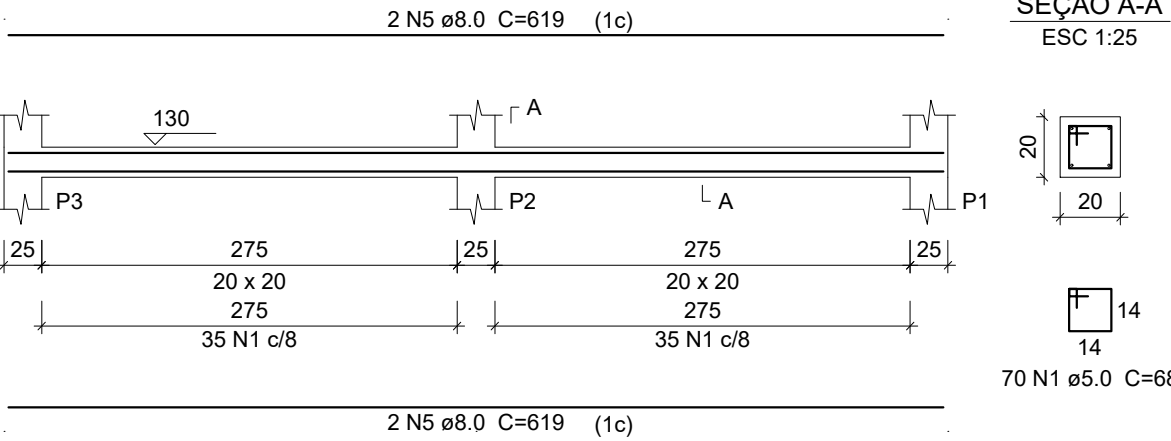

Relação do aço

AÇO	N	DIAM (mm)	QUANT (Barras)	UNIT (cm)	C.TOTAL (cm)
CA60	1	5.0	343	68	23324
CA50	2	8.0	2	554	1108
	3	8.0	2	562	1124
	4	8.0	4	598	2392
	5	8.0	12	619	7428


Resumo do aço

AÇO	DIAM (mm)	C.TOTAL (m)	PESO (kg)
CA50	8.0	120.6	47.6
CA60	5.0	233.3	36
PESO TOTAL (kg)			
CA50			47.6
CA60			36

Volume de concreto (C-25) = 1.22 m³
Área de forma = 18.23 m²


VS200

ESC 1:50

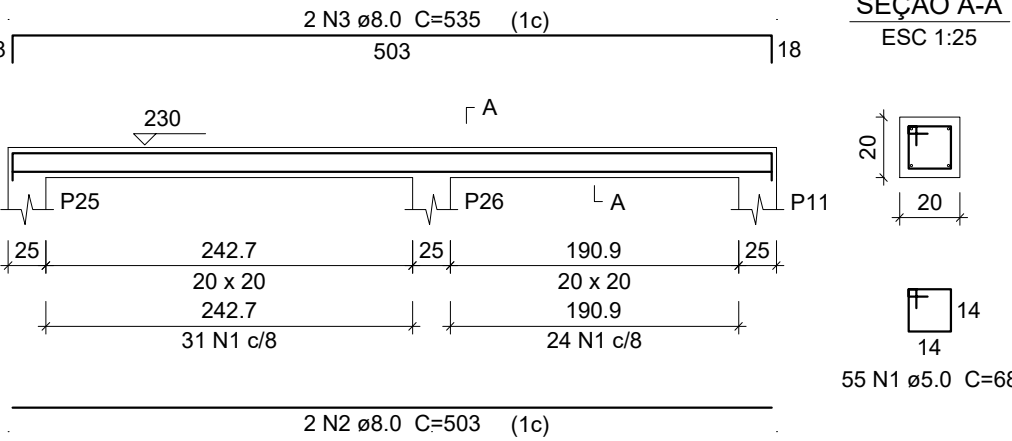


VS201

ESC 1:50

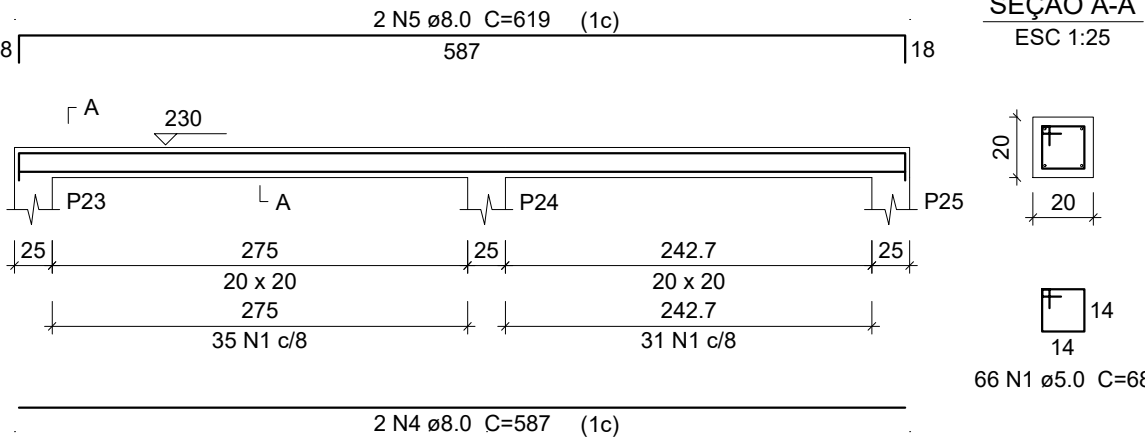


VS202

ESC 1:50

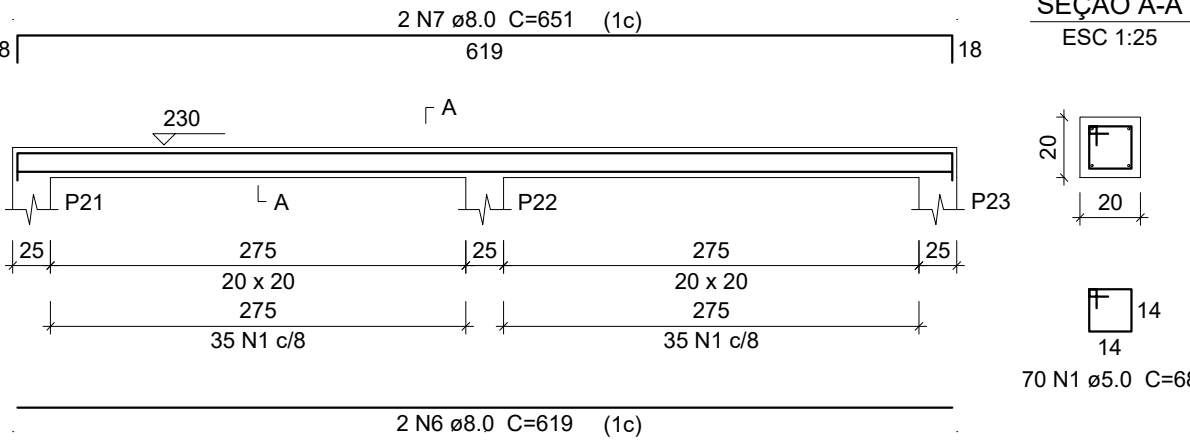


VS203

ESC 1:50

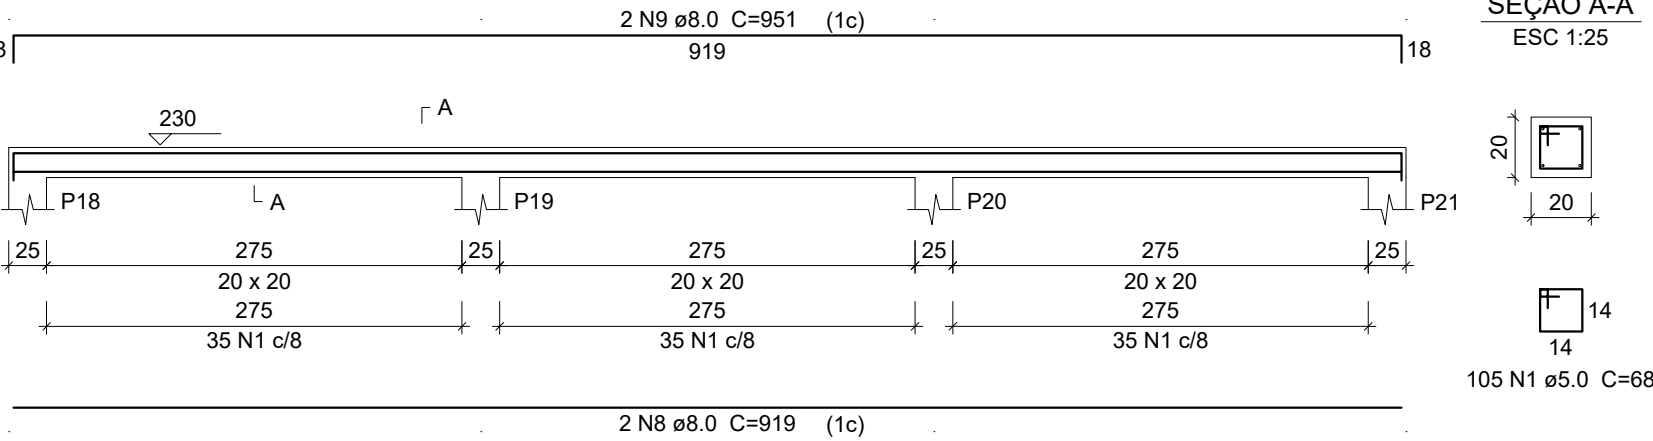


VS204

ESC 1:50

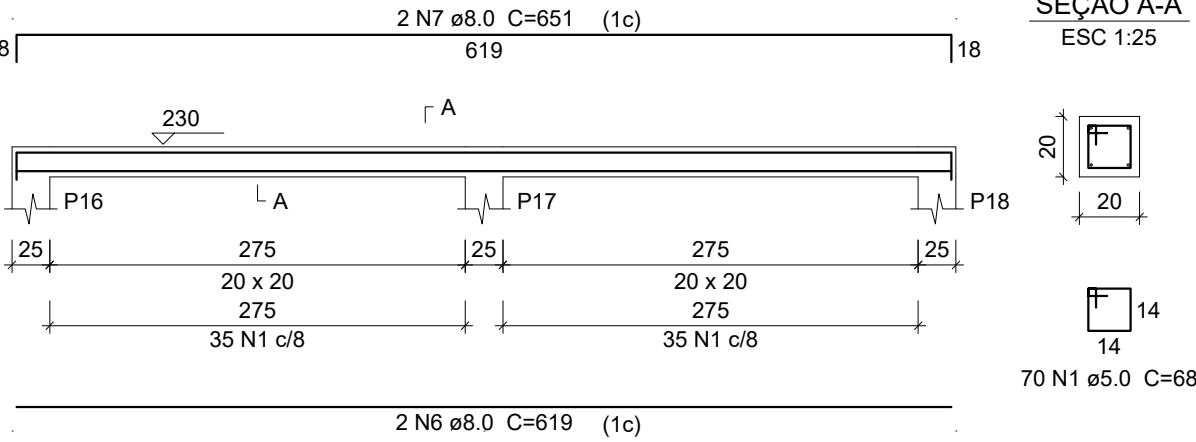


VS205

ESC 1:50

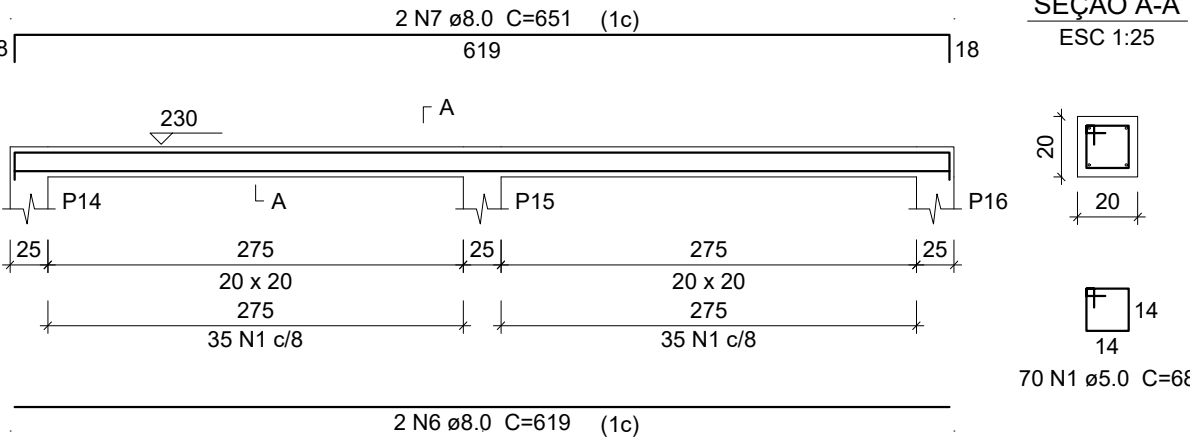

VS206

ESC 1:50

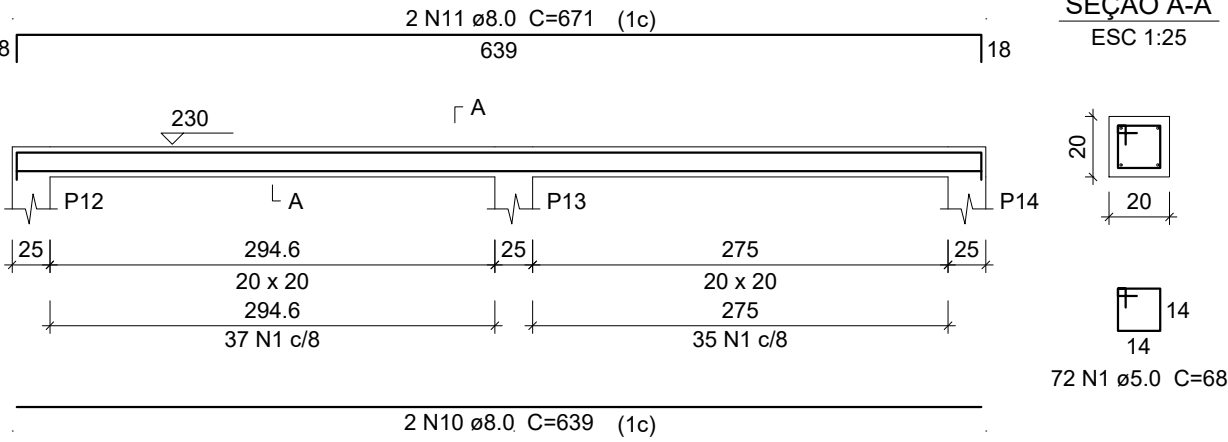

Relação do aço

AÇO	N	DIAM (mm)	QUANT (Barras)	UNIT (cm)	C.TOTAL (cm)
CA60	1	5.0	508	68	34544
CA50	2	8.0	2	503	1008
	3	8.0	2	535	1070
	4	8.0	2	587	1174
	5	8.0	2	619	1238
	6	8.0	6	619	3714
	7	8.0	6	651	3906
	8	8.0	2	919	1838
	9	8.0	2	951	1902
	10	8.0	2	639	1278
	11	8.0	2	671	1342

Resumo do aço

AÇO	DIAM (mm)	C.TOTAL (m)	PESO (kg)
CA50	8.0	184.7	72.9
CA60	5.0	345.5	53.2
PESO TOTAL (kg)			
CA50			72.9
CA60			53.2

Volume de concreto (C-25) = 1.82 m³
Área de forma = 27.28 m²

PROPRIETÁRIO: PREFEITURA MUNICIPAL DE COREMAS - PB

LINCOLN CARTAXO DE LIRA
Assinado de forma digital por LINCOLN CARTAXO DE LIRA JUNIOR:06897861405
Data: 2025.07.22 18:04:24 -03'00'

CONSTRUÇÃO:

FOLHA 06/06
PROJETO: PRAÇA NOVA - COREMAS (PROJETO GUARITA)
CONCEDENTE: PREFEITURA MUNICIPAL DE COREMAS - PB
CONVENIENTE: PREFEITURA MUNICIPAL DE COREMAS - PB
LOCALIDADE: COREMAS - PB

	DATA	RESPONSÁVEL	RUBRICA	DADOS
DESENHO	ABRIL/2025	LINCOLN CARTAXO		
CÓPIA				
VISTO				
ESCALAS	DESENHOS			CONVÊNIO
	- VIGAS BALDRAME.			
INDICADA				REVISÃO
				ARQUIVO

Aprovações: