


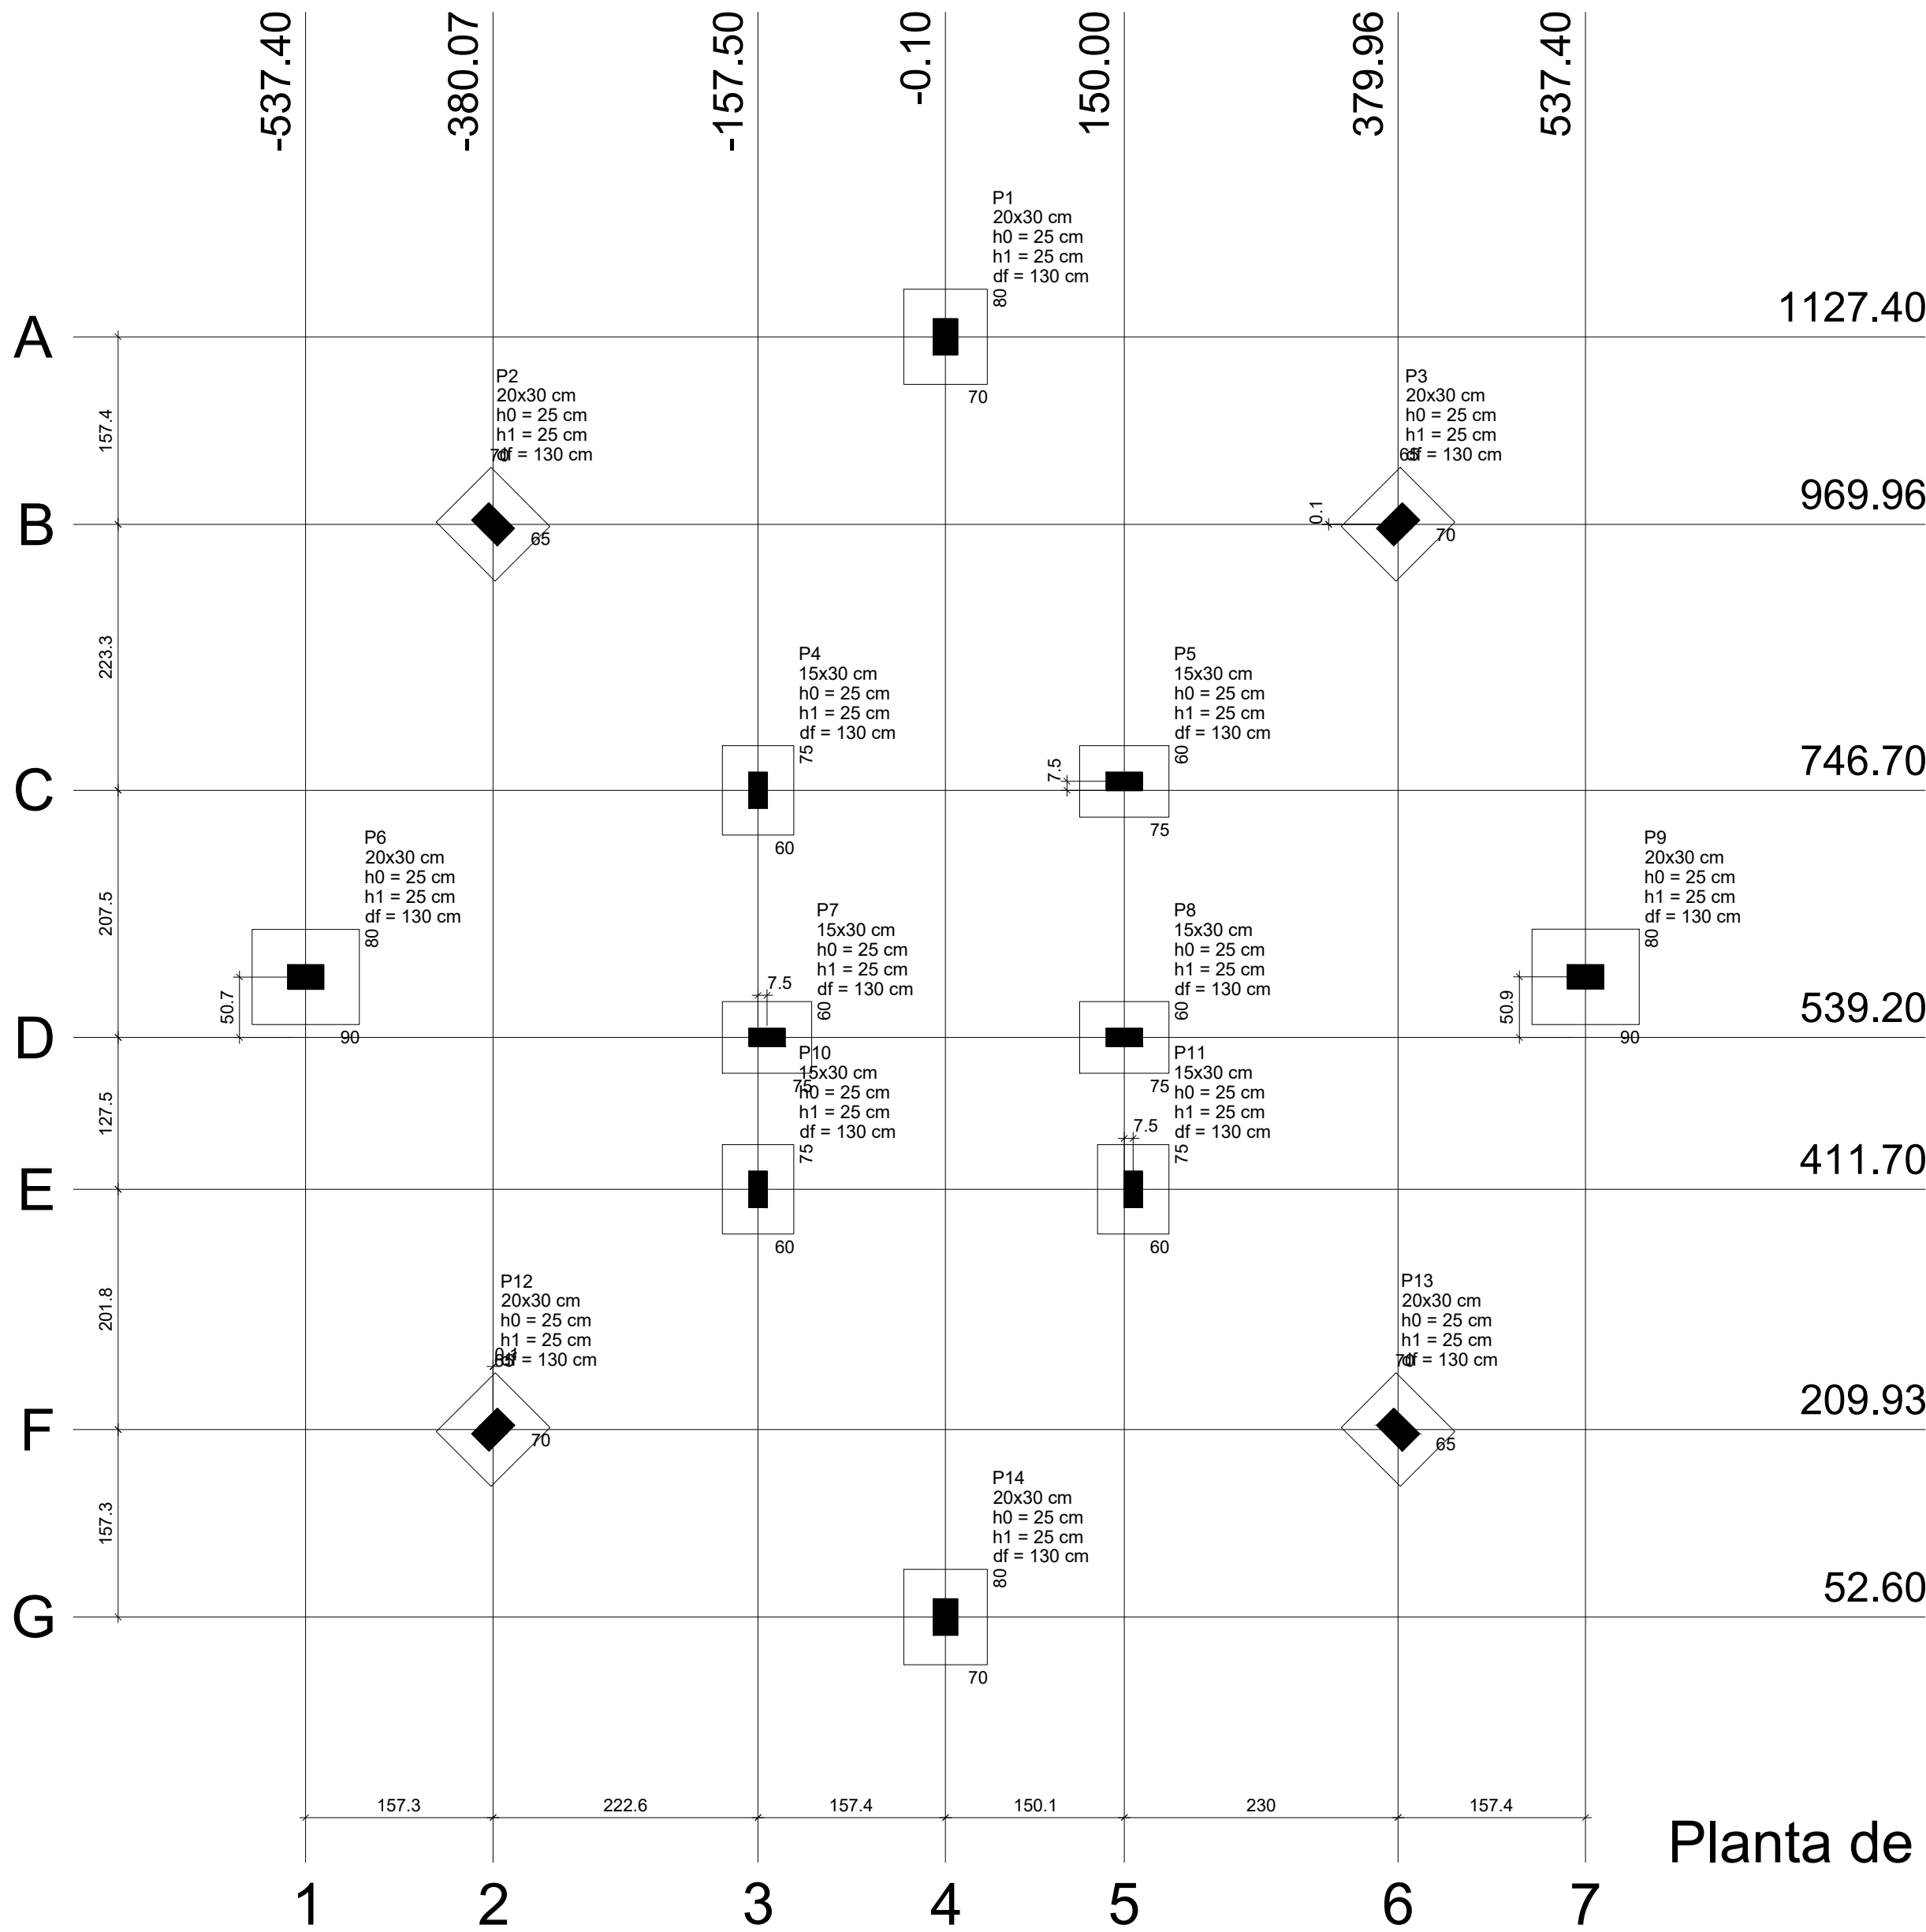

Planta de localização
escala 1:50

Pilar										Fundação				
Nome	Seção (cm)	X (cm)	Y (cm)	Carga Máx. (kgf)	Carga Mín. (kgf)	Mx (kgf.m)	My (kgf.m)	Fx (kgf)	Fy (kgf)	Lado B (cm)	Lado H (cm)	h0 / ha (cm)	h1 / hb (cm)	df (cm)
P1	20x30	-0.10	1127.40	1300	1100	400	100	100	500	70	80	25	25	130
P2	20x30	-380.07	969.96	1300	1100	200	300	500	100	65	70	25	25	130
P3	20x30	379.96	970.07	1300	1100	200	300	500	100	65	70	25	25	130
P4	15x30	-157.50	746.70	3900	3300	100	200	300	200	60	75	25	25	130
P5	15x30	150.00	754.20	4200	3500	100	300	400	200	60	75	25	25	130
P6	20x30	-537.40	589.90	1300	1100	100	500	200	100	80	90	25	25	130
P7	15x30	-150.00	539.20	4700	4000	100	300	300	200	60	75	25	25	130
P8	15x30	150.00	539.20	5100	4200	100	200	300	200	60	75	25	25	130
P9	20x30	537.40	590.10	1300	1100	100	500	200	100	80	90	25	25	130
P10	15x30	-157.50	411.70	3000	2400	200	200	400	200	60	75	25	25	130
P11	15x30	157.50	411.70	2800	2100	200	200	400	100	60	75	25	25	130
P12	20x30	-379.96	209.93	1300	1100	200	300	500	100	65	70	25	25	130
P13	20x30	379.96	209.93	1300	1100	200	300	500	100	65	70	25	25	130
P14	20x30	-0.10	52.60	1300	1100	400	100	100	500	70	80	25	25	130

Locação no eixo X	
Coordenadas (cm)	Nome
-537.40	P6
-380.07	P2
-379.96	P12
-157.50	P4, P10
-150.00	P7
-0.10	P1, P14
150.00	P5, P8
157.50	P11
379.96	P3, P13
537.40	P9

Locação no eixo Y	
Coordenadas (cm)	Nome
1127.40	P1
970.07	P3
969.96	P2
754.20	P5
746.70	P4
590.10	P9
589.90	P6
539.20	P7, P8
411.70	P10, P11
209.93	P12, P13
52.60	P14

PROPRIETÁRIO: PREFEITURA MUNICIPAL DE COREMAS - PB

PROJETO: LINCOLN CARTAXO DE LIRA JÚNIOR CREA 160.814.689-8

CONSTRUÇÃO:

FOLHA
01/07

PROJETO: PRAÇA NOVA - COREMAS (PROJETO GUARITA)
CONCEDENTE: PREFEITURA MUNICIPAL DE COREMAS - PB
CONVENIENTE: PREFEITURA MUNICIPAL DE COREMAS - PB
LOCALIDADE: COREMAS - PB

	DATA	RESPONSÁVEL	RUBRICA	DADOS
DESENHO	ABRIL/2025	LINCOLN CARTAXO		
CÓPIA				
VISTO				

ESCALAS	DESENHOS - LOCAÇÃO	CONVÊNIO
		REVISÃO
		ARQUIVO

Aprovações:



Av. Gov. Flávio Ribeiro Coutinho, 500, sl. 601
Jardim Oceania, 58037-005 - João Pessoa (PB)
Tel +55 (83) 3578.3426
Cel +55 (83) 99924.4447
e-mail: lcprojetos@hotmail.com