



Armação positiva das lajes do pavimento +275 (Eixo X)

escala 1:50

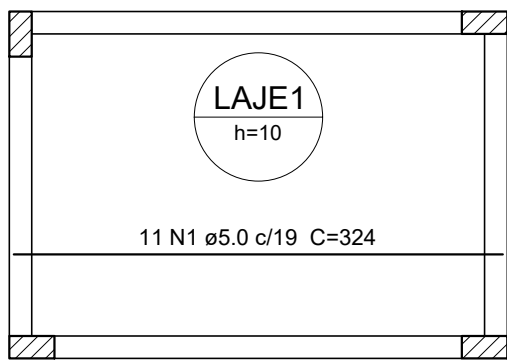

Armação positiva das lajes do pavimento +275 (Eixo Y)

escala 1:50

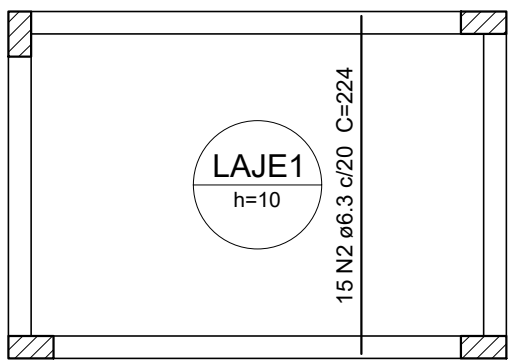

Relação do aço					
Positivos X			Positivos Y		
AÇO	N	DIAM (mm)	QUANT (Barras)	UNIT (cm)	C.TOTAL (cm)
CA60	1	5.0	11	324	3564
CA50	2	6.3	15	224	3360

Resumo do aço			
AÇO	DIAM (mm)	C.TOTAL (m)	PESO (kg)
CA50	6.3	33.6	8.2
CA60	5.0	35.7	5.5
PESO TOTAL (kg)			
CA50	8.2		
CA60	5.5		

Volume de concreto (C-25) = 0.6 m³
Área de forma = 6.04 m²

PROPRIETÁRIO: PREFEITURA MUNICIPAL DE COREMAS - PB





PROJETO: LINCOLN CARTAXO DE LIRA JÚNIOR CREA 160.814.689-8

CONSTRUÇÃO:

FOLHA 07/07	PROJETO: PRAÇA NOVA - COREMAS (PROJETO GUARITA)		
	CONCEDENTE: PREFEITURA MUNICIPAL DE COREMAS - PB		
	CONVENIENTE: PREFEITURA MUNICIPAL DE COREMAS - PB		
	LOCALIDADE: COREMAS - PB		

	DATA	RESPONSÁVEL	RUBRICA	DADOS
DESENHO	ABRIL/2025	LINCOLN CARTAXO		
CÓPIA				
VISTO				
ESCALAS INDICADA	DESENHOS - LAJES; - PILARES.			CONVÊNIO
				REVISÃO
				ARQUIVO

Aprovações:

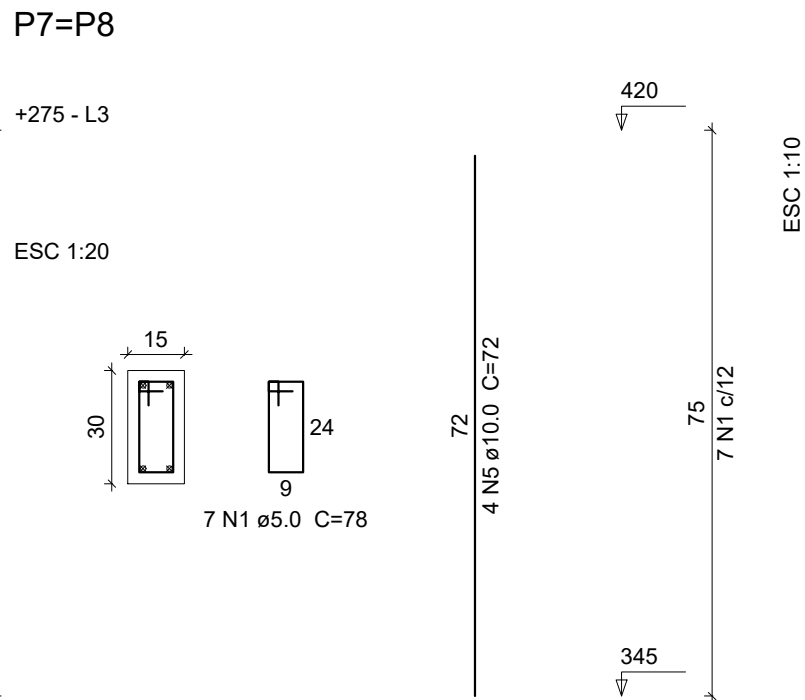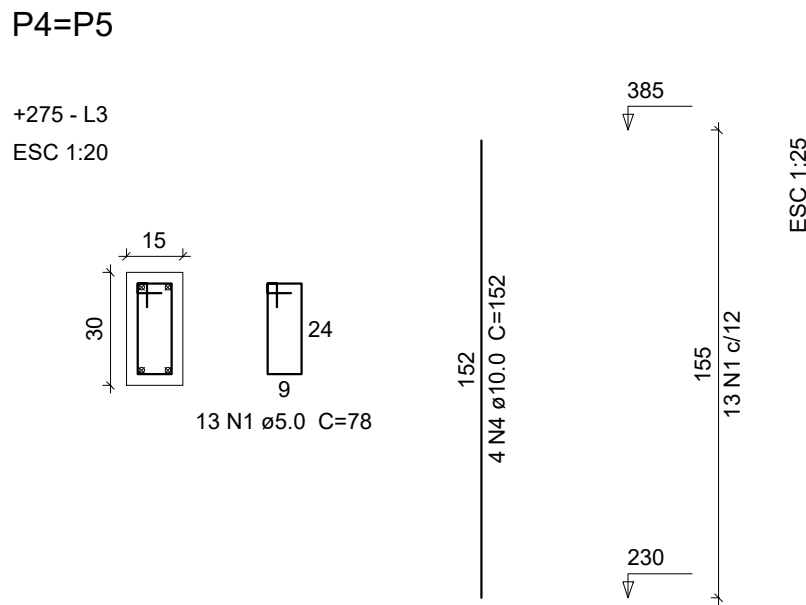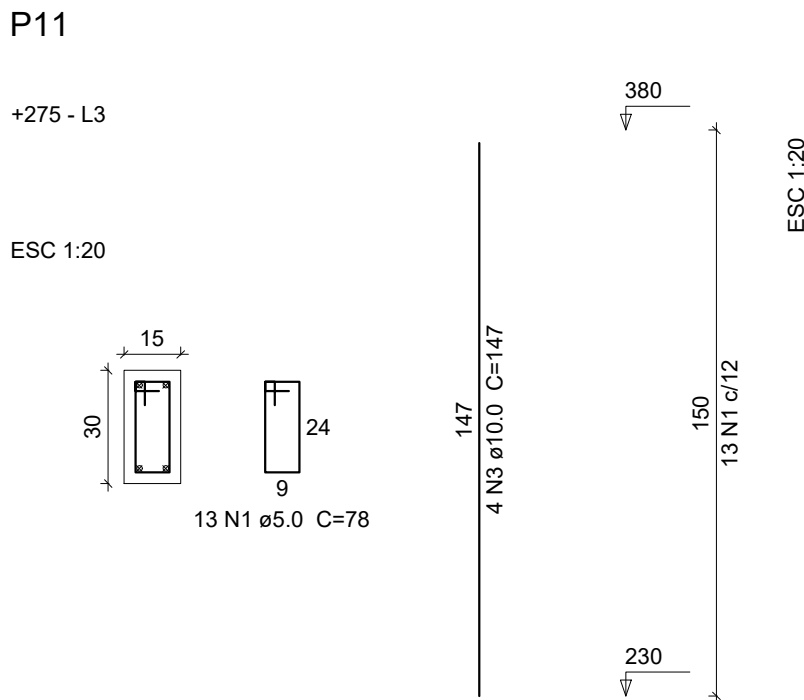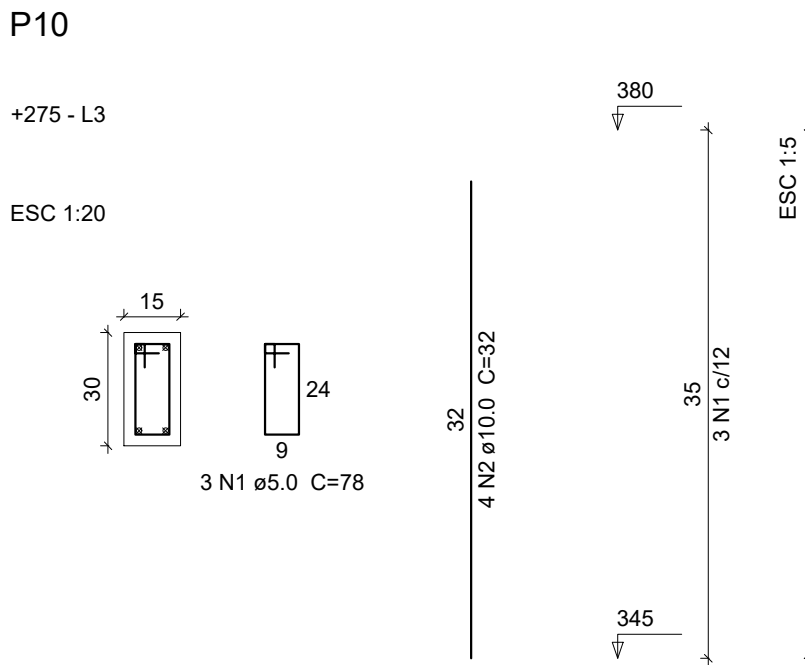

Relação do aço					
AÇO	N	DIAM (mm)	QUANT (Barras)	UNIT (cm)	C.TOTAL (cm)
CA60	1	5.0	56	78	4368
CA50	2	10.0	4	32	128
	3	10.0	4	147	588
	4	10.0	8	152	1216
	5	10.0	8	72	576

Resumo do aço			
AÇO	DIAM (mm)	C.TOTAL (m)	PESO (kg)
CA50	10.0	25.1	15.5
CA60	5.0	43.7	6.7
PESO TOTAL (kg)			
CA50	15.5		
CA60	6.7		

Volume de concreto (C-25) = 0.29 m³
Área de forma = 5.81 m²