


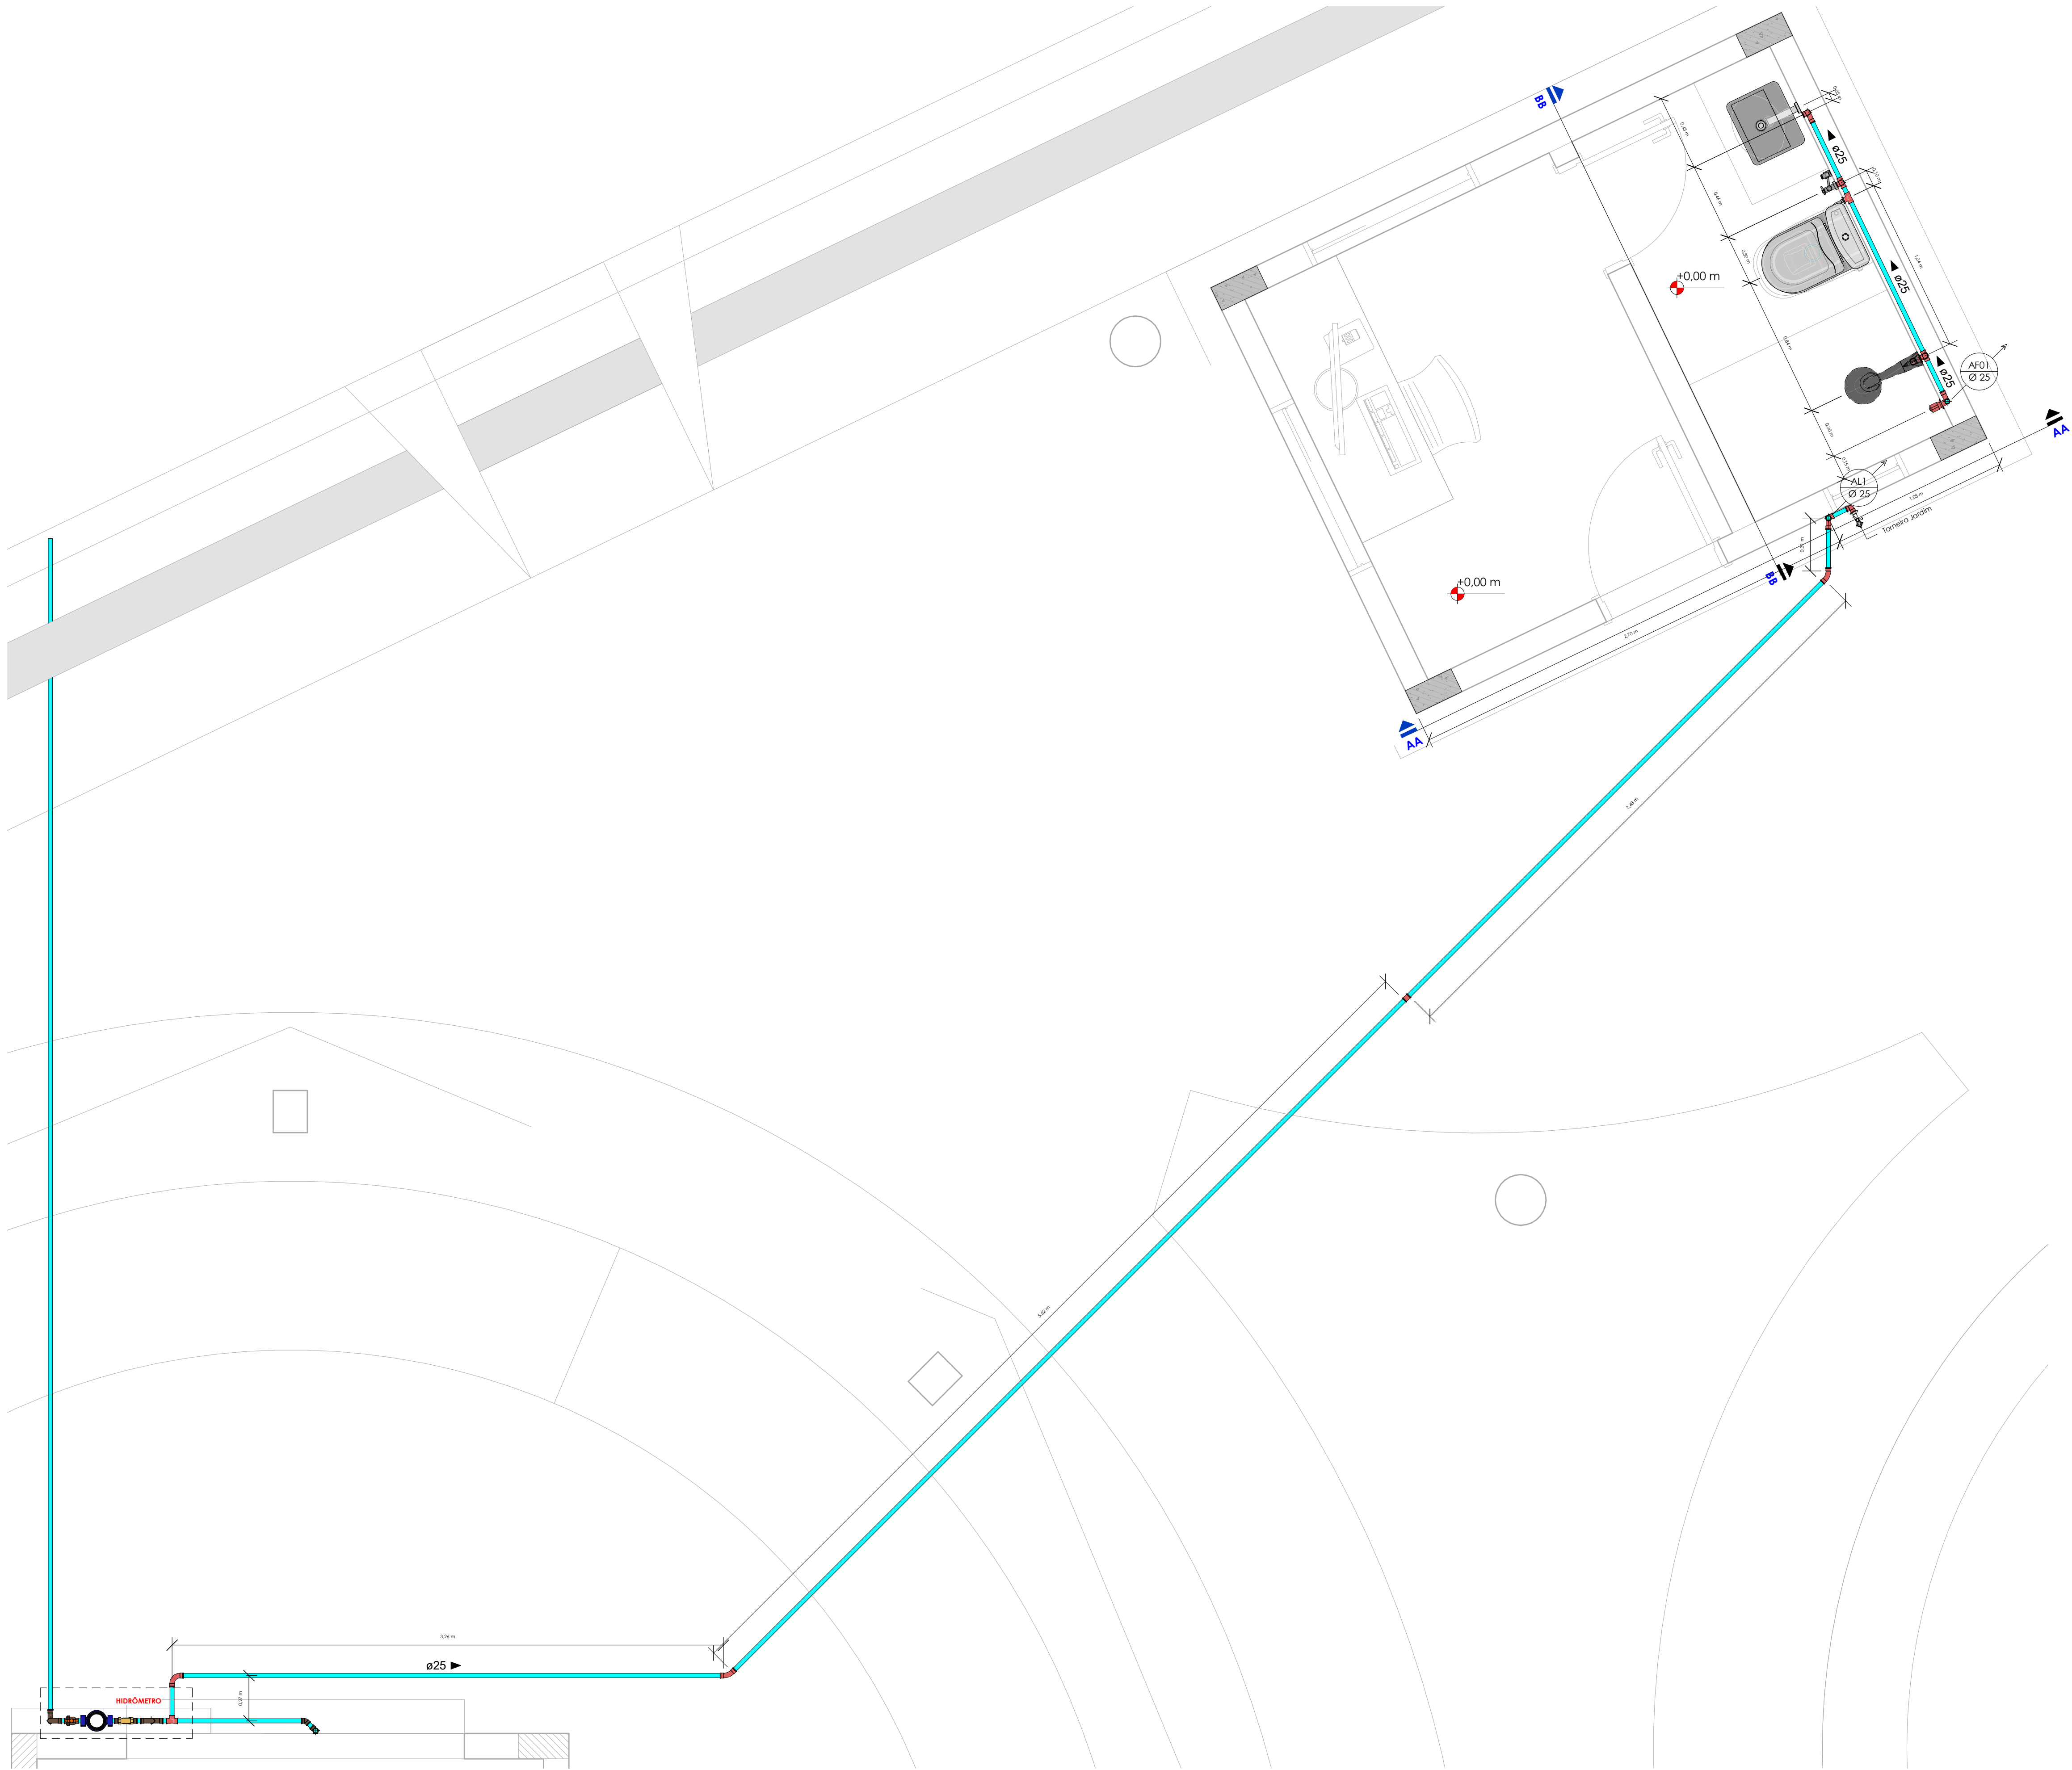

LEGENDA:

- TUBULAÇÃO PVC BRANCO - ESGOTO
- TUBULAÇÃO PVC BRANCO SN - VENTILAÇÃO ESGOTO
- TUBULAÇÃO PVC MARROM - ÁGUA FRIA
- AL-nn
Øxx -ALIMENTAÇÃO DO RESERV. SUPERIOR
nn: número da coluna
xx: diâmetro nominal da coluna
- CV-nn
Øxx -COLUNA DE VENTILAÇÃO
nn: número da coluna
xx: diâmetro nominal da coluna
- AF-nn
Øxx -COLUNA DE ÁGUA FRIA (BARRILETE)
nn: número da coluna
xx: diâmetro nominal da coluna

LEGENDA - TUBULAÇÕES

- ESGOTO - ÁGUAS CINZAS
- ESGOTO - ÁGUAS NEGRAS
- ÁGUA FRIA
- VENTILAÇÃO
- ÁGUA QUENTE

TABELA DE ALTURAS

SIGLA	PONTO	ALTURA
CH	CHUVEIRO	2,10 m
LV	LAVATÓRIO	0,95 m
VS	VASO SANITÁRIO	0,20 m
RG	REGISTRO DE GAVETA	1,80 m
RP	REGISTRO DE PRESSÃO	1,20 m
PIA	PIA DE COZINHA	0,90 m
TQ	TANQUE	1,10 m

PROPRIETÁRIO: PREFEITURA MUNICIPAL DE COREMAS - PB

PROJETO: LINCOLN CARTAXO DE LIRA JÚNIOR CREA 160.814.689-8

PROJETO: INSTALAÇÕES HIDRÁULICAS, GUARITA - PRAÇA NOVA COREMAS

CONCEDENTE: PREFEITURA MUNICIPAL DE COREMAS - PB

CONVENIENTE: MUNICÍPIO DE COREMAS - PB

LOCAL: COREMAS - PB

DATA	RESPONSÁVEL TÉCNICO	RUBRICA	DADOS
24/04/2025	LINCOLN CARTAXO		CREA 160.814.689-8
CÓPIA			
VISTO			

PRANCHA:

02 / 03

DESCRIÇÃO:

PLANTA BAIXA - TÉRREO

ESCALA:

INDICADA



Av. Gov. Flavio R. Coutinho, 500, sl. 601
Jd. Oceania, 58037-005 - João Pessoa (PB)
Tel +55 99924.4447
e-mail: contato@lclprojetos.com