

Reforma da Rodoviária e da Praça Padre Guilherme Town o município de Corenas-PB

Planilha Orçamentária Consolidada

Item	Fonte	Código	Discriminação dos Serviços	Quantidade	Unidade	Unitário sem BDI	Unitário com BDI	Total sem BDI	Total com BDI
SERVIÇOS INICIAIS									
1.1	ORSE	16	Demolição manual de piso cimentado sobre lastro de concreto	730,27	m²	R\$ 24,28	R\$ 29,74	R\$ 17.730,96	R\$ 21.716,23
1.2	CPU	1	Limpeza inicial da obra, inclusive retirada de entulho	15,00	dia	R\$ 139,76	R\$ 171,16	R\$ 2.096,40	R\$ 2.567,40
PAREDES									
2.1	SINAPI	103328	ALVENARIA DE VEDAÇÃO DE BLOCOS CERÂMICOS FURADOS NA HORIZONTAL DE 9X19X19 CM (ESPESSURA 9 CM) E ARGAMASSA DE ASSENTAMENTO COM PREPARO EM BETONEIRA	75,06	m³	R\$ 72,76	R\$ 88,11	R\$ 5.461,37	R\$ 6.688,60
2.2	SINAPI	88497	EMASSAMENTO COM MASSA LATEX, APLICAÇÃO EM PAREDE, DUAS DEMÃOIS, LIXAMENTO MANUAL	385,408	m²	R\$ 13,87	R\$ 16,99	R\$ 5.345,61	R\$ 6.548,08
2.3	SINAPI	88489	PINTURA LATEX ACRILICA PREMIUM, APLICAÇÃO MANUAL EM PAREDES, DUAS DEMÃOIS	385,408	m²	R\$ 8,69	R\$ 10,64	R\$ 3.349,20	R\$ 4.100,74
2.4	ORSE	11491	Pastilha em porcelana esmalhada, 5 x 10 cm, marca ATLAS, linha engenharia, ref. Branco - B2140 ou similar, aplicada com argamassa industrializada ac-ii, rejuntada, exclusive emboço (ou similar)	115,624	m²	R\$ 204,78	R\$ 250,79	R\$ 23.677,48	R\$ 28.997,34
2.5	ORSE	13240	Pastilha em porcelana esmalhada, 5 x 10 cm, marca ATLAS, série CAMPAINA, cor vermelho OM 10049 ou similar, aplicada com argamassa industrializada ac-ii, rejuntada, exclusive emboço (ou similar)	116,135	m²	R\$ 188,46	R\$ 230,81	R\$ 21.886,80	R\$ 26.805,12
2.6	ORSE	10894	Revestimento cerâmico para piso ou parede, 32 x 66 cm, pel. 3, Elizabeth, porcelanato, retificado, linha nevada acilnada ou similar, aplicado com argamassa industrializada ac-iii, rejunte acrílico, exclusive regularização de base ou emboço	352,604	m²	R\$ 83,31	R\$ 102,03	R\$ 29.375,44	R\$ 35.976,19
PISO									
3.1	SINAPI	92396	EXECUÇÃO DE PASSEIO EM PISO INTERTRAVADO, COM BLOCO RETANGULAR COR NATURAL DE 20 X 10 CM, ESPESSURA 6 CM.	543,51	m²	R\$ 60,36	R\$ 73,92	R\$ 32.805,26	R\$ 40.176,26
3.2	SINAPI	93679	EXECUÇÃO DE PASSEIO EM PISO INTERTRAVADO, COM BLOCO RETANGULAR COLORIDO DE 20 X 10 CM, ESPESSURA 6 CM.	730,3	m²	R\$ 66,44	R\$ 81,37	R\$ 48.521,13	R\$ 59.424,51
3.3	ORSE	8928	Revestimento cerâmico para piso ou parede, 50 x 50 cm, antiderrapante (porcelanato), Elizabeth ou similar, aplicado com argamassa industrializada ac-ii, rejuntado, exclusive regularização de base ou emboço	23,35	m²	R\$ 70,47	R\$ 86,30	R\$ 1.645,47	R\$ 2.015,11
3.4	ORSE	10983	Revestimento cerâmico para piso ou parede, 63 x 63 cm, pel. 5, Biancogrês, porcelanato esmalhado acilnado, retificado interno, linha cimento grigio ou similar, apl. d arg. ind. AC-III, rejunte acrílico, exclusive regularização de base ou emboço	195,05	m²	R\$ 85,56	R\$ 104,79	R\$ 16.688,48	R\$ 20.439,29
COBERTA									
4.1	CPU	2	ESTRUTURA EM AÇO GALVANIZADO REVESTIDO EM PINTURA ALTO MOTIVNA NA COR BRANCO	1,00	und	R\$ 1.777,05	R\$ 2.176,35	R\$ 1.777,05	R\$ 2.176,35
4.2	CPU	2	COBERTA EM AÇO GALVANIZADO REVESTIDO EM PINTURA ALTO MOTIVNA NA COR BRANCO E POLICARBONATO NA COR BRONZE	1,00	und	R\$ 39.536,07	R\$ 48.419,82	R\$ 39.536,07	R\$ 48.419,82
4.3	SINAPI	100383	FABRICAÇÃO E INSTALAÇÃO DE PONTALETES DE MADEIRA NÃO APARELHADA PARA TELHADOS COM ATÉ 2 ÁGUAS E COM TELHA ONDULADA DE FIBROCIMENTO, ALUMÍNIO OU PLÁSTICA EM EDIFÍCIO RESIDENCIAL DE MÚLTIPLOS PAVIMENTOS, INCLUSIVE TRANSPORTE VERTICAL	140,20	m²	R\$ 20,84	R\$ 25,52	R\$ 2.921,77	R\$ 3.577,90
4.4	SINAPI	94207	TELHAMENTO COM TELHA ONDULADA DE FIBROCIMENTO E = 6 MM, COM RECORRIMENTO LATERAL DE 1/4 DE ONDA PARA TELHADO COM INCLINAÇÃO MAIOR QUE 10° - C OM ATÉ 2 ÁGUAS, INCLUSIVE ICAMENTO	140,2	m²	R\$ 59,07	R\$ 72,34	R\$ 8.281,61	R\$ 10.142,07
4.5	SINAPI	94228	CALHA EM CHAPA DE AÇO GALVANIZADO NÚMERO 24, DESENVOLVIMENTO DE 5	34,12	m	R\$ 79,67	R\$ 97,57	R\$ 2.718,34	R\$ 3.329,08
4.6	SINAPI	94231	RUFO EM CHAPA DE AÇO GALVANIZADO NÚMERO 24, CORTE DE 25 CM, INCLUSIVE TRANSPORTE VERTICAL	52,18	m	R\$ 49,95	R\$ 61,17	R\$ 2.606,39	R\$ 3.191,85
BANCOS									
5.1	4420	ORSE	Banco de concreto em alvenaria de tijolos maciços, assento em concreto simples, sem encosto, revestido em todas as faces com cerâmica Elizabeth 20x20 cm ou similar	337,29	m	R\$ 224,87	R\$ 275,40	R\$ 75.846,40	R\$ 92.889,67

Fernando Matias Mamede
Engenheiro Civil

CREA: 11466382021

Fernando Matias Mamede
Eugenheiro Civil
CREA: 11466382021

8.2		METAIS, ACESSÓRIOS E TUBULAÇÃO													
8.2.1	SINAPI	89353	REGISTRO DE GAVETA BRUTO, LATÃO, ROSCÁVEL, 3/4" - FORNECIMENTO E INSTALAÇÃO.	2,00	und	R\$	44,99	R\$	55,10	R\$	89,98	R\$	110,20		
8.2.2	SINAPI	89707	CAIXA SIFONADA, PVC, DN 100 X 100 X 50 MM, JUNTA ELÁSTICA, FORNECIDA E INSTALADA EM RAMAL DE DESCARGA OU EM RAMAL DE ESGOTO SANITÁRIO.	8,00	und	R\$	38,73	R\$	47,43	R\$	309,84	R\$	379,44		
8.2.3	SINAPI	89957	PONTO DE CONSUMO TERMINAL DE ÁGUA FRIA (SUBRAMAL) COM TUBULAÇÃO DE PVC, DN 25 MM, INSTALADO EM RAMAL DE ÁGUA, INCLUSOS RASGO E CHUMBAMENTO E M ALVENARIA.	8,00	und	R\$	115,91	R\$	141,95	R\$	927,28	R\$	1.135,60		
8.2.4	SINAPI	89512	TUBO PVC, SÉRIE R, ÁGUA PLUVIAL, DN 100 MM, FORNECIDO E INSTALADO EM RAMAL DE ENCAMINHAMENTO.	15,00	m	R\$	44,63	R\$	54,66	R\$	669,45	R\$	819,90		
8.2.5	SINAPI	89446	TUBO, PVC, SOLDÁVEL, DN 25MM, INSTALADO EM PRUMADA DE ÁGUA - FORNECIMENTO E INSTALAÇÃO.	74,80	m	R\$	5,58	R\$	6,83	R\$	417,38	R\$	510,88		
8.2.6	SINAPI	89362	JOELHO 90 GRAUS, PVC, SOLDÁVEL, DN 25MM, INSTALADO EM RAMAL OU SUB-RAMAL DE ÁGUA - FORNECIMENTO E INSTALAÇÃO.	8,00	und	R\$	7,14	R\$	8,74	R\$	57,12	R\$	69,92		
8.2.7	SINAPI	94686	JOELHO 90 GRAUS, PVC, SOLDÁVEL, DN 110 MM INSTALADO EM RESERVAÇÃO DE ÁGUA DE EDIFICAÇÃO QUE POSSUA RESERVATÓRIO DE FIBRA/FIBROCIMENTO FORN ECIMENTO E INSTALAÇÃO.	4,00	und	R\$	259,51	R\$	317,82	R\$	1.038,04	R\$	1.271,28		
8.2.8	SINAPI	89387	LUIVA DE CORRER, PVC, SOLDÁVEL, DN 32MM, INSTALADO EM RAMAL OU SUB-RAMAL DE ÁGUA FORNECIMENTO E INSTALAÇÃO.	4,00	und	R\$	30,16	R\$	36,94	R\$	120,64	R\$	147,76		
8.2.9	SINAPI	94671	LUIVA, PVC, SOLDÁVEL, DN 110 MM, INSTALADO EM RESERVAÇÃO DE ÁGUA DE EDIFICAÇÃO QUE POSSUA RESERVATÓRIO DE FIBRA/FIBROCIMENTO FORNECIMENTO E INSTALAÇÃO.	2,00	und	R\$	04,88	R\$	128,45	R\$	209,76	R\$	256,90		
8.2.10	SINAPI	89617	TE, PVC, SOLDÁVEL, DN 25MM, INSTALADO EM PRUMADA DE ÁGUA - FORNECIMENT UN CR 6,00 O E INSTALAÇÃO.	8,00	und	R\$	6,00	R\$	7,35	R\$	48,00	R\$	58,80		
8.2.11	SINAPI	89571	TE, PVC, SÉRIE R, ÁGUA PLUVIAL, DN 100 X 100 MM, JUNTA ELÁSTICA, FORNECIDO E INSTALADO EM RAMAL DE ENCAMINHAMENTO.	3,00	und	R\$	67,70	R\$	82,91	R\$	203,10	R\$	248,73		
8.2.12	SINAPI	89714	TUBO PVC, SÉRIE NORMAL, ESGOTO PREDIAL, DN 100 MM, FORNECIDO E INSTALADO EM RAMAL DE DESCARGA OU RAMAL DE ESGOTO SANITÁRIO.	20,00	m	R\$	32,26	R\$	39,51	R\$	645,20	R\$	790,20		
8.2.13	SINAPI	89856	LUIVA SIMPLES, PVC, SÉRIE NORMAL, ESGOTO PREDIAL, DN 100 MM, JUNTA ELÁSTICA, FORNECIDO E INSTALADO EM SUBCOLETOR AÉREO DE ESGOTO SANITÁRIO, A	4,00	und	R\$	17,11	R\$	20,95	R\$	68,44	R\$	83,80		
8.2.14	SINAPI	89746	JOELHO 45 GRAUS, PVC, SÉRIE NORMAL, ESGOTO PREDIAL, DN 100 MM, JUNTA ELÁSTICA, FORNECIDO E INSTALADO EM RAMAL DE DESCARGA OU RAMAL DE ESGOTO SANITÁRIO.	6,00	und	R\$	25,89	R\$	31,71	R\$	155,34	R\$	190,26		
9.			ELETRICO												
9.1	SINAPI	103782	LUMINÁRIA TIPO PLAFON CIRCULAR, DE SOBREPOR, COM LED DE 12/13 W - FORN UN CR 31,15 ECIMENTO E INSTALAÇÃO.	16,00	und	R\$	31,20	R\$	38,21	R\$	499,20	R\$	611,36		
10.			SERVIÇOS COMPLEMENTARES												
10.1	SINAPI	103307	Instalação de fixação metálica dupla, capacidade de 60 l, em tubo de aço carbono e cestos em chapa de aço com pintura eletrolítica, sobre piso de concreto existente.	4	und	R\$	1.338,66	R\$	1.639,46	R\$	5.354,64	R\$	6.557,84		
10.2	SINAPI	100623	POSTE DE AÇO CONICO CONTINUO CURVO DUPL O, ENGASTADO, H=9M, INCLUSIVE LUMINÁRIAS, SEM LÂMPADAS - FORNECIMENTO E INSTALACAO	14	und		2.659,77	R\$	3.257,42	R\$	37.236,78	R\$	45.603,88		
10.3	ORSE	8814	Fornecimento e plantio de palmeira mini imperial, média	8	und	R\$	88,00	R\$	107,77	R\$	704,00	R\$	862,16		
10.4	ORSE	2397	Fornecimento e plantio de arbustos ornamentais	93	und	R\$	37,12	R\$	45,46	R\$	3.452,16	R\$	4.227,78		
TOTAL:												R\$	452.613,00	R\$	554.317,53

Fernando Matias Mamede
Engenheiro Civil
CREA: 11466382021

Composição	Fonte	Código	Descrição		Tipo	Quantidade	Unidade	Valor	Total
1.2	CPU	1	Limpeza inicial da obra, inclusive retirada de entulho		SERVIÇO		H	R\$ 11,87	R\$ 139,76
COMPOSIÇÃO	SINAPI	6111	SERVENTE					R\$ 94,96	
INSUMO	MERCADO	1	CAÇAMBA 5M3 PARA RETIRADA DE ENTULHO		ALUGUEL	8 0,14	UND	R\$ 320,00	R\$ 44,80

Composição	Fonte	Código	Descrição		Tipo	Quantidade	Unidade	Valor	Total
4.1	CPU	2	ESTRUTURA EM AÇO GALVANIZADO REVESTIDO EM PINTURA ALTOMOTIVA NA COR BRANCO		SERVIÇO	30	H	R\$ 11,56	R\$ 1.777,05
COMPOSIÇÃO	SINAPI	88240	AJUDANTE DE ESTRUTURA METÁLICA COM ENCARGOS COMPLEMENTARES		SERVIÇO	30	H	R\$ 21,10	R\$ 633,00
COMPOSIÇÃO	SINAPI	88317	SOLDADOR COM ENCARGOS COMPLEMENTARES		SERVIÇO	31,2	Kg	R\$ 10,90	R\$ 340,08
INSUMO	SINAPI	11026	CHAPA DE AÇO GALVANIZADA BITOLA GSG 14, E = 1,95 MM (15,60 KG/M2)		MATERIAL	0,8	BARRA	R\$ 105,89	R\$ 84,71
INSUMO	ORSE	9453	Tubo de condução de ferro galvanizado leve c/ costura c/ rosca BSP Ø = 80mm (3"), e = 3,35mm, l = 6000mm NBR 8261 m		MATERIAL	2,00	KG	R\$ 170,32	R\$ 340,64
INSUMO	SINAPI	13388	SOLDA EM BARRA DE ESTANHO-CHUMBO 50/50		SERVIÇO	2	m²	R\$ 7,37	R\$ 14,74
COMPOSIÇÃO	SINAPI	100717	LIXAMENTO MANUAL EM SUPERFÍCIES METÁLICAS EM OBRA		SERVIÇO	2	m²	R\$ 8,54	R\$ 17,08
COMPOSIÇÃO	SINAPI	100735	PINTURA COM TINTA ACRILICA DE ACABAMENTO PULVERIZADA SOBRE SUPERFÍCIES METÁLICAS (EXCETO PERFIL) EXECUTADO EM OBRA (POR DEMÃO).		SERVIÇO	2	m²	R\$ 8,54	R\$ 17,08

Composição	Fonte	Código	Descrição		Tipo	Quantidade	Unidade	Valor	Total
4.2	CPU	3	COBERTA EM AÇO GALVANIZADO REVESTIDO EM PINTURA ALTOMOTIVA NA COR BRANCO E POLICARBONATO NA COR BRONZE		SERVIÇO	30	H	R\$ 11,56	R\$ 346,80
COMPOSIÇÃO	SINAPI	88240	AJUDANTE DE ESTRUTURA METÁLICA COM ENCARGOS COMPLEMENTARES		SERVIÇO	30	H	R\$ 21,10	R\$ 633,00
COMPOSIÇÃO	SINAPI	88317	SOLDADOR COM ENCARGOS COMPLEMENTARES		SERVIÇO	25	BARRA	R\$ 105,89	R\$ 2.647,25
INSUMOS	ORSE	9453	Tubo de condução de ferro galvanizado leve c/ costura c/ rosca BSP Ø = 80mm (3"), e = 3,35mm, l = 6000mm NBR 8261 m		MATERIAL	3,50	KG	R\$ 170,32	R\$ 596,12
INSUMOS	SINAPI	13388	SOLDA EM BARRA DE ESTANHO-CHUMBO 50/50		MATERIAL	86,45	m²	R\$ 320,14	R\$ 27.676,10
INSUMOS	ORSE	9215	Cobertura em policarbonato alveolar de 8mm, fixado em peças de alumínio inclusive		SERVIÇO	480	m²	R\$ 7,37	R\$ 3.537,60
COMPOSIÇÃO	SINAPI	100717	LIXAMENTO MANUAL EM SUPERFÍCIES METÁLICAS EM OBRA		SERVIÇO	480	m²	R\$ 8,54	R\$ 4.099,20
COMPOSIÇÃO	SINAPI	100735	PINTURA COM TINTA ACRILICA DE ACABAMENTO PULVERIZADA SOBRE SUPERFÍCIES METÁLICAS (EXCETO PERFIL) EXECUTADO EM OBRA (POR DEMÃO).		SERVIÇO	480	m²	R\$ 8,54	R\$ 4.099,20

Composição	Fonte	Código	Descrição		Tipo	Quantidade	Unidade	Valor	Total
6.1	CPU	4	PORTICO EM CONCRETO ARMADO E ALVENARIA EMASSADO E PINTADO COM TINTA ACRILICA SEMI BRILHO ACETINADA NA COR VINHEDO (10RR 13 / 250 - CORAL)		MATERIAL	3,07	m³	R\$ 966,39	R\$ 2.936,12
COMPOSIÇÃO	SINAPI	103669	CONCRETO EM PILARES, FCK = 25 MPa, COM USO DE BALDES - LANÇAMENTO, ADENSAMENTO E ACABAMENTO.		MATERIAL	27,77	Kg	R\$ 10,60	R\$ 294,36
COMPOSIÇÃO	SINAPI	89996	ARMAÇÃO VERTICAL DE ALVENARIA ESTRUTURAL, DIÂMETRO DE 10,0 MM.		SERVIÇO	36,7	m²	R\$ 8,69	R\$ 318,92
COMPOSIÇÃO	SINAPI	88489	PINTURA LATEX ACRILICA PREMIUM, APLICAÇÃO MANUAL EM PAREDES, DUAS DEMÃOS		SERVIÇO	36,7	m²	R\$ 8,34	R\$ 306,08
COMPOSIÇÃO	SINAPI	88484	FUNDO SELADOR ACRILICO, APLICAÇÃO MANUAL EM TETO, DUAS DEMÃOS.		SERVIÇO	36,7	m²	R\$ 8,34	R\$ 306,08


Fernando Matias Mamede
 Engenheiro Civil
 CREA: 11466382021

CRONOGRAMA FÍSICO-FINANCEIRO												
Item	Descrição	Valor	MÊS 1	MÊS 2	MÊS 3	MÊS 4	MÊS 5	MÊS 6				
1.	SERVIÇOS INICIAIS	% R\$ 24.285,63	100,00% R\$ 24.285,63									
2.	PAREDES	% R\$ 109.116,07	33,33% R\$ 36.372,02	33,33% R\$ 36.372,02	33,33% R\$ 36.372,02							
3.	PISO	% R\$ 122.055,17			50,00% R\$ 61.027,59	50,00% R\$ 61.027,59						
4.	COBERTA	% R\$ 70.837,08				50,00% R\$ 35.418,54	50,00% R\$ 35.418,54					
5.	BANCOS	% R\$ 92.889,67		100,00% R\$ 92.889,67								
6.	PORTICO	% R\$ 7.912,74					100,00% R\$ 7.912,74					
7.	ESQUADRIAS	% R\$ 50.807,04						100,00% R\$ 50.807,04				
8.	HIDRAULICO	% R\$ 18.551,11			50,00% R\$ 9.275,56	50,00% R\$ 9.275,56						
9.	ELETRICO	% R\$ 611,36							100,00% R\$ 611,36			
10.	SERVIÇOS COMPLEMENTARES	% R\$ 57.251,66								100,00% R\$ 57.251,66		
Total			R\$ 60.657,65	R\$ 190.289,28	R\$ 142.093,71	R\$ 44.694,10	R\$ 7.912,74	R\$ 108.670,06				
Total Acumulado		R\$ 554.317,53	R\$ 60.657,65	R\$ 250.946,93	R\$ 393.040,64	R\$ 437.734,74	R\$ 445.647,48	R\$ 554.317,54				
Percentual Mensal			10,94%	34,33%	25,63%	8,06%	1,43%	19,60%				
Percentual Acumulado			10,94%	45,27%	70,90%	78,96%	80,39%	100,0%				


 Fernando Matias Mamede
 Engenheiro Civil
 CREA: 11466382021

CÁLCULO DE BDI																							
Construção e Reforma de quaisquer Edificações inclusive Unidades Habitacionais, Escolas, Hospitais, de uso Agropecuário, Estações p/Trens/Metrô, Estádios e Quadras Esportivas Instalações				Construção de Rodovias, Ferrovias, Pistas de Aeroportos, Pontes, Viadutos, Metrô, Túneis, Barreiras Acústicas, Praças de Pedágio, Sinalização de Rodovias e Aeroportos, Placas de Sinalização de Tráfego e Semelhantes, Infra Viária Urbana, Estacionamento de Veículos, Praças, Calçadas p/Pedestres, Elevados, Passarelas, Ciclovias e VLT				Abastecimento de Água, Coleta de Esgoto				Fornecimento de materiais e equipamentos				Construção e Manutenção de Estações e Redes de Distribuição de Energia Elétrica				Portuárias, Marítimas e Fluviais			
Item componente do BDI		% Informado		1º Q	Médio	3º Q	1º Q	Médio	3º Q	1º Q	Médio	3º Q	1º Q	Médio	3º Q	1º Q	Médio	3º Q	1º Q	Médio	3º Q		
Administração Central (AC)		3,00		3,00	4,00	5,50	3,80	4,01	4,67	3,43	4,93	6,71	1,50	3,45	4,49	5,29	5,92	7,93	4,00	5,52	7,85		
Seguro (S) e Garantia (G)		0,80		0,80	0,80	1,00	0,32	0,40	0,74	0,28	0,49	0,75	0,30	0,48	0,82	0,25	0,51	0,56	0,81	1,22	1,99		
Risco (R)		0,97		0,97	1,27	1,27	0,50	0,56	0,97	1,00	1,39	1,74	0,56	0,85	0,89	1,00	1,48	1,97	1,46	2,32	3,16		
Despesas Financeiras (DF)		0,59		0,59	1,23	1,39	1,02	1,11	1,21	0,94	0,99	1,17	0,85	0,85	1,11	1,01	1,07	1,11	0,94	1,02	1,33		
Lucro (L)		6,16		6,16	7,40	8,96	6,64	7,30	8,69	6,74	8,04	9,40	3,50	5,11	6,22	8,00	8,31	9,51	7,14	8,40	10,43		
Impostos (I) - PIS, COFINS, ISSQN				Conforme Legislação Específica																			

Observações

1) Preencher apenas a coluna % Informado (Coluna B)

2) Os Tributos normalmente aplicáveis são: PIS (0,65%), COFINS (3,00%) e ISS (0,5%) e CPRB (4,5%)

3) O cálculo do BDI se baseia na fórmula abaixo utilizada pelo Acórdão 2622/13 do TCU, conforme CE GEPAD 354/2013 de 17/10/2013.


B.D.I = 22,47%

Fórmula Utilizada:

$$BDI = \left[\frac{(1 + AC + G + R) * (1 + DF) * (1 + L)}{1 - I} - 1 \right] * 100$$


VALORES DE BDI POR TIPO DE OBRA			
Tipo de Obra		1º Q	3º Q
Construção de Edifícios		20,34	25,00
Construção de Rodovias e Ferrovias		19,60	24,23
Rede de Abastecimento de Água, Coleta de Esgotos		20,76	26,44
Estações e Redes de Distribuição de Energia Elétrica		24,00	27,86
Obras Portuárias, Marítimas e Fluviais		22,80	30,95
Fornecimento de Materiais e Equipamentos		11,10	16,80


Fernando Matias Mamede
Engenheiro Civil
CREA: 11466382021

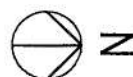


ELDER ■ ARAQUITETO ■ (83) 99999-3464

Comprovação da Aprovação do Projeto Básico. Doc. 111214/23. Data: 06/11/2023 11:07. Responsável: Irani A. da Silva.
Impresso por convidado em 25/02/2026 11:15. Validação: 690B.5F61.33AC.E923.BF3C.0185.1B1E.CE6F.

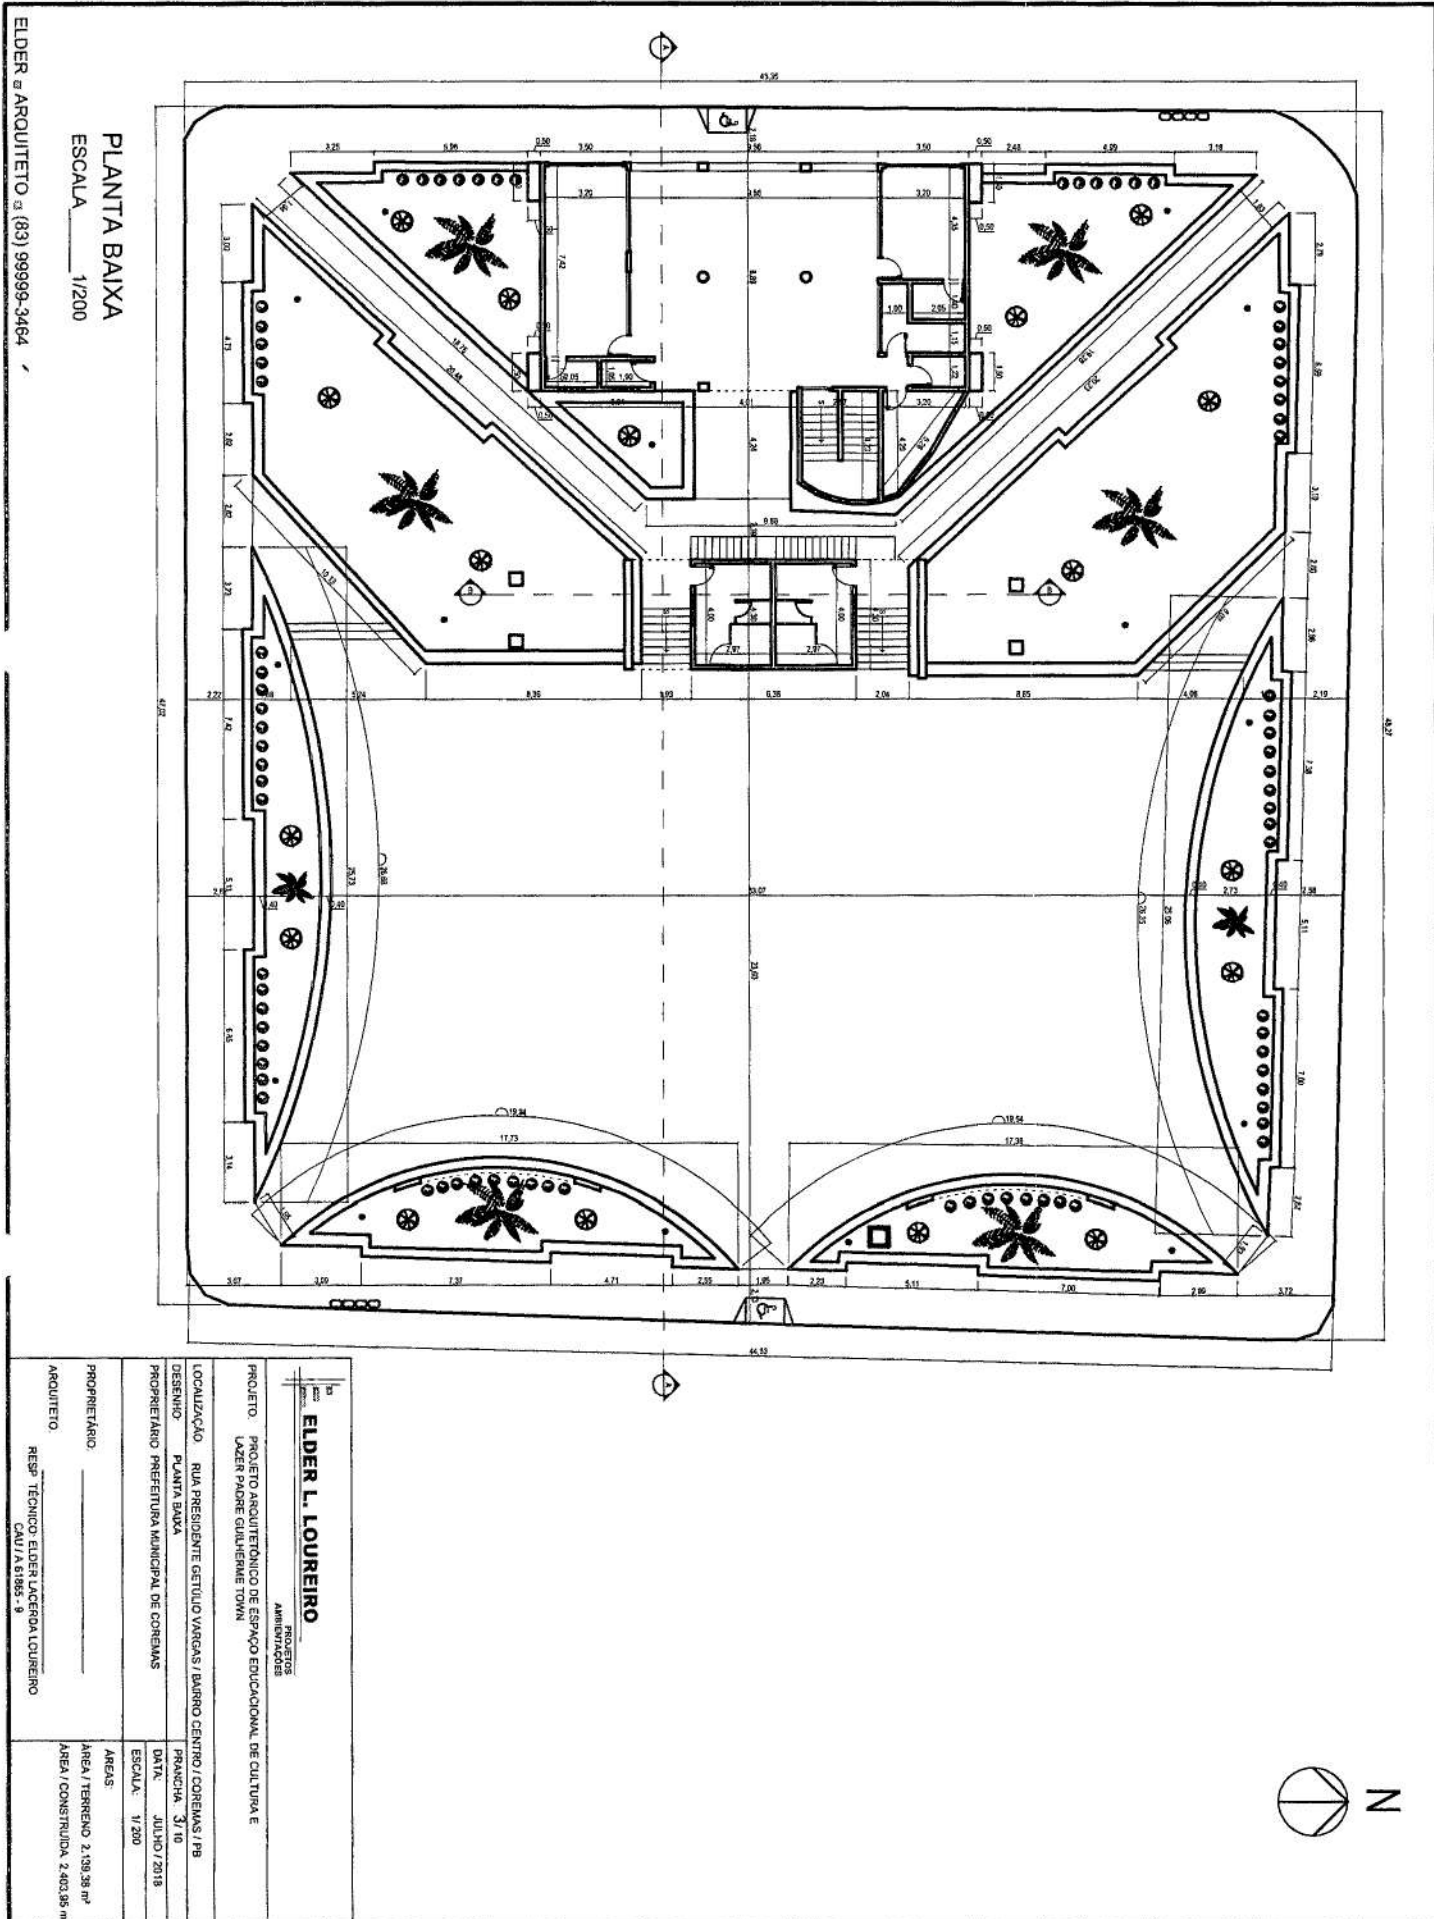

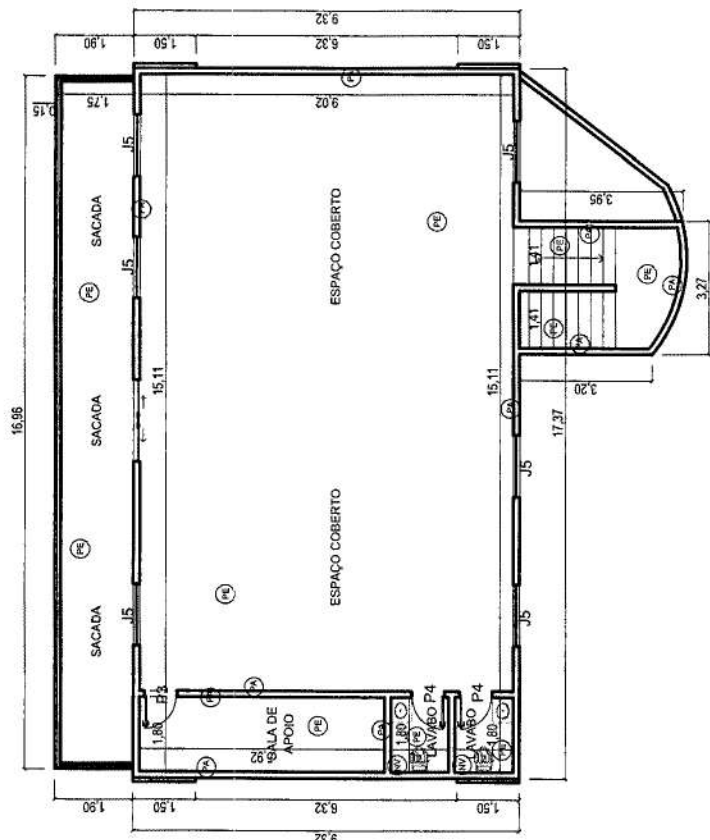


PLANTA BAIXA_LAYOUT_1º PAVIMENTO
ESCALA 1/125

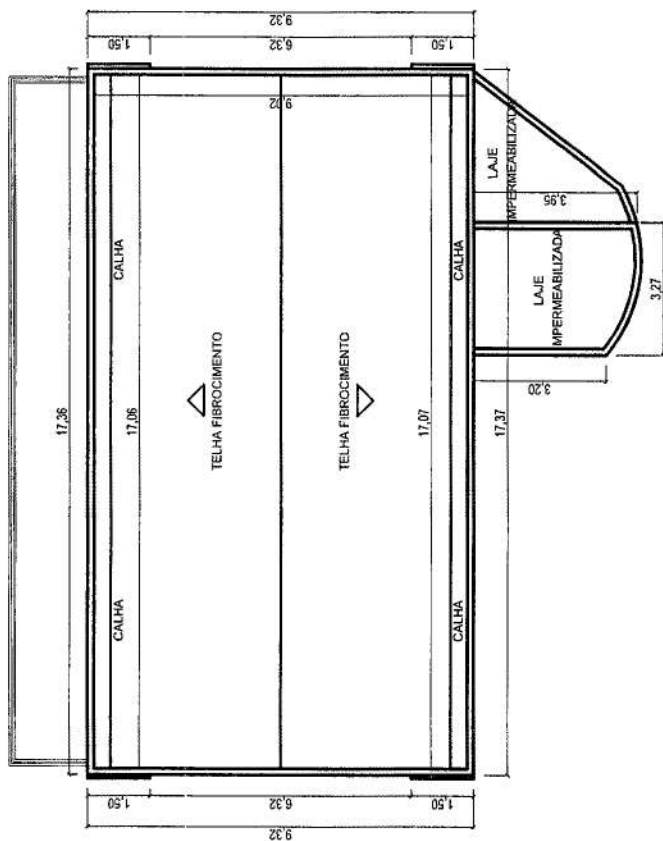


PLANTA DE COBERTA
ESCALA 1/125

 ELDER L. LOUREIRO PROFESSOR PROFESSOR	PROJETO ARQUITETÔNICO DE ESPAÇO EDUCACIONAL DE CULTURA E LAZER PAVILHÃO DE LAZER PAVILHÃO DE LAZER PROFESSOR PROFESSOR	PROJETO PROJETO ARQUITETÔNICO DE ESPAÇO EDUCACIONAL DE CULTURA E LAZER PAVILHÃO DE LAZER PAVILHÃO DE LAZER	LOCALIZAÇÃO RUA PRESIDENTE GETULIO VARGAS / BAIRRO CENTRO / COREMAS / PB PRANCHETA: 8/ 10 PRANCHETA: 8/ 10	DESENHO PLANTA BAIKA _ PLANTA DE COBERTA PROPRIETÁRIO PROPRIETÁRIO	DATA: JULHO / 2018 ESCALA: 1/ 125 ESCALA: 1/ 125	ÁREAS: ÁREA / TERRENO 2.139,36 m² ÁREA / CONSTRUÍDA 2.403,96 m² RESP. TÉCNICO: ELDER LACERDA LOUREIRO CAVALARIAS, 8 CAVALARIAS, 8
---	---	---	---	---	---	--

ELEVAÇÃO FRONTAL
ESCALA 1/200

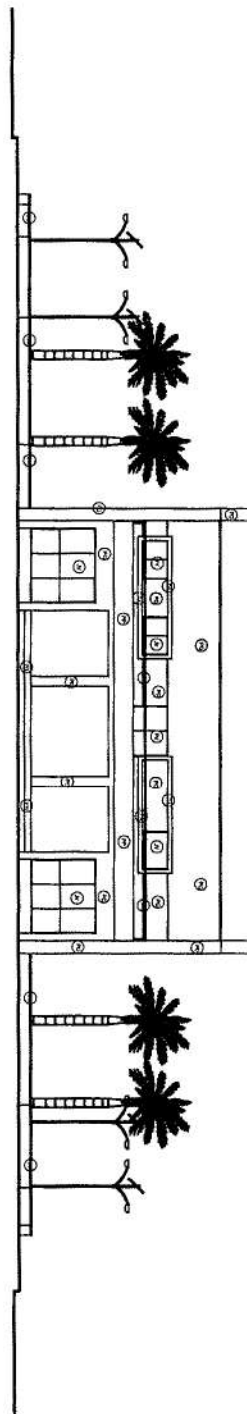




ELEVAÇÃO FRONTAL
ESCALA 1/200

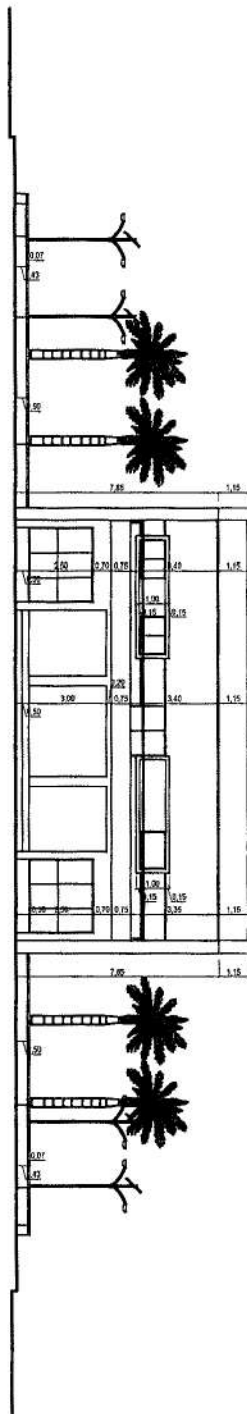


ELDER L. LOUREIRO
ARQUITETO (83) 99989-3464


ELDER L. LOUREIRO	
PROJETO	PROJETO ARQUITETÔNICO DE ESPAÇO EDUCACIONAL DE CULTURA E LAZER PADRE CILHNERNE TOWN
LOCALIZAÇÃO	RUA PRESIDENTE GETÚLIO VARGAS / BAIRRO CENTRO / COREMAS / PB
DESENHO	EL. ELEV. 4/10
PROPRIETÁRIO	PREFEITURA MUNICIPAL DE COREMAS
PROPRIETÁRIO	ÁREAS: 1/200
PROPRIETÁRIO	ÁREA / TERRENO 2.139,38 m²
PROPRIETÁRIO	ÁREA / CONSTRUÍDA 2.403,95 m²
PROPRIETÁRIO	RESP. TÉCNICO: ELDER LACERDA LOUREIRO
PROPRIETÁRIO	CAU / A. 81865 - 9

ELDER L. LOUREIRO A (83) 99989-3464

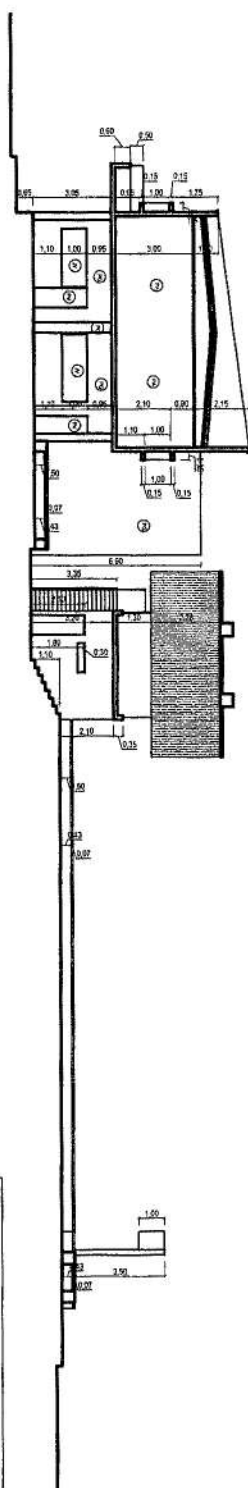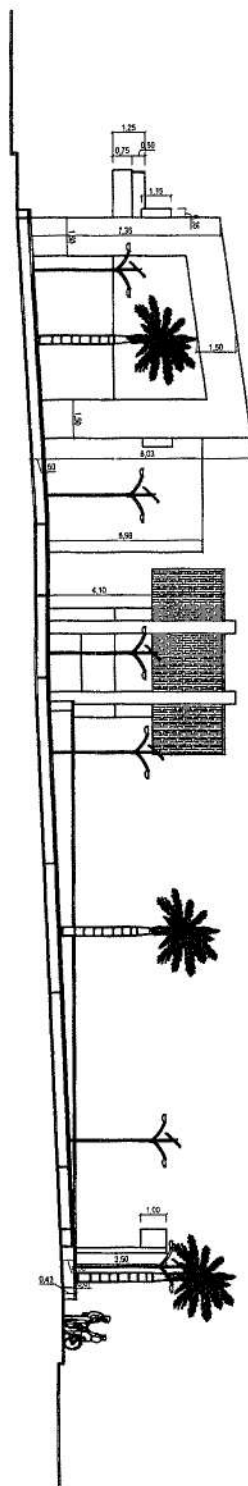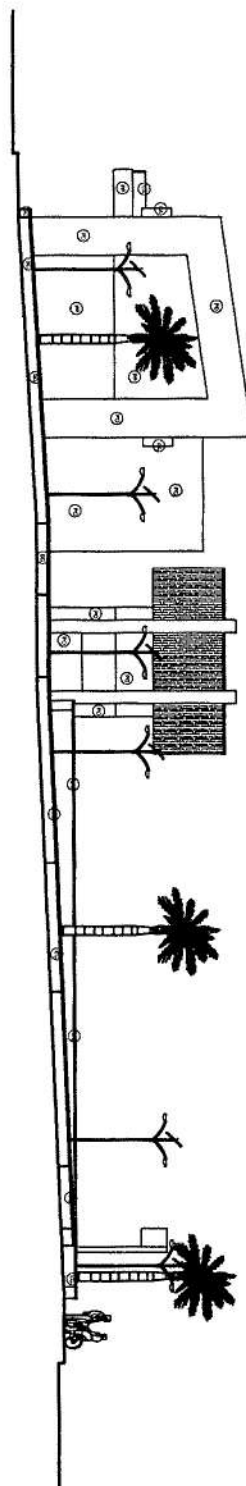
CORTE - AA
ESCALA 1/200ELEVACÃO LATERAL
ESCALA 1/200ELEVACÃO LATERAL
ESCALA 1/200

ELDER L. LOUREIRO PROJETOS ARQUITETURAIS	
PROJETO: PROJETO ARQUITETÔNICO DE ESPAÇO EDUCACIONAL DE CULTURA E LAZER PADRE GUILHERME TOWN	
LOCALIZAÇÃO	RUA PRESIDENTE GETÚLIO VARGAS / BAIRRO CENTRO / COREMAS / PB
DESENHO	ELEVACÃO - CORTE
PROPRIETÁRIO	PREFEITURA MUNICIPAL DE COREMAS
DATA	JULHO / 2018
ESCALA	V 200
PROPRIETÁRIO	
ARQUITETO	RESP. TÉCNICO ELDER LACERDA LOUREIRO CAU / A 81865 - 8
ÁREAS:	ÁREA / TERRENO 2.139,28 m² ÁREA / CONSTRUÍDA 2.403,95 m²

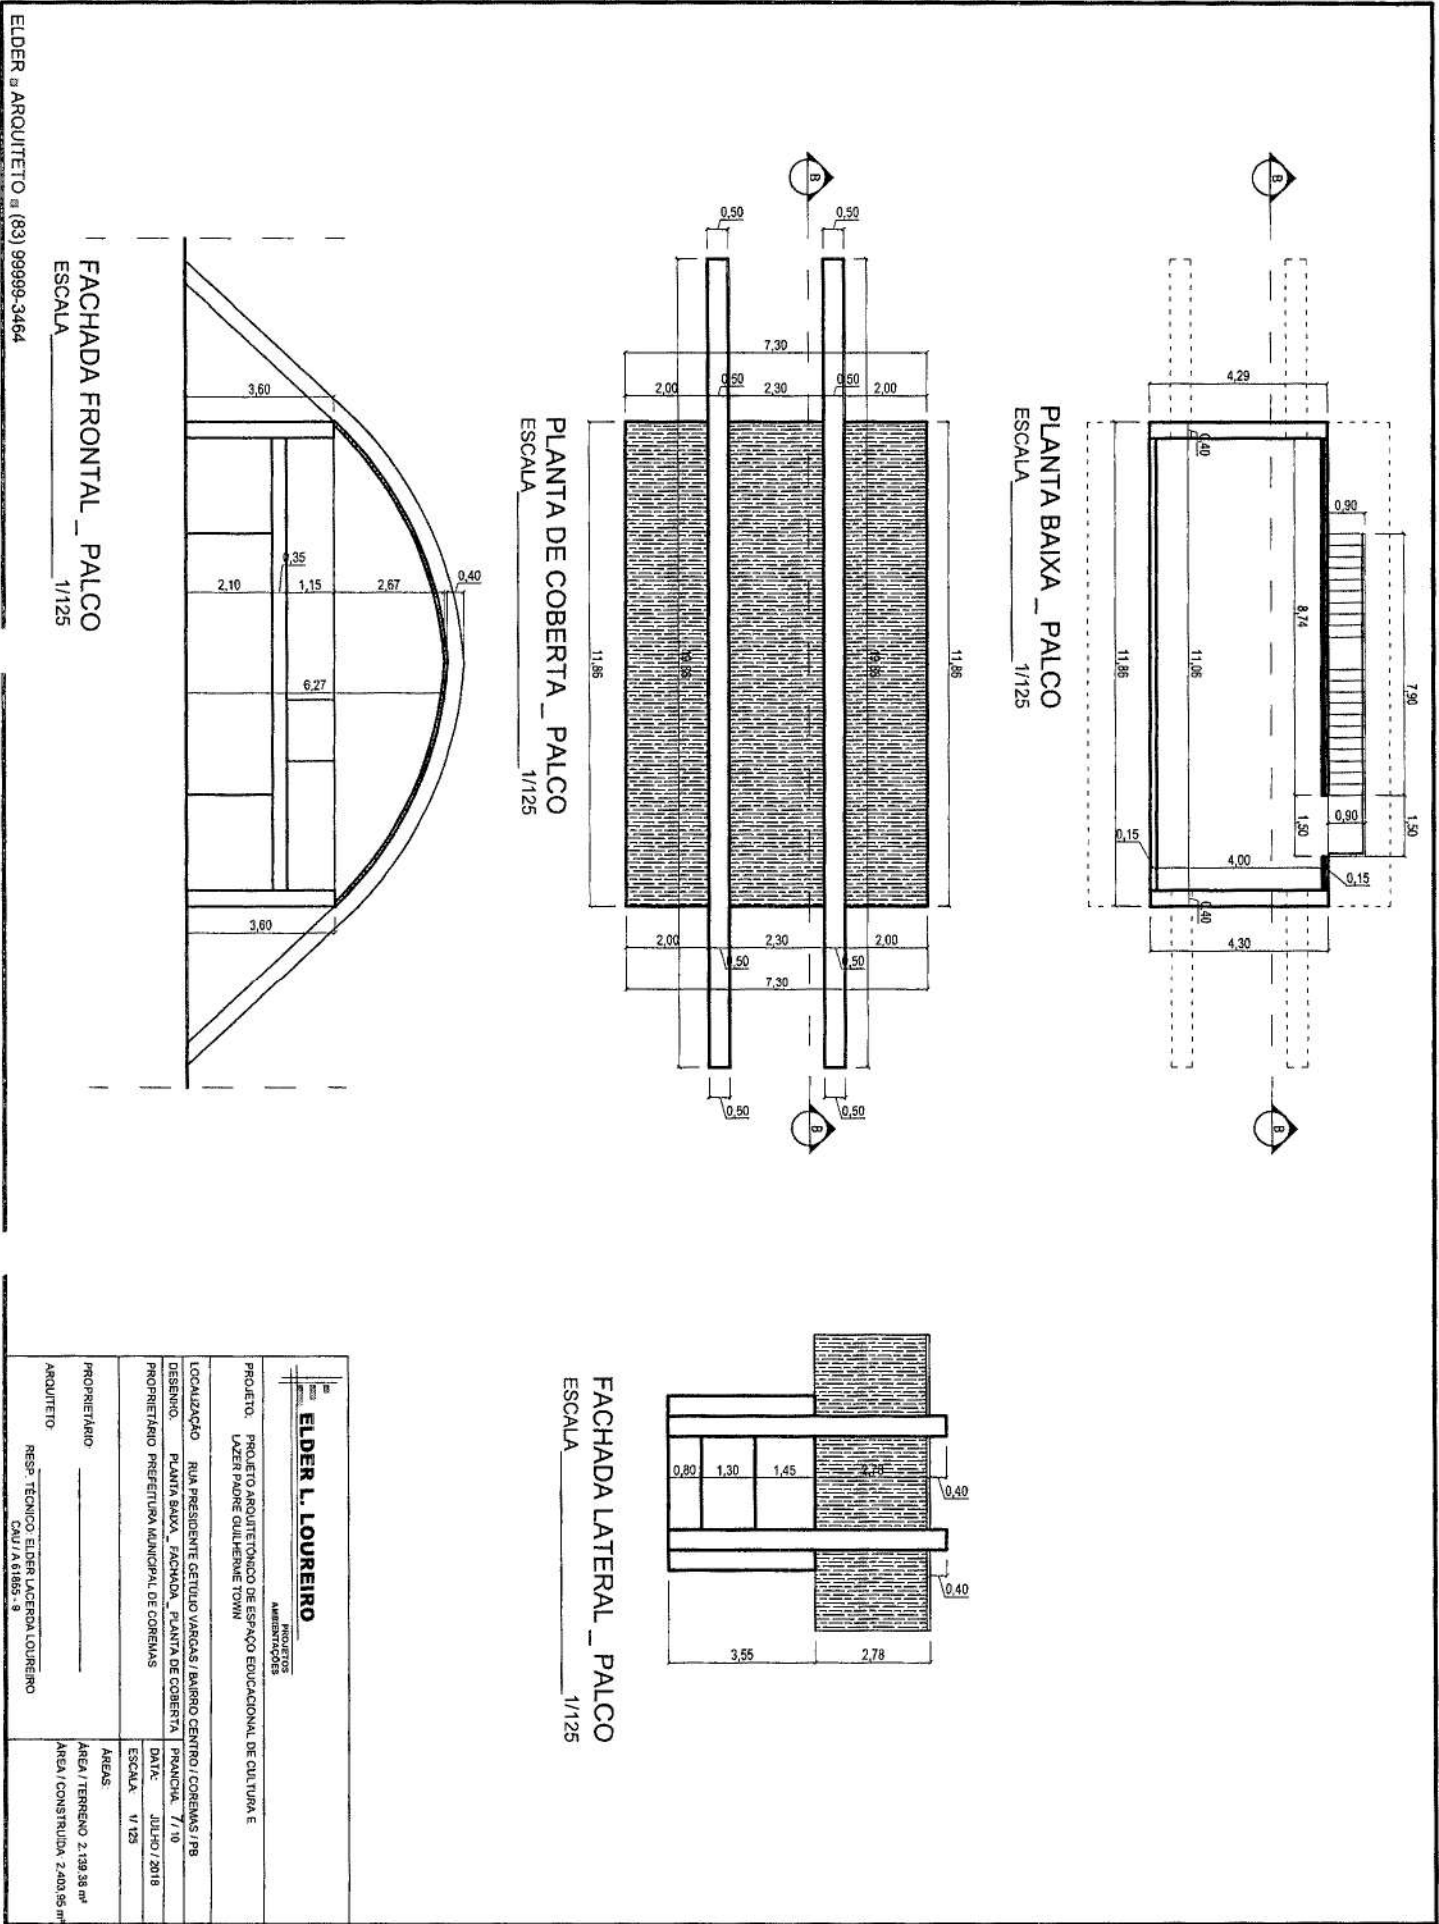


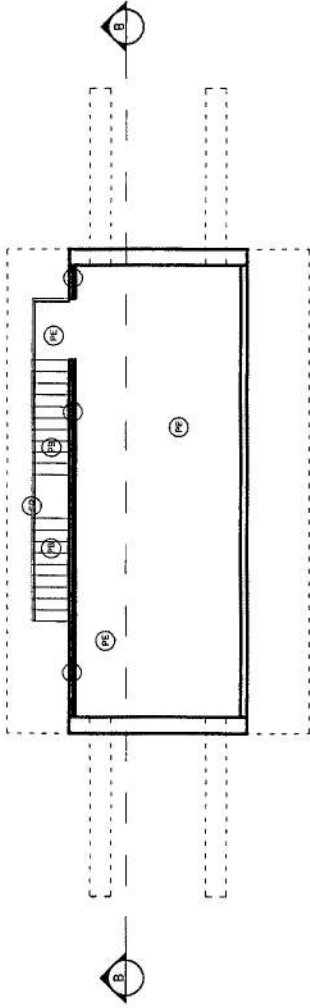


PLANTA BAIXA _ PALCO
ESCALA 1/125

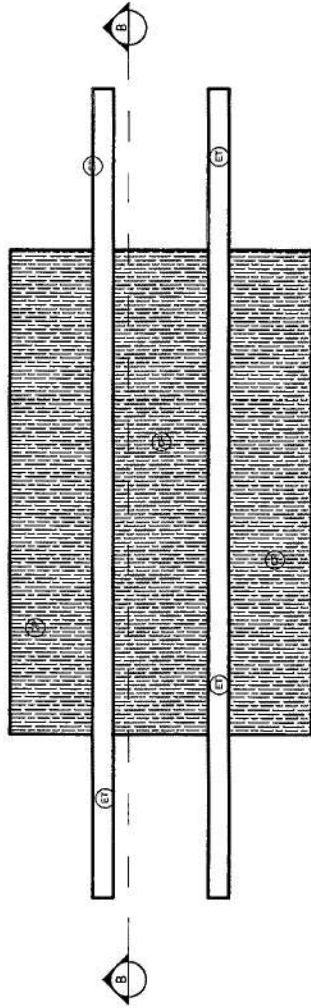

PLANTA DE COBERTA _ PALCO
ESCALA 1/125

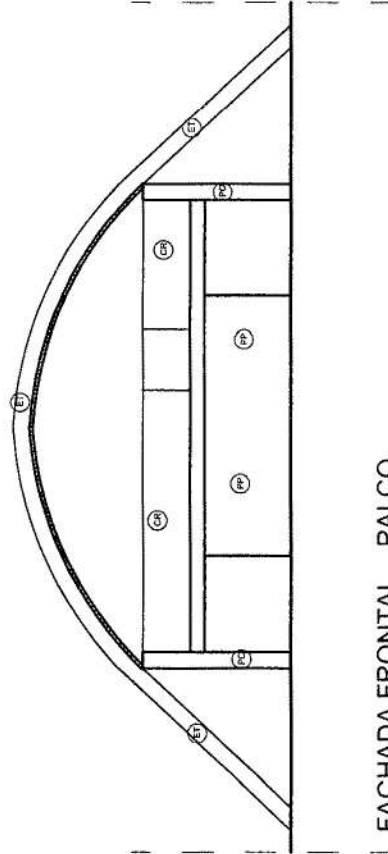

FACHADA FRONTAL _ PALCO
ESCALA 1/125

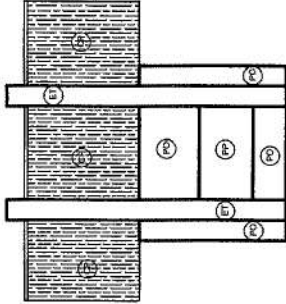


FACHADA LATERAL _ PALCO
ESCALA 1/125

ELDER L. LOUREIRO PROJETOS ARQUITETURA	
PROJETO: PROJETO ARQUITETÔNICO DE ESPAÇO EDUCACIONAL DE CULTURA E LAZER PADRE GUILHERME TOWN	
LOCALIZAÇÃO: RUA PRESIDENTE GETÚLIO VARGAS / BAIRRO CENTRO / COREMAS / PB	PRANCHAS: 01/10
DESENHO: PLANTA BAIXA, FACHADA, PLANTA DE COBERTA	DATA: JULHO / 2018
PROPRIETÁRIO: PREFEITURA MUNICIPAL DE COREMAS	ESCALA: 1/125
PROPRIETÁRIO: _____	ÁREAS: _____
ARQUITETO: _____	ÁREA / TERRENO: 2.139,38 m²
RESP. TÉCNICO: ELDER LACERDA LOUREIRO	ÁREA / CONSTRUÍDA: 2.403,95 m²
CAU / A 01865 - 9	

ESPECIFICAÇÕES PISOS, REVESTIMENTOS E MATERIAIS	
01	PARADE EM ALVENARIA EMASSADA E PINTADA NA COR BRANCO GELO
02	PARADE EM ALVENARIA EMASSADA E PINTADA NA COR AREIA
03	COBERTA EM AÇO GALVANIZADO REVESTIDO EM PINTURA ALUMOTIVA NA COR BRANCO E POLICARBONATO NA COR BRONZE
04	ESTRUTURA EM AÇO GALVANIZADO REVESTIDO EM PINTURA ALUMOTIVA NA COR BRANCO
05	PARADE REVESTIDA EM PASTILHA MATONE ARANCO 5 X 10 CM (MARCA ELIZABETH)
06	PORTA EM VIDRO TEMPERADO 10 MM REFLETIVO / MOLDURA EM ALUMINIO BRANCO
07	JANELA EM VIDRO TEMPERADO 8 MM REFLETIVO / MOLDURA EM ALUMINIO BRANCO
08	PARADE REVESTIDA EM PORCELANATO NEVADA ACETINADO 32 X 66 CM (MARCA ELIZABETH)
09	PARADE REVESTIDA EM PASTILHA CRISTAL BRANCO 5 X 10 CM (MARCA ELIZABETH)
10	PISO REVESTIDO EM PORCELANATO RETIFICADO ELIZABETH (72 X 72 CM) BRANCO NATURAL ESCOVADO
11	PISO INTERTRAVADO NA COR CINZA (10 X 20 X 06 CM)
12	PISO INTERTRAVADO NA COR VERMELHO (10 X 20 X 06 CM)
13	COBERTA EM TELHA FIBROCIMENTO 06 MM
14	BANCO EM ALVENARIA REVESTIDO EM PORCELANATO ESMALTADO HD ANTIQUE WOOD AMBER 25 X 101 CM (MARCA ELIZABETH) E GRANITO BRANCO CRISTAL
15	PISO REVESTIDO EM GRANITO BRANCO CRISTAL COM FISSURAS ANTERDERRAPANTE
16	VIDRO TEMPERADO 8MM REFLETIVO BRONZE E CORRIMÃO SEÇÃO QUADRA 50 MM EM INOX
17	VEGETAÇÃO (PALMEIRA IMPERIAL)
18	VEGETAÇÃO DE PEQUENO PORTE
19	GRAMA
20	POSTE EM AÇO GALVANIZADO COM LUMINARIAS EM LED SCHREDER MODELO ALBANY, COMPLETA COM LÂMPADA VSAP 250 W
21	LIXEIRA ECOLÓGICA COM 4 UNIDADES EM POLETILENO
22	PORTICO EM CONCRETO ARMADO E ALVENARIA EMASSADO E PINTADO COM TINTA ACRILICA SEMI BRILHO ACETINADA NA COR VINHEDO (10RR 13 / 250 - CORAL)
23	LIXEIRA ECOLÓGICA COM 4 UNIDADES EM POLETILENO
24	MONUMENTO EM ALVENARIA REVESTIDO EM GRANITO BRANCO CRISTAL

ESQUADRIAS / JANELAS			
TIPO	ALT.	LARG.	ESPECIF.
J1	2.50	2.90	- Fixa
J2	1.00	3.35	1.10 Correr
J3	1.00	2.70	1.10 Correr
J4	0.30	1.45	2.20 Basculante
J5	1.00	1.50	1.10 Correr
ESQUADRIAS / PORTAS			
TIPO	ALT.	LARG.	ESPECIF.
P1	2.50	1.45	- Correr
P2	2.10	3.00	Correr
P3	2.10	0.80	Pivoltante
P4	2.10	0.80	Pivoltante
P5	2.10	1.20	Pivoltante
P6	2.10	2.00	Correr

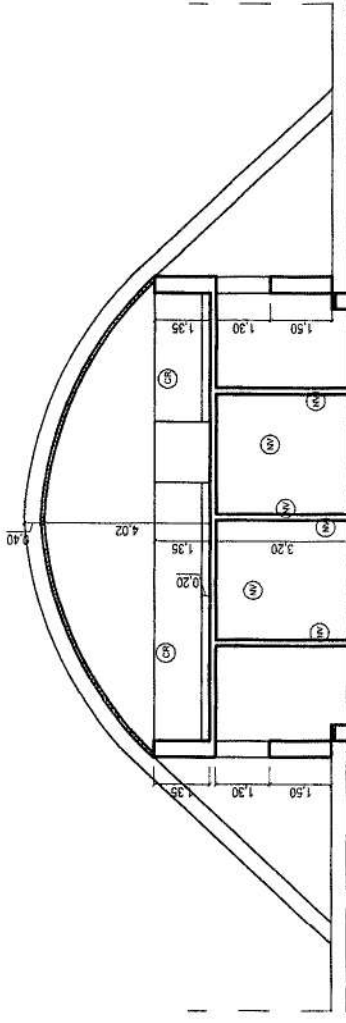

CORTE_BB
ESCALA 1/125

ELDER L. LOUREIRO

PROJETOS
ARQUITETONICOS

PROJETO: PROJETO ARQUITETONICO DE ESPAÇO EDUCACIONAL DE CULTURA E LAZER PAIPE GUILHERME TOWN

LOCALIZAÇÃO: RUA PRESIDENTE GETULIO VARGAS / BAIRRO CENTRO / COREMAS / PB

DESENHO: CORTE

PRONETÁRIO: PREFEITURA MUNICIPAL DE COREMAS

DATA: JULHO / 2018

ESCALA: 1/125

ÁREAS:
ÁREA / TERRENO 2.139,38 m²
ÁREA / CONSTRUÍDA: 2.403,95 m²

PROPRIETÁRIO: _____

ARQUITETO: _____

RESP. TÉCNICO: ELDER LACERDA LOUREIRO
CAU / A 61885 - 9

