


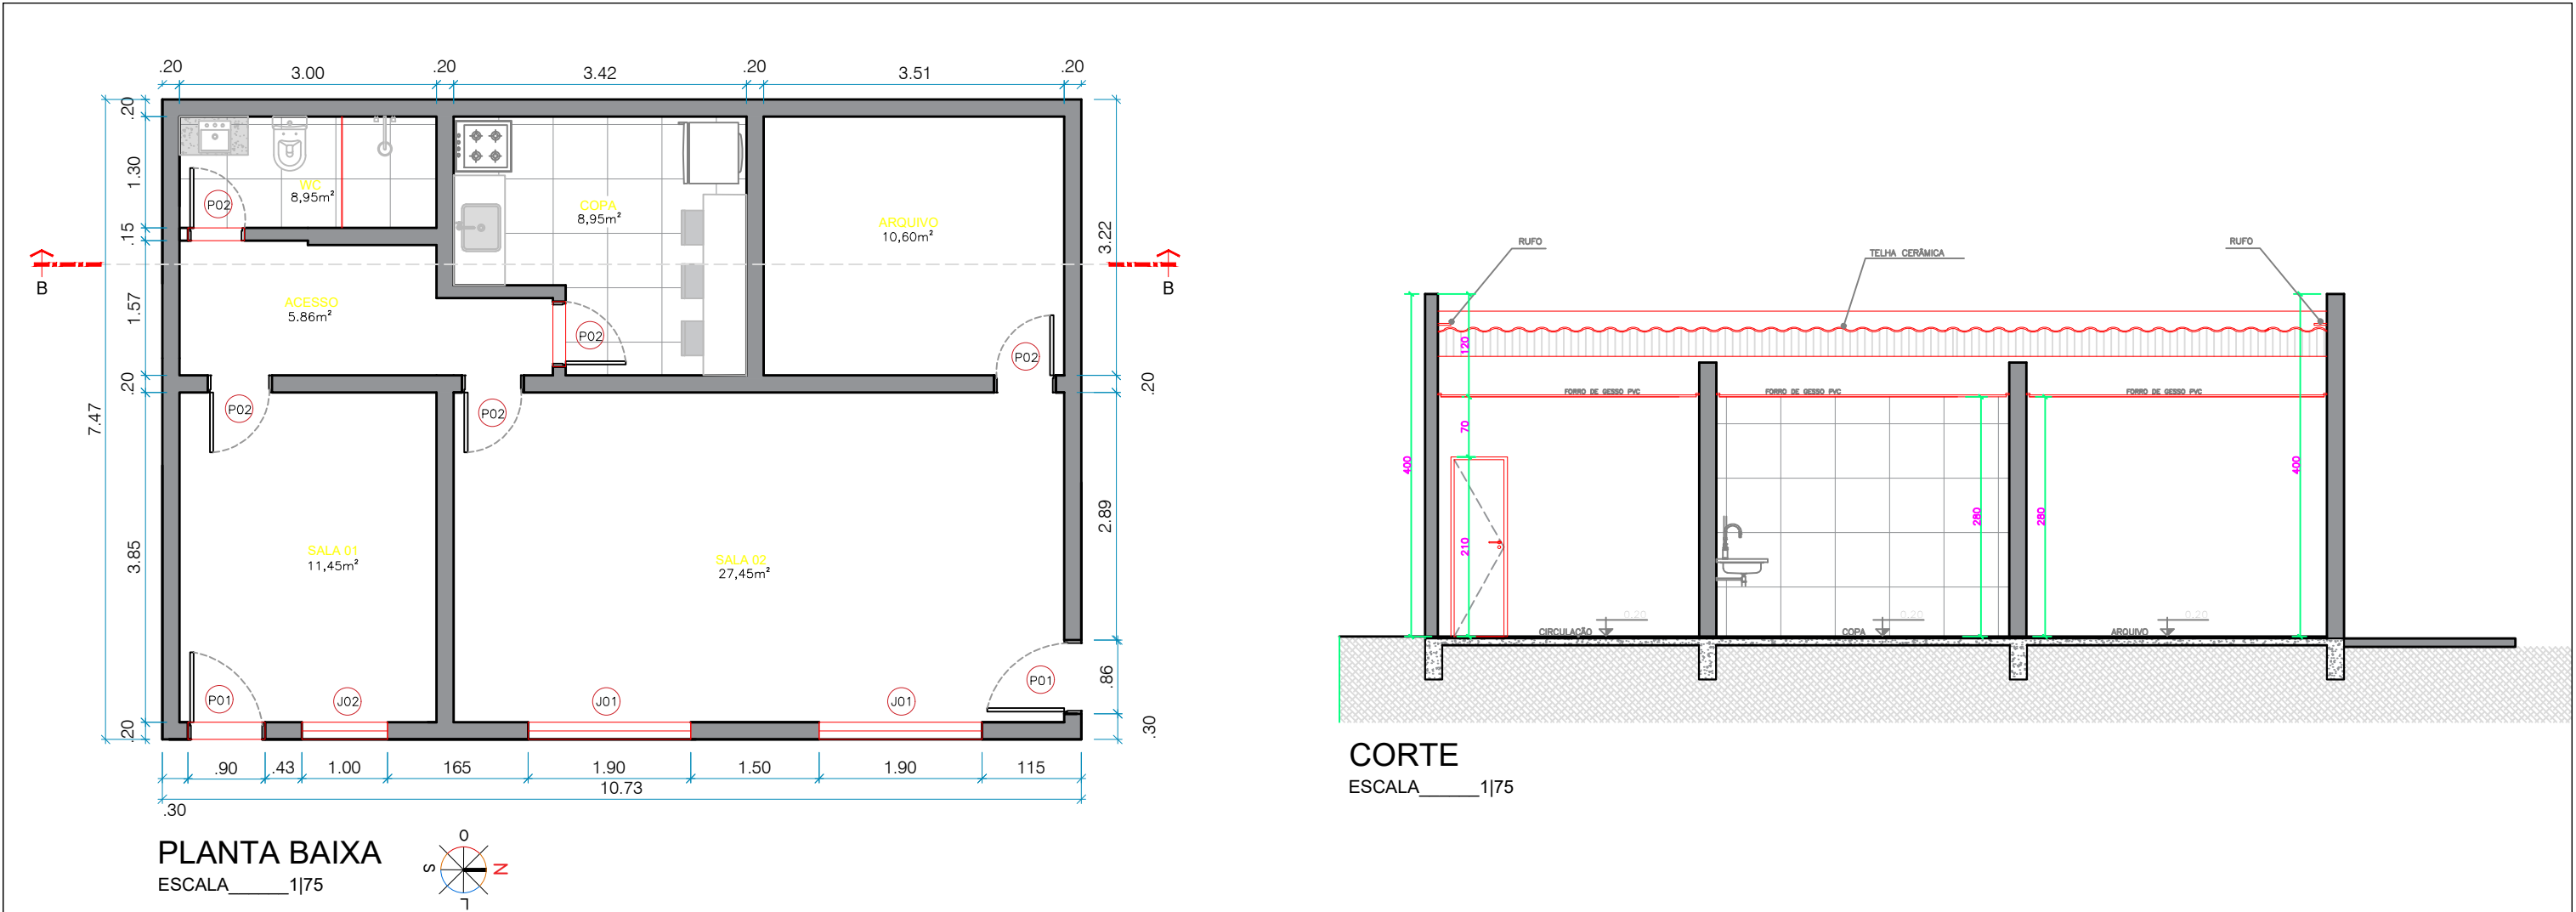

ACABAMENTOS - ESCRITÓRIO			
REVESTIMENTO	Especificação	LOCAL	ÁREA
Cemâmico	Piso Cerâmico Marmorizado Brilhante Borda Reta Interno 54x54cm Phanteon Lef	PISO GERAL	73,03m²
	Cobertura de parede 280cm com Cerâmico Marmorizado Brilhante Borda Reta Interno 54x54cm Phanteon Lef	COPA, WC	60,15m²
Pintura	Parede pintada e emassada com tinta para ambientes externos com acabamento fosco na cor branca	FACHADA NORTE, LESTE E SUL	105m²
	Parede pintada e emassada com Tinta Látex Coralar + Econômico Sem Cheiro 18 L Branco Gelo	ACESSO, SALA 01, 02 E ARQUIVO	135m²
	Fechamento com forro em reguas de pvc, frisado para ambientes comerciais	GESSO GERAL	73,03m²

ACABAMENTOS - ESCRITÓRIO			
ESQUADRIA	Especificação	LOCAL	QTE
PORTA	Porta de Madeira Lisa Nevada MGM 210cmx90cm Melamínico Mogno	SALA 01 E SALA 02	02
	Porta de Madeira Lisa Nevada MGM 210cmx70cm Melamínico Mogno	SALA 02, ARQUIVO COPA E WC	05
JANELA	Restauração das janelas existentes 190x110cm e 100x110cm com lixamento e nova pintura na cor cinza sem brilho	SALA 01 E 02	03