
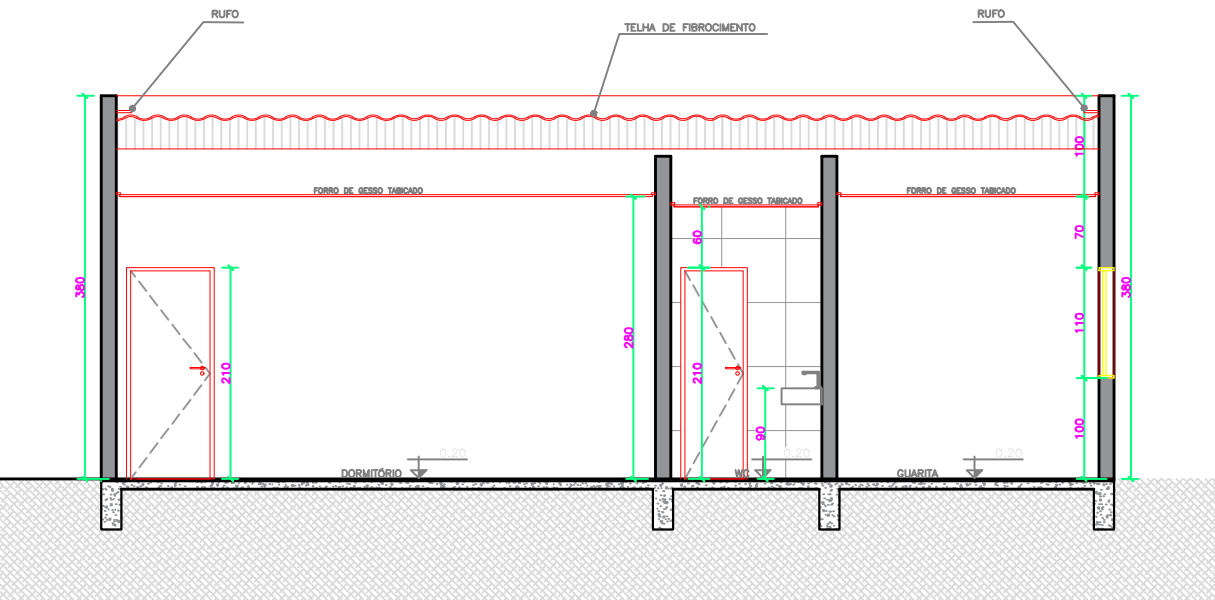


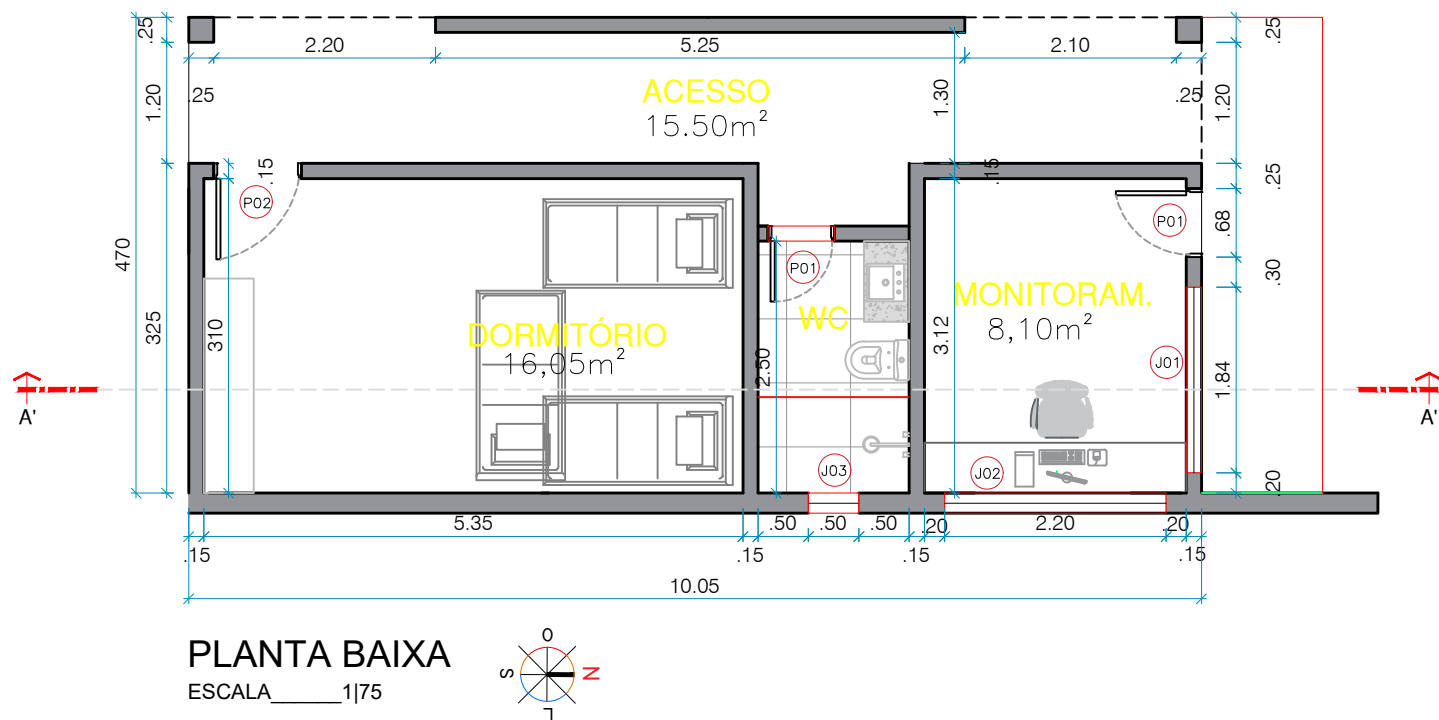

ACABAMENTOS - GUARITA			
REVESTIMENTO	Especificação	LOCAL	ÁREA
Cemâmico	Piso Cerâmico Marmorizado Brilhante Borda Reta Interno 54x54cm Phanteon Lef	PISO GERAL	47.44m²
	Cobertura de parede 280cm com Cerâmico Marmorizado Brilhante Borda Reta Interno 54x54cm Phanteon Lef	BANHEIRO	23m²
Pintura	Parede pintada e emassada com tinta para ambientes externos com acabamento fosco na cor branca	FACHADA NORTE, SUL E OESTE	115m²
	Parede pintada e emassada com Tinta Látex Coralar + Econômico Sem Cheiro 18 L Branco Gelo	ACESSO, SALA 01, 02 E ARQUIVO	112m²
	Fechamento com forro em reguas de pvc, frisado para ambientes comerciais	GESSO GERAL	46m²

ACABAMENTOS - GUARITA			
ESQUADRIA	Especificação	LOCAL	QTE
PORTA	Porta de Madeira Lisa Nevada MGM 210cmx70cm Melamínico Mogno	MONITORAMENTO BANHEIRO	02
	Porta de Madeira Lisa Nevada MGM 210cmx70cm Melamínico Mogno	DORMITÓRIO	01
JANELA	J01 - Janela de aluminio com vidro 185 x 110cm J02 - Janela de aluminio com vidro fumê 220 x 110cm J03 - Janela basculante horizontal de vidro 50 x 40cm	SALA 01 E 02 BANHEIRO	03