

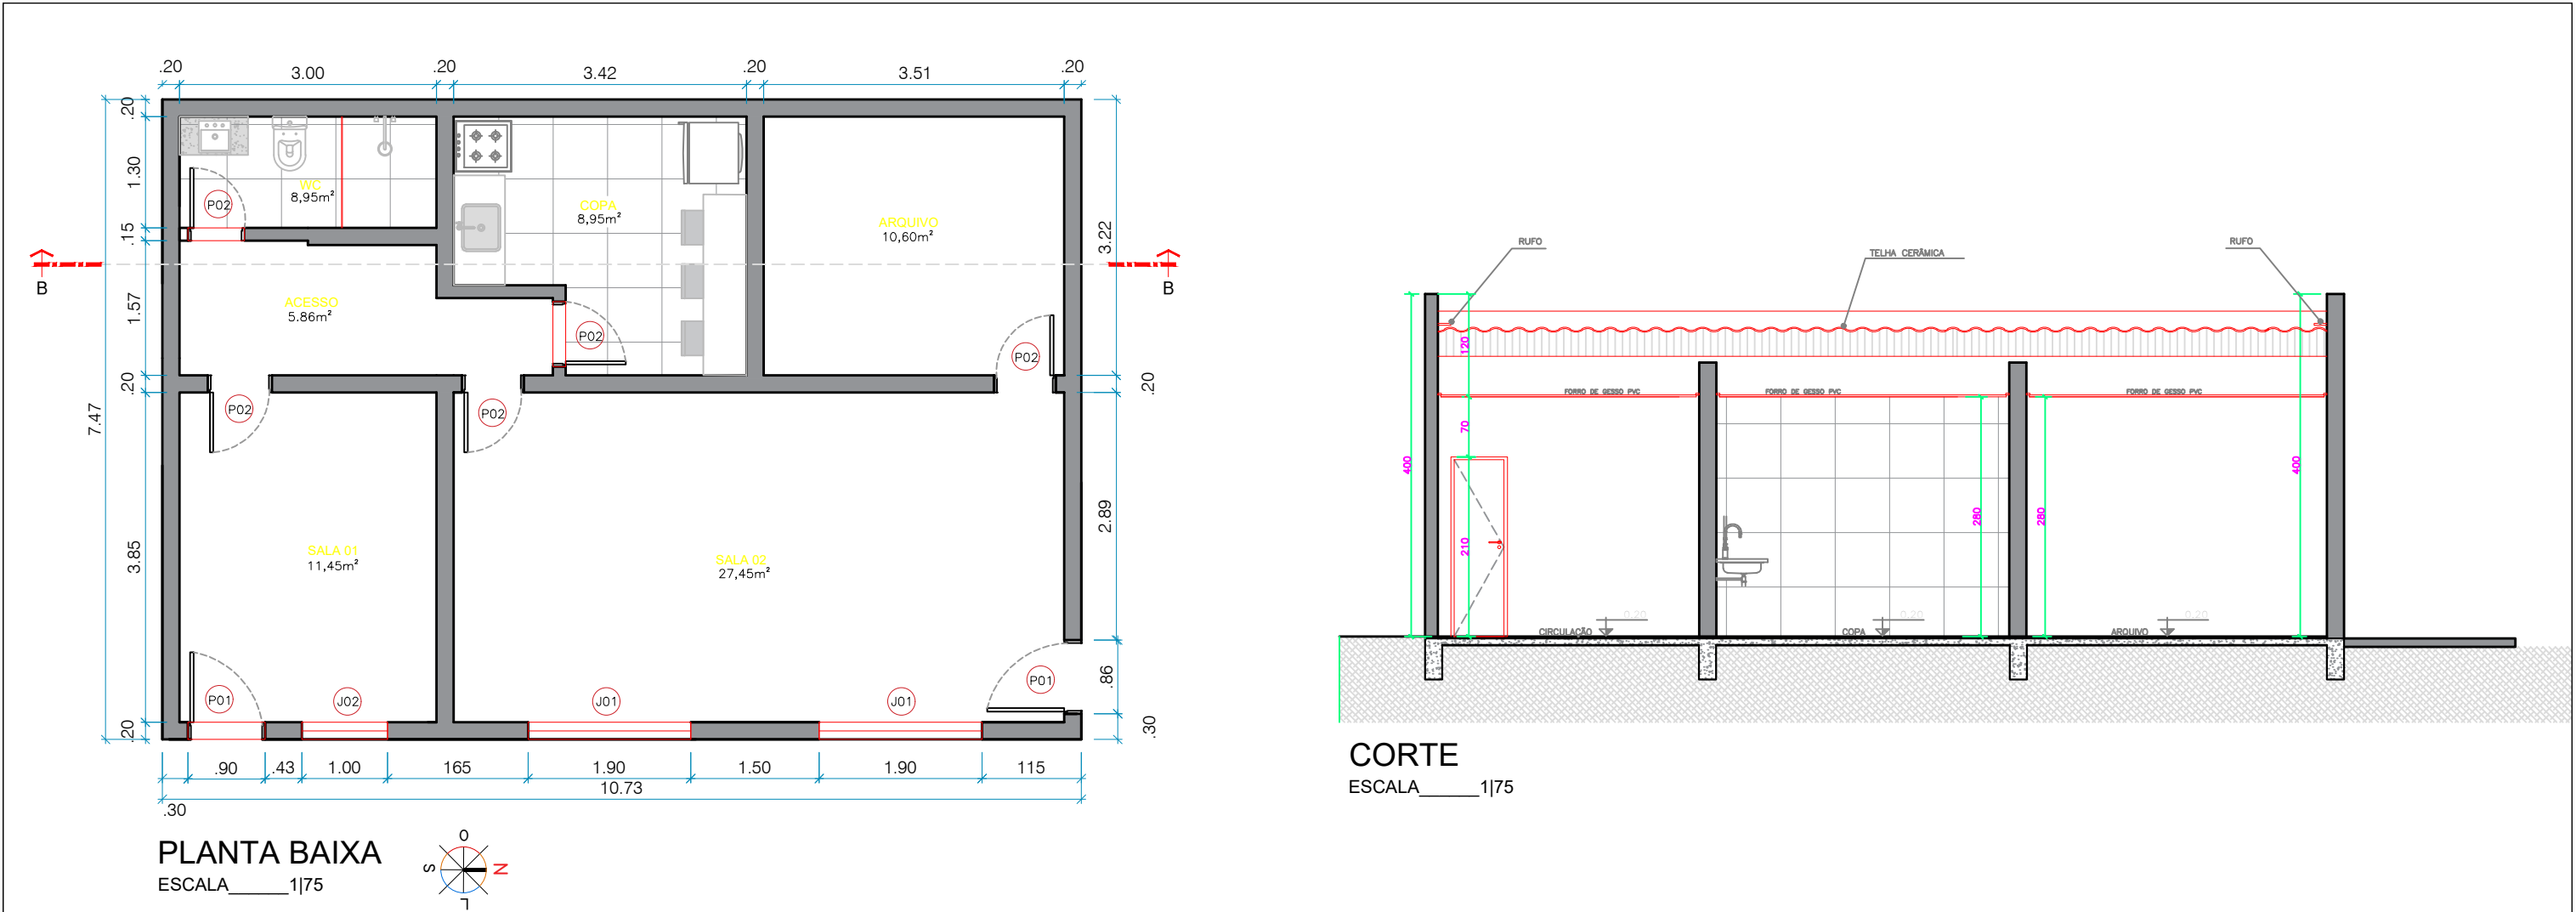


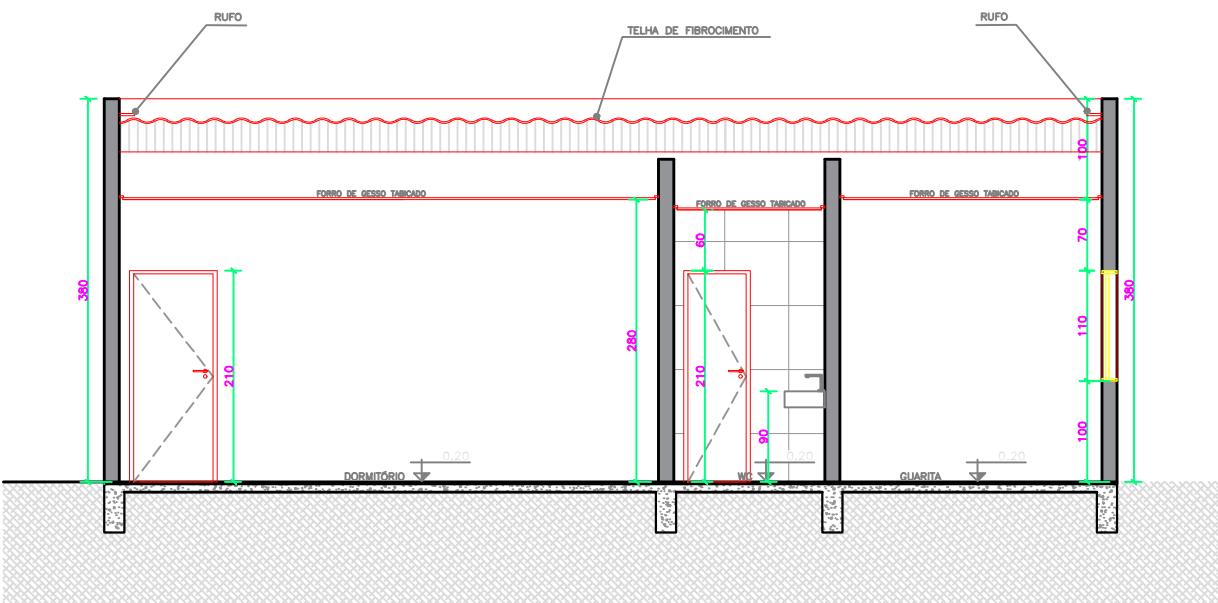


ACABAMENTOS - ESCRITÓRIO			
REVESTIMENTO	Especificação	LOCAL	ÁREA
Cemâmico	Piso Cerâmico Marmorizado Brilhante Borda Reta Interno 54x54cm Phanteon Lef	PISO GERAL	73,03m²
	Cobertura de parede 280cm com Cerâmico Marmorizado Brilhante Borda Reta Interno 54x54cm Phanteon Lef	COPA, WC	60,15m²
Pintura	Parede pintada e emassada com tinta para ambientes externos com acabamento fosco na cor branca	FACHADA NORTE, LESTE E SUL	105m²
	Parede pintada e emassada com Tinta Látex Coralar + Econômico Sem Cheiro 18 L Branco Gelo	ACESSO, SALA 01, 02 E ARQUIVO	135m²
	Fechamento com forro em reguas de pvc, frisado para ambientes comerciais	GESSO GERAL	73,03m²

ACABAMENTOS - ESCRITÓRIO			
ESQUADRIA	Especificação	LOCAL	QTE
PORTA	Porta de Madeira Lisa Nevada MGM 210cmx90cm Melamínico Mogno	SALA 01 E SALA 02	02
	Porta de Madeira Lisa Nevada MGM 210cmx70cm Melamínico Mogno	SALA 02, ARQUIVO COPA E WC	05
JANELA	Restauração das janelas existentes 190x110cm e 100x110cm com lixamento e nova pintura na cor cinza sem brilho	SALA 01 E 02	03

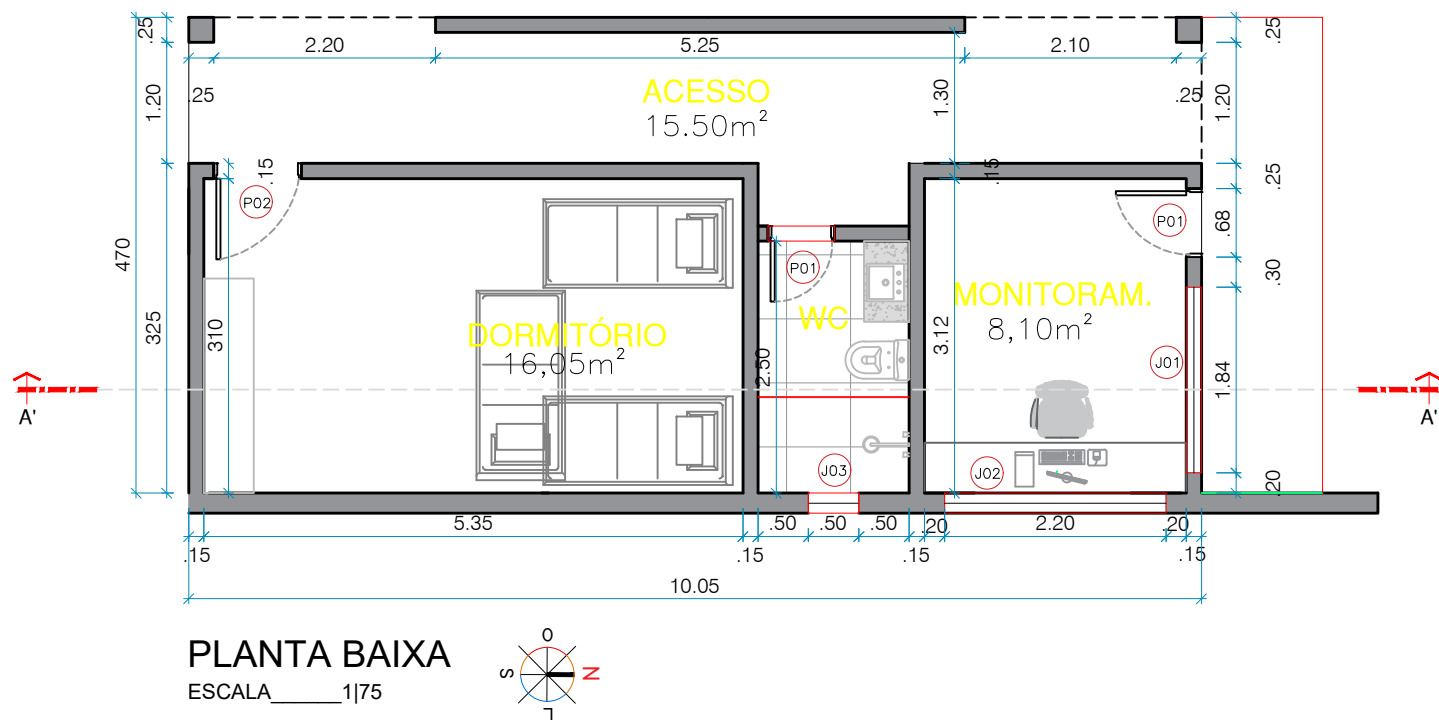


ACABAMENTOS - GUARITA			
REVESTIMENTO	Especificação	LOCAL	ÁREA
Cemâmico	Piso Cerâmico Marmorizado Brilhante Borda Reta Interno 54x54cm Phanteon Lef	PISO GERAL	47.44m²
	Cobertura de parede 280cm com Cerâmico Marmorizado Brilhante Borda Reta Interno 54x54cm Phanteon Lef	BANHEIRO	23m²
Pintura	Parede pintada e emassada com tinta para ambientes externos com acabamento fosco na cor branca	FACHADA NORTE, SUL E OESTE	115m²
	Parede pintada e emassada com Tinta Látex Coralar + Econômico Sem Cheiro 18 L Branco Gelo	ACESSO, SALA 01, 02 E ARQUIVO	112m²
	Fechamento com forro em reguas de pvc, frisado para ambientes comerciais	GESSO GERAL	46m²

ACABAMENTOS - GUARITA			
ESQUADRIA	Especificação	LOCAL	QTE
PORTA	Porta de Madeira Lisa Nevada MGM 210cmx70cm Melamínico Mogno	MONITORAMENTO BANHEIRO	02
	Porta de Madeira Lisa Nevada MGM 210cmx70cm Melamínico Mogno	DORMITÓRIO	01
JANELA	J01 - Janela de aluminio com vidro 185 x 110cm J02 - Janela de aluminio com vidro fumê 220 x 110cm J03 - Janela basculante horizontal de vidro 50 x 40cm	SALA 01 E 02 BANHEIRO	03

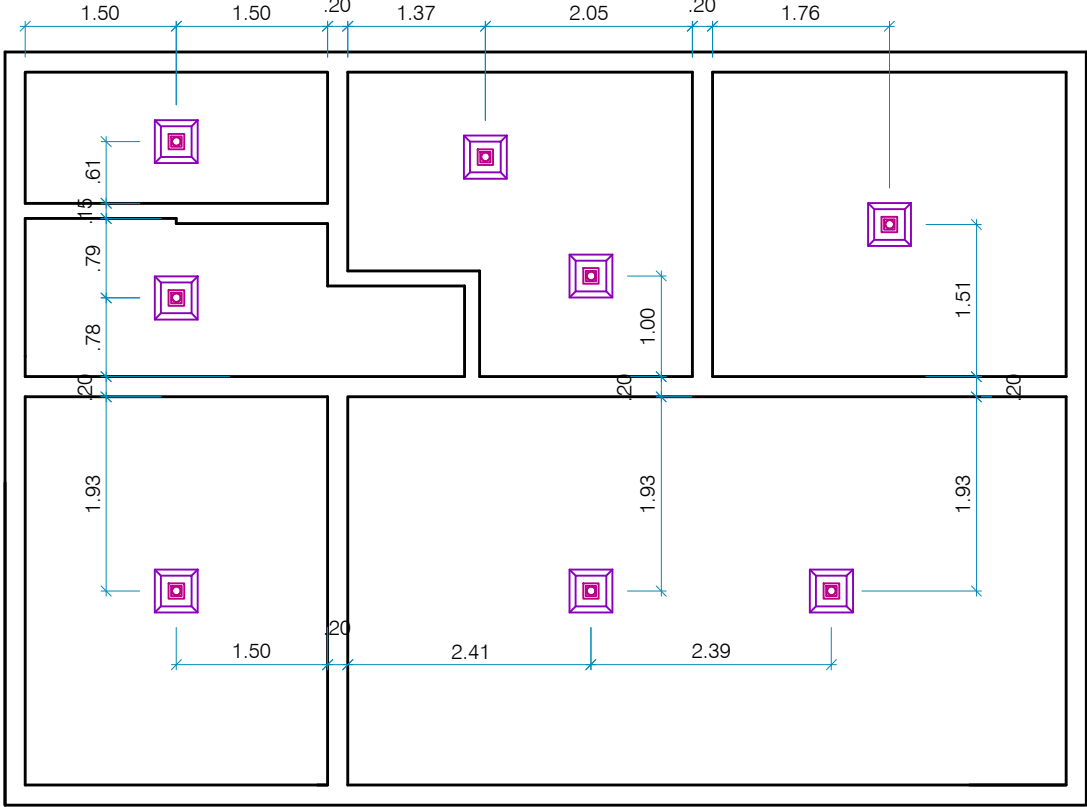


PLANTA BAIXA
PONTOS LUMINICOS_____1/75



PONTOS LUMINICOS			
SIMBOLO	ESPECIFICAÇÃO	UNI	LOCAL
	Plafon quadrado sobrepor 40x40 30w branco frio	08	SALA 01, 02, ARQUIVO, COPA, BANHEIRO
	Conjunto 4x2 com 1 Interruptor Simples Liz 10 A 250 V Branco	08	SALA 01, 02, ARQUIVO, COPA, BANHEIRO
	Tomada Dupla 4x2 10A Branca Habitat Fame MÉDIA=1,20m	06	ARQUIVO, COPA
	Tomada Dupla 4x2 10A Branca Habitat Fame BAIXA=0,50m	07	SALA 01, 02, ARQUIVO

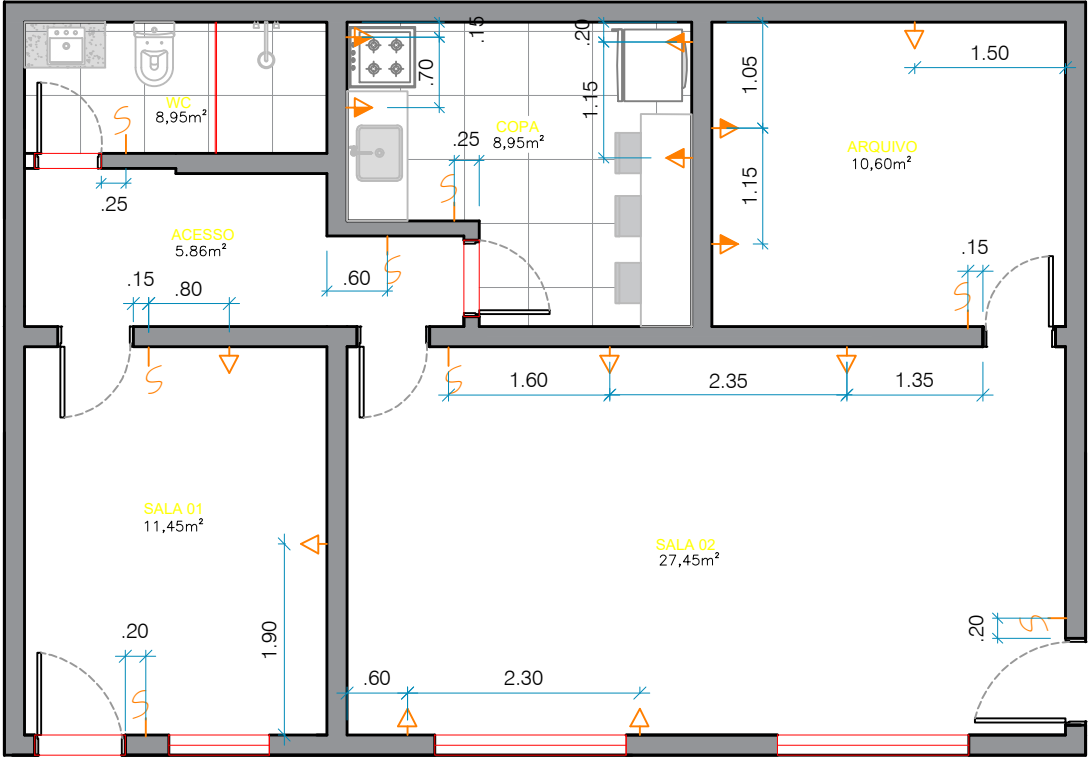


PLANTA BAIXA
PONTOS ELETRICOS_____1/75

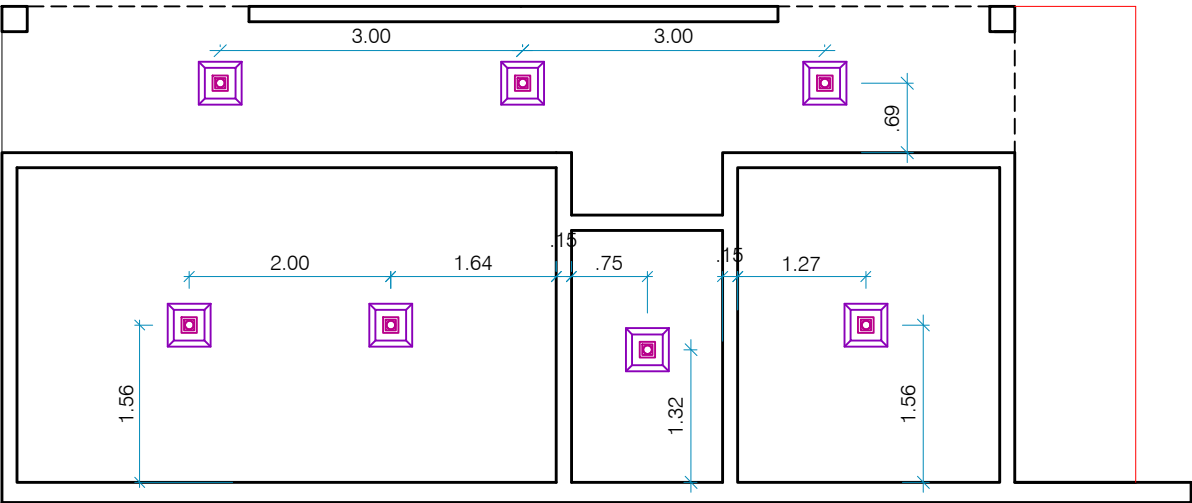

PLANTA BAIXA
PONTOS LUMINICOS _____ 1/75

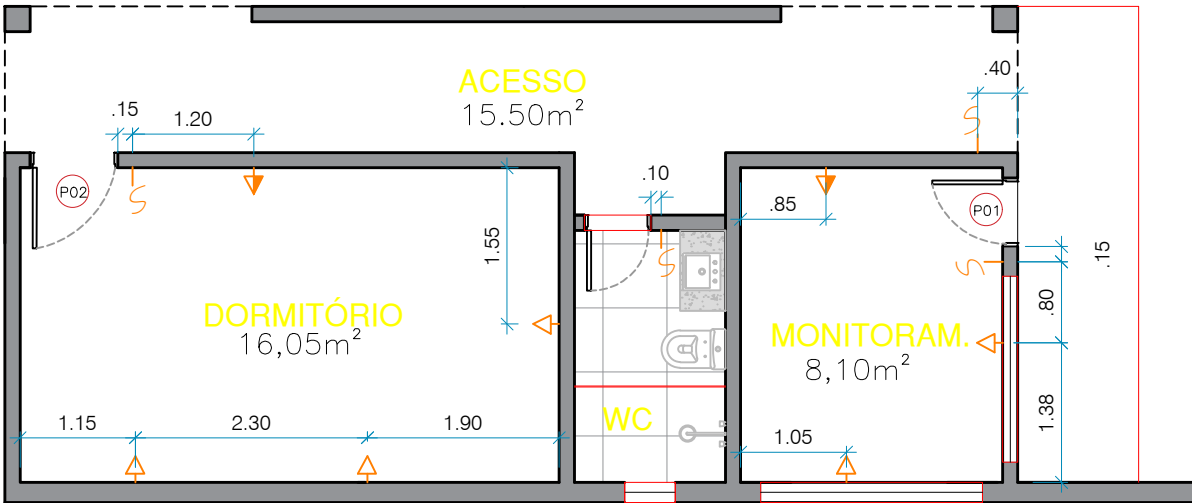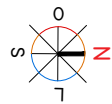

PLANTA BAIXA
PONTOS ELÉTRICOS _____ 1/75

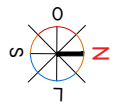


PONTOS LUMINICOS			
SIMBOLO	ESPECIFICAÇÃO	UNI	LOCAL
	Plafon quadrado sobrepor 40x40 30w branco frio	07	MONITORAMENTO, DORMITÓRIO E WC
	Conjunto 4x2 com 1 Interruptor Simples Liz 10 A 250 V Branco	03	SALA 01, 02, ARQUIVO, COPA, BANHEIRO
	Tomada Dupla 4x2 10A Branca Habitat Fame MÉDIA= 1,20m	02	MONITORAMENTO, DORMITÓRIO
	Tomada Dupla 4x2 10A Branca Habitat Fame BAIXA=0,50m	05	MONITORAMENTO, DORMITÓRIO





PLANTA BAIXA
GARAGEM MUNICIPAL ESC: 1/150

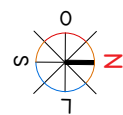

versão	data	alterações efetuadas
original		projeto original

CARIMBO PROTOCOLO GERAL		CARIMBO PREFEITURA	VERSÃO V02

CARIMBO SECRETARIO	CARIMBO DIRETORIA	CARIMBO FISCAL

CARIMBO APROVAÇÃO	CARIMBO COORDENADOR

ASSINATURAS			
PROPRIETÁRIO	ARQUITETO	RT	

 PREFEITURA DE COREMAS TRABALHANDO E RESPEITANDO O MEIO AMBIENTE	DESCRIÇÃO	PROJETO DE REFORMA - GARAGEM MUNICIPAL		
	RAÇA SOCIAL	DATA	03-2025	
	ESTADO	EXECUTIVO	DATA	MAIO 2025
	ENDEREÇO	COORDENADOR	COORDENADOR	COREMAS-PB
	PROPRIETÁRIO	AUTOR	CAYO NOGUEIRA KIRYA CRISTINE	CAU

02	PLANTA BAIXA		
02			
ESCALA	INDICADA	REVISÃO	REVISÃO