


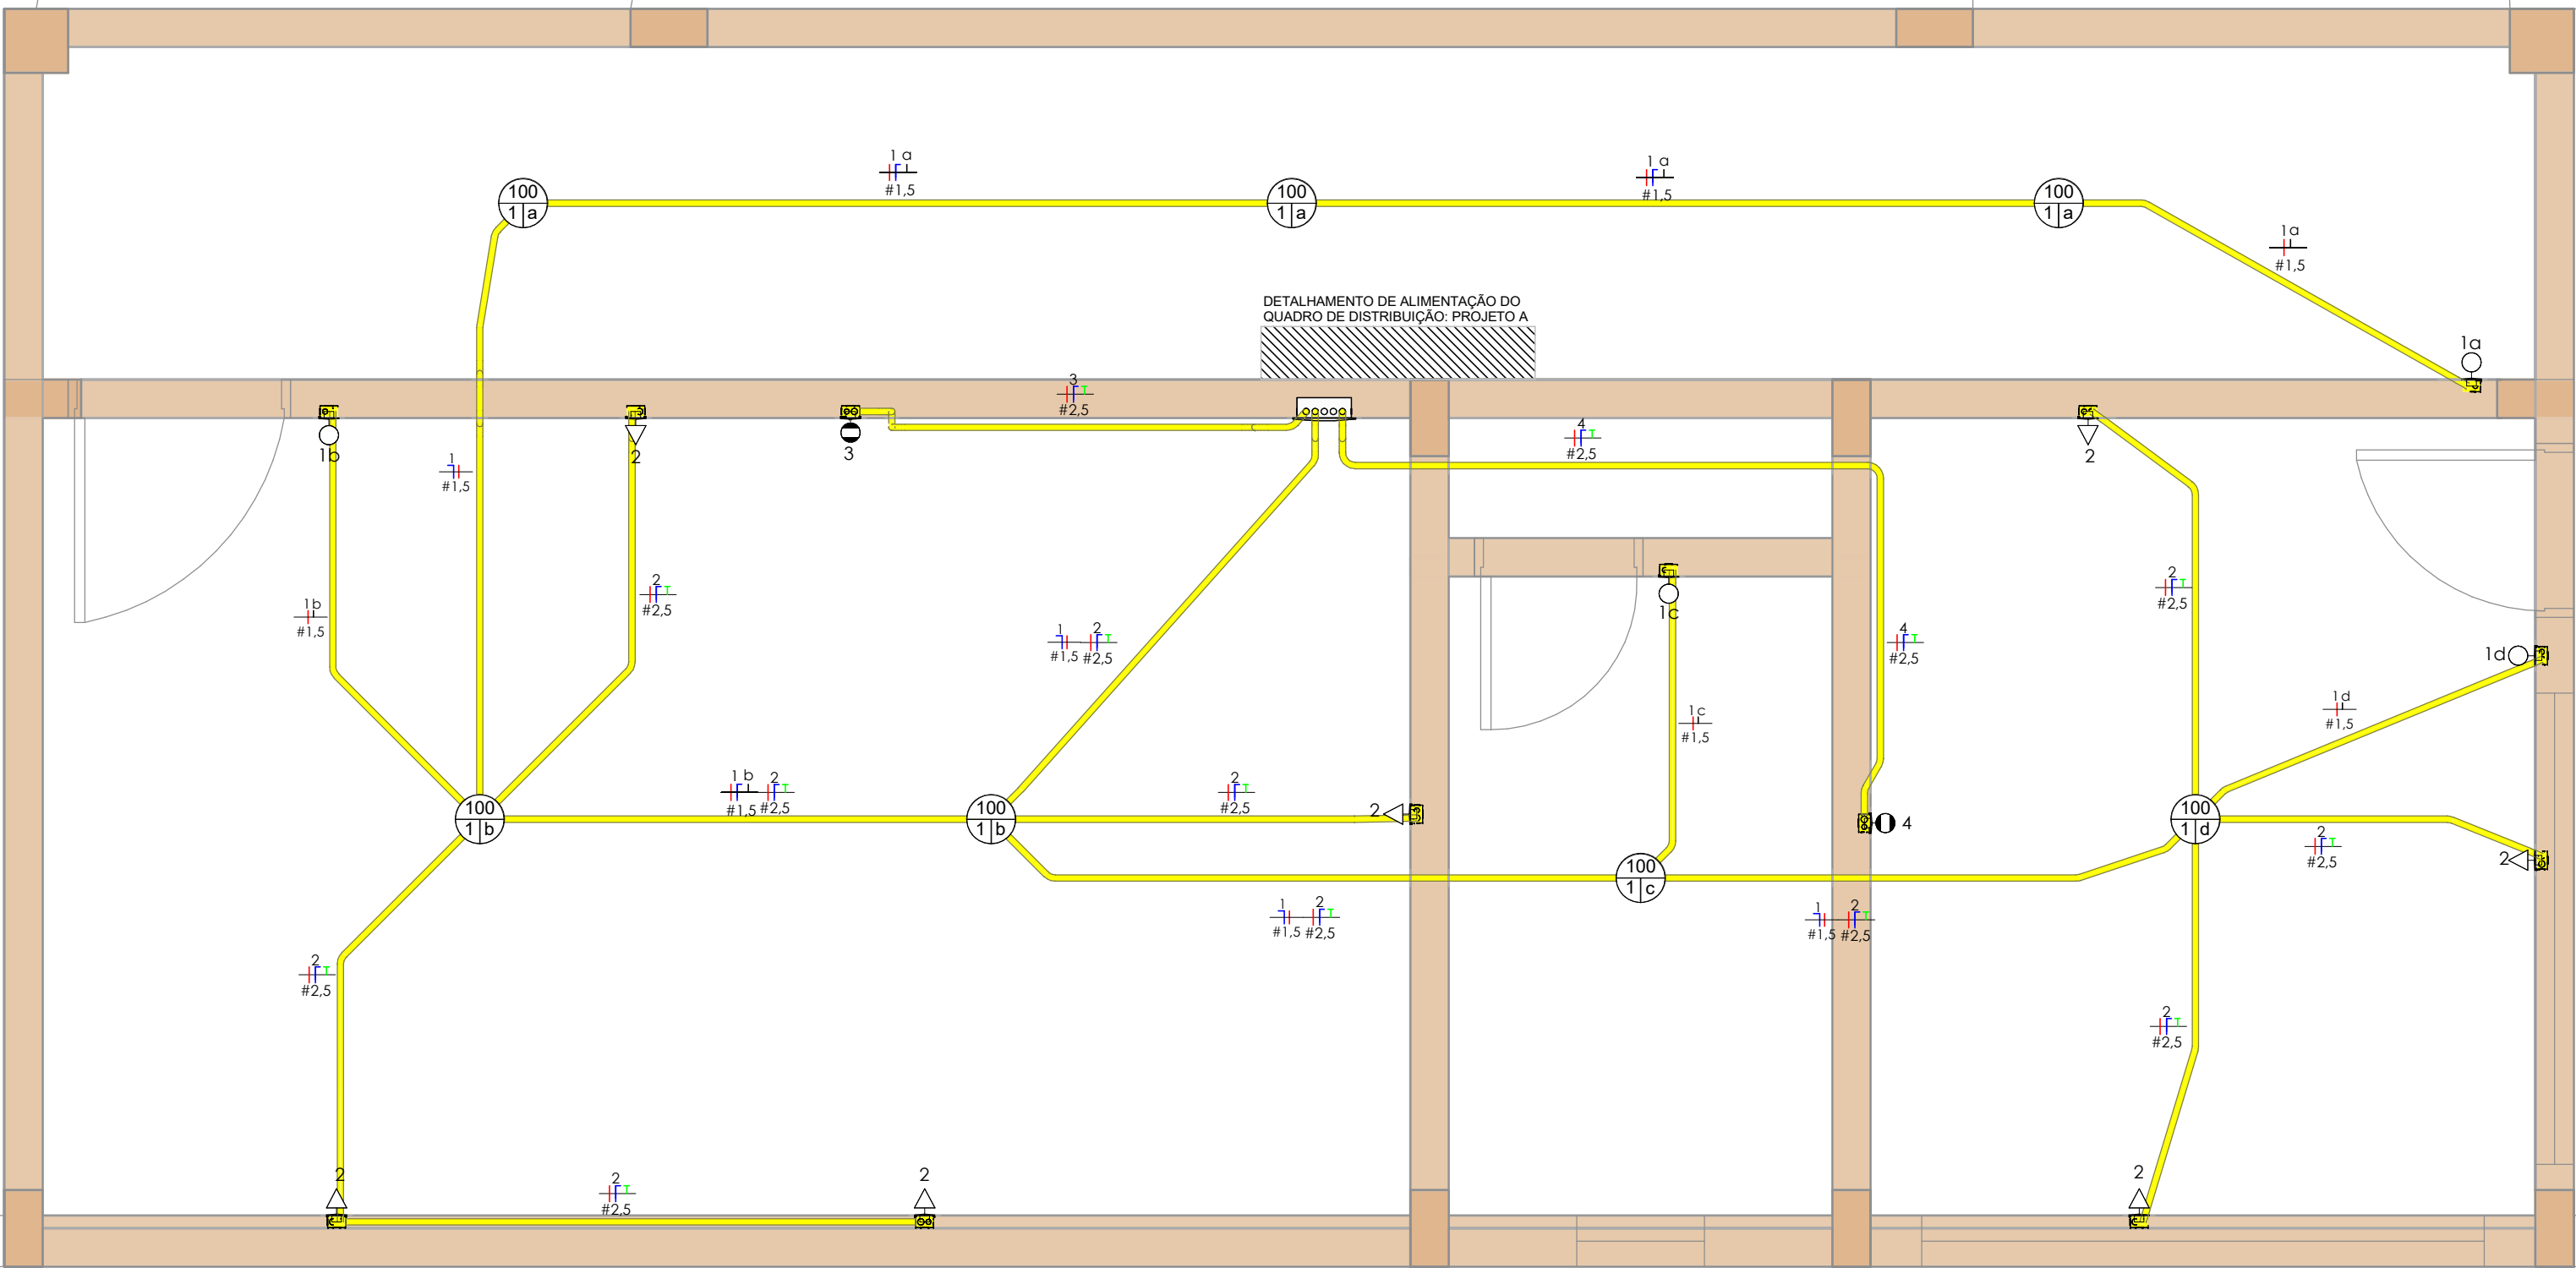


PLANTA BAIXA - TÉRREO

ESCALA_____ 1 : 25

GERAL - LISTA DE MATERIAIS - COMPONENTES		
Descrição do Material	Dimensões	Quantidade (peças)
Interruptores Conjunto montado com 1 Interruptor simples, 10A 250V~, 4"x2"	1S, 4"x2"	4
Ponto de Ar Condicionado Ponto em caixa 4x2	Ponto de Ar Condicionado	2
Quadros Quadro de Distribuição 6/8 Disjuntores, de embutir, fabricado em PVC antichamas, com barramento de terra e neutro, porta branca, dimensões 245x190x78,7mm.	6/8 Disjuntores	1
Tomadas Conjunto montado de 1 Tomada 2P+T, 10A, posto horizontal, 4"x2"	10A, 4"x2"	7

QUANTITATIVO DE CABOS EM METROS (Cobre/Un/Iso. PVC/750V/70°C)						
(F - Condutor Fase), (N - Condutor Neutro), (T - Condutor Terra), (Re - Condutor de Retorno)						
Sugestão de Cores para os condutores- F: Vermelho, N: Azul Claro, PE: Verde, Re - Branco						
F-1,5mm²	F-2,5mm²	N-1,5mm²	N-2,5mm²	T-2,5mm²	Re-1,5mm²	Tipo de Condutor
35,1	47,7	20,9	47,7	47,7	23,5	CABO COBRE PVC 70°C 450/750V

GERAL - LISTA DE MATERIAIS - ELETRODUTOS		
Descrição do Material	Diâmetro Nominal	Comprimento (m)
Eletroduto flexível corrugado	Ø25	68,60 m

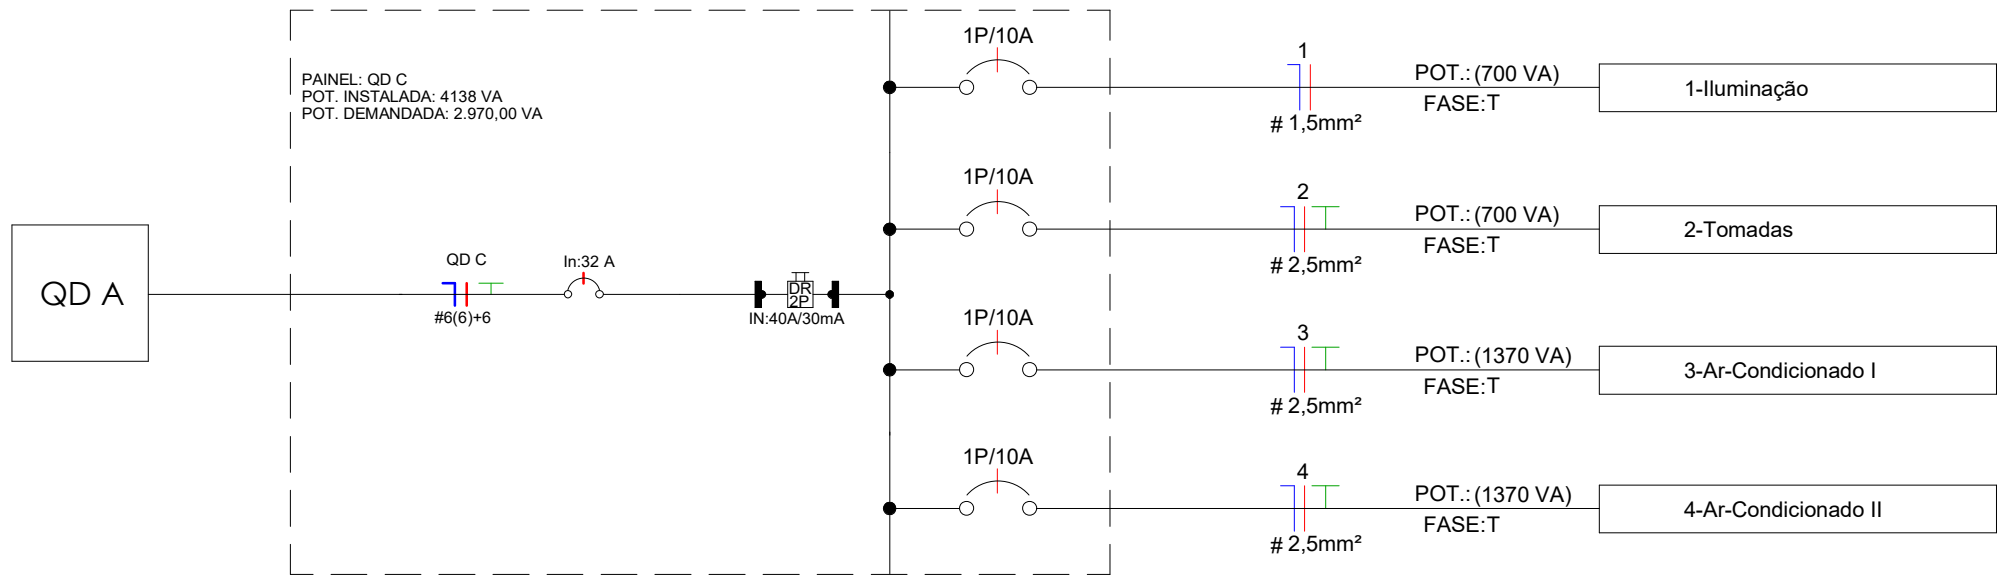

COMO ALTERNATIVA À ADOÇÃO DE FITA ISOLANTE, PARA UNIÃO DAS FIAÇÕES, QUE PORVENTURA IRÃO SER NECESSÁRIAS, RECOMENDAMOS A UTILIZAÇÃO DE **CONECTORES**.

ABAIXO ALGUNS MODELOS DISPONÍVEIS NO MERCADO.



Painel: QD C

Localização:

Alimentado por:

Montagem:

Notas:

Alimentação: 220V/380V Monofásico (F+N+T)

Circuito	Descrição	Tensão (V)	Esquema	Potência Total (VA)	FP	Potência Total (W)	Corrente Nominal (A)	FCA	FCT	Ib: Corrente de Projeto Corrigida (A)	In: Disjuntor (A)	Tipo de Instalação	Condutor Pré-Dimensionado (Seção e Iz: Capacidade de condução de Corrente)	Seção do Condutor Adotado (mm²)	L Aprox. (m)	L Considerado (m)	Queda de Tensão (%)	Potência
1	Iluminação	220,00	FNT	700 VA	0,92	644 W	3,18 A	0,8	1	3,98 A	10,00 A	[Cu/PVC/750V/70°]-Un-B1-2Cc (Ilum.)	1-#1,5(17,5A), 1-#1,5(17,5A), 1-#1,5	1,5	7,83	10	0,39	700 VA
2	Tomadas	220,00	FNT	700 VA	0,9	630 W	3,18 A	0,8	1	3,98 A	10,00 A	[Cu/PVC/750V/70°]-Un-B1-2Cc	1-#2,5(24A), 1-#2,5(24A), 1-#2,5	2,5	12,18	15	0,34	700 VA
3	Ar-Condicionado I	220,00	FNT	1370 VA	0,92	1260 W	6,23 A	1	1	6,23 A	10,00 A	[Cu/PVC/750V/70°]-Un-B1-2Cc	1-#2,5(24A), 1-#2,5(24A), 1-#2,5	2,5	4,99	10	0,46	1370 VA
4	Ar-Condicionado II	220,00	FNT	1370 VA	0,92	1260 W	6,23 A	1	1	6,23 A	10,00 A	[Cu/PVC/750V/70°]-Un-B1-2Cc	1-#2,5(24A), 1-#2,5(24A), 1-#2,5	2,5	6,58	10	0,46	1370 VA
5																		
Totais:																		4138 VA

Legenda:

FP: Fator de Potência

FCA:Fator de Correção por Agrupamento

FCT:Fator de Correção por Temperatura

Ib: Corrente de Projeto Corrigida(A)

In:Corrente Nominal do Disjuntor (A)

Iz: Capacidade de condução de corrente do condutor(A)

Tipo de Carga

Iluminação+TUGs (Residencial)

Ar Condicionado

Potência Instalada (VA)

1400 VA

2739 VA

Fator de Demanda

0,40

0,88

Potência Demandada (VA)

560 VA

2410 VA

Totais do Pannel

Potência Instalada: 4138 VA

Potência Demandada: 2970 VA

Corrente Total: 18,81 A

Corrente Total Demandada: 13,50 A

Notas:

PROPRIETÁRIO: PREFEITURA MUNICIPAL DE COREMAS-PB			
PROJETO: LINCOLN CARTAXO DE LIRA JÚNIOR CREA 160.814.689-8			
PROJETO:	PROJETO C - ELÉTRICO GARAGEM COREMAS - PB		
CONCEDENTE:	PREFEITURA MUNICIPAL DE COREMAS - PB		
CONVENIENTE:	MUNICÍPIO DE COREMAS - PB		
LOCAL:	COREMAS-PB		
DESENHO	DATA	RESPONSÁVEL TÉCNICO	RUBRICA
CÓPIA	JUN/2025	LINCOLN CARTAXO	
VISTO			
PRANCHA:	DESCRICO: PROJETO ELÉTRICO - PLANTA BAIXA - QUANTITATIVOS - DETALHAMENTOS		ESCALA:
04 /04			INDICADA



Av. Gov. Flavio R. Coutinho, 500, sl. 601
Jd. Oceania, 58037-005 - João Pessoa (PB)
Tel +55 99924.4447
e-mail: contato@lclprojetos.com