



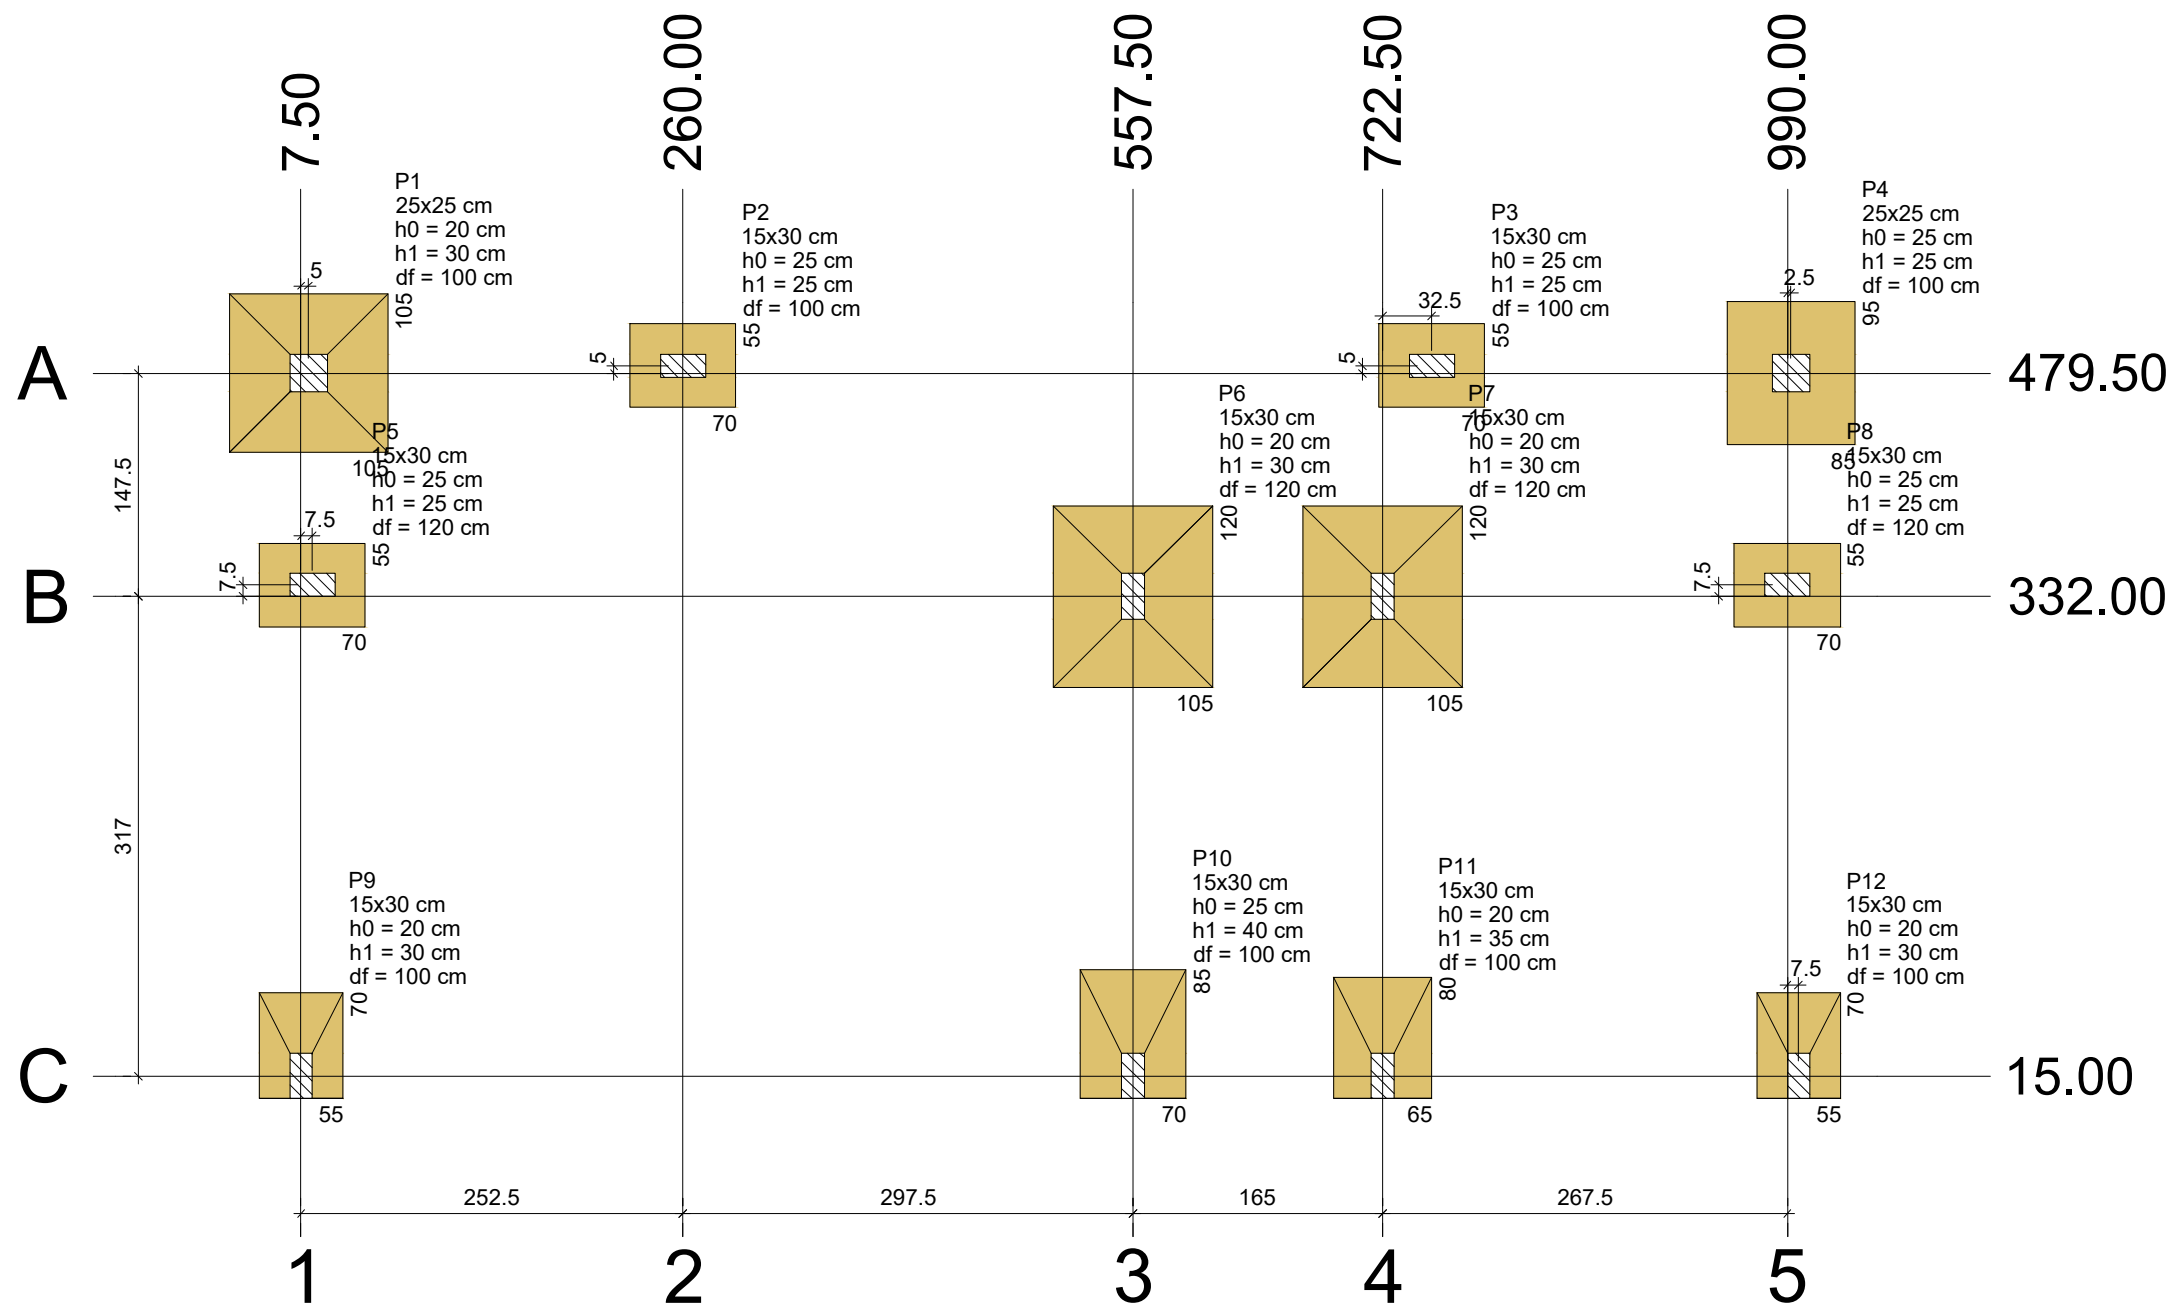

Planta de localização
escala 1:50

Pilar													
Nome	Seção (cm)	X (cm)	Y (cm)	Carga Máx. (tf)	Carga Mín. (tf)	Mx Máximo (kgf.m)		My Máximo (kgf.m)		Fx Máximo (tf)		Fy Máximo (tf)	
						Positivo	Negativo	Positivo	Negativo	Positivo	Negativo	Positivo	Negativo
P1	25x25	12.50	479.50	3.3	1.7	700	-400	100	-200	0.0	-0.3	0.4	-0.5
P2	15x30	260.00	484.50	3.0	2.7	200	-300	300	-200	0.4	0.0	0.1	-0.2
P3	15x30	755.00	484.50	3.0	2.6	200	-300	100	-200	0.0	-0.4	0.1	-0.2
P4	25x25	992.50	479.50	3.3	1.7	600	-700	300	-200	0.3	0.0	0.5	-0.4
P6	15x30	557.50	332.00	4.9	2.9	1300	-300	100	-200	0.0	-0.3	0.0	-1.3
P7	15x30	722.50	332.00	4.5	2.6	1200	-300	200	0	0.2	0.0	0.2	-1.0
P8	15x30	990.00	339.50	2.7	1.4	300	-300	200	-300	0.1	-0.1	0.3	-0.3
P9	15x30	7.50	15.00	2.7	2.3	0	-400	0	0	0.0	-0.1	0.4	0.0
P10	15x30	557.50	15.00	5.6	3.6	0	-1000	0	0	0.2	0.0	1.0	0.0
P11	15x30	722.50	15.00	4.7	2.7	0	-800	0	0	0.1	-0.1	0.8	0.0
P12	15x30	997.50	15.00	2.3	1.8	0	0	0	0	0.1	0.0	0.2	-0.3
P5	15x30	15.00	339.50	2.8	1.6	300	-100	200	-300	0.2	-0.2	0.2	-0.5

Os esforços indicados nesta tabela são os valores máximos obtidos pela envoltória de todas as combinações definidas para as fundações. Para análises complementares, deve-se consultar o relatório de esforços na fundação, que apresenta os valores calculados para cada combinação.

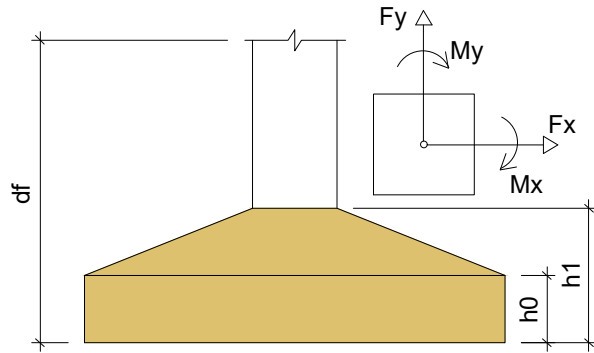

Fundação				
Lado B (cm)	Lado H (cm)	h0 / ha (cm)	h1 / hb (cm)	df (cm)
105	105	20	30	100
55	70	25	25	100
55	70	25	25	100
95	85	25	25	100
105	120	20	30	120
105	120	20	30	120
55	70	25	25	120
70	55	20	30	100
85	70	25	40	100
80	65	20	35	100
70	55	20	30	100
55	70	25	25	120

Locação no eixo X	
Coordenadas (cm)	Nome
7.50	P9
12.50	P1
15.00	P5
260.00	P2
557.50	P6, P10
722.50	P7, P11
755.00	P3
990.00	P8
992.50	P4
997.50	P12

Locação no eixo Y	
Coordenadas (cm)	Nome
484.50	P2, P3
479.50	P1, P4
339.50	P5, P8
332.00	P6, P7
15.00	P9, P10, P11, P12



PROPRIETÁRIO: PREFEITURA MUNICIPAL DE COREMAS- PB

PROJETO: LINCOLN CARTAXO DE LIRA JÚNIOR CREA 160.814.689-8

FOLHA	PROJETO: GARAGEM COREMAS (ESTRUTURAL ANEXO I)		
01/09	CONVENIENTE: PREFEITURA MUNICIPAL DE COREMAS-PB		
	CONCIDENTE: PREFEITURA MUNICIPAL DE COREMAS-PB		
	LOCALIDADE: COREMAS- PB		
DESENHO	DATA	RESPONSÁVEL	RUBRICA
CÓPIA	JUN/2025	LINCOLN CARTAXO	
VISTO			
ESCALAS	DESENHOS	CONVÊNIO	
INDICADO	- PLANTA DE LOCAÇÃO	ARQUIVO	

Aprovações: