


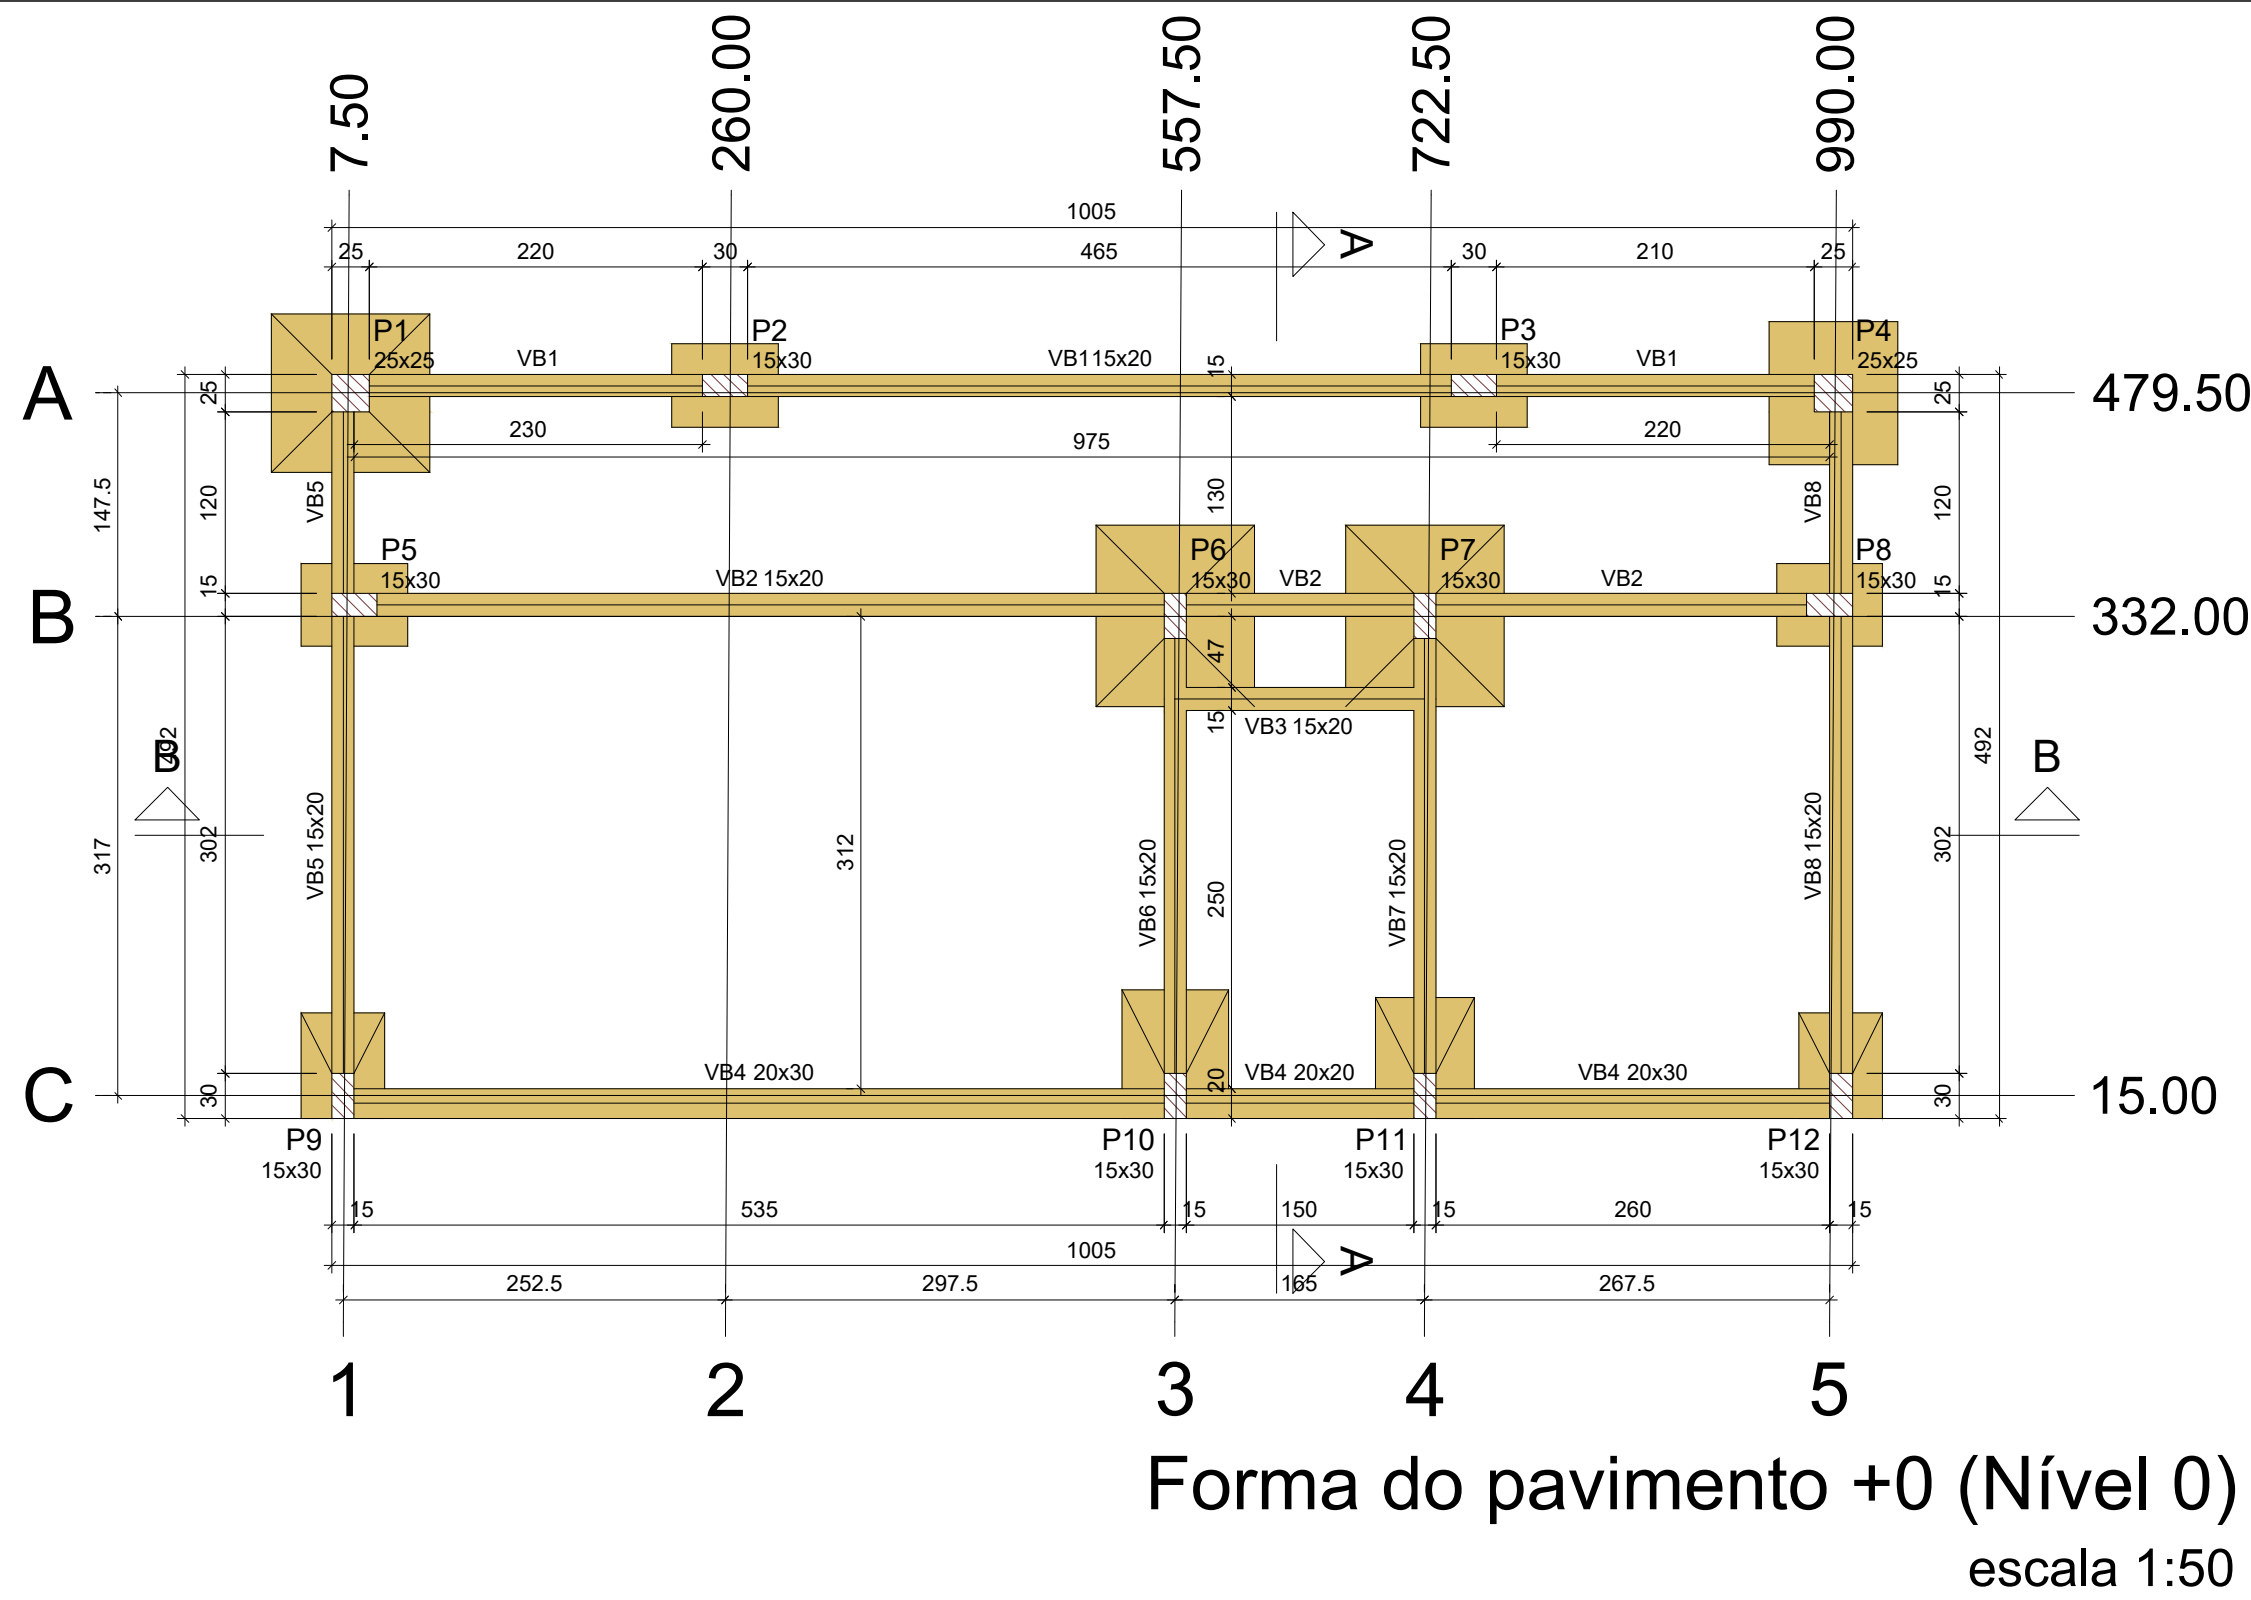


Vigas			
Nome	Seção (cm)	Elevação (cm)	Nível (cm)
VB1	15x20	0	0
VB2	15x20	0	0
VB3	15x20	0	0
VB4	20x30	0	0
	20x20	0	0
	20x30	0	0
VB5	15x20	0	0
VB6	15x20	0	0
VB7	15x20	0	0
VB8	15x20	0	0

Características dos materiais	
fck (kgf/cm²)	Ecs (kgf/cm²)
250	241500

Legenda dos pilares	
	Pilar que passa
	Pilar com mudança de seção

Legenda das vigas e paredes	
	Viga

Pilares			
Nome	Seção (cm)	Elevação (cm)	Nível (cm)
P1	25x25	0	0
P2	15x30	0	0
P3	15x30	0	0
P4	25x25	0	0
P6	15x30	0	0
P7	15x30	0	0
P8	15x30	0	0
P9	15x30	0	0
P10	15x30	0	0
P11	15x30	0	0
P12	15x30	0	0
P5	15x30	0	0

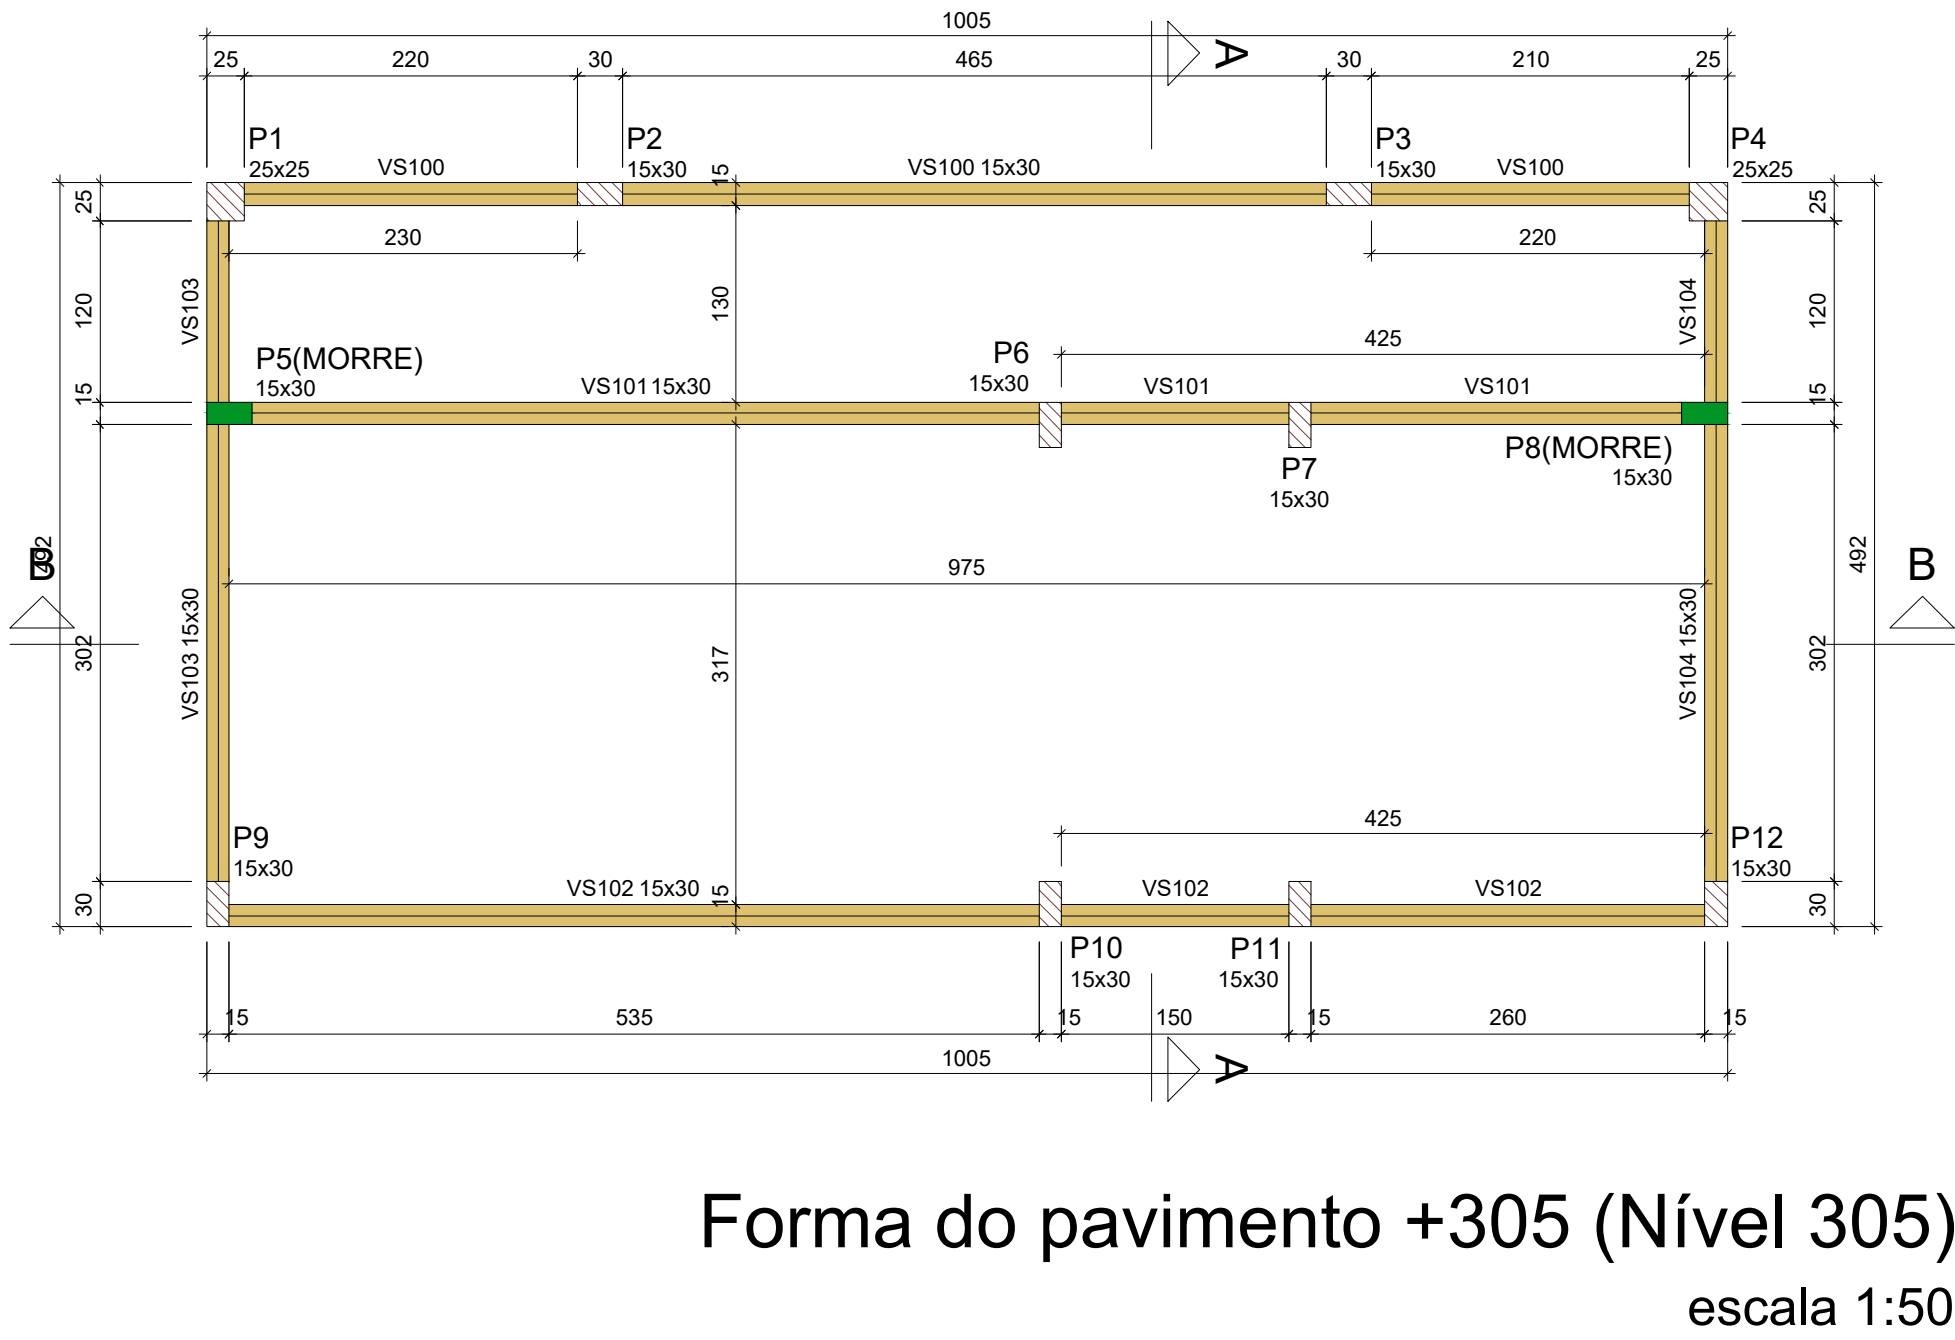


Vigas			
Nome	Seção (cm)	Elevação (cm)	Nível (cm)
VS100	15x30	0	305
VS101	15x30	0	305
VS102	15x30	0	305
VS103	15x30	0	305
VS104	15x30	0	305

Características dos materiais	
fck (kgf/cm²)	Ecs (kgf/cm²)
250	241500

Legenda das vigas e paredes	
	Viga

Legenda dos pilares	
	Pilar que morre
	Pilar que passa

Pilares			
Nome	Seção (cm)	Elevação (cm)	Nível (cm)
P1	25x25	0	305
P2	15x30	0	305
P3	15x30	0	305
P4	25x25	0	305
P6	15x30	0	305
P7	15x30	0	305
P8	15x30	0	305
P9	15x30	0	305
P10	15x30	0	305
P11	15x30	0	305
P12	15x30	0	305
P5	15x30	0	305

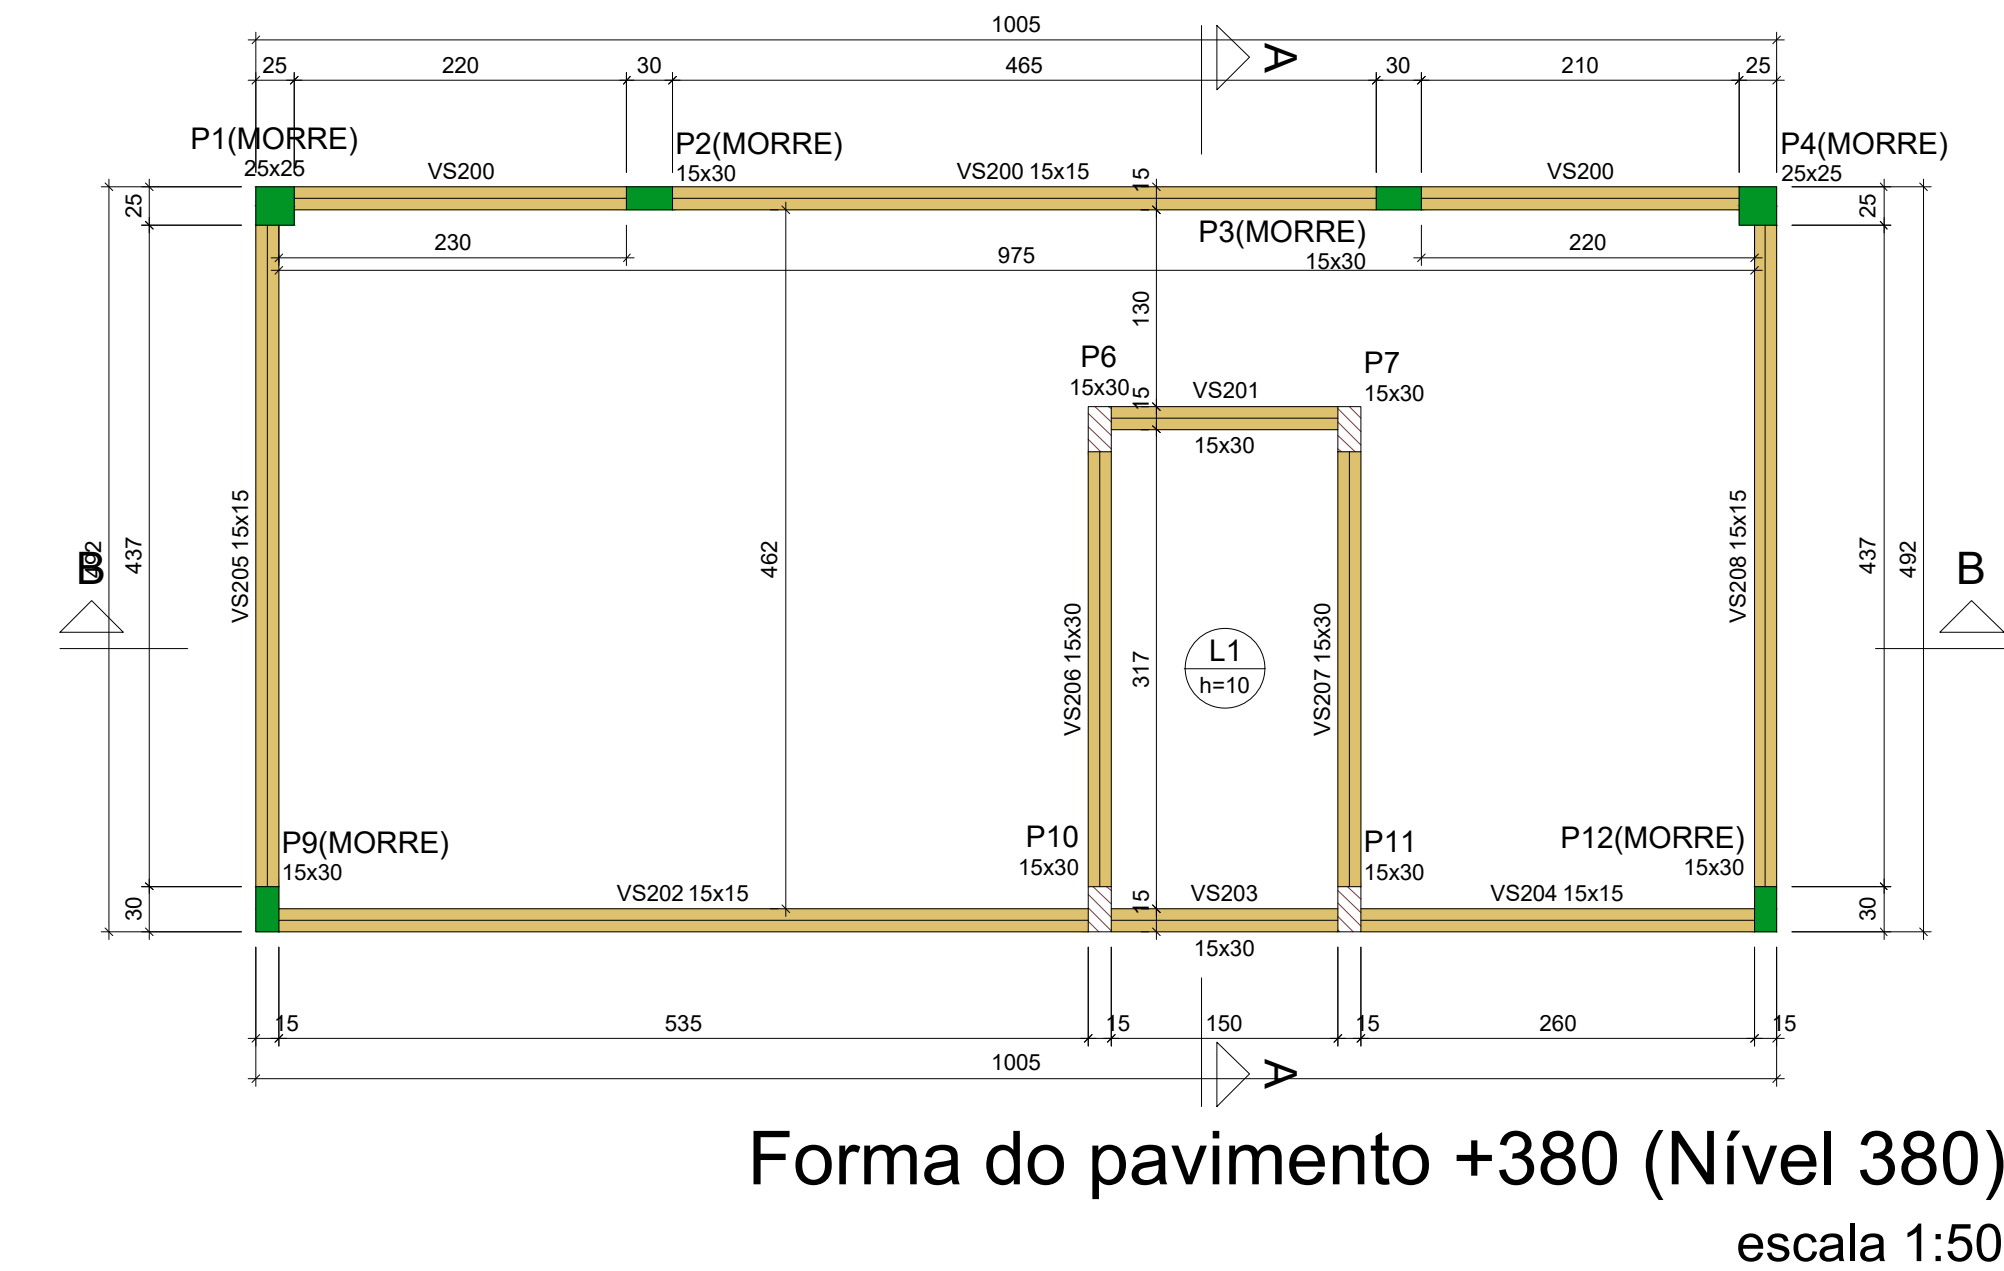

Lajes								
Dados					Sobrecarga (kgf/m²)			
Nome	Tipo	Altura (cm)	Elevação (cm)	Nível (cm)	Peso próprio (kgf/m²)	Adicional	Acidental	Água
L1	Maciça	10	0	380	250	100	50	950

Área de lajes			
Tipo	Altura (cm)	Bloco de Enchimento	Área (m²)
Maciça	10	-	4.75

Vigas			
Nome	Seção (cm)	Elevação (cm)	Nível (cm)
VS200	15x15	0	380
VS201	15x30	0	380
VS202	15x15	0	380
VS203	15x30	0	380
VS204	15x15	0	380
VS205	15x15	0	380
VS206	15x30	0	380
VS207	15x30	0	380
VS208	15x15	0	380

Legenda dos pilares	
	Pilar que morre
	Pilar que passa

Legenda das vigas e paredes	
	Viga

Características dos materiais	
fck (kgf/cm²)	Ecs (kgf/cm²)
250	241500

Pilares			
Nome	Seção (cm)	Elevação (cm)	Nível (cm)
P1	25x25	0	380
P2	15x30	0	380
P3	15x30	0	380
P4	25x25	0	380
P6	15x30	0	380
P7	15x30	0	380
P9	15x30	0	380
P10	15x30	0	380
P11	15x30	0	380
P12	15x30	0	380

PROPRIETÁRIO: PREFEITURA MUNICIPAL DE COREMAS- PB

PROJETO: LINCOLN CARTAXO DE LIRA JÚNIOR CREA 160.814.689-8

FOLHA
02/09

PROJETO: GARAGEM COREMAS (ESTRUTURAL ANEXO I)
CONVENIENTE: PREFEITURA MUNICIPAL DE COREMAS-PB
CONCENDENTE: PREFEITURA MUNICIPAL DE COREMAS-PB
LOCALIDADE: COREMAS- PB

DESENHO	DATA	RESPONSÁVEL	RUBRICA	DADOS
CÓPIA	JUN/2025	LINCOLN CARTAXO		
VISTO				

ESCALAS	DESENHOS	CONVÊNIO
INDICADO	- PLANTA DE FORMAS -- Pav. +0; -- Pav. +305; -- Pav. +380.	ARQUIVO

Aprovações: