


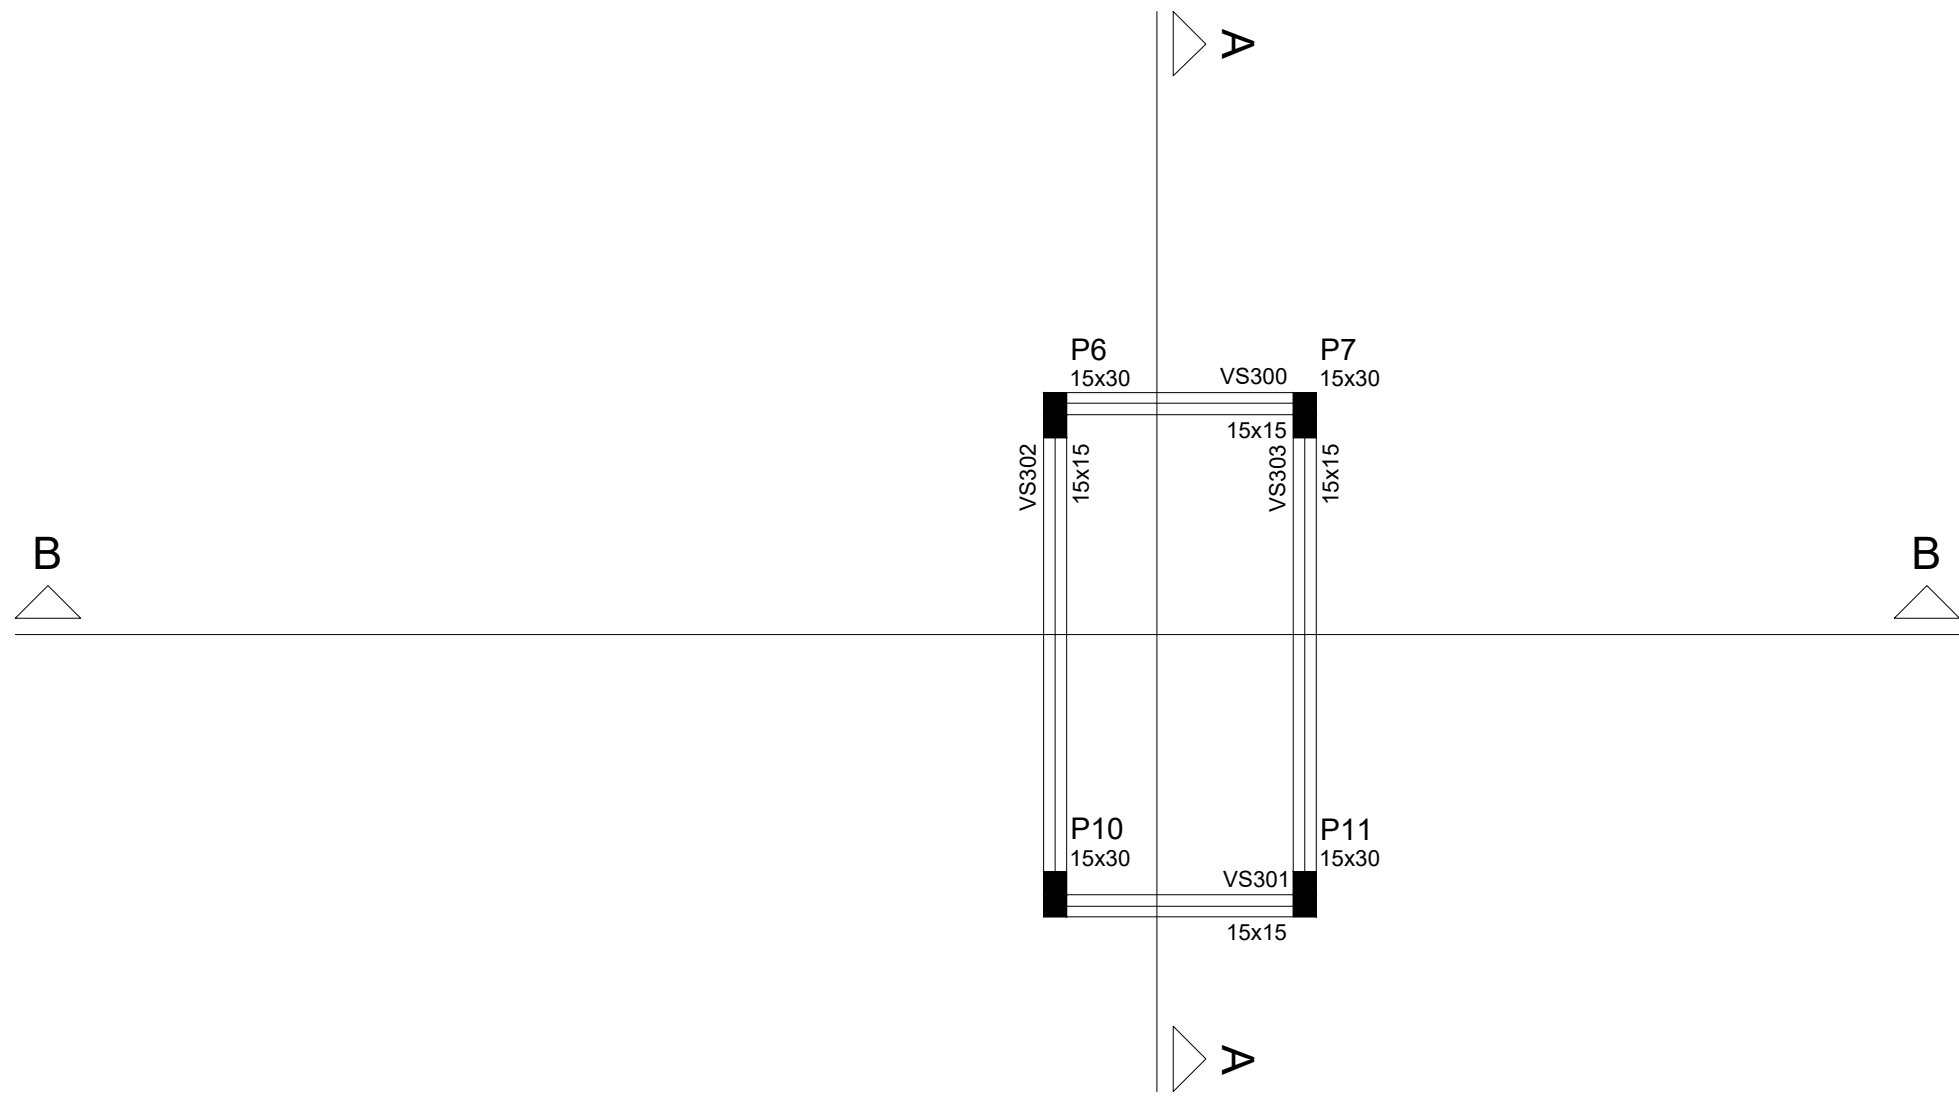


Forma do pavimento +490
escala 1:50

Vigas			
Nome	Seção (cm)	Elevação (cm)	Nível (cm)
VS300	15x15	0	490
VS301	15x15	0	490
VS302	15x15	0	490
VS303	15x15	0	490



Características dos materiais	
fck (kgf/cm²)	Ecs (kgf/cm²)
250	238000

Pilares			
Nome	Seção (cm)	Elevação (cm)	Nível (cm)
P6	15 x 30	0	490
P7	15 x 30	0	490
P10	15 x 30	0	490
P11	15 x 30	0	490


Legenda dos Pilares	
	Pilar que morre
	Pilar que passa
	Pilar que nasce
	Pilar com mudança de seção

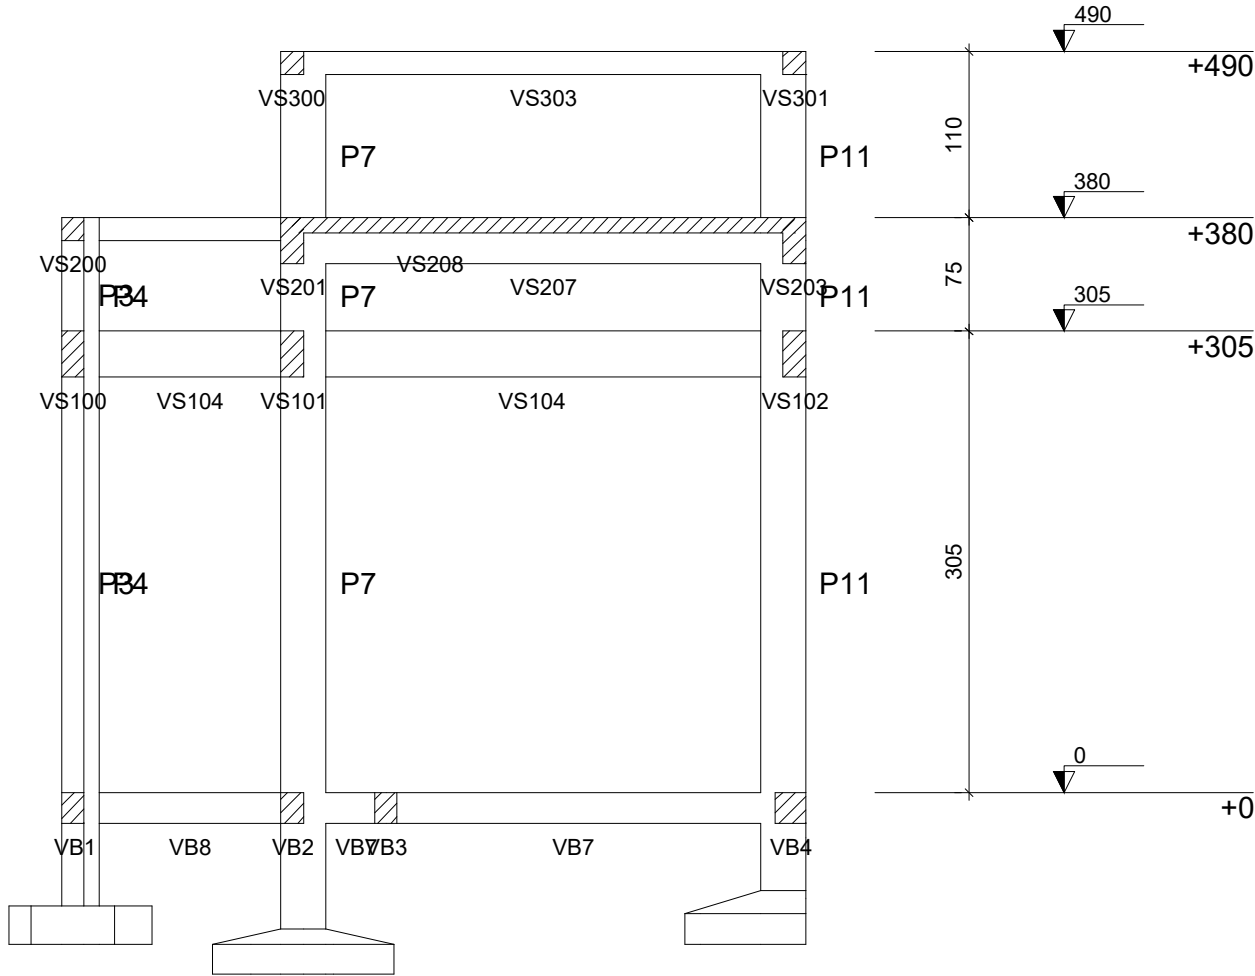

Corte A-A
escala 1:50

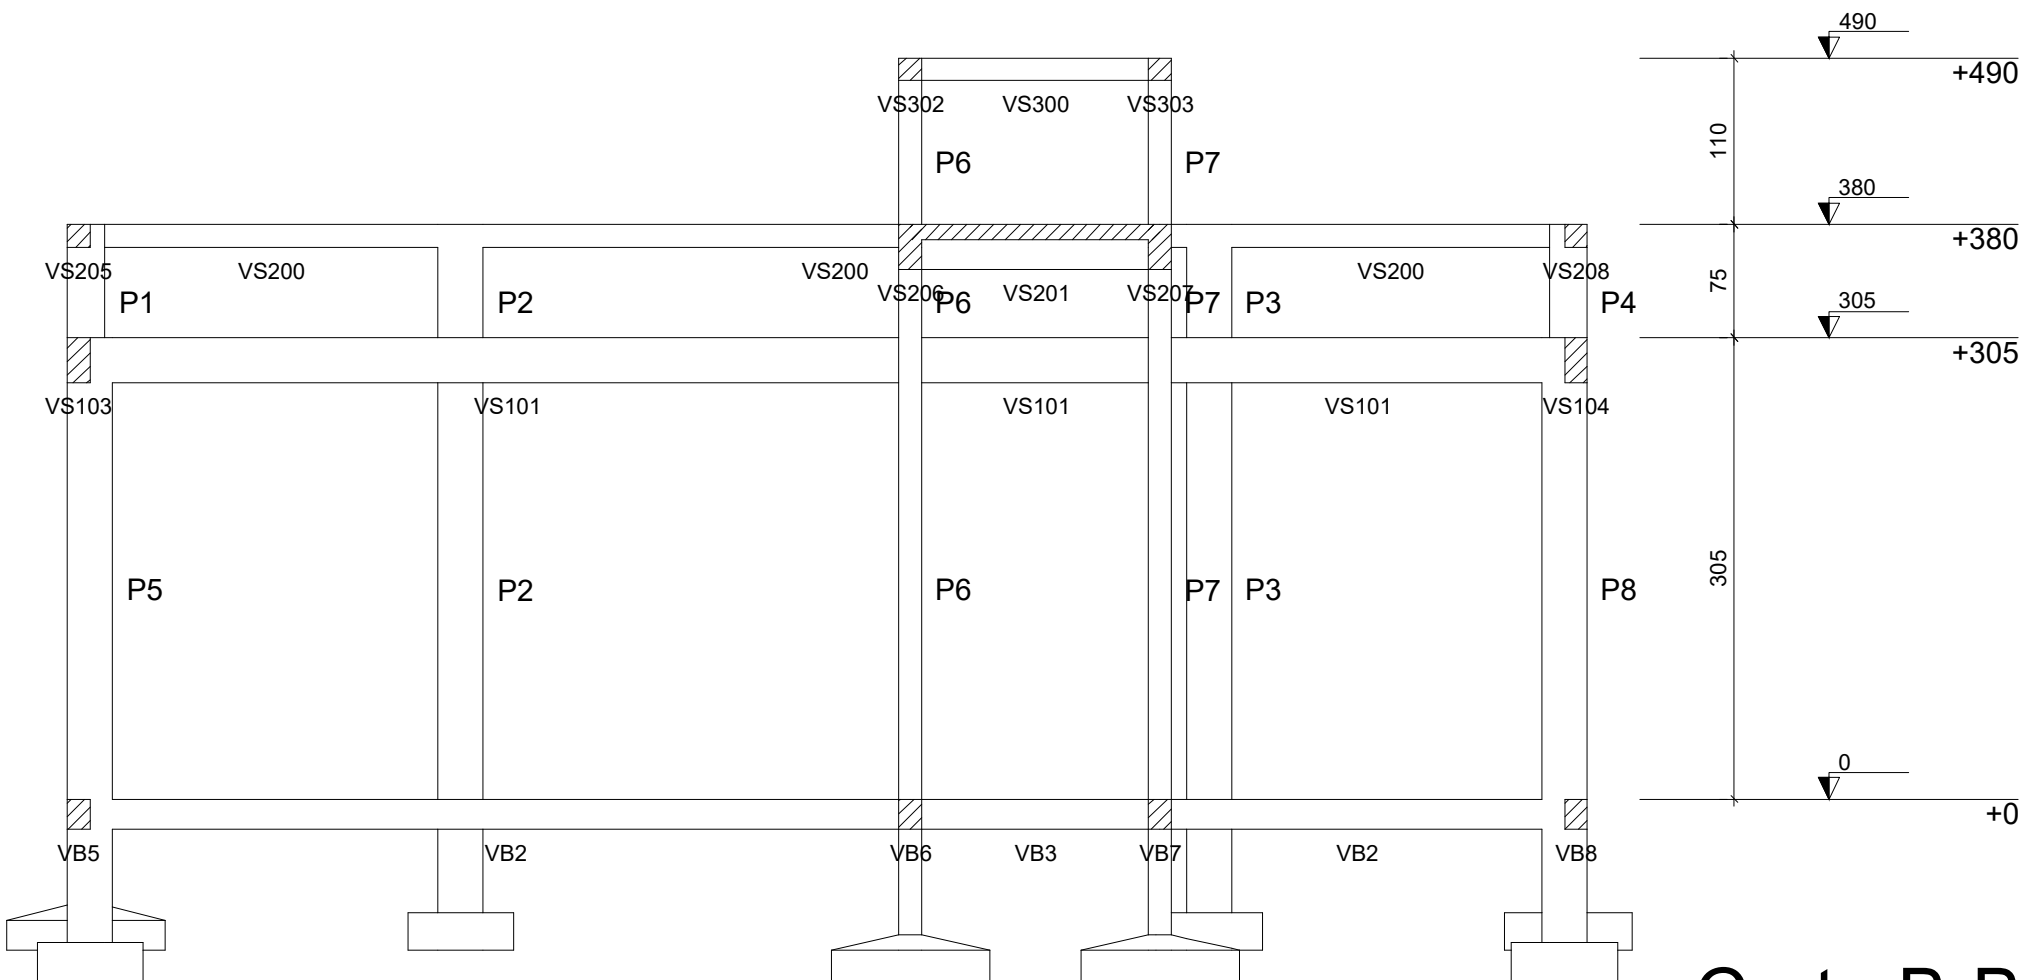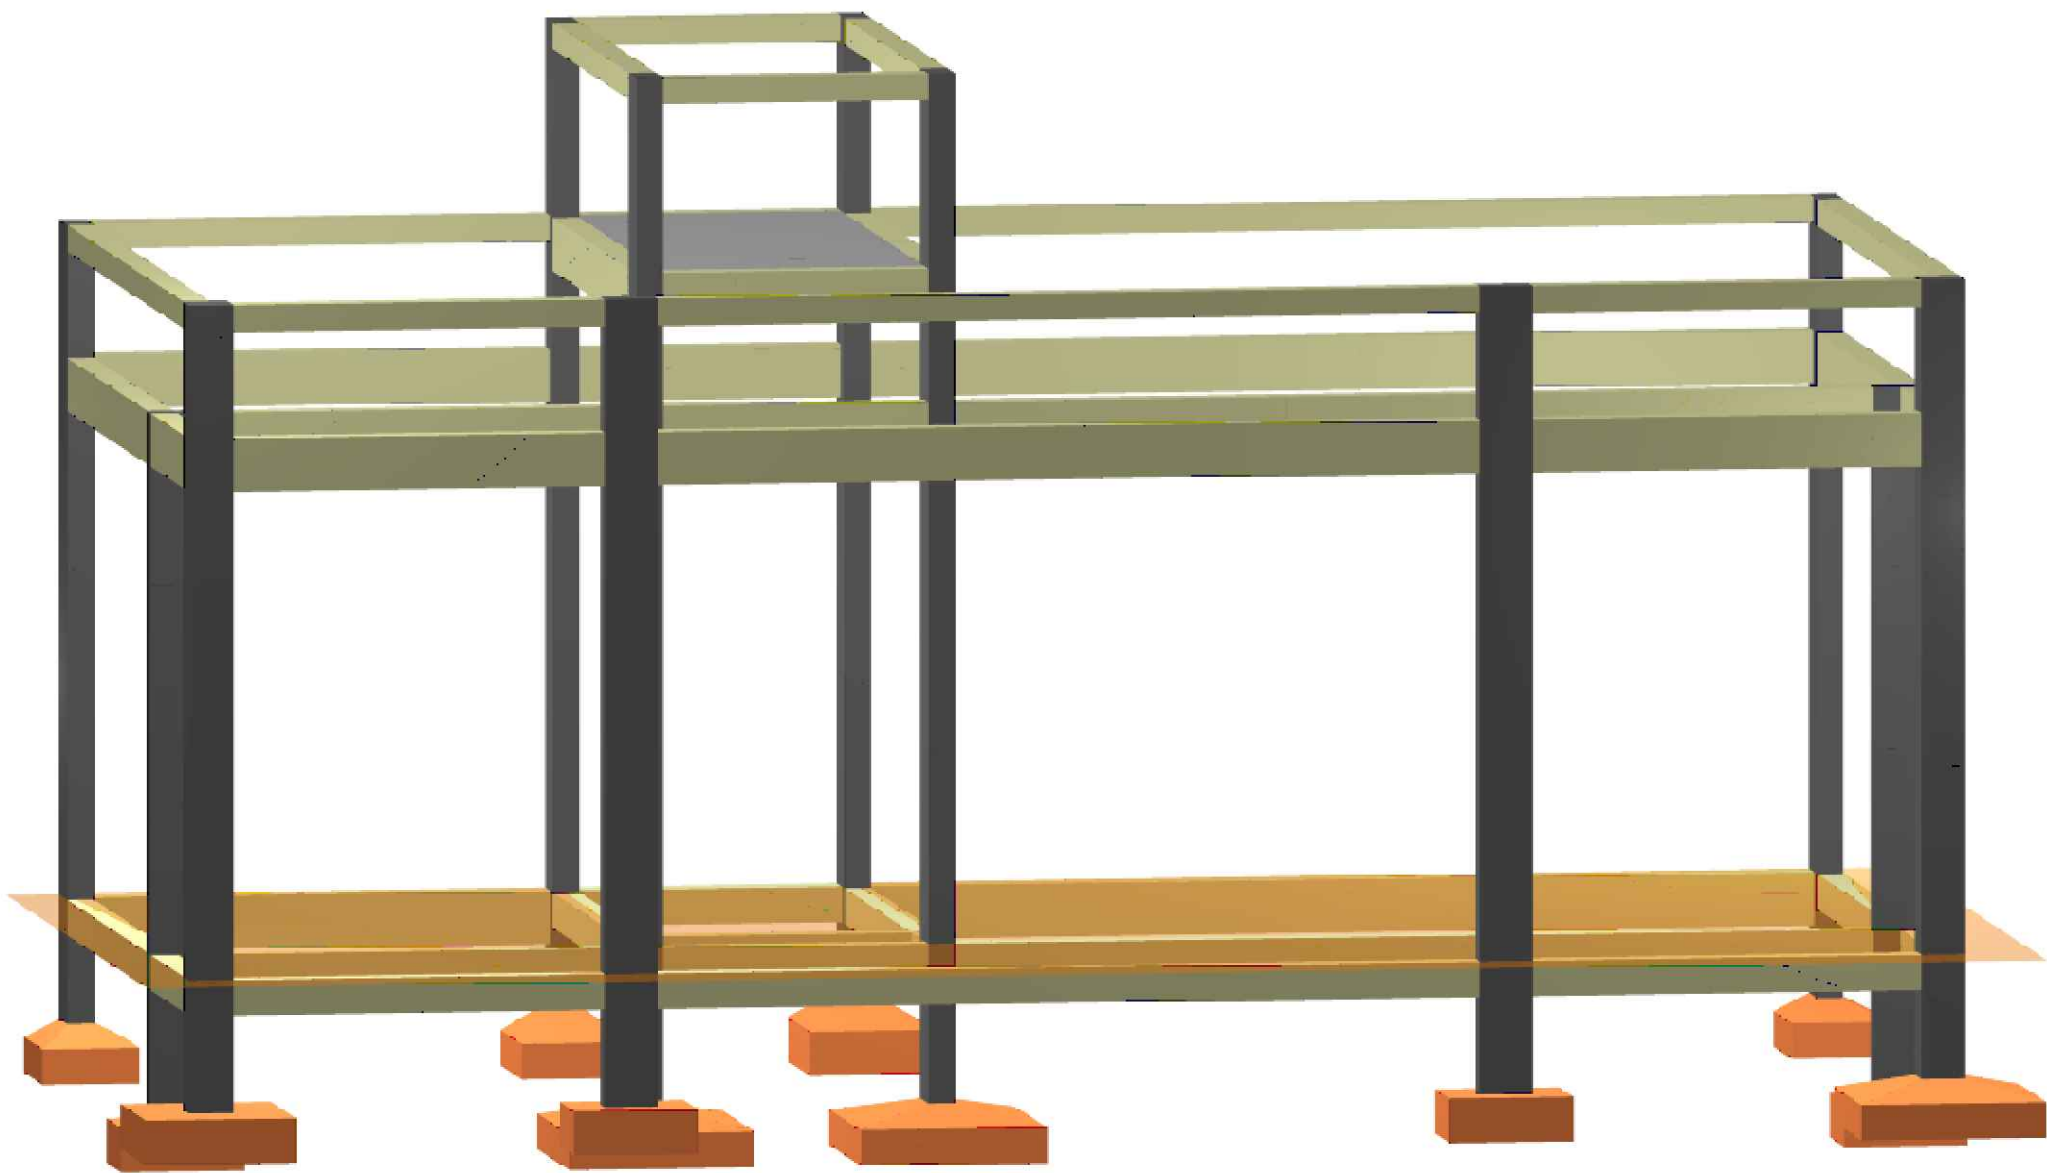

Corte B-B
escala 1:50

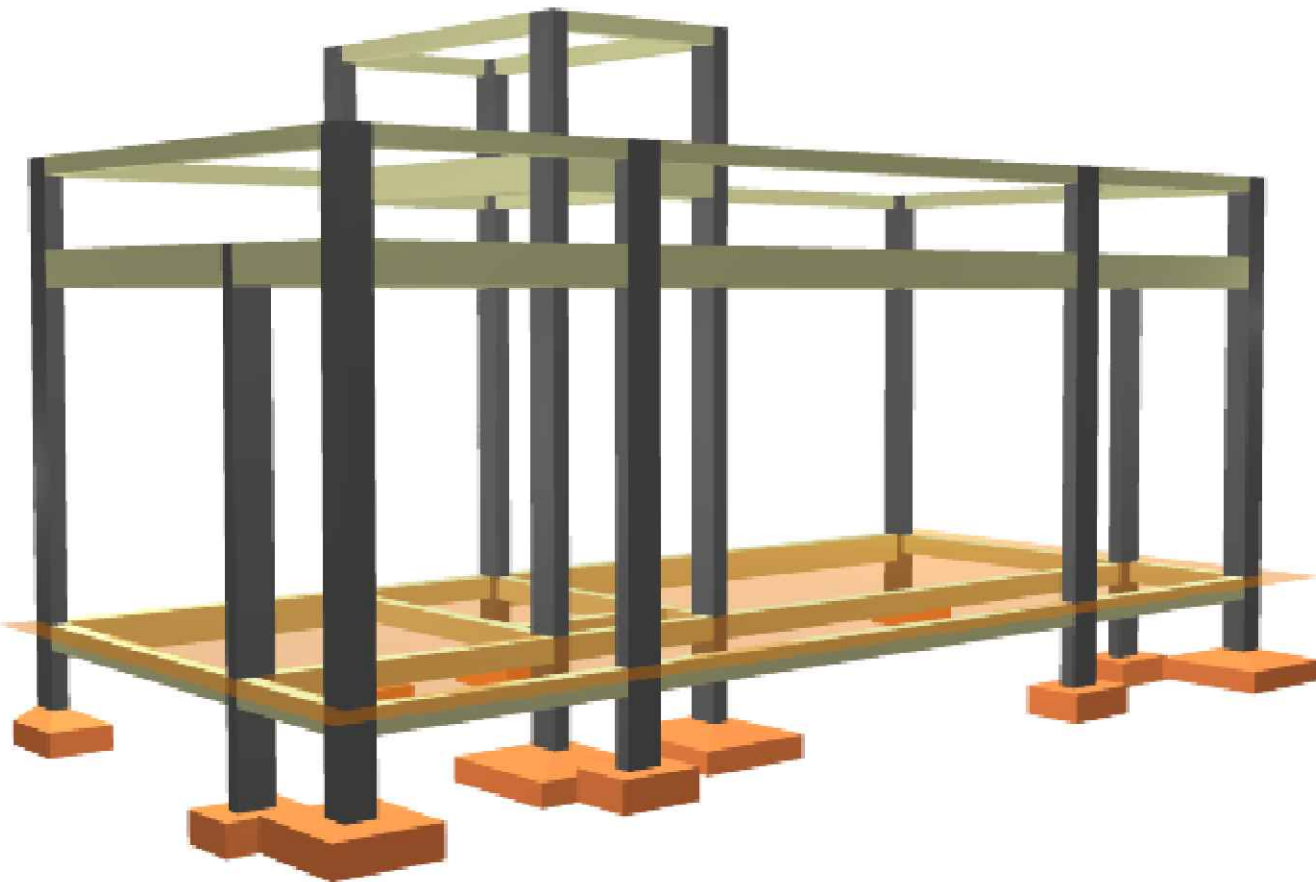

PROPRIETÁRIO: PREFEITURA MUNICIPAL DE COREMAS- PB

LINCOLN CARTAXO DE LIRA JUNIOR:06897861405

Assinado de forma digital por LINCOLN CARTAXO DE LIRA JUNIOR:06897861405
Dados: 2025.07.14 11:27:07 -03'00'

PROJETO: LINCOLN CARTAXO DE LIRA JÚNIOR CREA 160.814.689-8

FOLHA 03/09
PROJETO: GARAGEM COREMAS (ESTRUTURAL ANEXO I)
CONVENIENTE: PREFEITURA MUNICIPAL DE COREMAS-PB
CONCIDENTE: PREFEITURA MUNICIPAL DE COREMAS-PB
LOCALIDADE: COREMAS- PB

DATA		RESPONSÁVEL	RUBRICA	DADOS	
DESENHO		JUN/2025	LINCOLN CARTAXO		
CÓPIA					
VISTO					
ESCALAS		DESENHOS - PLANTA DE FORMAS -- Pav. +490. - CORTES -- Corte A-A; -- Corte B-B.	CONVÊNIO		
INDICADO					
			ARQUIVO		