
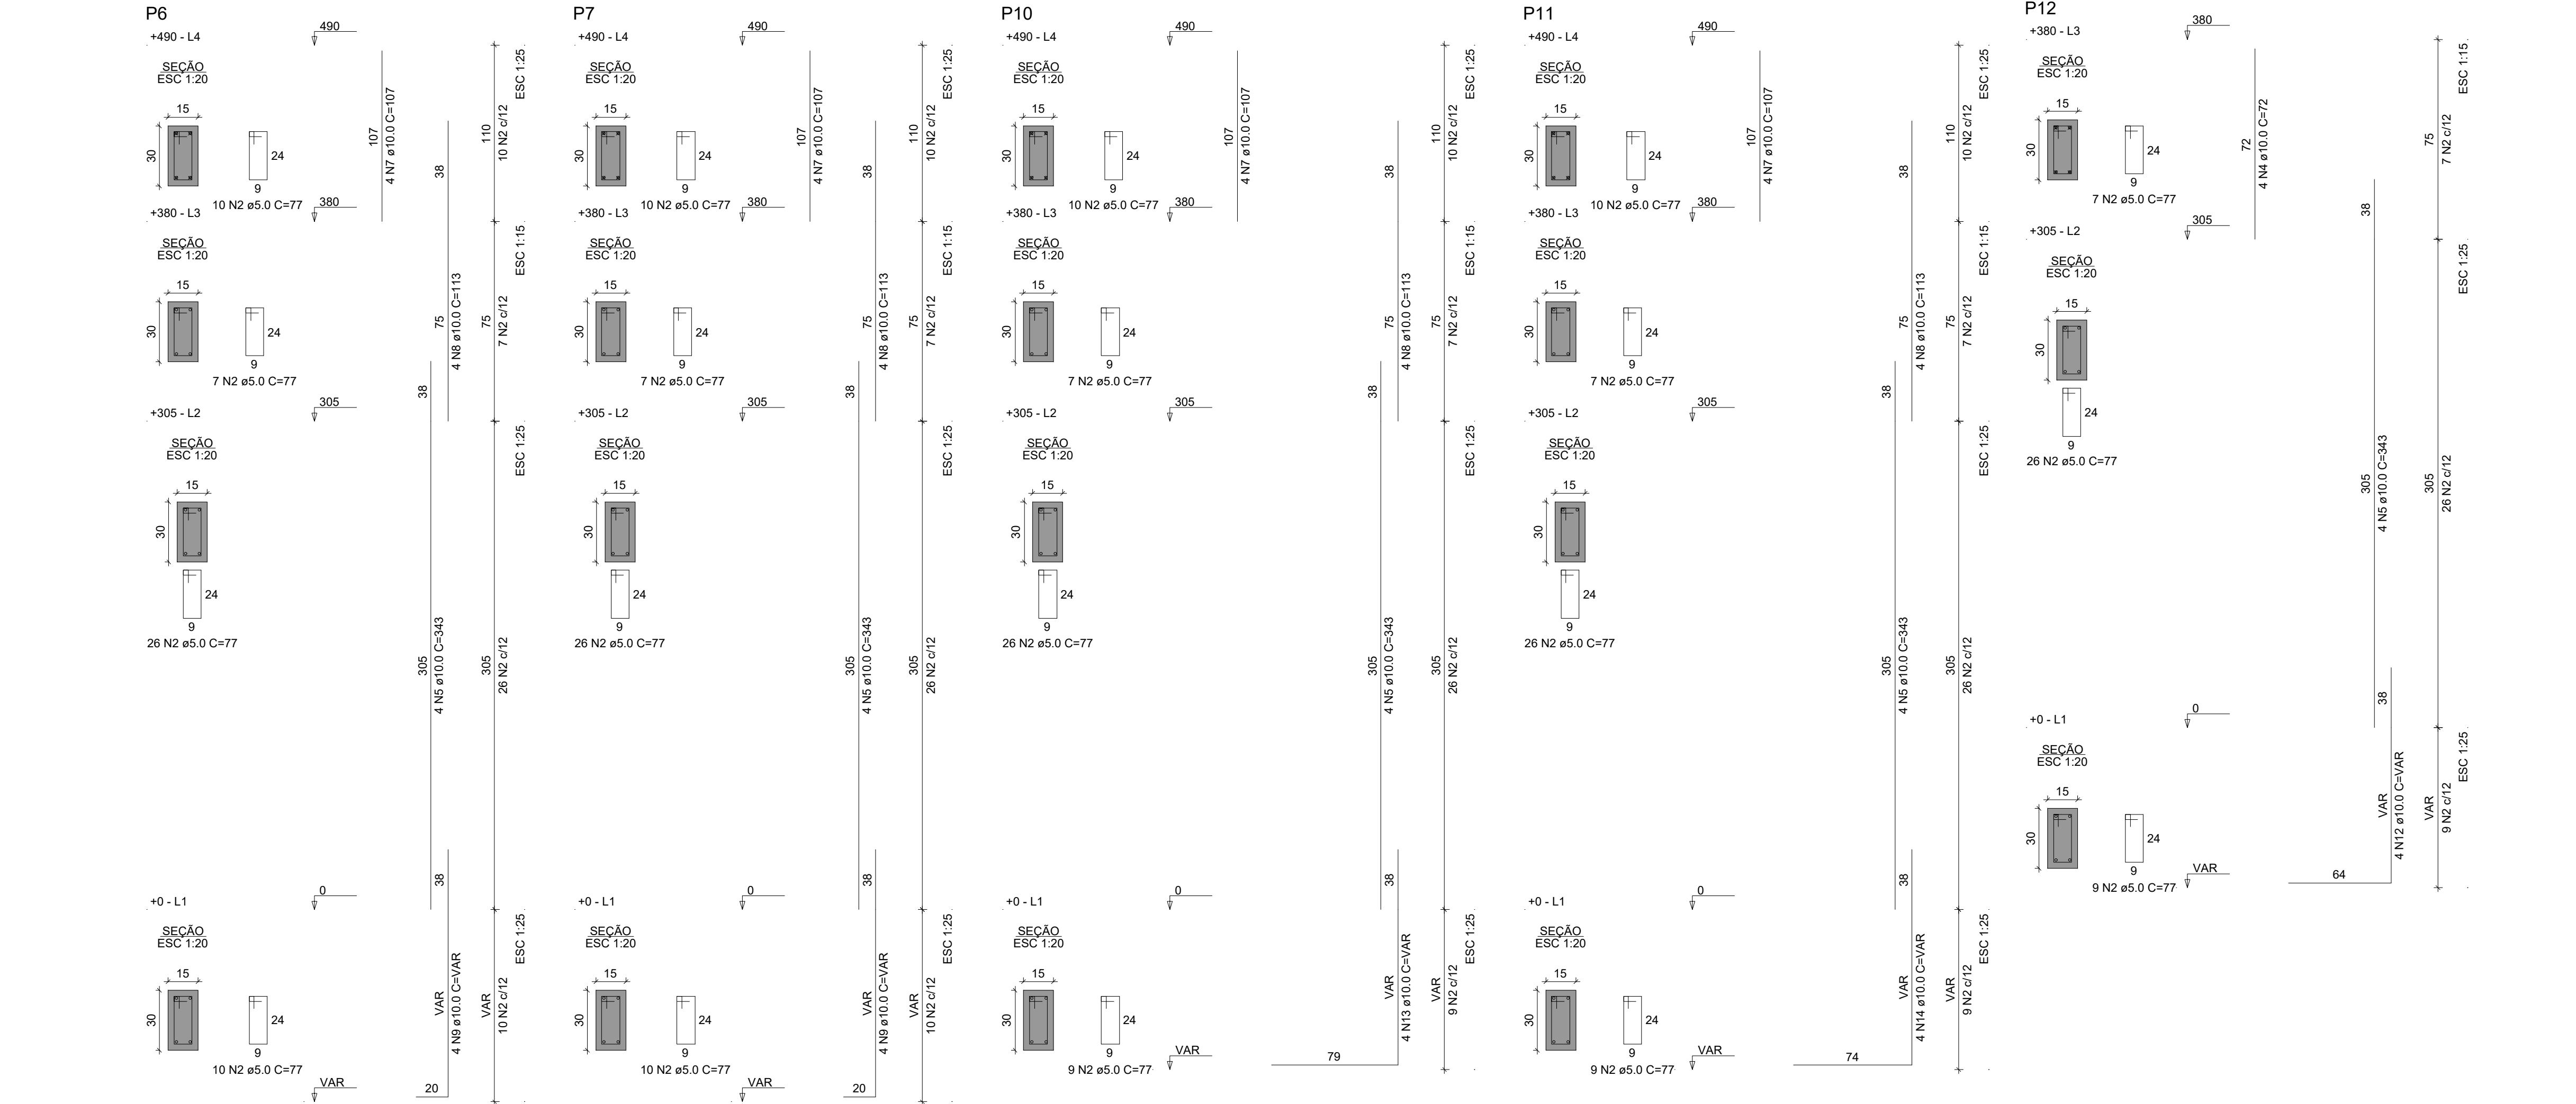


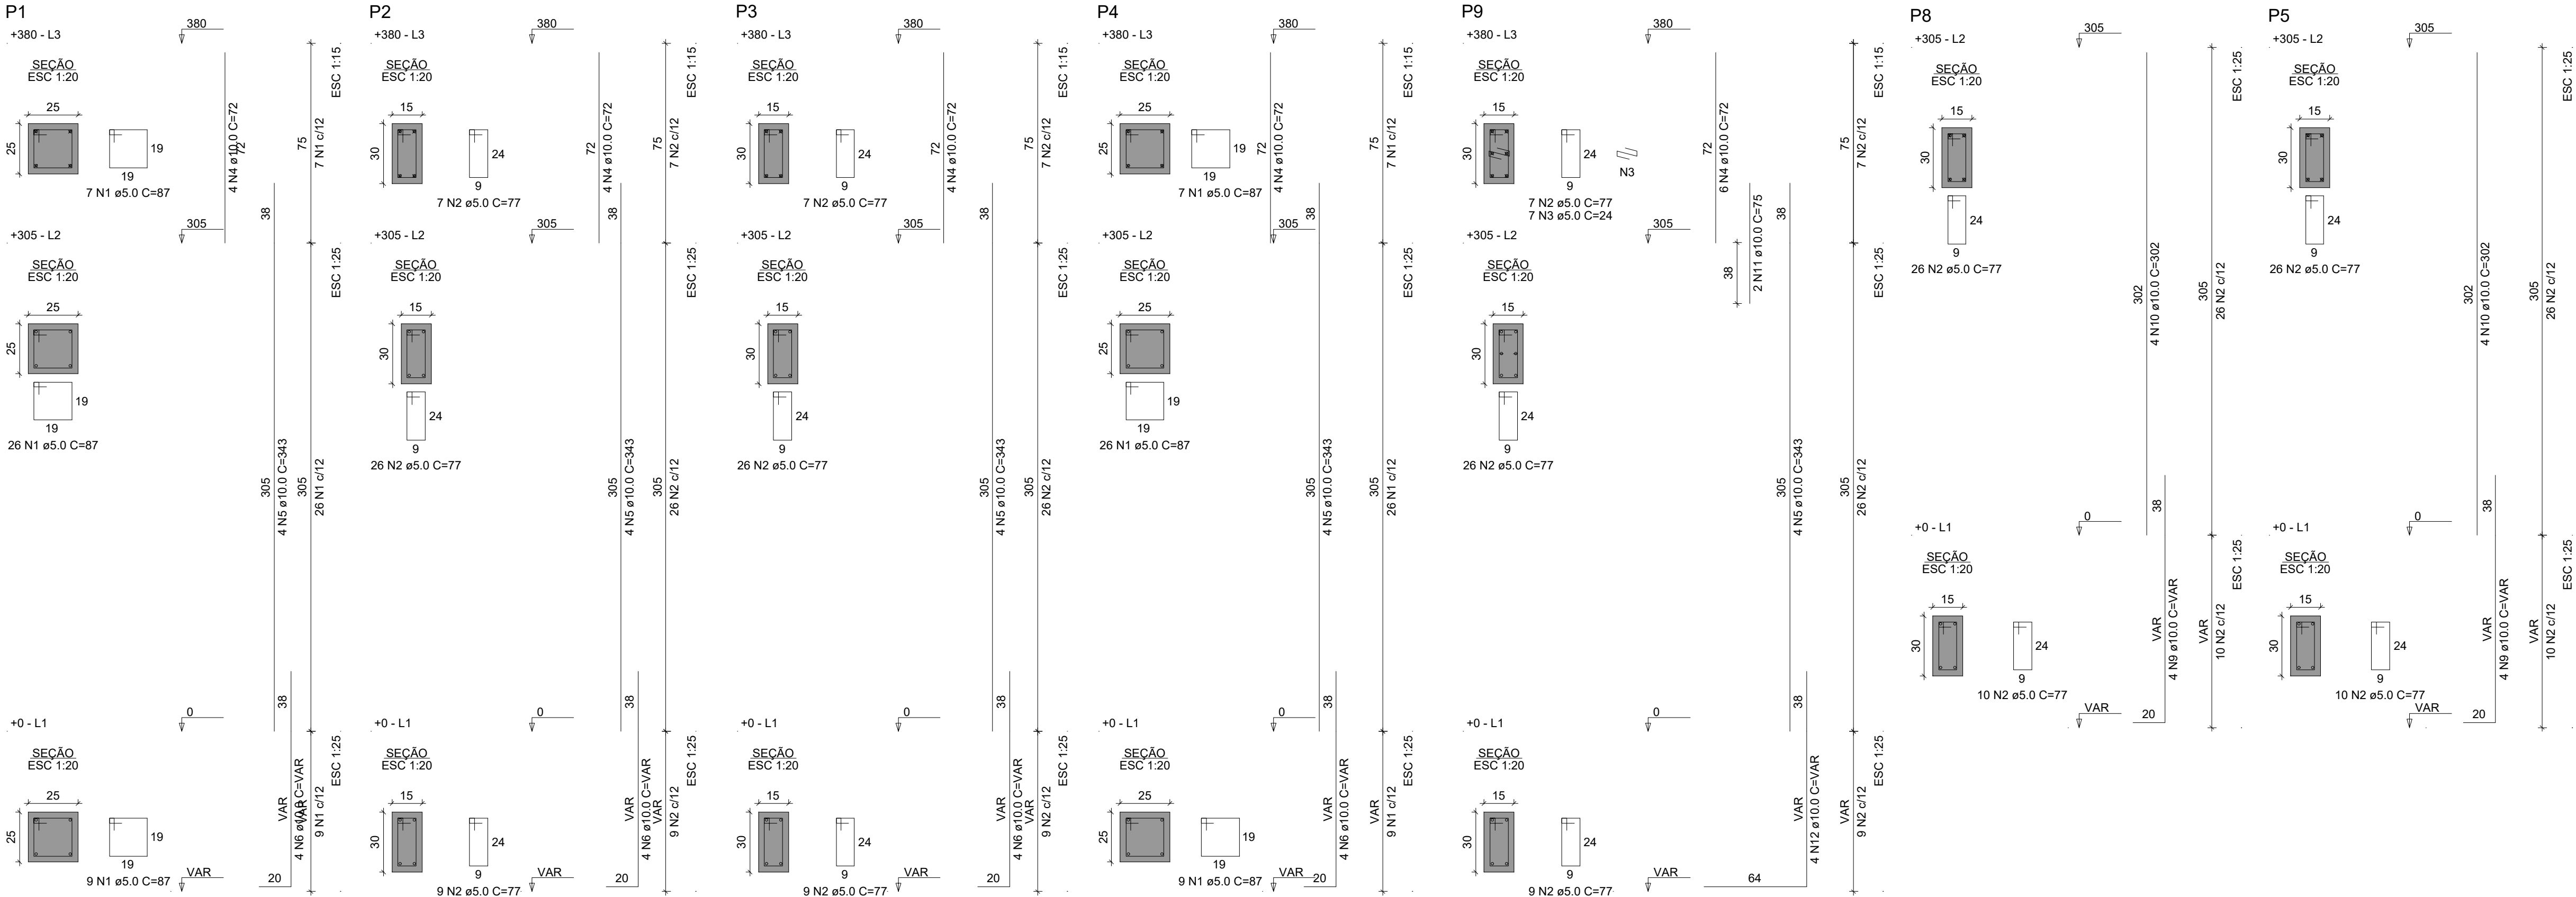

RELAÇÃO DO AÇO

P1-L3	P1-L2	P1-L1
P2-L3	P2-L2	P2-L1
P3-L3	P3-L2	P3-L1
P4-L3	P4-L2	P4-L1
P6-L4	P6-L3	P6-L2
P6-L1	P7-L4	P7-L3
P7-L2	P7-L1	P8-L2
P8-L1	P9-L3	P9-L2
P9-L1	P10-L4	P10-L3
P10-L2	P10-L1	P11-L4
P11-L3	P11-L2	P11-L1
P12-L3	P12-L2	P12-L1
P5-L2	P5-L1	

AÇO	N	DIAM (mm)	QUANT	C.UNIT (cm)	C.TOTAL (cm)
CA60	1	5.0	84	87	7308
	2	5.0	450	77	34650
CA50	3	5.0	7	24	168
	4	10.0	26	72	1872
	5	10.0	40	343	13720
	6	10.0	16	VAR	VAR
	7	10.0	16	107	1712
	8	10.0	16	113	1808
	9	10.0	16	VAR	VAR
	10	10.0	8	302	2416
	11	10.0	2	75	150
	12	10.0	8	VAR	VAR
	13	10.0	4	VAR	VAR
	14	10.0	4	VAR	VAR

RESUMO DO AÇO

AÇO	DIAM (mm)	C.TOTAL (m)	PESO + 10% (kg)
CA50	10.0	301.5	204.4
CA60	5.0	421.3	71.4
PESO TOTAL (kg)			
CA50		204.4	
CA60		71.4	

Volume de concreto (C-25) = 2.93 m³
Área de forma = 56.13 m²

PROPRIETÁRIO: PREFEITURA MUNICIPAL DE COREMAS- PB
LINCOLN CARTAXO DE LIRA JUNIOR:06897861405 Assinado de forma digital por LINCOLN CARTAXO DE LIRA JUNIOR:06897861405
Dados: 2025.07.14 11:28:00 -03'00'

PROJETO: LINCOLN CARTAXO DE LIRA JÚNIOR CREA 160.814.689-8

FOLHA
05/09
PROJETO: GARAGEM COREMAS (ESTRUTURAL ANEXO I)
CONVENIENTE: PREFEITURA MUNICIPAL DE COREMAS-PB
CONCIDENTE: PREFEITURA MUNICIPAL DE COREMAS-PB
LOCALIDADE: COREMAS- PB

DESENHO	DATA	RESPONSÁVEL	RUBRICA	DADOS
COPIA	JUN/2025	LINCOLN CARTAXO		
VISTO				
ESCALAS	DESENHOS	CONVÊNIO		
INDICADO	PILARES	ARQUIVO		

Aprovações: